



OPERATIONS PROFILE

W.K. TUPPER
Deputy Executive Director,
Operations

S.A. AUSTIN
Senior Corporate Director,
Customer Affairs/Training

G.L. HARDWIDGE
Chief Transportation Officer

ELECTRIC DISTRICT

PROJECT MANAGER & CHIEF DESIGNER:
J.M. GOTTLIEB

OPERATING RULES DATA:
L.C. MICHAEL

COMPLIANCE, EDITING & REORGANIZATION:
L.G. GOMM

FIELD VERIFICATION TEAM:
METRA POLICE DEPT.
(for off right-of-way locations)
J.S. TALLYN, A.E. HOOKER,
T.G. PITZEN, R.E. THOMPSON

YARDS & R-of-W South of University Park
J.S. TALLYN

PARKING LOT DATA:
L.G. GOMM

TABLE OF CONTENTS

ELECTRIC DISTRICT	8
University Park Sub District	12
CN from Stuenkel to Peotone	26
South Chicago Sub District	32
Blue Island Sub District	34
Interlocking Detail Maps	36
KENSINGTON & EASTERN (NICTD)	38
INDEX.....	42

JULY 15, 2009

Operations Profile represents Metra's compliance with 49CFR239 governing emergency preparedness specific to geographic locations on specific line segments.

OFFICE OF ROAD FOREMAN OF ENGINES-RANDOLPH STREET.
CONCERNING: TRAIN NO. 505 - TIE UP INSTRUCTIONS
EFFECTIVE IMMEDIATELY, TRAIN NO. 505 IS TO LEAVE
PANTOGRAPHS RAISED ON THE TWO (2) SOUTH CARS, AND
LOWER PANTOGRAPHS ON THE TWO (2) NORTH CARS OF THE
CONSIST, MONDAY THROUGH WEDNESDAY, AND ALL
PANTOGRAPHS ARE TO REMAIN RAISED ON THURSDAY AND
FRIDAY.

300.16 DWARF SIGNALS AT RANDOLPH ST. YARD

DWARF SIGNAL GOVERNING DEPARTURE FROM RANDOLPH ST:
ROUTE LINEUPS ARE AS FOLLOWS:
YELLOW: LINED OUT OF YARD - PROCEED PREPARED TO
STOP AT NEXT SIGNAL.
RED OVER YELLOW: LINED FOR STORAGE TRACK 5
-PROCEED AT RESTRICTED SPEED.
GREEN: LINED OUT OF YARD - PROCEED ON ROUTE LINED.

DWARF SIGNAL GOVERNING MOVEMENT FROM STORAGE 5
TO CSS LEAD:
RED OVER YELLOW: LINED FOR CSS LEAD-PROCEED AT
RESTRICTED SPEED.

3032


ELECTRIC DISTRICT / RANDOLPH INTERLOCKING

REV 5/20/09

P-11

ON No. 4 STORAGE TRACK
TRAINS READY TO LEAVE THE NORTH END OF NO. 4 STORAGE
TRACK WILL MOVE TO THE YELLOW MARKER STAKE (NEAR
MONROE ST.) TO ACTIVATE THE TRACK CIRCUIT AND
INDICATE TO THE METRA ELECTRIC TERMINAL DISPATCHER
THAT THE TRAIN IS READY.


MAIN TRACKS

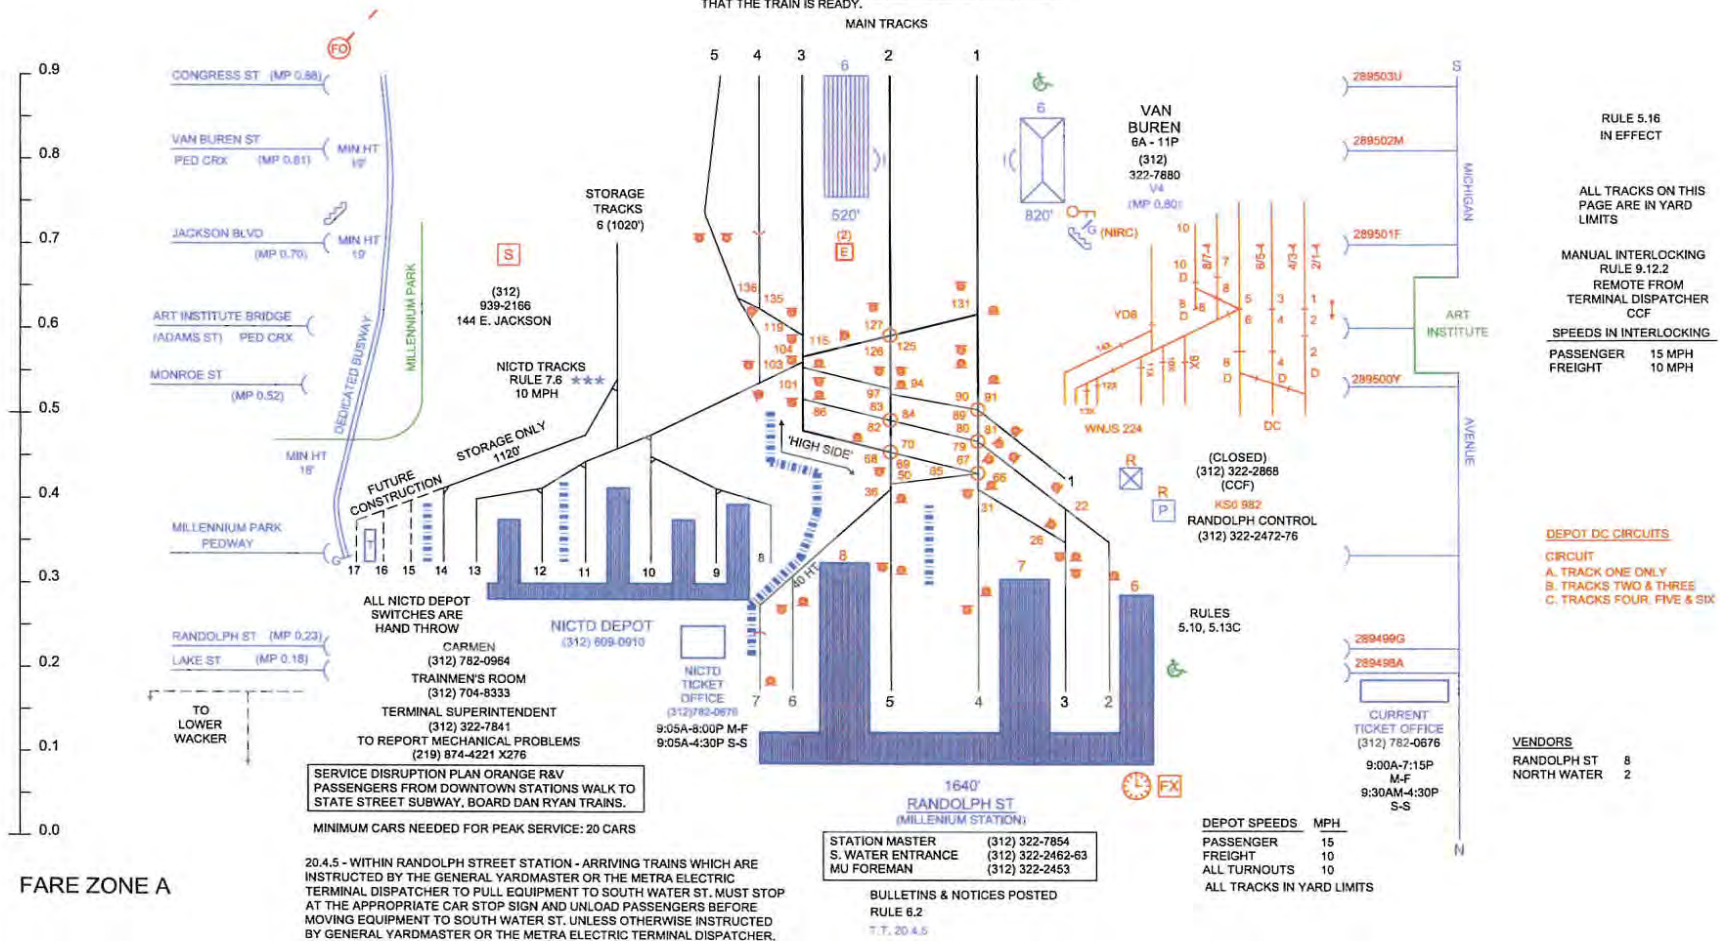

11 MED=11 NICTD

CONTROL POINT PHONE NUMBERS
 RANDOLPH TERMINAL DISPATCHER (312) 322-2868
 RANDOLPH CONTROL (312) 322-2472-76

RFQ 161.025 AAR 22

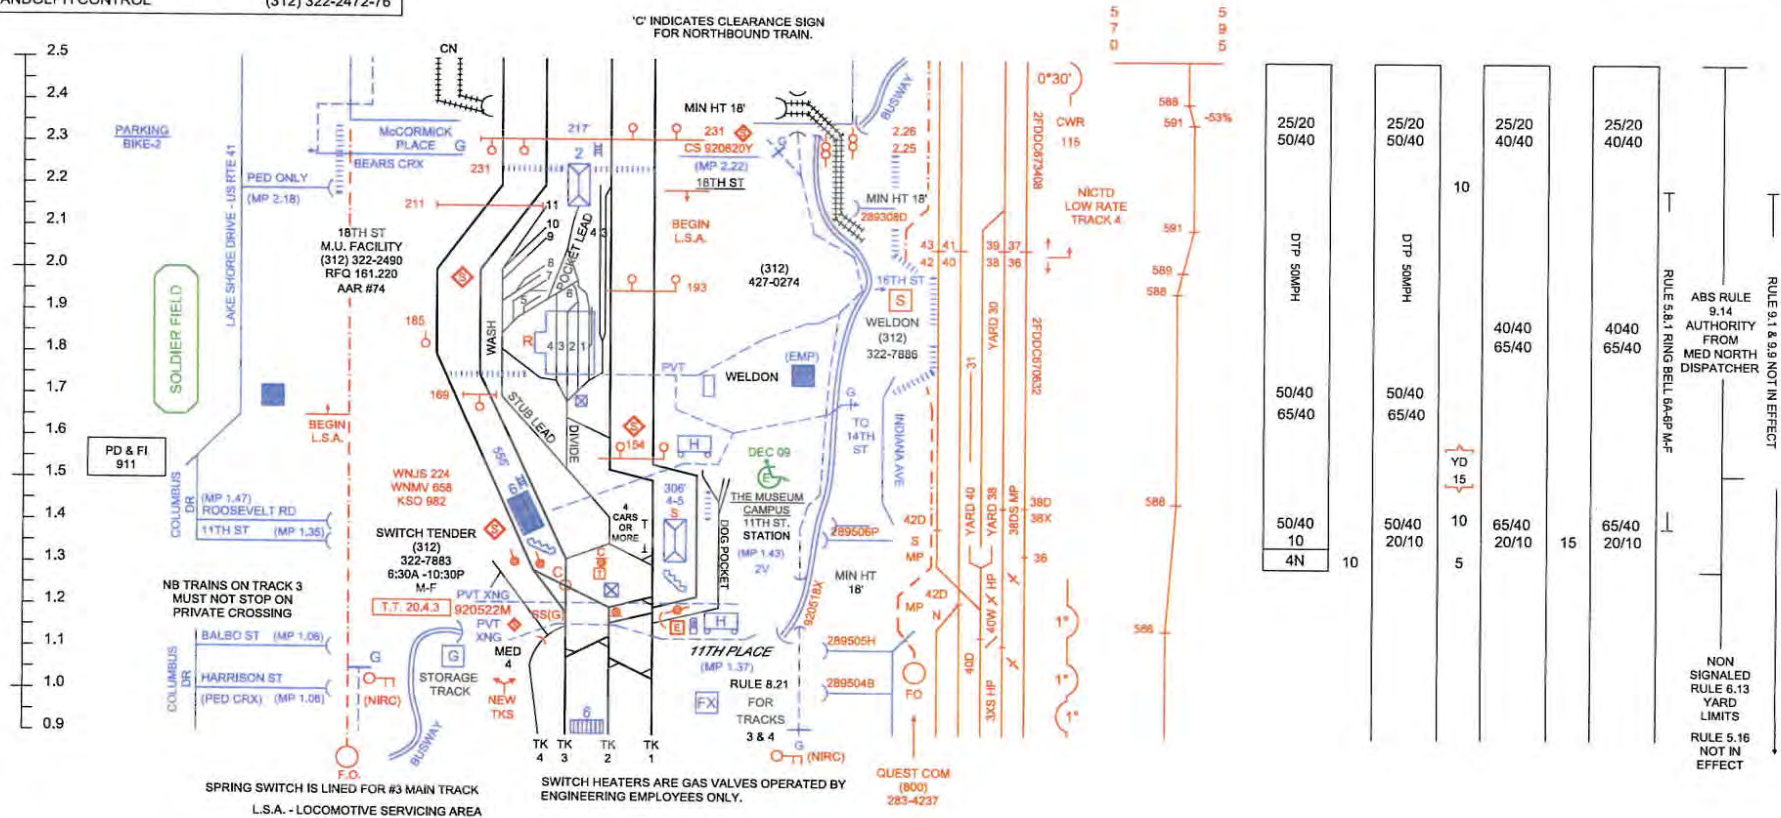

MED12=NICTD12


© S L W
 7 13 26 42

3032
 3092


ELECTRIC DISTRICT / UNIVERSITY PARK SUBDISTRICT

REV 7/28/09

P-12

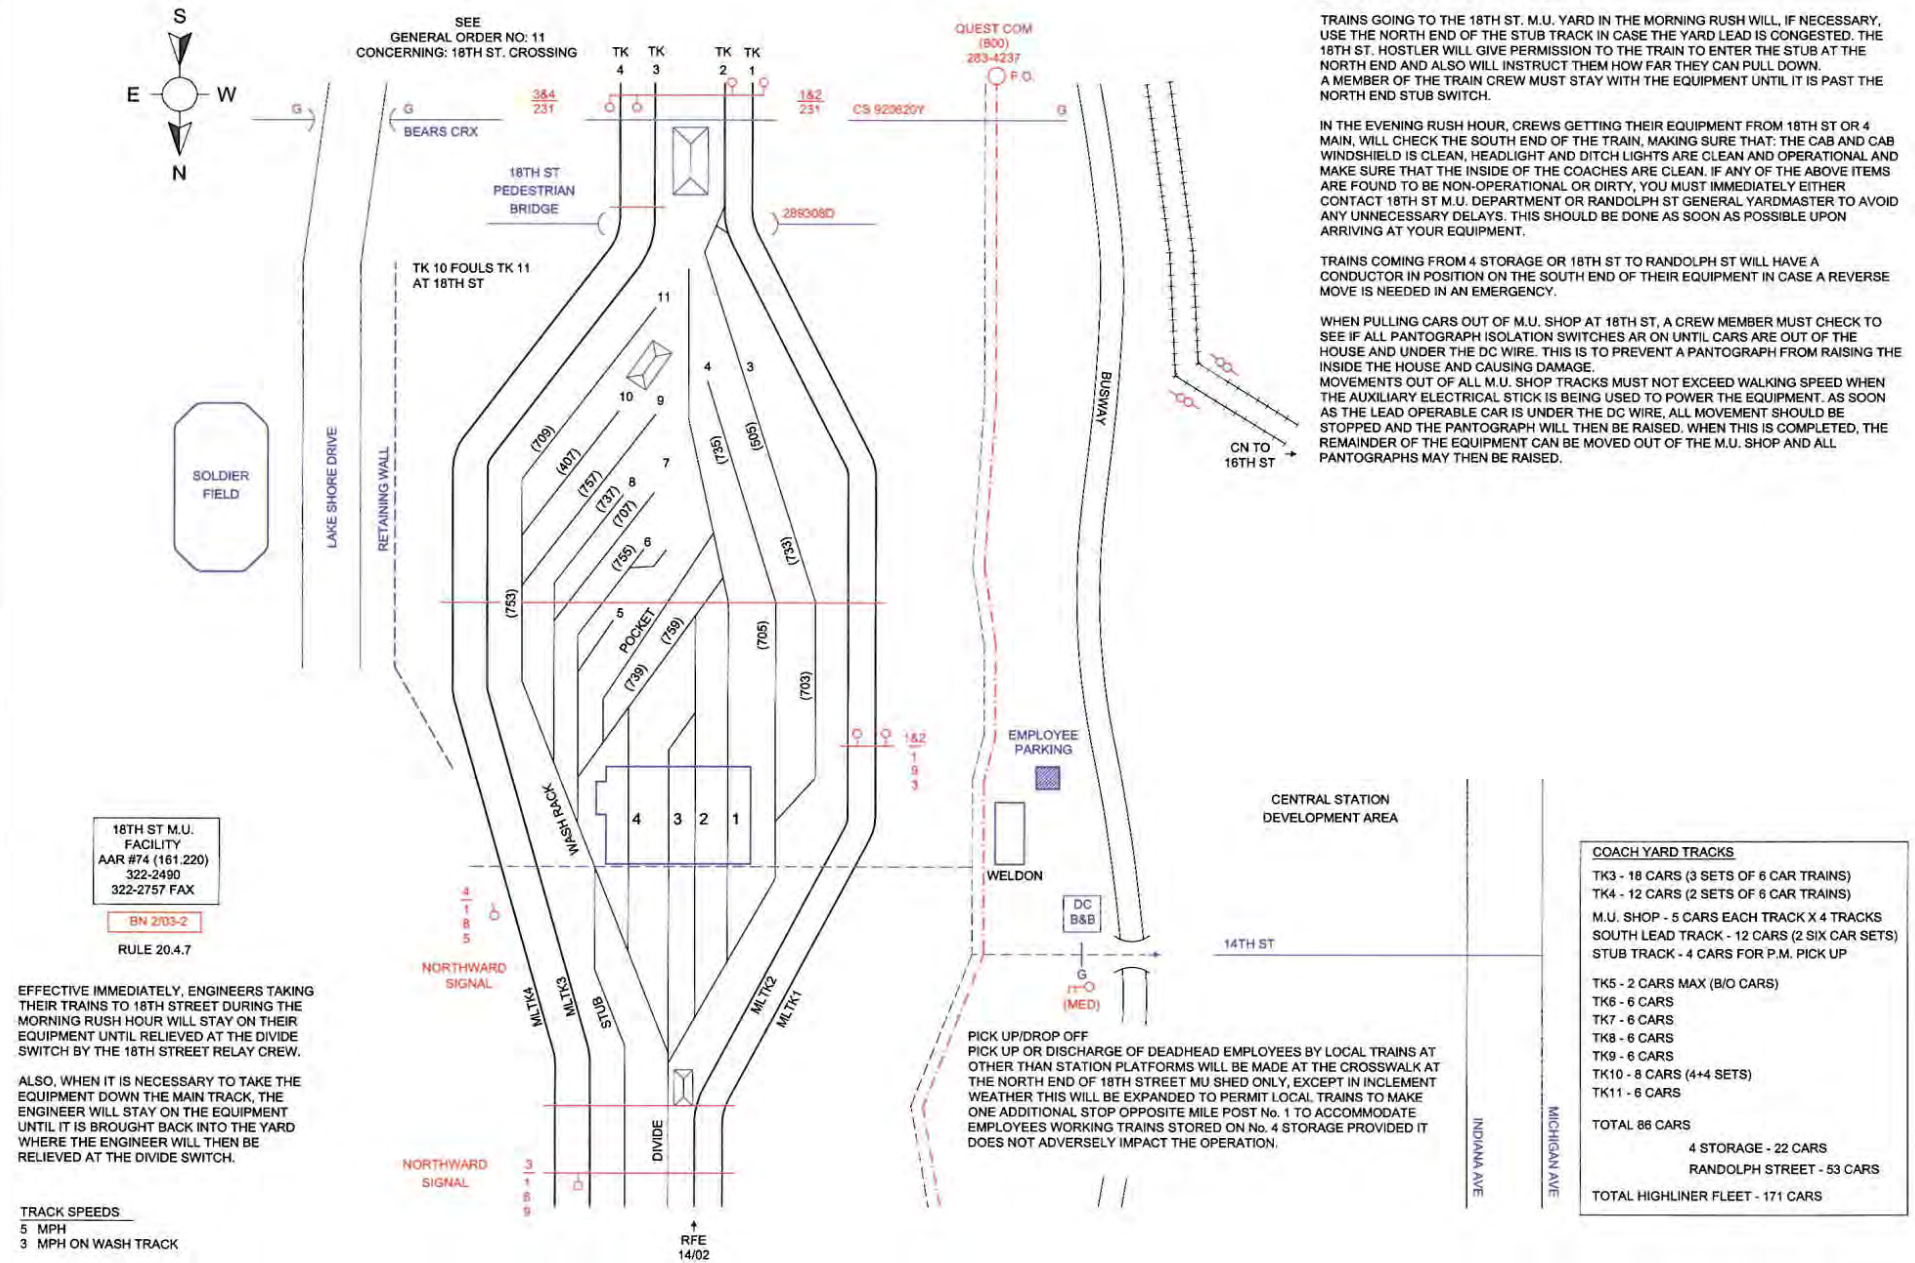


CN RR TRAIN SPEEDS:
65/50 MPH ON TRACKS 1 & 2
10 MPH ON OTHER TRACKS

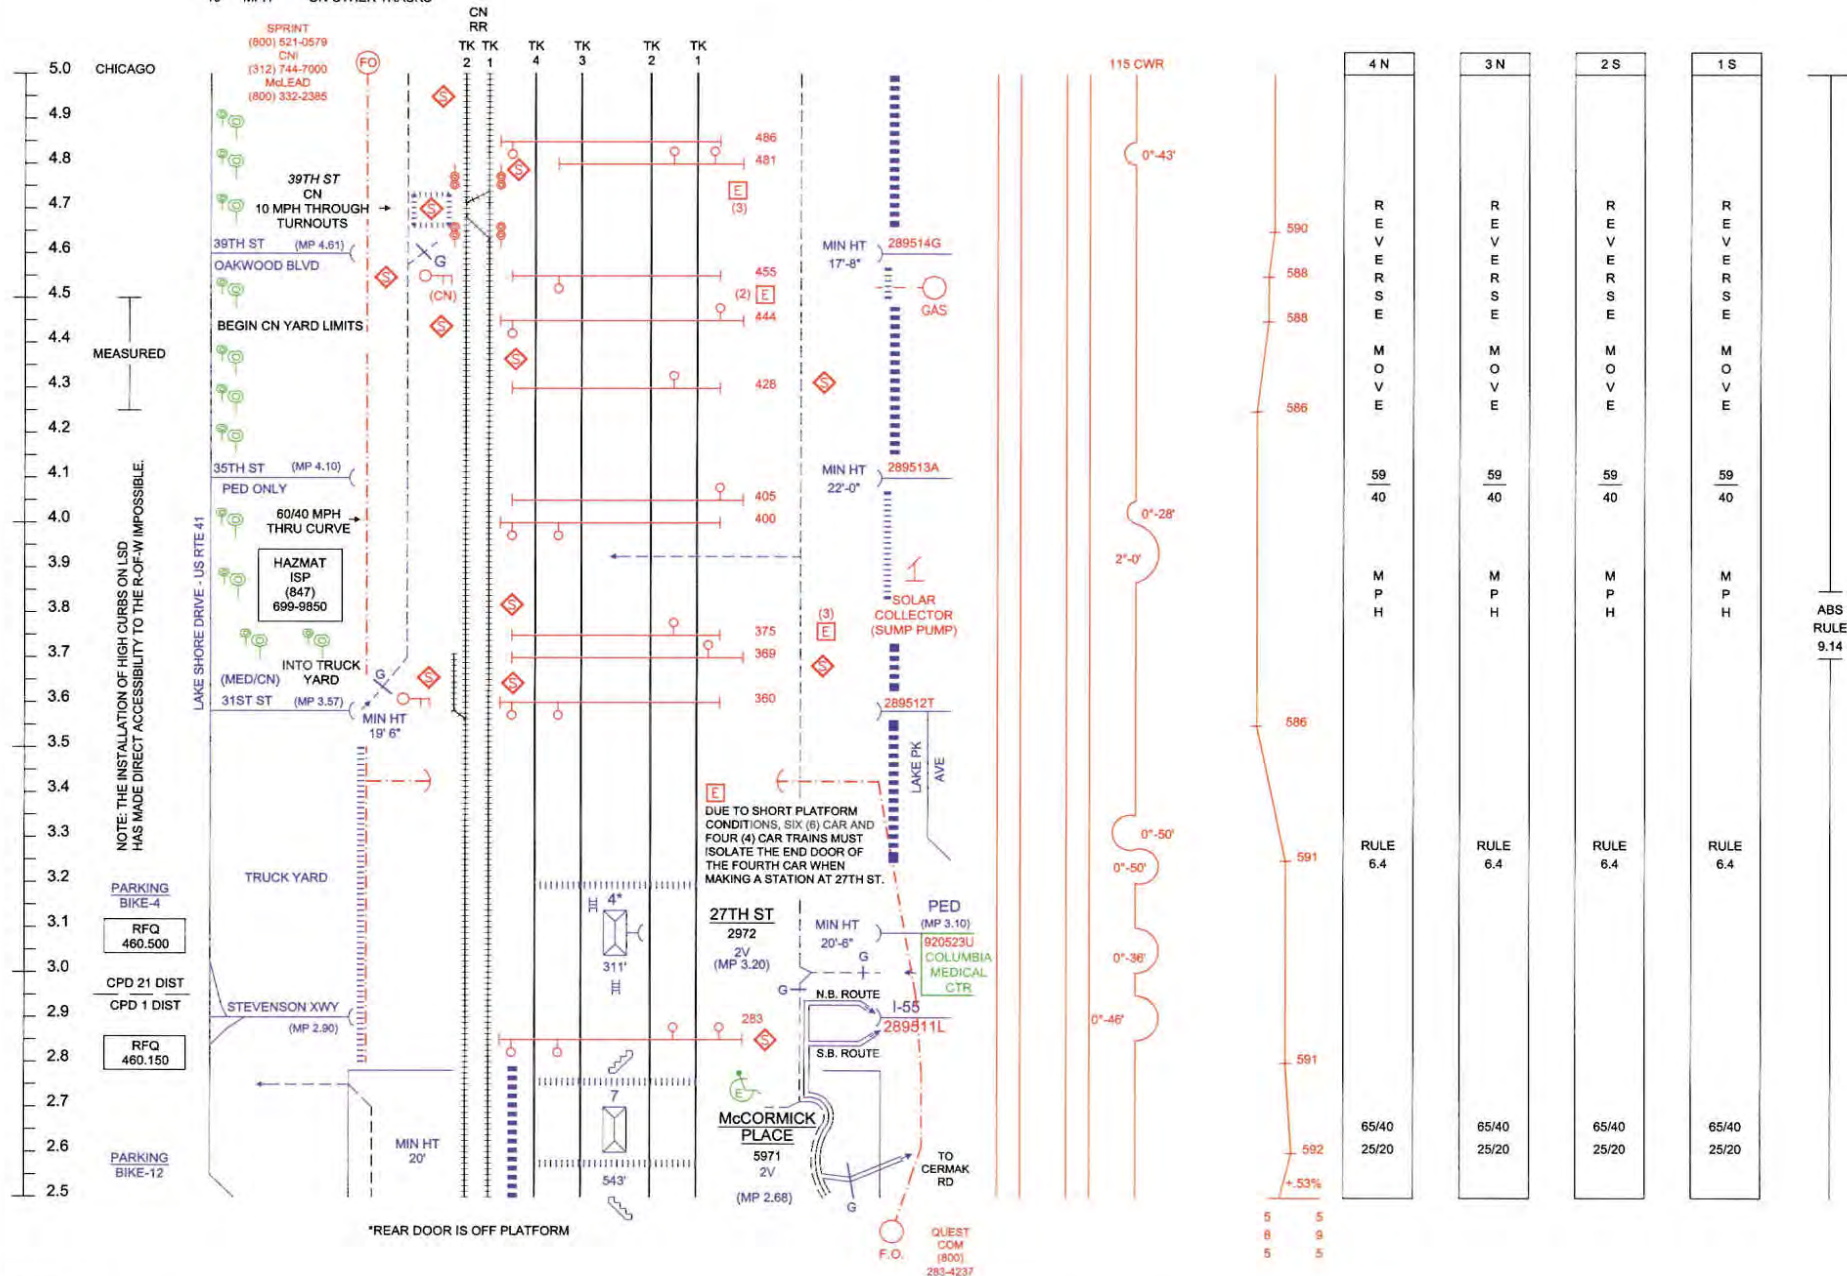

CONTROL POINT PHO.	NUMBERS
RANDOLPH CONTROL	(312) 322-2472, -76
67TH TOWER	(312) 322-7875
51ST ST - NORTH DISP. CCF	(312) 522-2861

1V 2G
6A-2P
(312) 322-7838

WHEN TRAIN 502 IS LATE AND MISSES THE CONNECTION WITH TRAIN 106 AT 59TH STREET, TRAIN 402 IS AUTHORIZED TO MAKE FLAG DISCHARGE STOPS AT 47TH AND/OR 18TH STREET TO ACCOMMODATE PASSENGERS WHO MAY HAVE MISSED THEIR CONNECTION

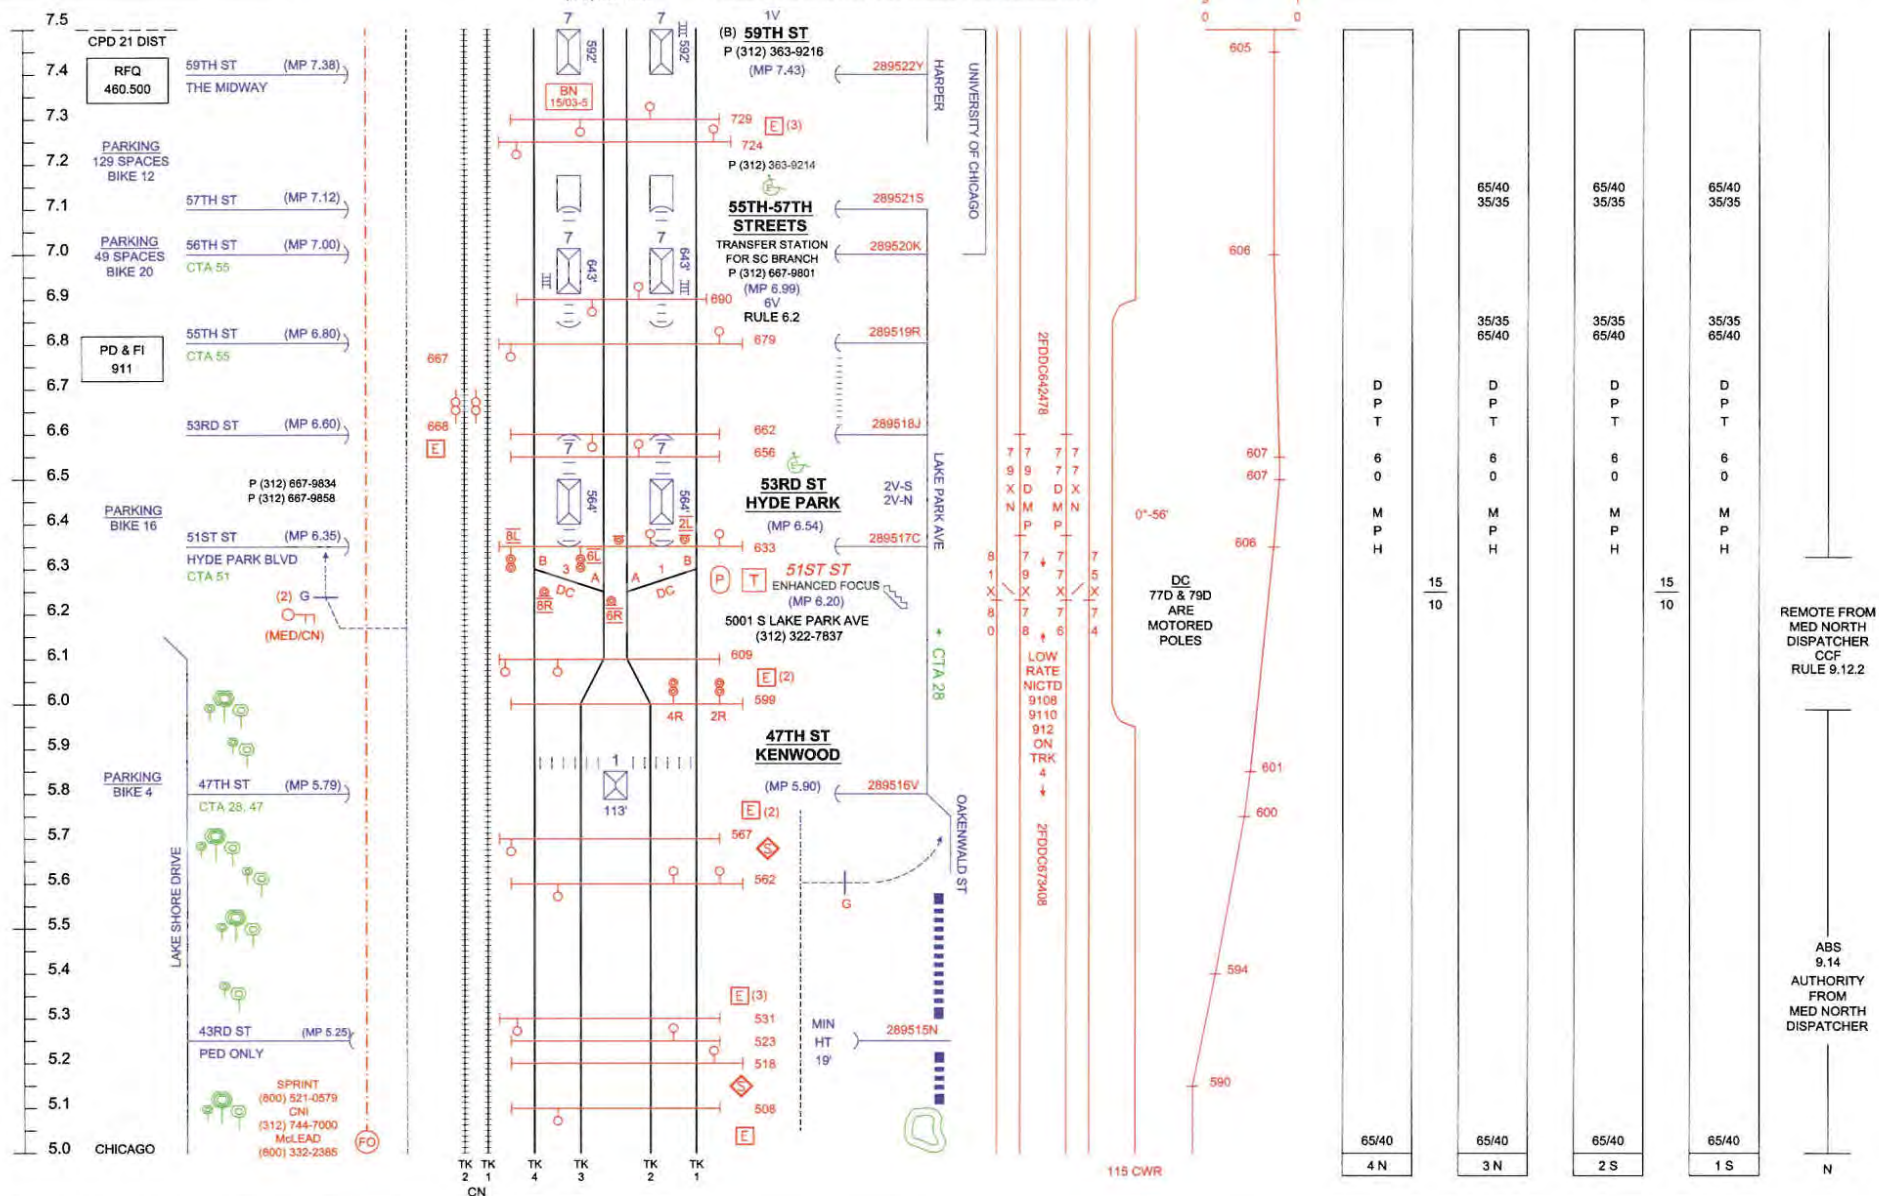

FARE ZONE B

**SERVICE DISRUPTION
PLAN ORANGE R&V
PASSENGERS FOR HYDE PARK
LEAVE CTA DAN RYAN LINE
AT 47TH ST AND BOARD #28 BUS**

(C)	(S)	(L)	(W)	3092
7,1	13	25 26	4,5	3153


ELECTRIC DISTRICT / UNIVERSITY PARK SUBDISTRICT

P-16

16MED=16IND

REV 5/20/09

CN TRAIN SPEEDS:
65/50 MPH ON TRACKS 1&2
10 MPH THROUGH TURNOUTS AT 67TH ST

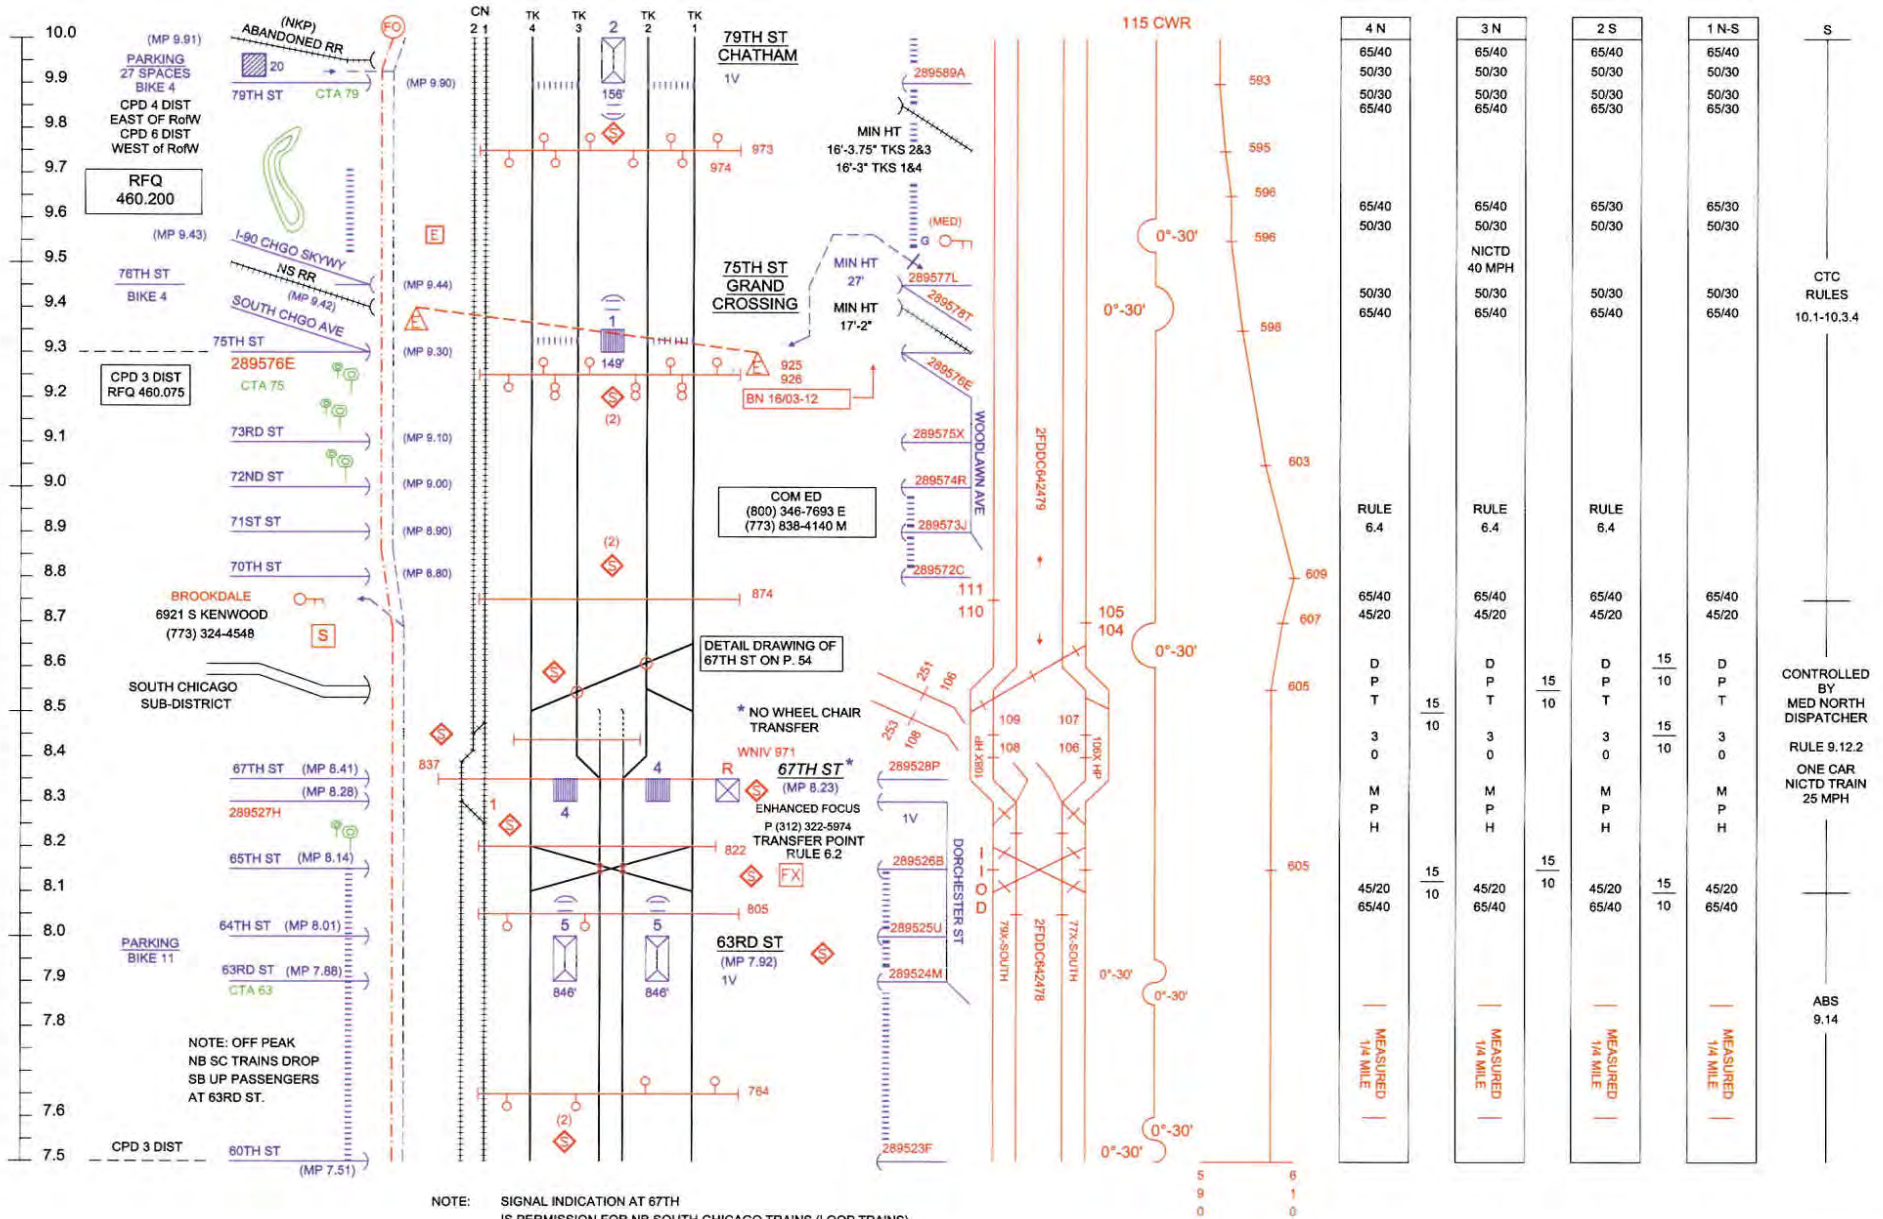

C	S	L	W
1	17	34	8

3214

P-18

RFQ 161.025 AAR 61




14 POCKET
(NS INTERCHANGE)

KYD RFQ 161.610 AAR #01

ELECTRIC DISTRICT / UNIVERSITY PARK SUBDISTRICT


P-20

CN TRAIN SPEEDS
65/50 MPH ON TRACKS 1 & 2
10 MPH ON OTHER TRACKS
20 MPH AT MP 20
TO ALLOW FOR ID.

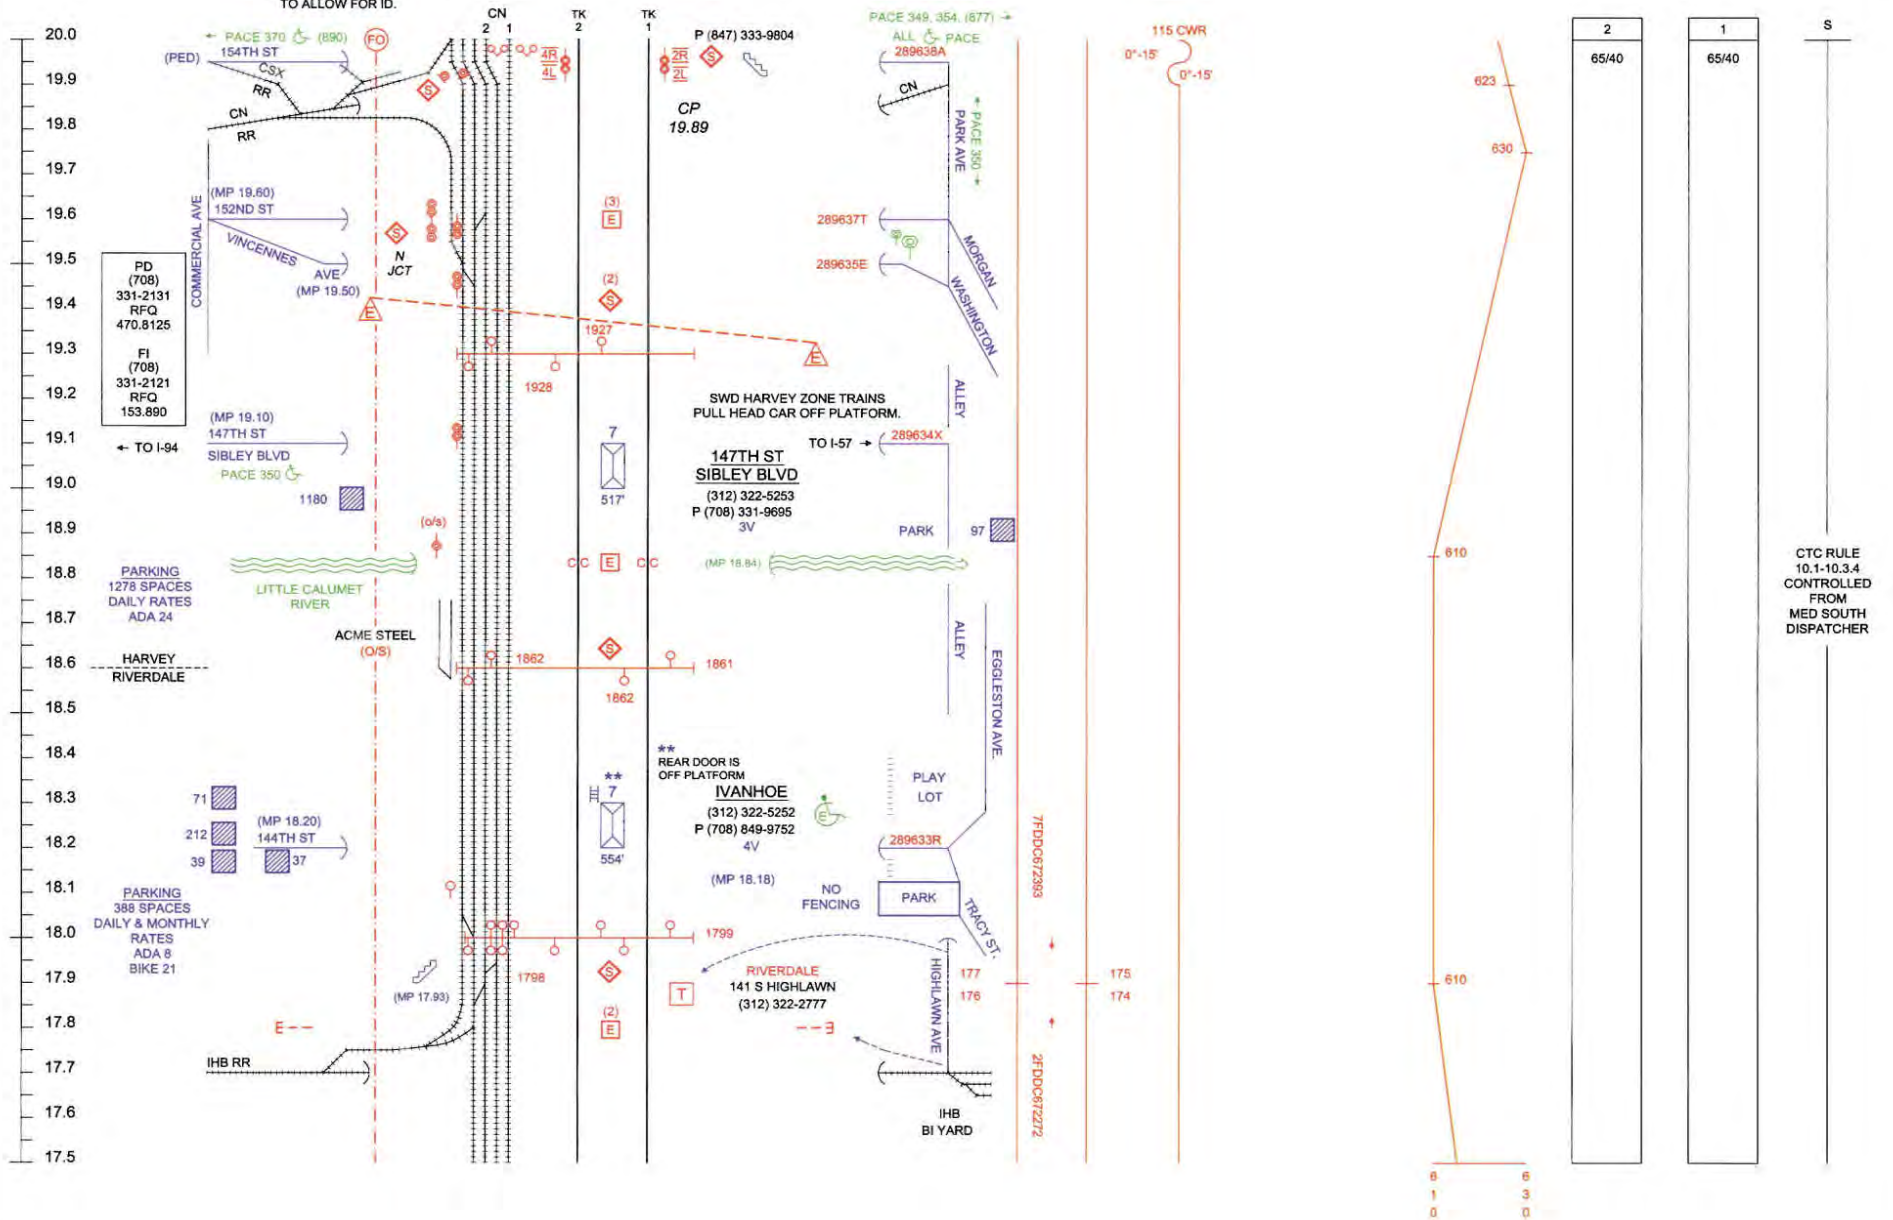



CONTROL POINT PHONE NUMBERS
 (CCF) CTC (312) 322-2860
 MED SOUTH DISPATCHER (312) 322-2260

RFQ 1.025 AAR 61

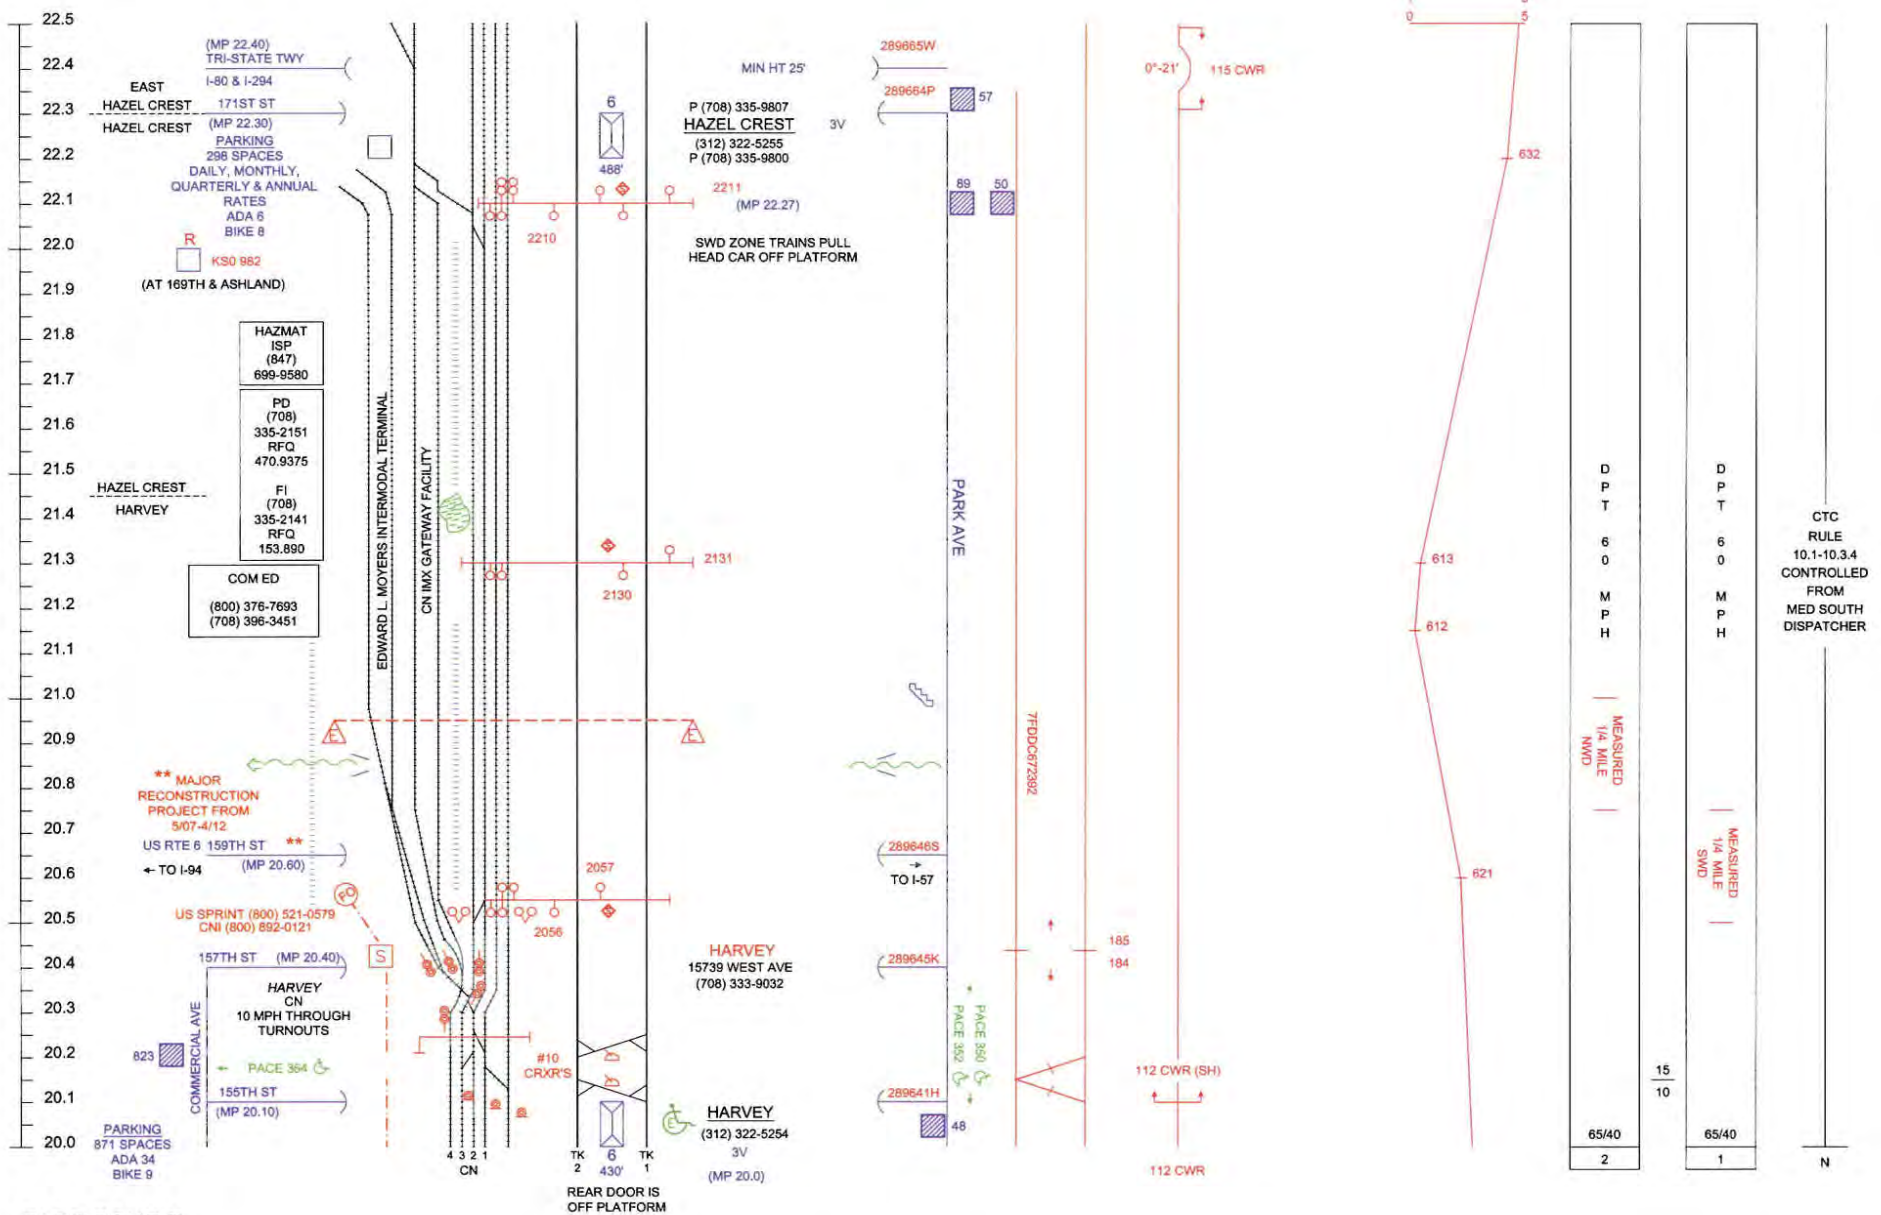

CN TRAIN SPEED:
79/50 MPH ON TRACK 1
40/40 MPH ON TRACKS 2&3
10 MPH ON OTHER TRACKS
20 MPH THROUGH TURNOUTS

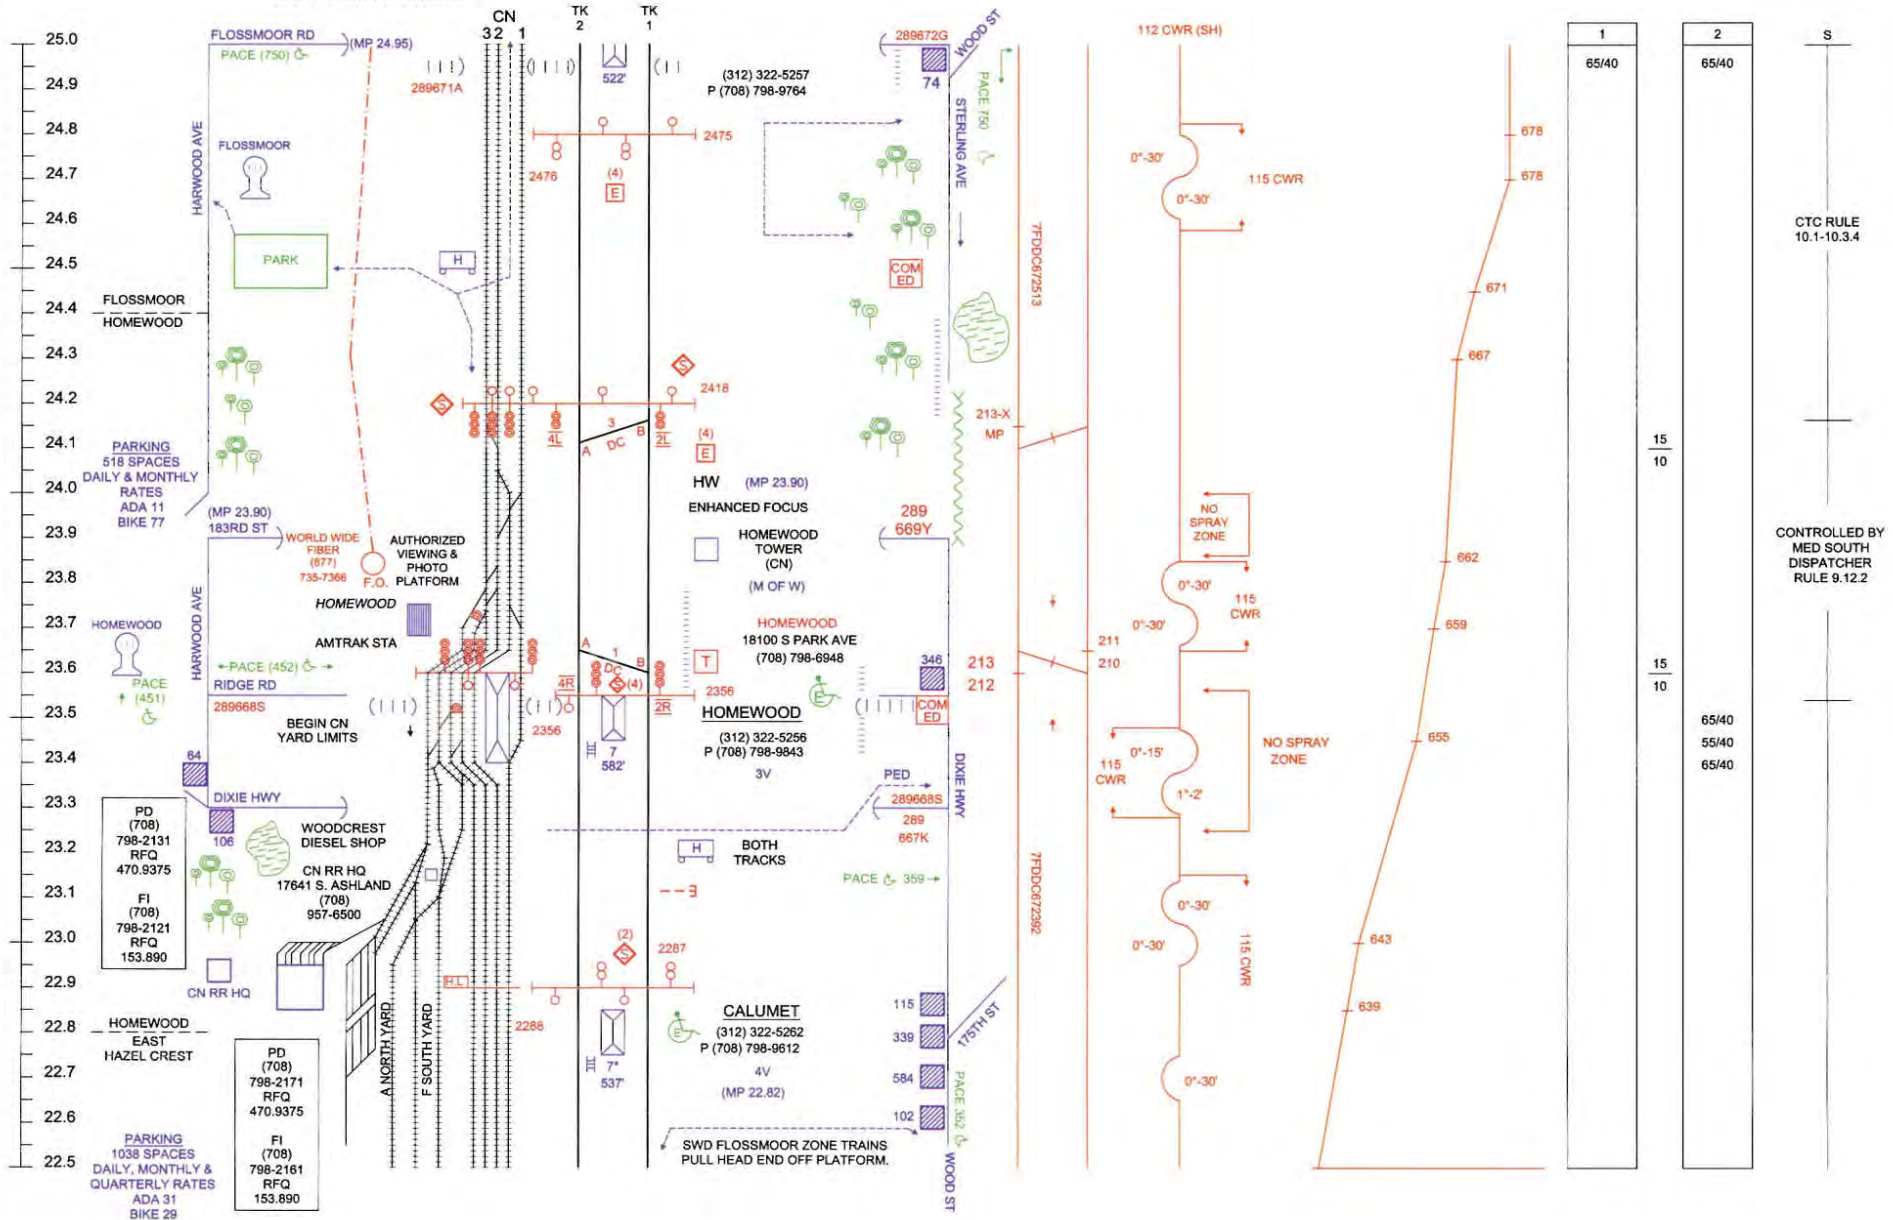

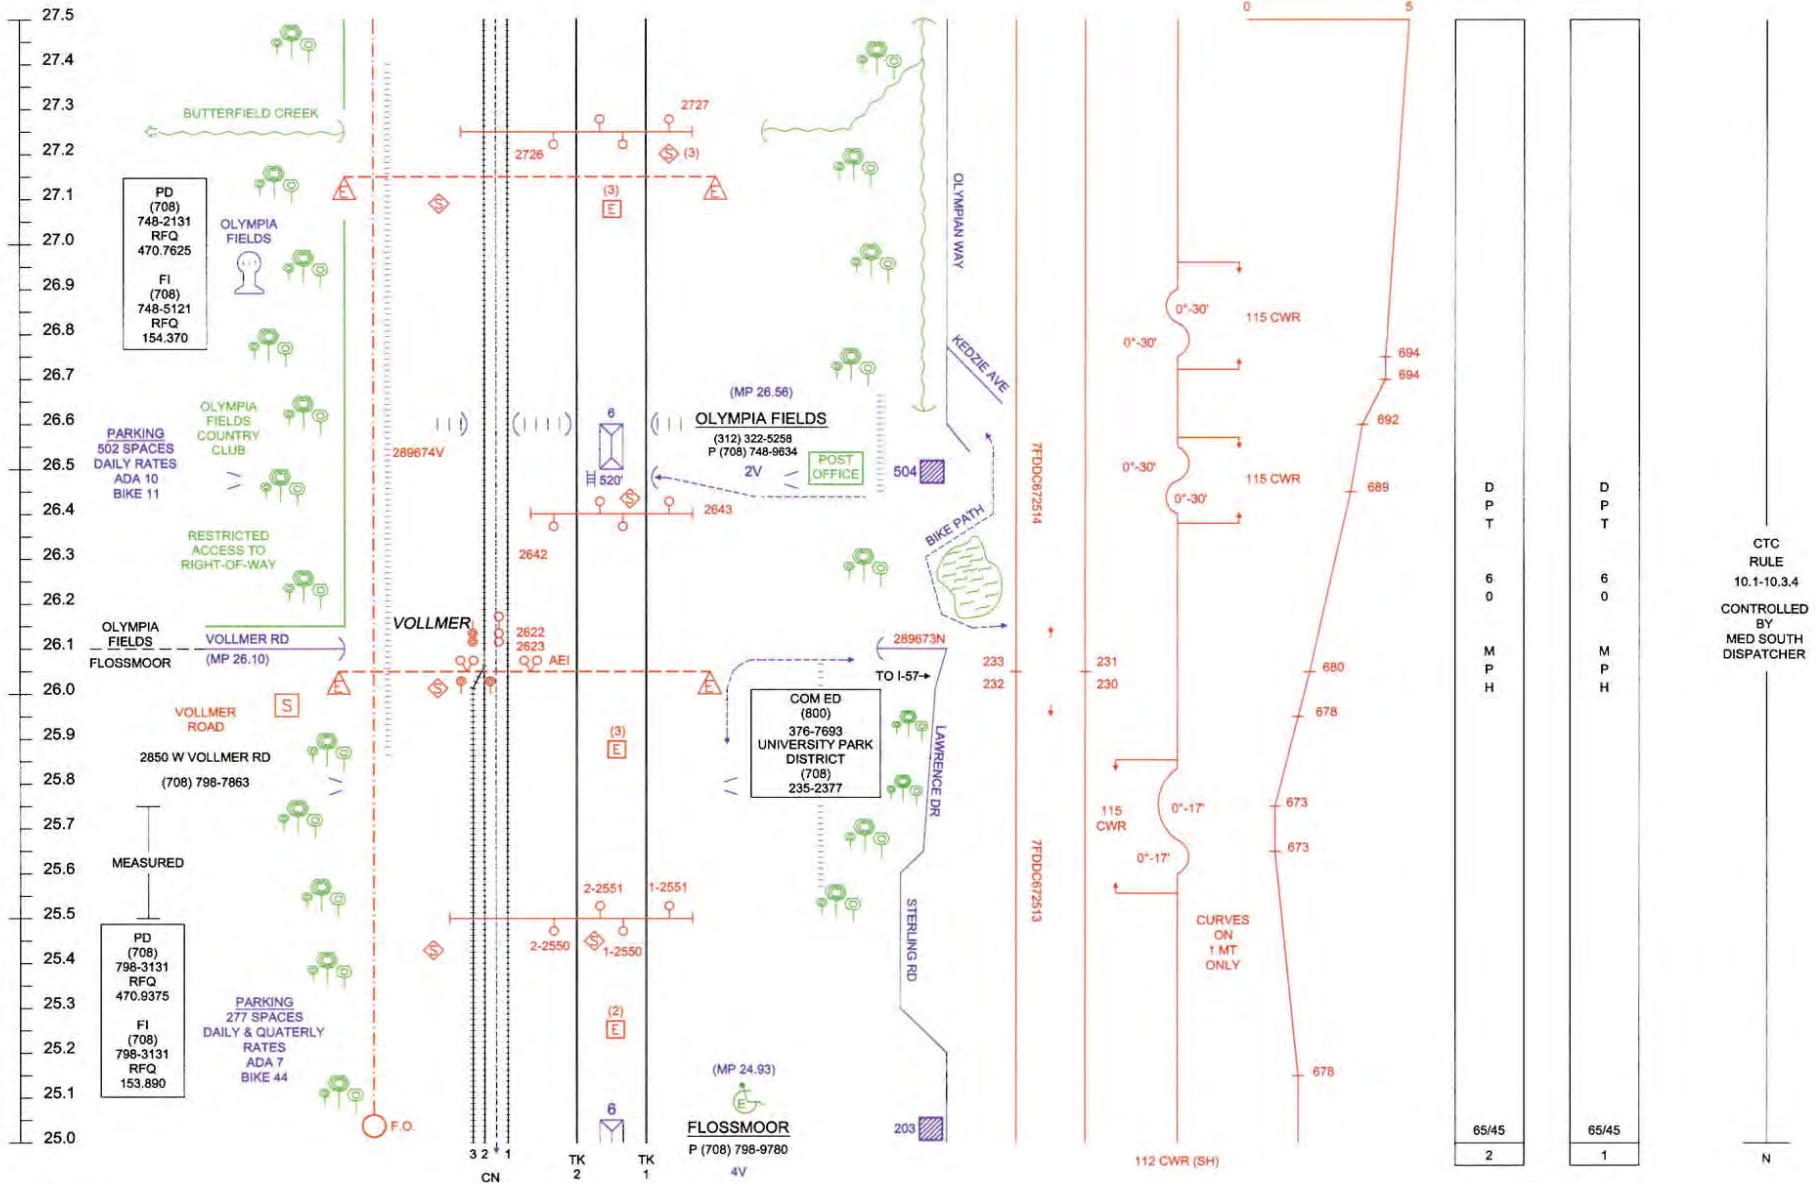

FARE ZONE F


© S L
2 19 38

3507

ELECTRIC DISTRICT / UNIVERSITY PARK SUBDISTRICT

P-24

CN TRAIN SPEEDS:
79/50 MPH ON TRACK 1
40/40 MPH ON TRACKS 2&3
10 MPH ON OTHER TRACKS

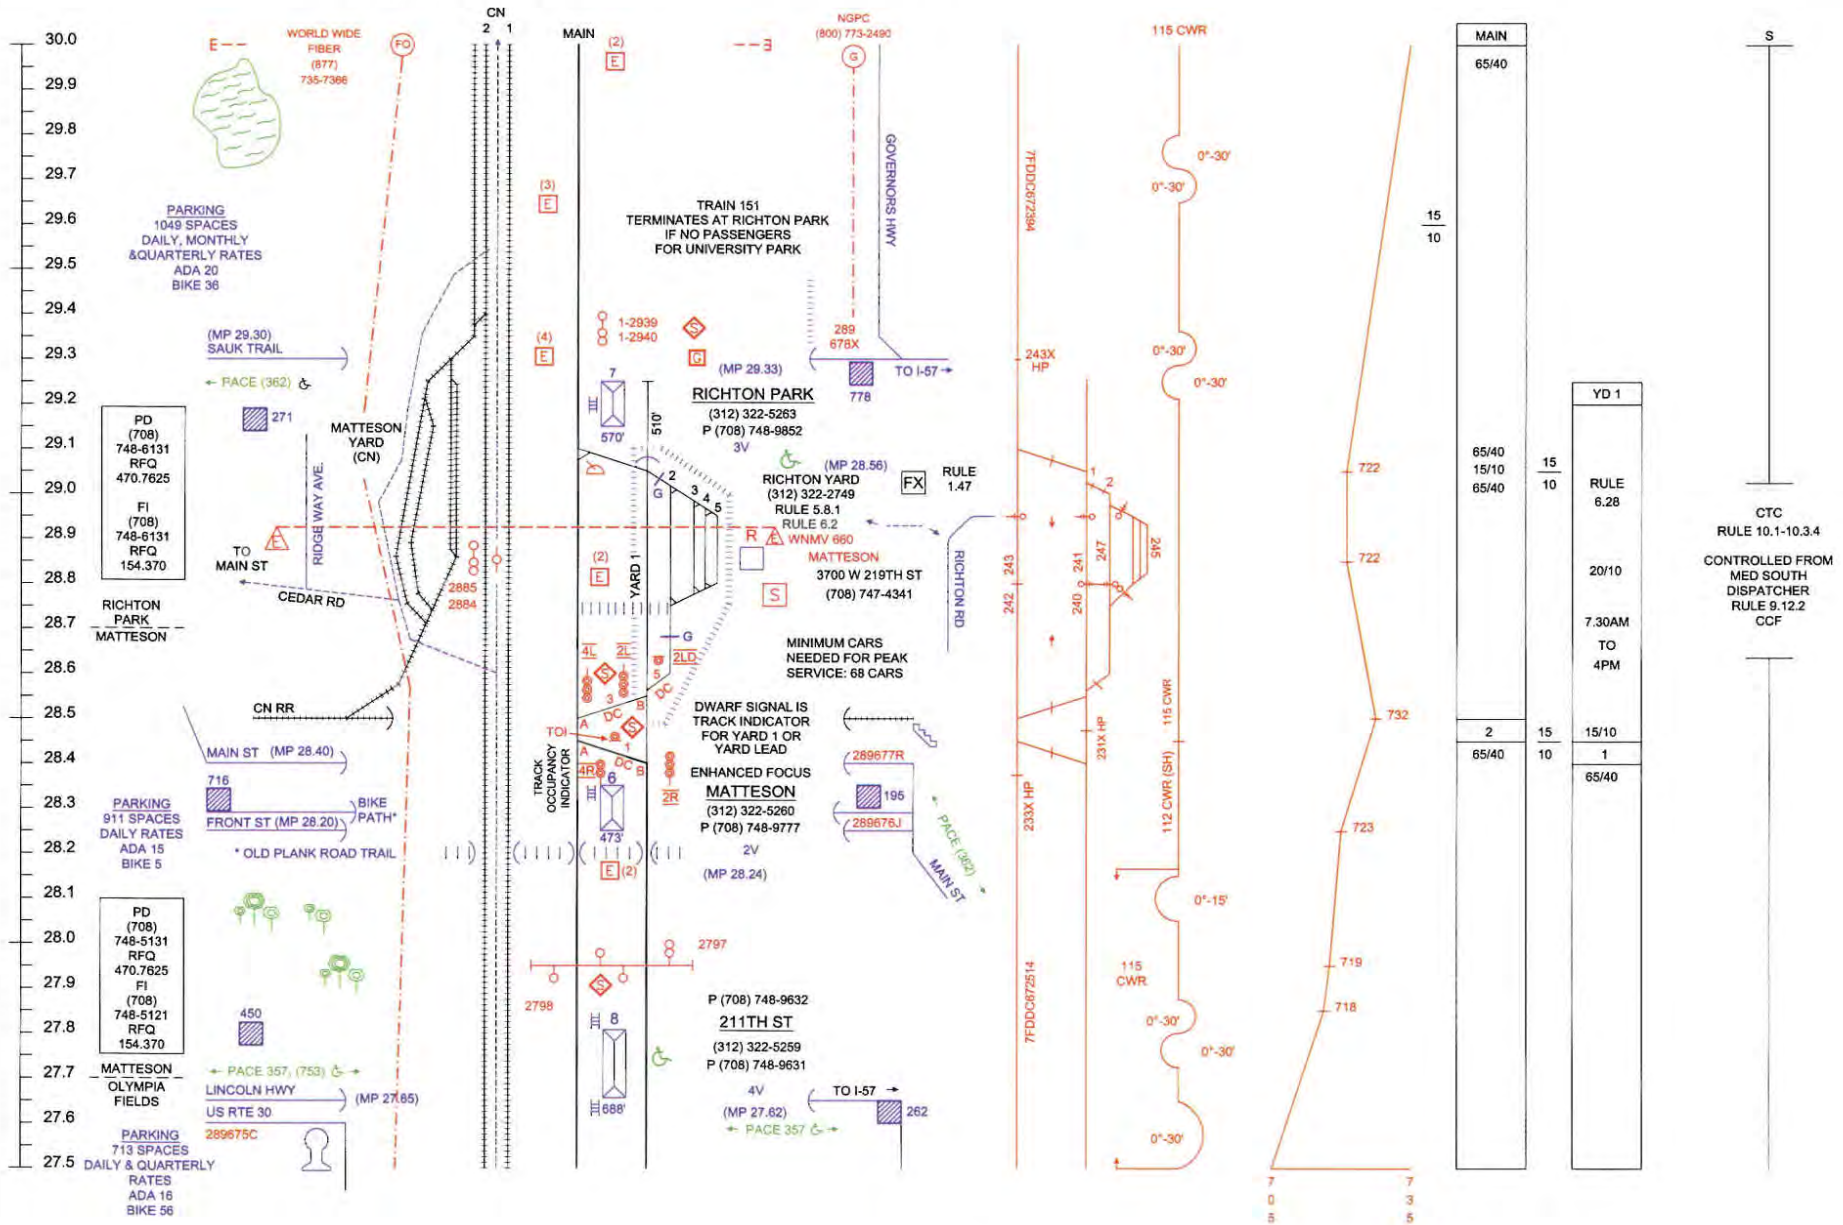



IF SIGNAL IS
'STOP' CALL 67TH ST
RULE 9.12.4, 9.12.5

CN MED
MAIN LINE

(C) (S) (L) (W)
2 13 25 5,7

ELECTRIC DISTRICT / SOUTH CHICAGO SUBDISTRICT

REV 05/20/09

P-32

(C)	(S)	(L)	(W)
2	16	31	7,10


3215
3216

REV 7/27/09

P-33



G1- GATE INDICATORS AS PER RULE 6.32.2
*REAR DOOR IS OFF PLATFORM

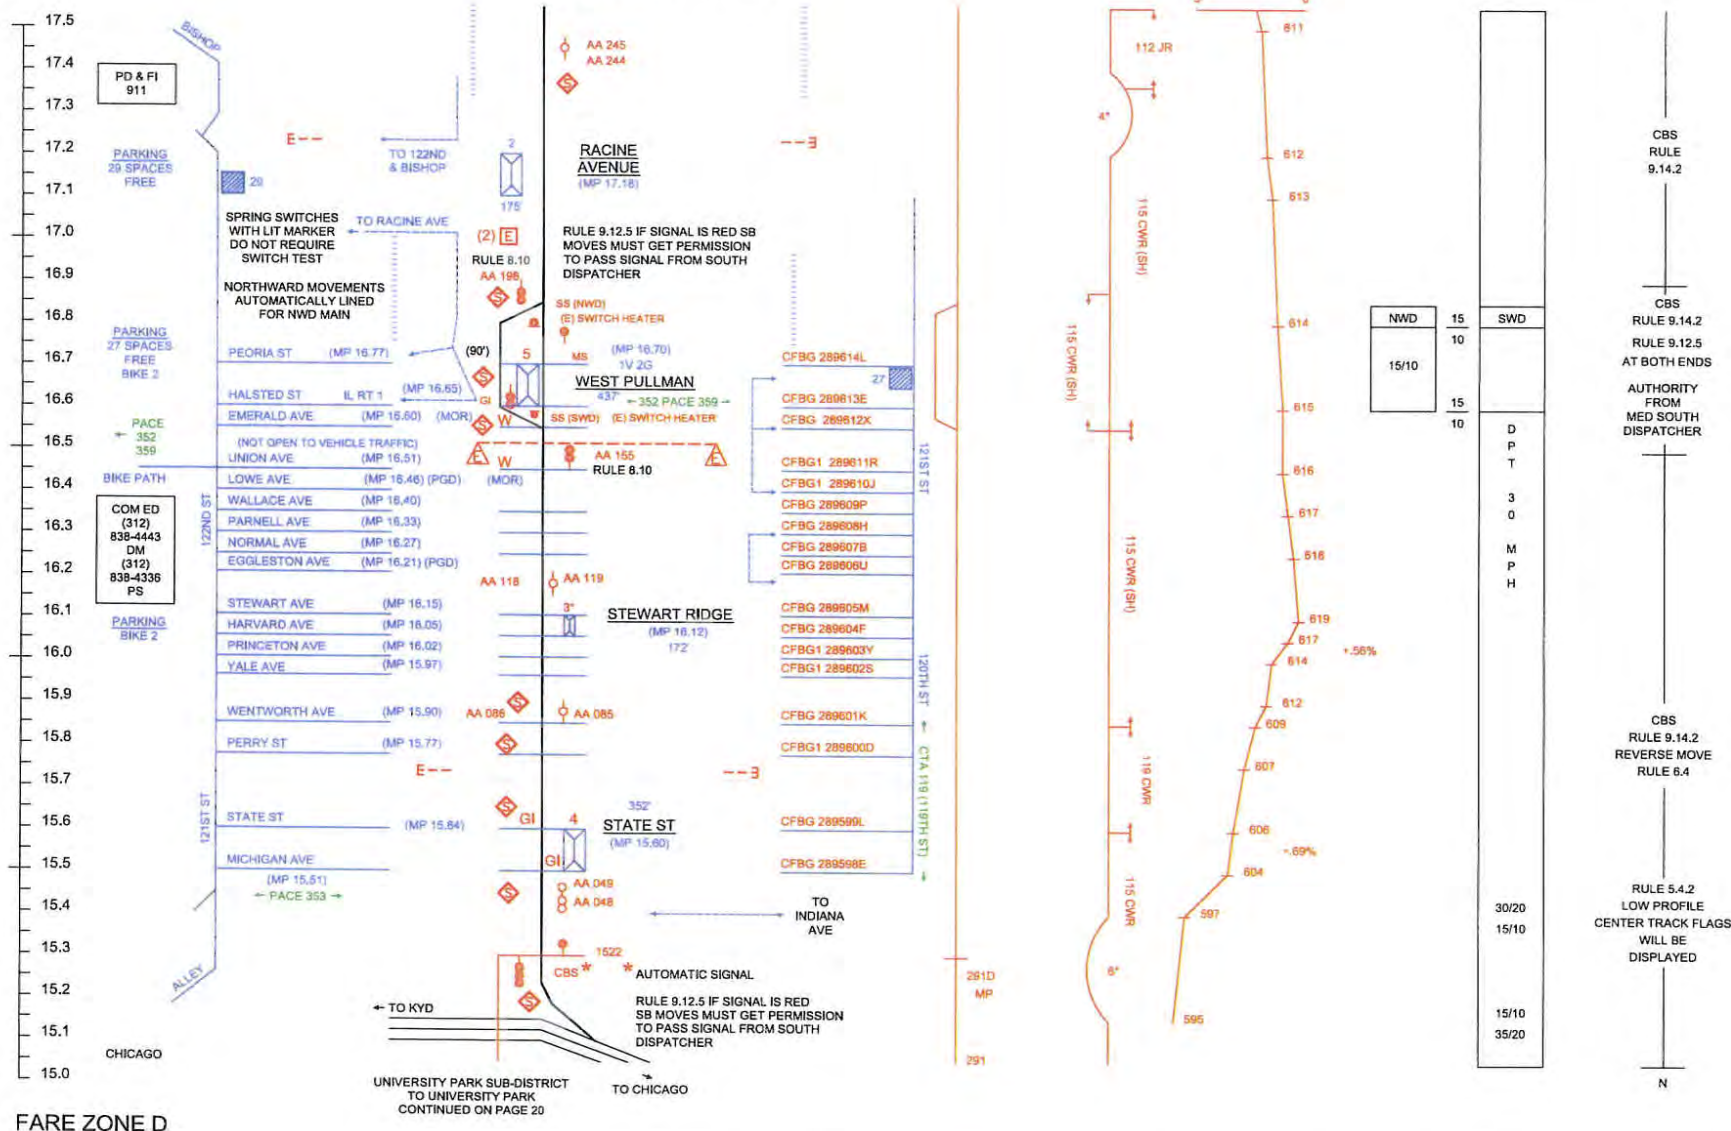

NOTE: BLUE ISLAND CONTINUED ON PAGE 18 IN RID OPS PRO.

BLUE ISLAND CONNECTION:

TRAIN NO. 501 CARRIES AN AVERAGE OF SOME TWENTY-FIVE PASSENGERS WHO CONNECT WITH ROCK ISLAND DISTRICT NO. 411, WHICH DEPARTS BLUE ISLAND AT 5:45 P.M. WHENEVER TRAIN NO. 501 IS RUNNING LATE, THERE IS A QUESTION AS TO WHETHER OR NOT THESE PASSENGERS WILL MAKE THE CONNECTION. THE CONDUCTOR WILL IMMEDIATELY NOTIFY METRA ELECTRIC SOUTH DISPATCHER, ADVISING HIS EXPECTED ARRIVAL TIME TO BLUE ISLAND. WHEN SO NOTIFIED, METRA ELECTRIC SOUTH DISPATCHER WILL NOTIFY THE ROCK ISLAND DISTRICT BLUE ISLAND TOWER OPERATOR AT 708-293-6180 OR AT 708-388-7434, ADVISING OF THE EXPECTED ARRIVAL TIME OF TRAIN 501. THE TOWER OPERATOR SHOULD THEN ADVISE THE METRA ELECTRIC SOUTH DISPATCHER WHETHER HE WILL HOLD TRAIN NO. 411 OR MAKE ARRANGEMENTS FOR TRAIN 413 OR 415 TO PICK UP THE PASSENGERS. METRA ELECTRIC SOUTH DISPATCHER WILL RELAY THIS INFORMATION TO THE CONDUCTOR OF TRAIN 501 SO THAT PASSENGERS WILL BE KEPT INFORMED.

MINIMUM CARS NEEDED FOR PEAK SERVICE: 14 CARS

RULE 9.1 NOT IN EFFECT ON SUB-DISTRICT

RULE 9.14.2 CONTACT MED SOUTH DISPATCHER WHEN
ARRIVING AND DEPARTING BLUE ISLAND.
MAKE NOTE OF AUTHORIZATION ON BACK OF TRACK WARRANT.
USE FORM RC99081

**RULE 6.32.2 WHEN CROSSING GATES FAIL
USE OF TORPEDOES IS PROHIBITED**

TRAINMENS ROOM
(312) 322-2761
P (708) 385-9539
BLUE ISLAND
(MP 18.95)

AUTHORITY FOR NB MOVEMENT
GIVEN VERBALLY
FROM SOUTH DISPATCHER
FOR TRACK PERMIT USE RC 99081

ROCK ISLAND DISTRICT
JOLIET SUBDISTRICT
CONTINUED ON PAGE 62
BI-CTC (312) 322-7780
RFQ 161.610
AAR RADIO CH 99

