



NOTICE:
BLUE DOT DENOTES A LINK
THROUGHOUT THIS CD



NOTICE:
CLICK ON THIS SYMBOL
FOR NOTES AND WARNINGS
THROUGHOUT THIS CD

OPERATIONS PROFILE

W. K. TUPPER Chief Operations Officer G.L. HARDWIDGE Chief Transportation Officer

S.A. AUSTIN Sr. Director, Customer Services/System Security

D.A. ORSENO Chief, Safety & Rules Officer

CUS SERVICES-NORTH

TABLE OF CONTENTS

- MILWAUKEE DISTRICT (CUS) 8
 - North Line (C&M) (FL) 11
 - West Line (ELGIN) 36
- OTHER CUS LINES
 - North Central Service (CN) 54
- INDEX 73

August 15, 2008

PROJECT MANAGER & CHIEF DESIGNER:

J. M. GOTTLIEB

OPERATING RULES DATA:

L. C. MICHAEL

COMPLIANCE, EDITING & REORGANIZATION:

L. G. GOMM, R. P. OPPENHEIM

FIELD VERIFICATION TEAM:

METRA POLICE DEPT.

(for off right-of-way locations)

J. S. TALLYN, R. P. OPPENHEIM,

T. G. PITZEN, M.B. MINOR


GRADE CROSSING DATA:

S. C. LAFFEY - ICC


PARKING LOT DATA:

L. G. GOMM, M. C. PALMER

Operations Profile represents Metra's compliance with **49CFR239** governing emergency preparedness specific to geographic locations on specific line segments.

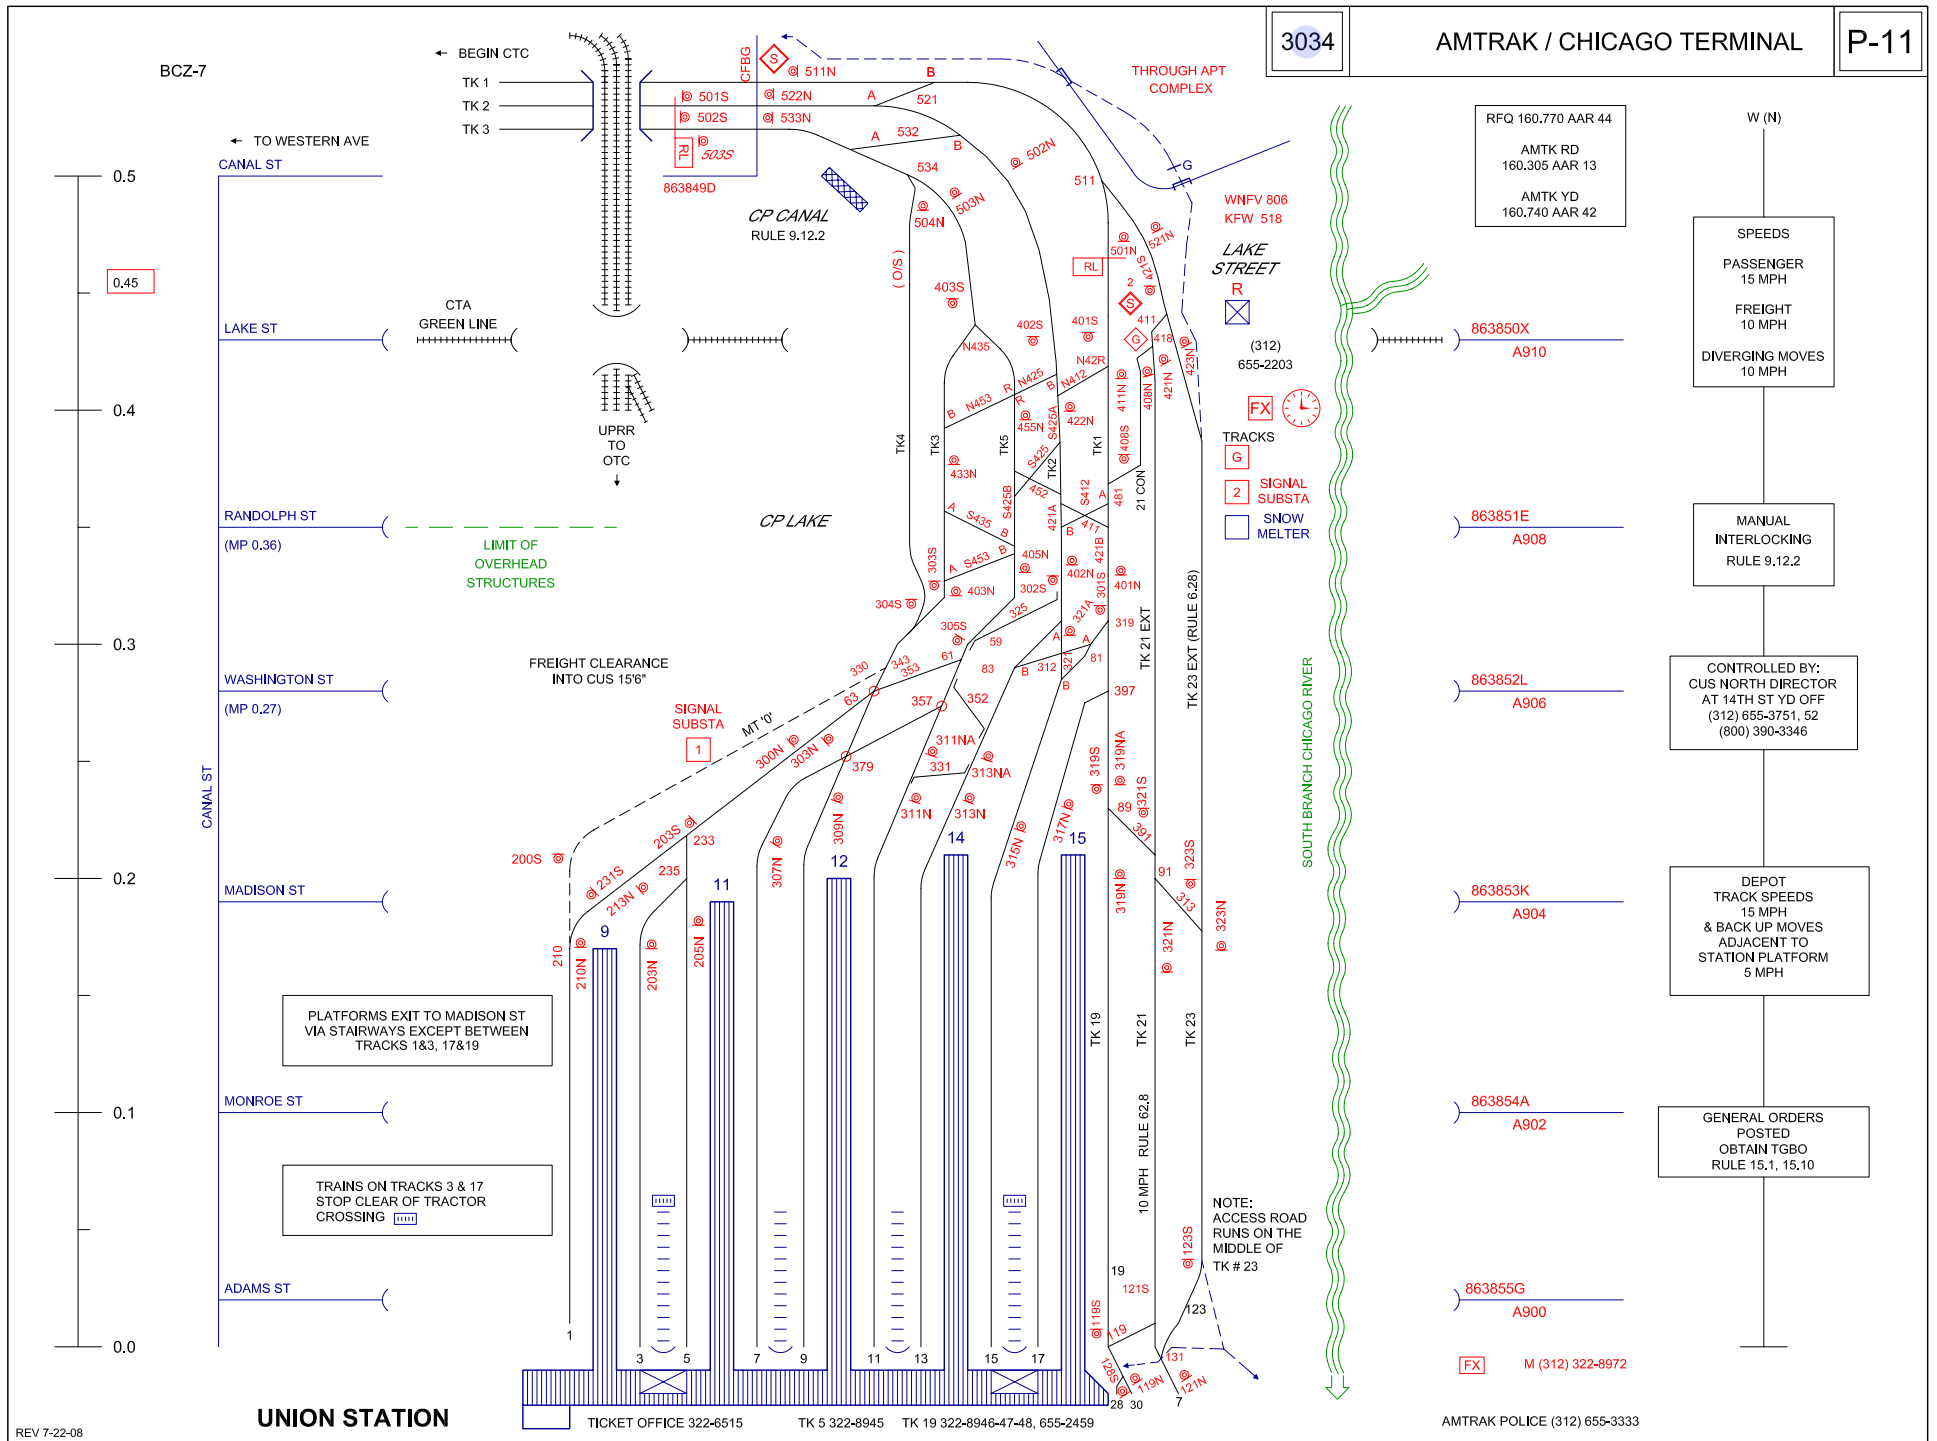



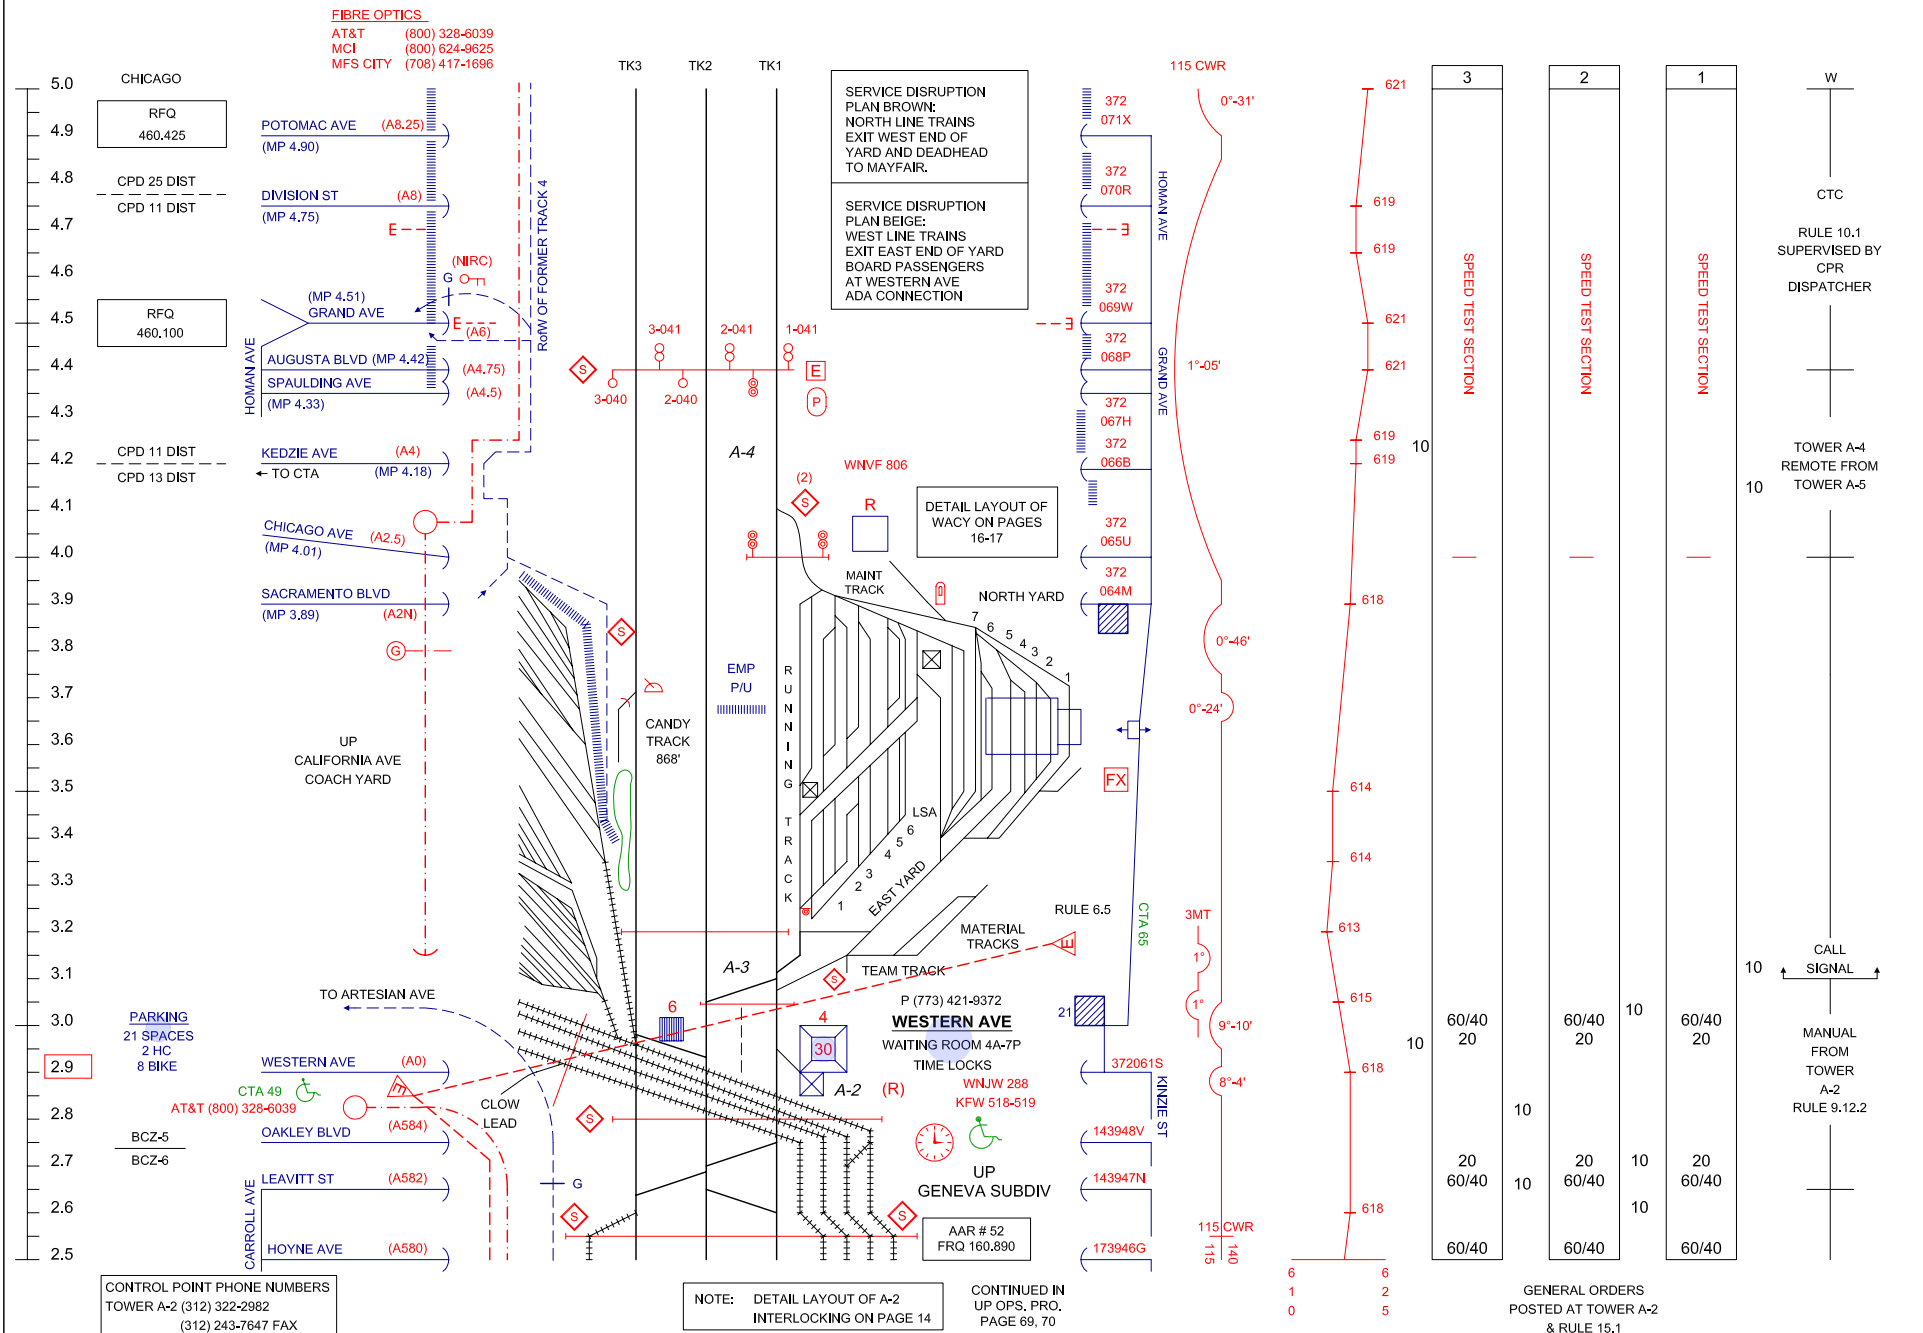


TOWER A-2 (312) 322-2982

METRA TRAINS WILL NOT REQUIRE
A TRACK WARRANT AT TOWER A-2.

ALL ENGINES AND EMPTY EQUIPMENT MOVES
LEAVING WESTERN AVE COACH YARD DESTINED
FOR POINTS EAST OF TOWER A-2 MUST HAVE A
CPR TGBO FOR THAT TERRITORY, AND MUST
CONTACT TRAIN DIRECTOR AT TOWER A-2,
BEFORE PASSING TOWER A-2 TO ASCERTAIN IF
ANY CHANGES TO THEIR TGBO'S ARE IN EFFECT.


DO NOT RIDE
ON SIDE OF
EQUIPMENT

RESTRICTED
CLEARANCE
BETWEEN
TRACKS 2 & 3
AT DEPOT

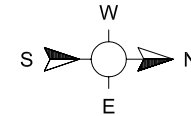


RUNNING
TRACK
TO
WESTERN
AVE
COACH
YARD
(METRA)

STATION ADDRESS
420 N. ARTESIAN

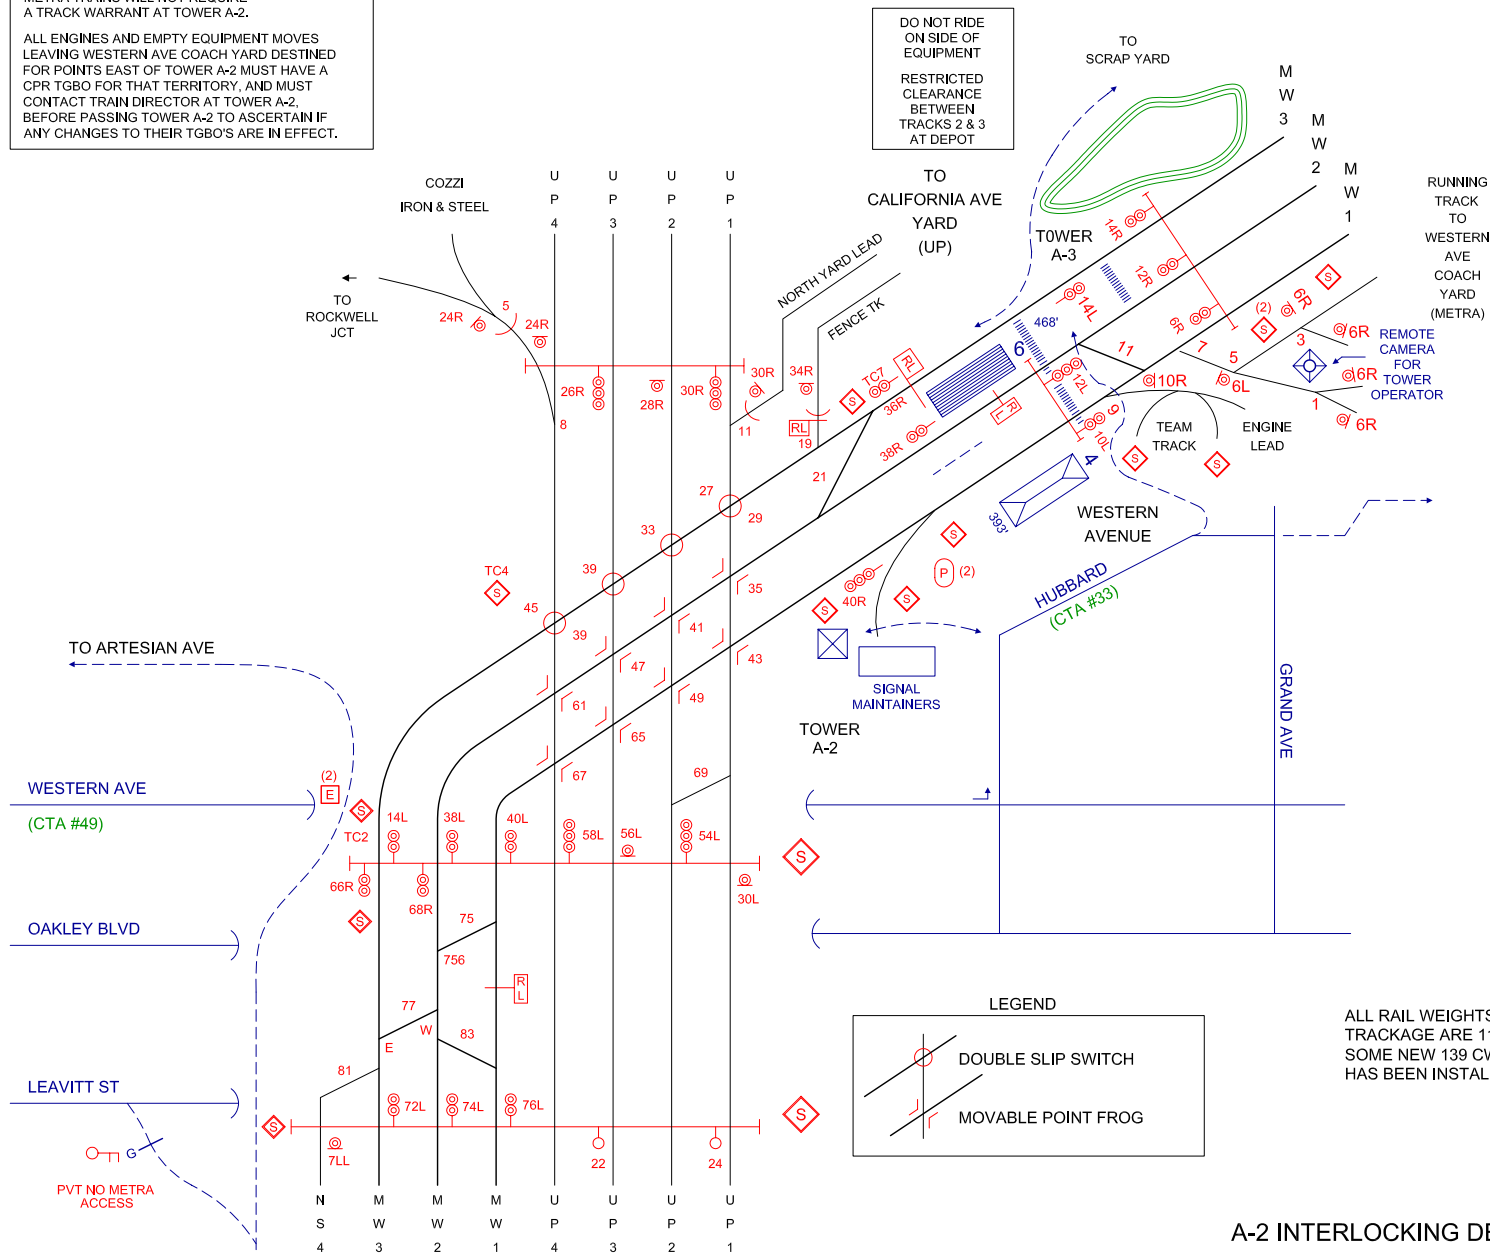

A-2 INTERLOCKING DETAIL VIEW

A-5 INTERLOCKING DETAIL VIEW

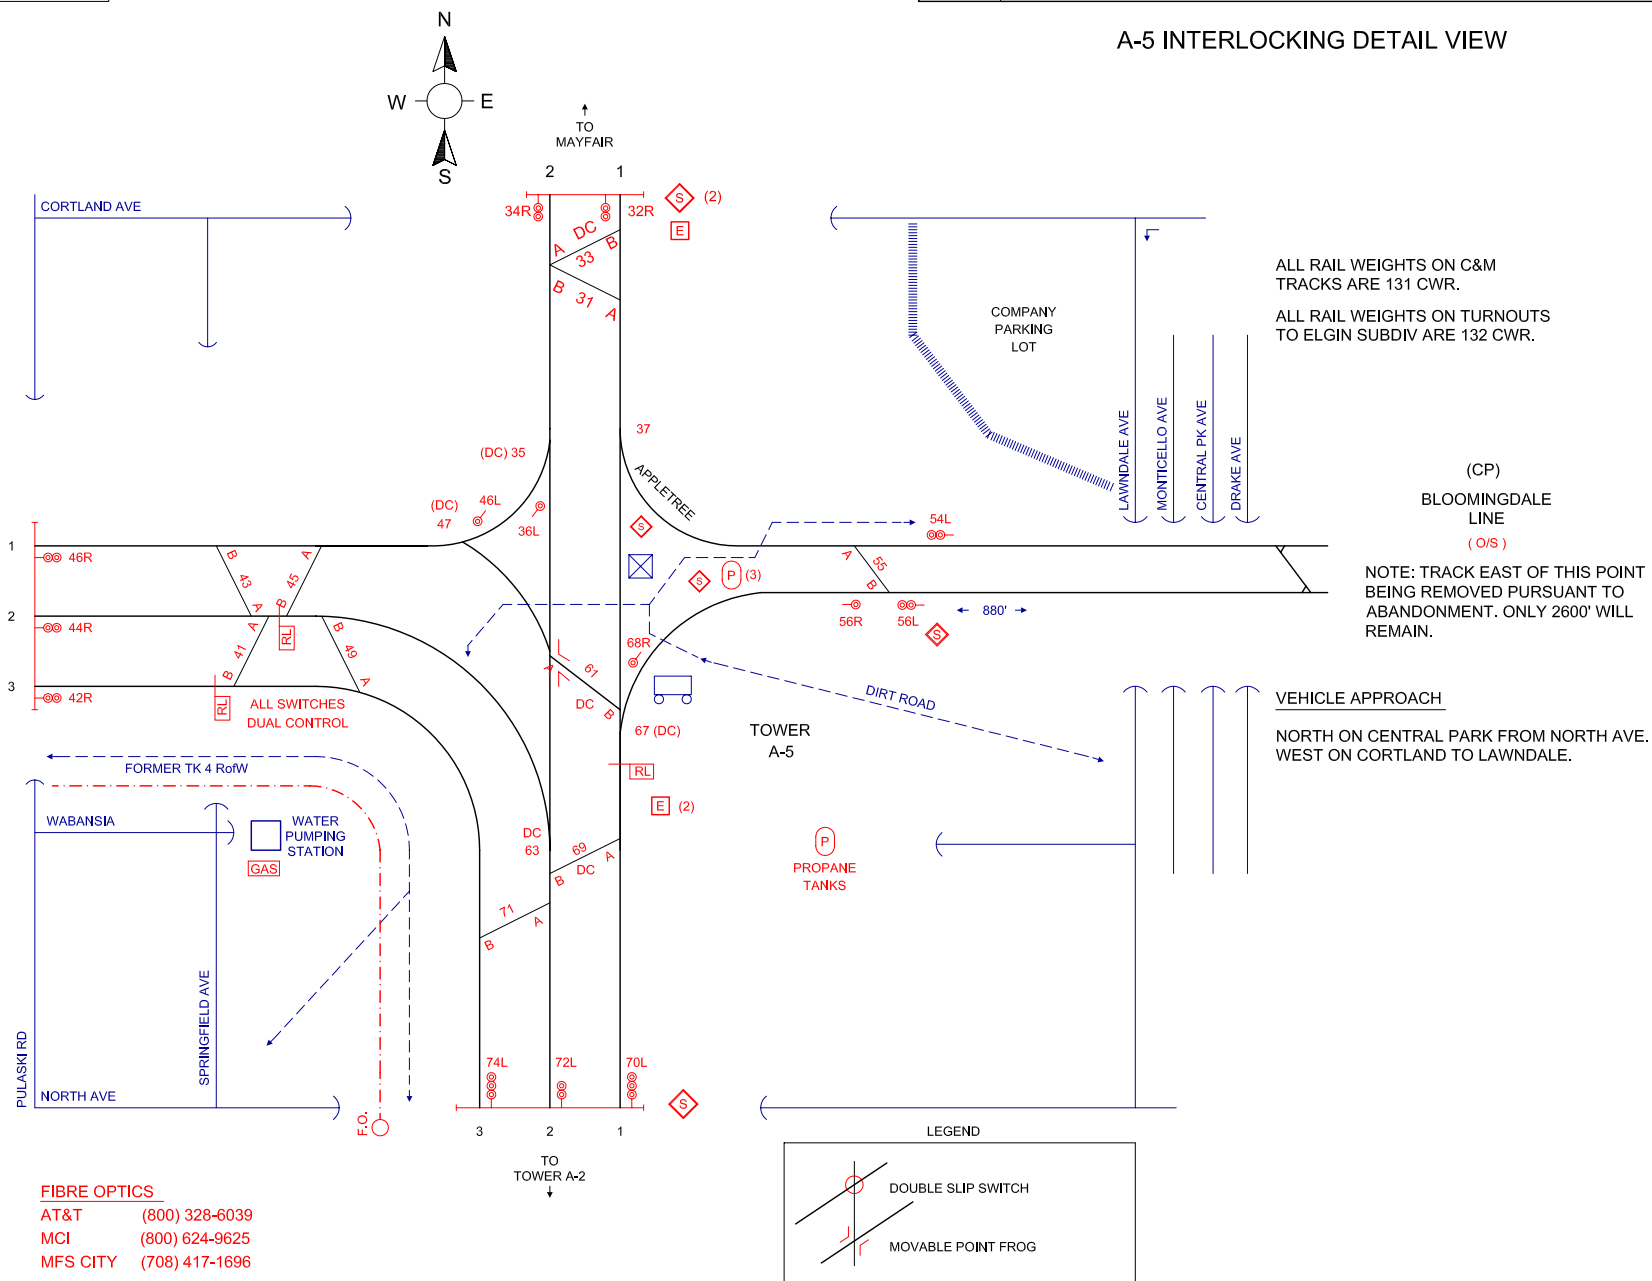

FIBRE OPTICS

AT&T (800) 328-6039
MCI (800) 624-9625
MFS CITY (708) 417-1696

ENGINE WILL DISPLAY HEADLIGHT DURING DAYLIGHT HOURS.

IN ADDITION TO PROVISIONS OF RULE 5.8.1, IN ORDER TO PROVIDE ADDITIONAL WARNING, ENGINE OR CONTROL CAR BELL WILL BE RUNG CONTINUOUSLY WHILE MOVING ON TRACK 6 NORTH.

THE PROVISIONS OF RULE 6.5 OF THE GENERAL CODE OF OPERATING RULES APPLY IN WESTERN AVENUE COACH YARD. PRIOR TO SHOVING TRACKS, A CONDUCTOR (PILOT) MUST PROVIDE PROTECTION IN ADVANCE OF THE MOVEMENT.

WHEN LOCOMOTIVES ARE BACKED OR SHOVED INTO YARDS TRACKS, A CONDUCTOR (PILOT) WILL RIDE THE LEADING END OF THE MOVEMENT THROUGH THE SWITCH AND PAST THE DERAIL TO INSURE THE ROUTE IS PROPERLY LINED AND CLEAR.

NORMAL POSITIONS OF ALL "LEAD" SWITCHES WILL BE LINED FOR THE "LEAD". EMPLOYEES HANDLING "LEAD" SWITCHES WILL RESTORE THEM TO NORMAL POSITION AFTER USE.

ALL VARIABLE AND HAND OPERATED SWITCHES IN THE COACH YARD AND DIESEL HOUSE AREAS MUST BE HAND OPERATED BEFORE MOVEMENT IS MADE THROUGH THEM.

EXCEPT IN AREAS WHERE HOSTLER HELPERS ARE ON DUTY, ALL LIGHT ENGINE MOVEMENTS WILL HAVE A CONDUCTOR (PILOT) HANDLE ALL SWITCHES TO PROTECT ROUTE TO BE USED.

UNLESS THE LEADING END OF THE MOVEMENT IS BEING PROTECTED BY A SWITCHMAN/PILOT OR MECHANICAL DEPARTMENT EMPLOYEE, ALL LIGHT ENGINES MAKING EWD MOVEMENTS INTO THE FUELING/SANDING AREAS OF SHOP TRACKS 6 AND 7, AT THE WESTERN AVENUE DIESEL HOUSE, WILL COMMUNICATE BY RADIO, ON THE METRA YARD CHANNEL, WITH THE MECHANICAL DEPARTMENT EMPLOYEE IN CHARGE OF THE DERAILS TO ASCERTAIN THE POSITION OF DERAILS AT WEST END OF THESE TRACKS.

IF UNABLE TO CONTACT THE MECHANICAL DEPARTMENT EMPLOYEE IN CHARGE BY RADIO, EWD LIGHT ENGINE MOVEMENTS WILL APPROACH DERAILS AT THE WEST END OF SHOP TRACKS 6 AND 7 EXPECTING TO FIND THE DERAILS IN THE DERAILING POSITION.


WHEN HANDLING ENGINES FROM THE DIESEL HOUSE TO THE COACH YARD, THE FOLLOWING WILL APPLY: (1) THE AIR MUST BE TRAIN LINED AND CUT ON ALL ENGINES. (2) NO MORE THAN FOUR COUPLED TOGETHER WILL BE HANDLED AT ONE TIME AND (3) A CONDUCTOR PILOT MUST HANDLE THE MOVE.

WHEN ENGINES ARE COUPLED TO TRAINS, IN ANTICIPATION OF DEPARTURE FROM YARD THE FOLLOWING WILL BE DONE: HAND BRAKE MUST BE SET, INDEPENDENT BRAKE MUST BE SET, AUTOMATIC BRAKE VALVE WILL BE LEFT IN RELEASE POSITION AND CUT IN, GENERATOR FIELD SWITCH WILL BE LEFT IN THE OFF POSITION.

UNLESS OTHERWISE INSTRUCTED, AFTER UNCOUPLING FROM TRAINS EACH ENGINE SERVICE ASSIGNMENT WILL BE RESPONSIBLE FOR MOVING THEIR OWN ENGINE TO THE DESIGNATED ENGINE TIE-UP AREA.

ENGINEERS WORKING WITHOUT A FIREMAN WILL NOTIFY THE YARDMASTER AT WESTERN AVENUE COACH YARD. ON ARRIVAL, TO ARRANGE FOR A CONDUCTOR (PILOT) IF THEIR ASSIGNMENT INCLUDES A LIGHT ENGINE MOVEMENT FROM WESTERN AVENUE COACH YARD TO CHICAGO UNION STATION.

THE LADDER LEADING TO THE YARDMASTER'S OFFICE ON THE OUTSIDE OF THE DIESEL/COACH SHOP BUILDING IS FOR EMERGENCY USE ONLY. THE LADDER WILL NOT BE USED AS A CONVENIENCE BY EMPLOYEES GOING IN OR OUT OF THE YARDMASTER'S OFFICE.

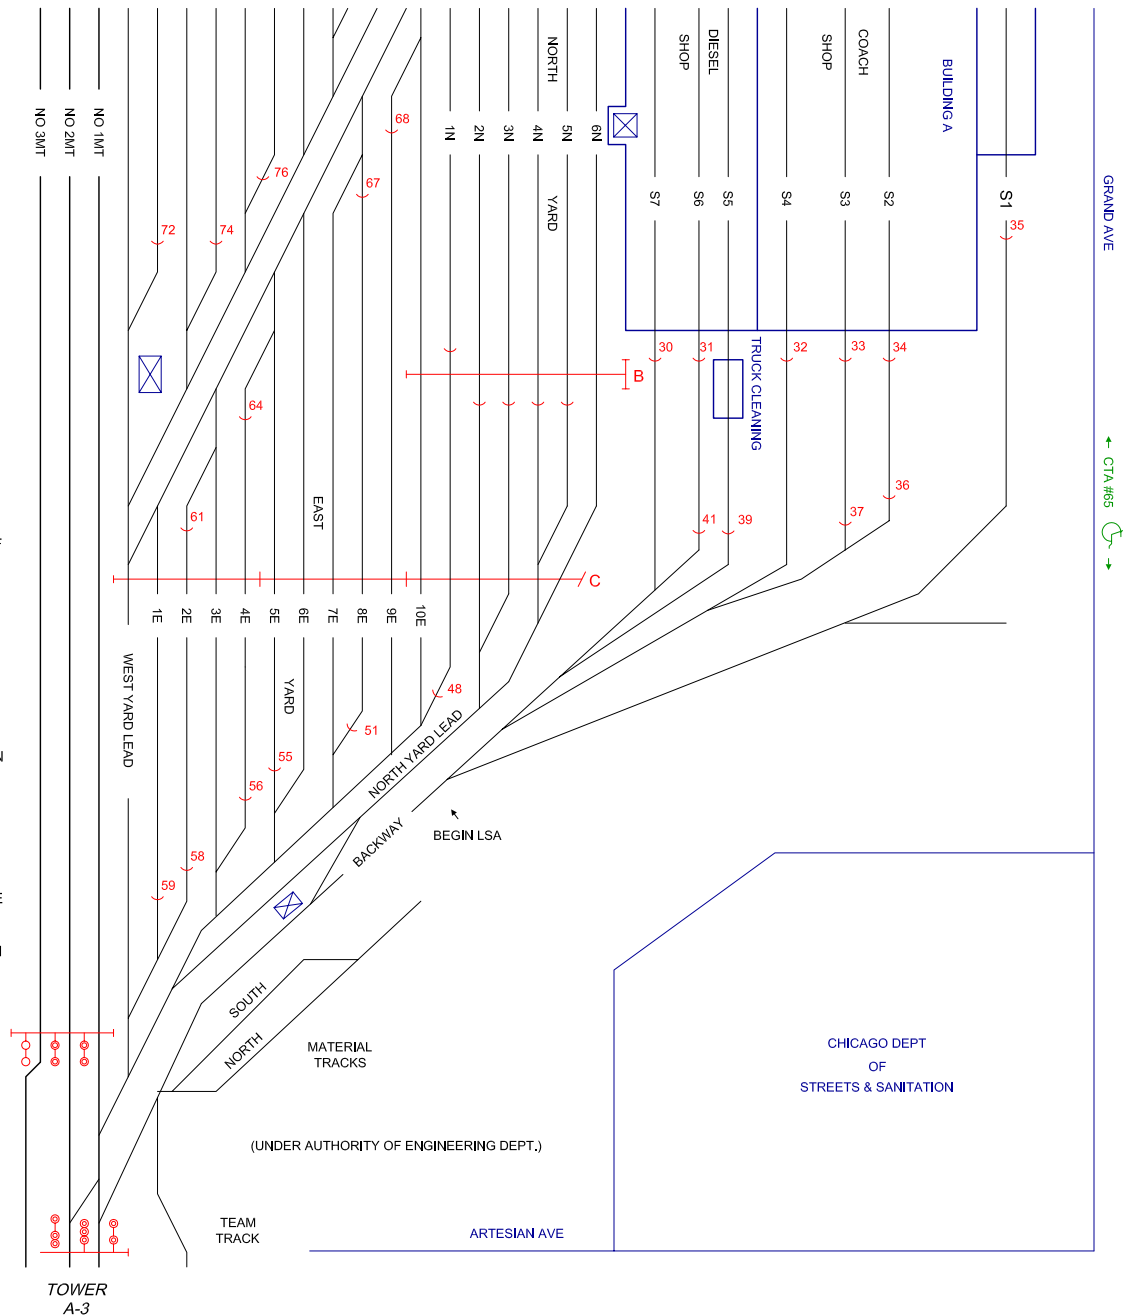

COACH YARD
(312) 322-4120
YARDMASTER
(312) 322-4113
FAX
(312) 542-8338

GRAND AVE
CTA #65
CHICAGO DEPT
OF
STREETS & SANITATION
ARTESIAN AVE




CONTROL POINT PHONE NUMBERS
 CUS YARDMASTER (312) 322-8946-47-48
 TOWER A-5 (312) 322-2985 (773) 278-6793
 CPR DISPATCHER (612) 904-5830 (877) 588-9129

RFQ 460.475

RFQ 160.770 AAR 44

CPR DISP FAX (612) 904-5882

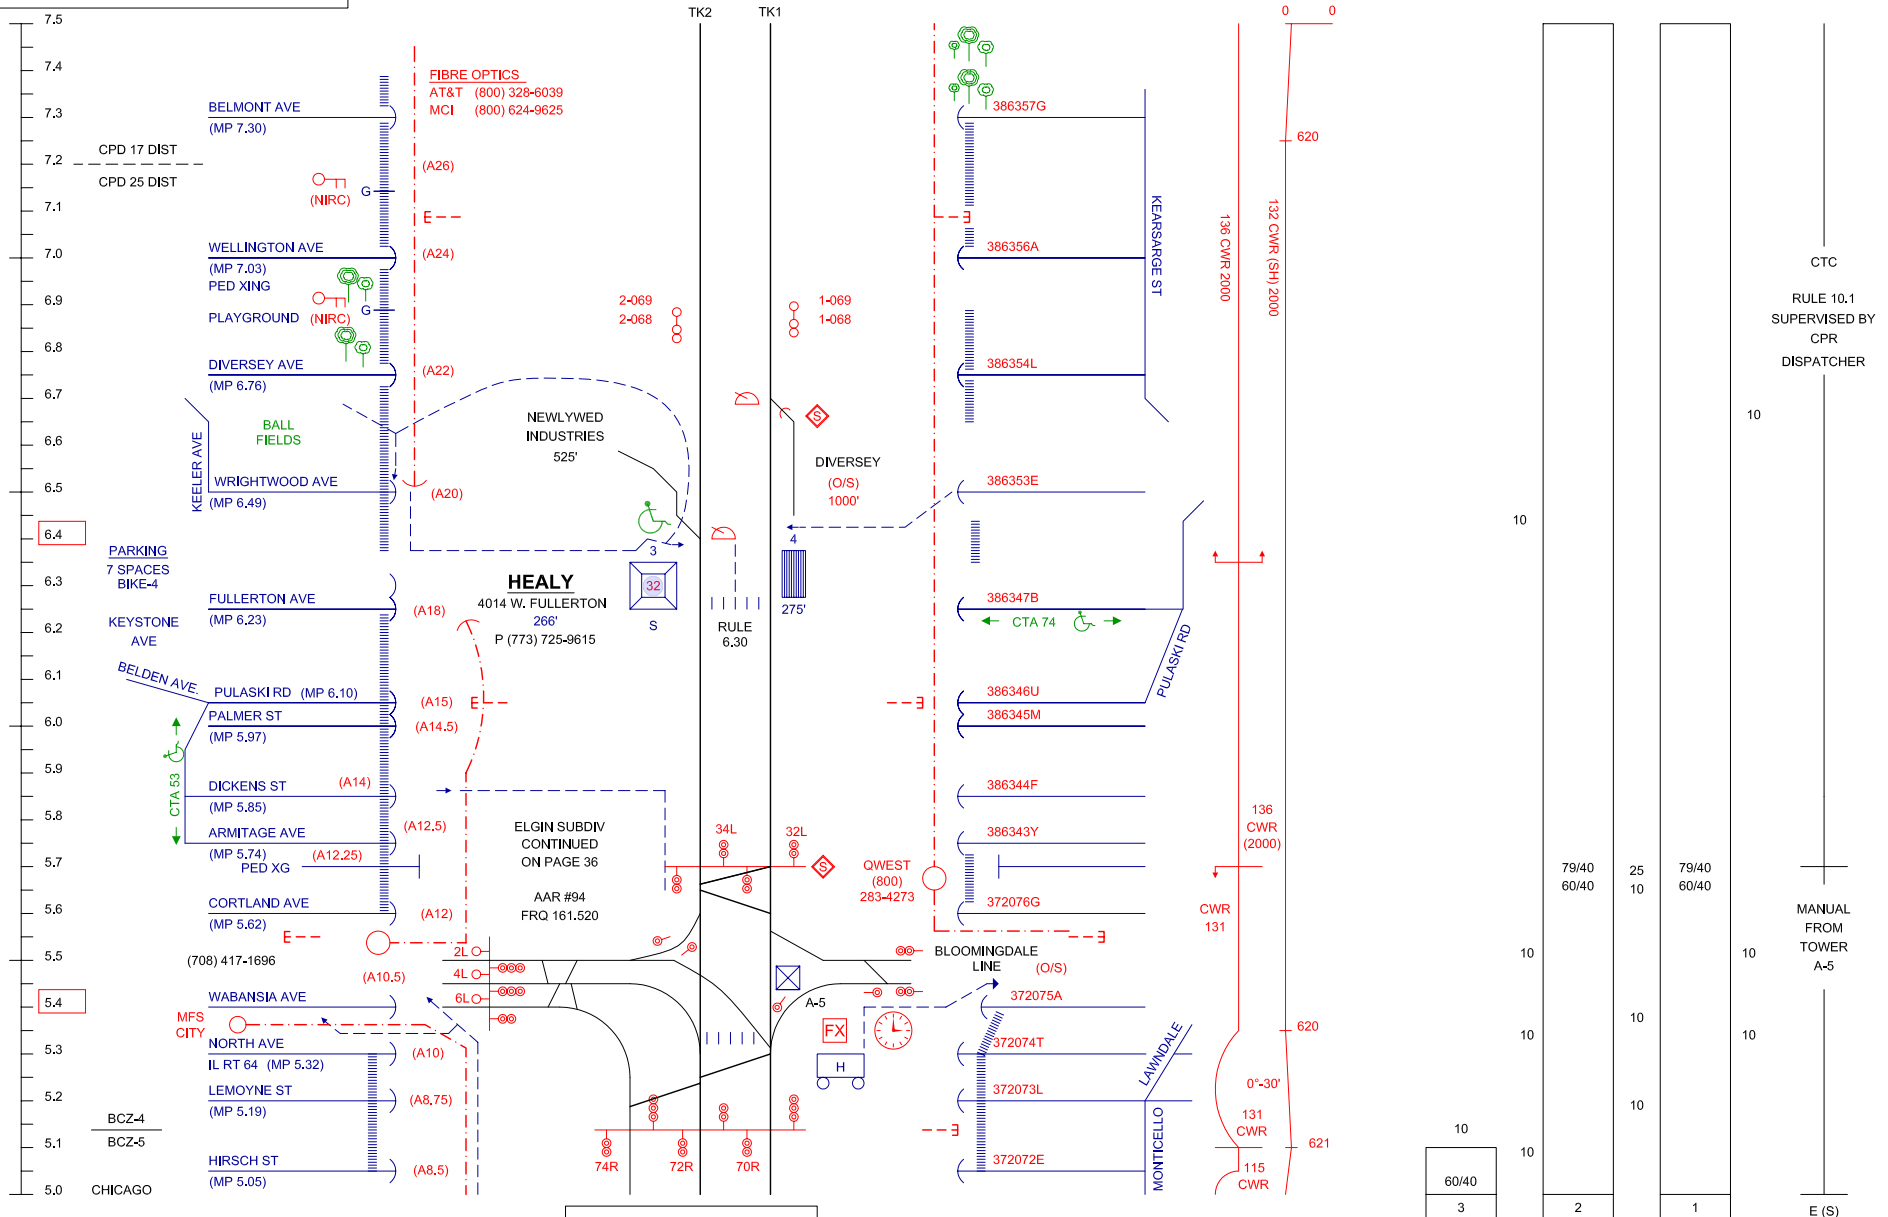

FARE ZONE B


C S L W
 4 2 4 26,30,31

2976
 3032

MILWAUKEE DISTRICT / (CPR) C&M SUBDIVISION

P-18

QWEST
(800)
283-4273

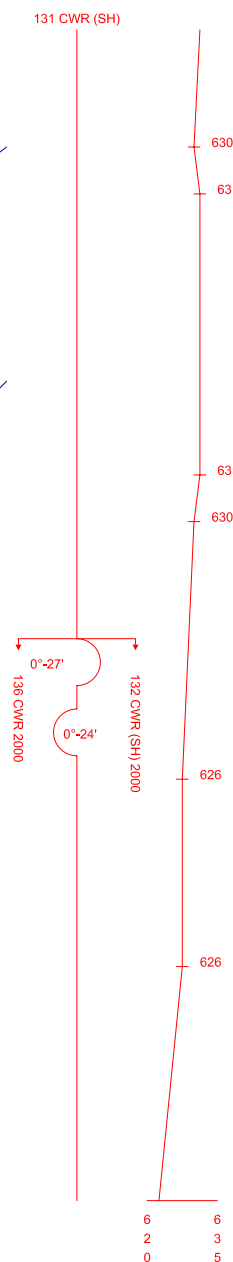

10

CTC
RULE 10.1
SUPERVISED BY
CPR
DISPATCHER

MANUAL FROM
TOWER A-5

REMOTE FROM
CY
TOWER
UPRR
RULE
9.12.2

REMOTE FROM
CP RAIL
DISPATCHER

CTC
RULE 10.1
REMOTE FROM
CP RAIL
DISPATCHER


W (N)

REV 7-22-08

CONTROL POINT PHONE NUMBERS
 CUS YARDMASTER (312) 322-8946-47-48
 CPR DISPATCHER (612) 904-5830
 (877) 588-9129

NOTE: EWD TRAINS O/S CY FROM EDGEBROOK
 FOR PASSAGE THRU MAYFAIR.

RFQ 160.770 AAR 44

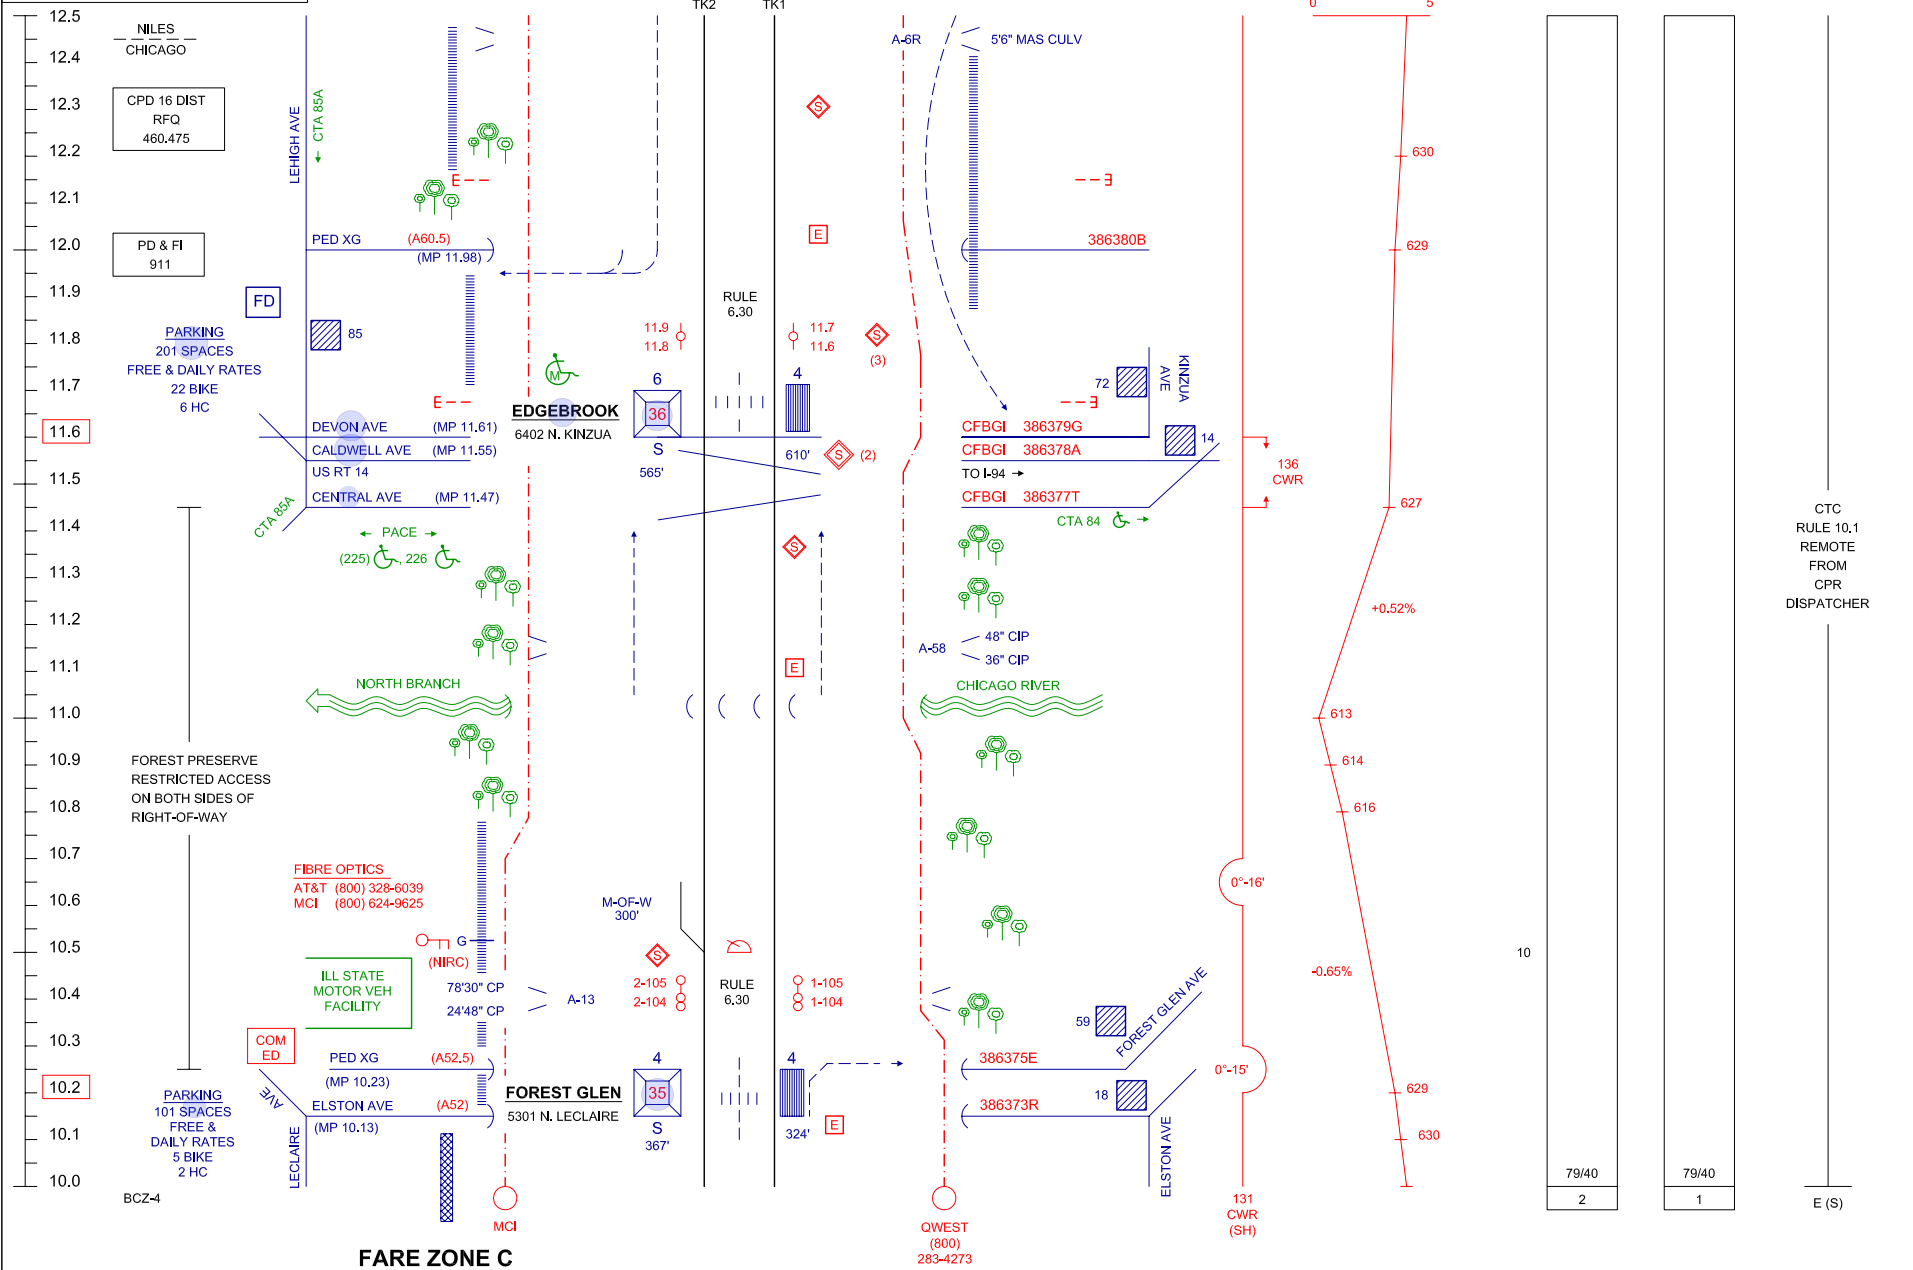


REV 7-22-08

C	S	L	W
5	8,10	15,19	41,45


2919 MILWAUKEE DISTRICT / (CPR) C&M SUBDIVISION

P-20

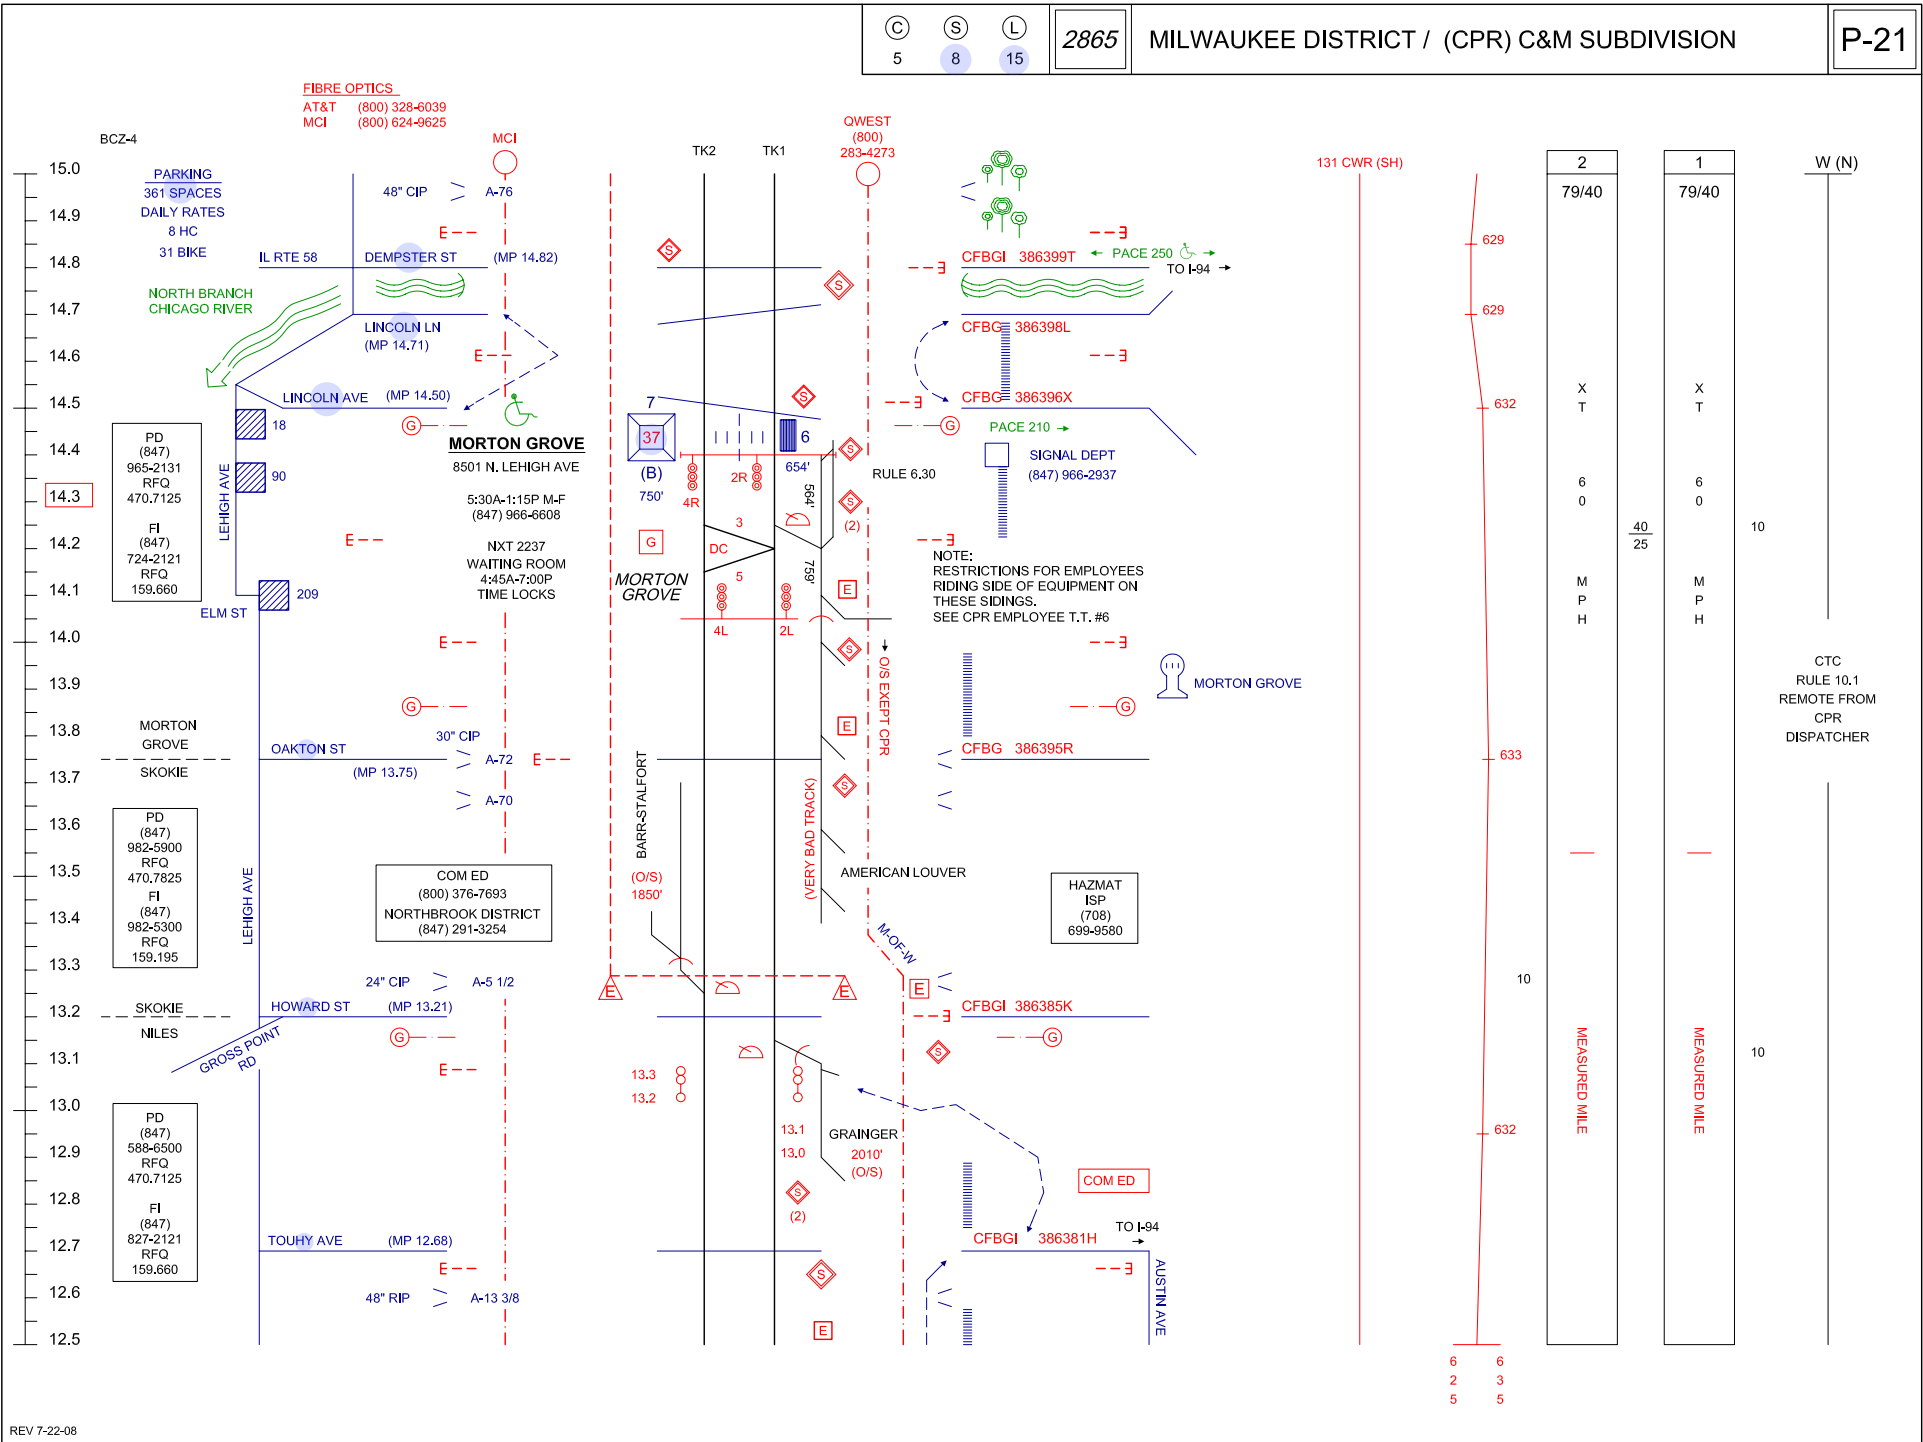

NOTE: SHERMER INTERLOCKING CONTROLLED BY CPR
DISPATCHER, MINNEAPOLIS.


BCZ-4

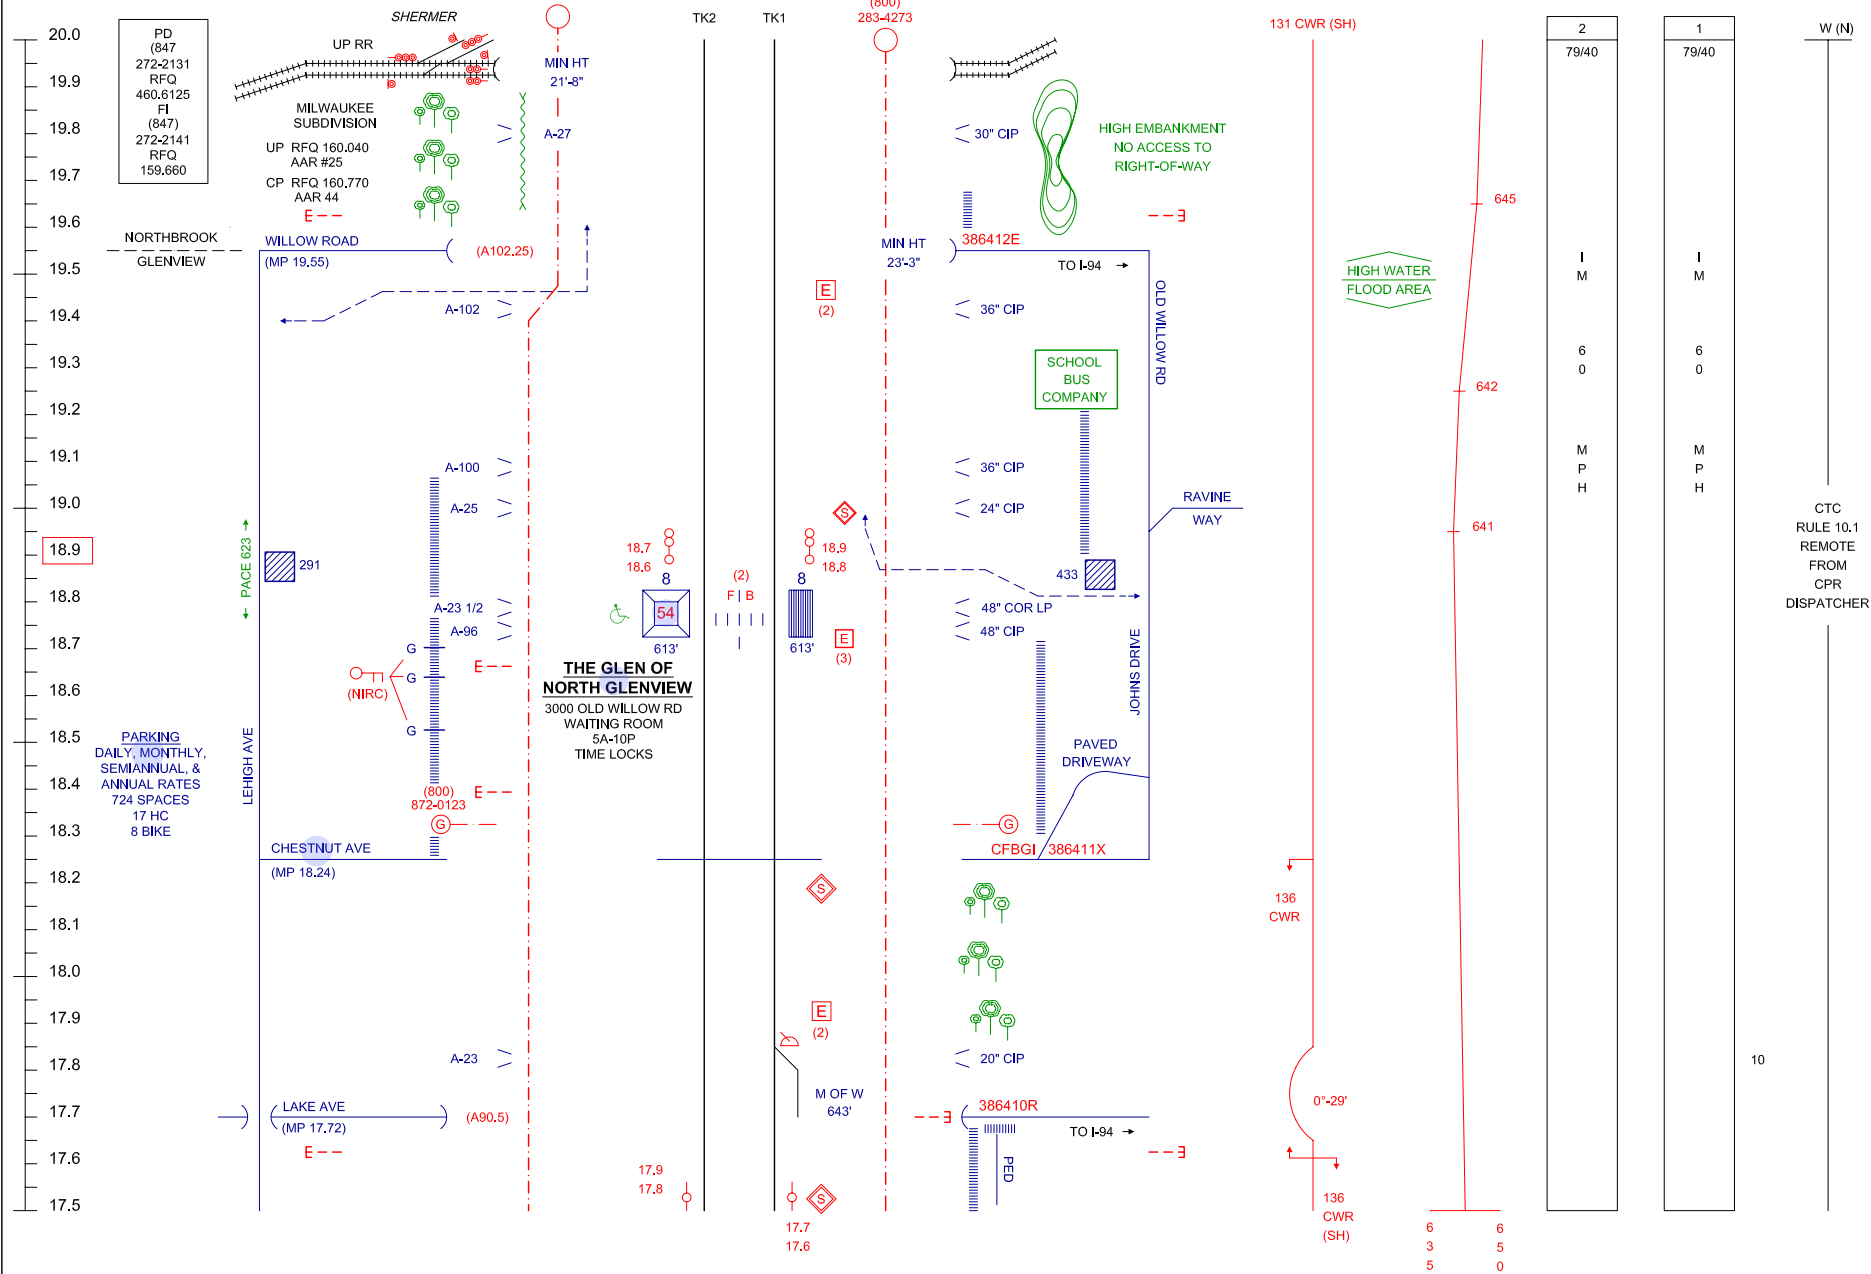

RFQ 160.770 AAR 44




(C) 10
(S) 29
(L) 58
2757
MILWAUKEE DISTRICT / (CPR) C&M SUBDIVISION
P-24

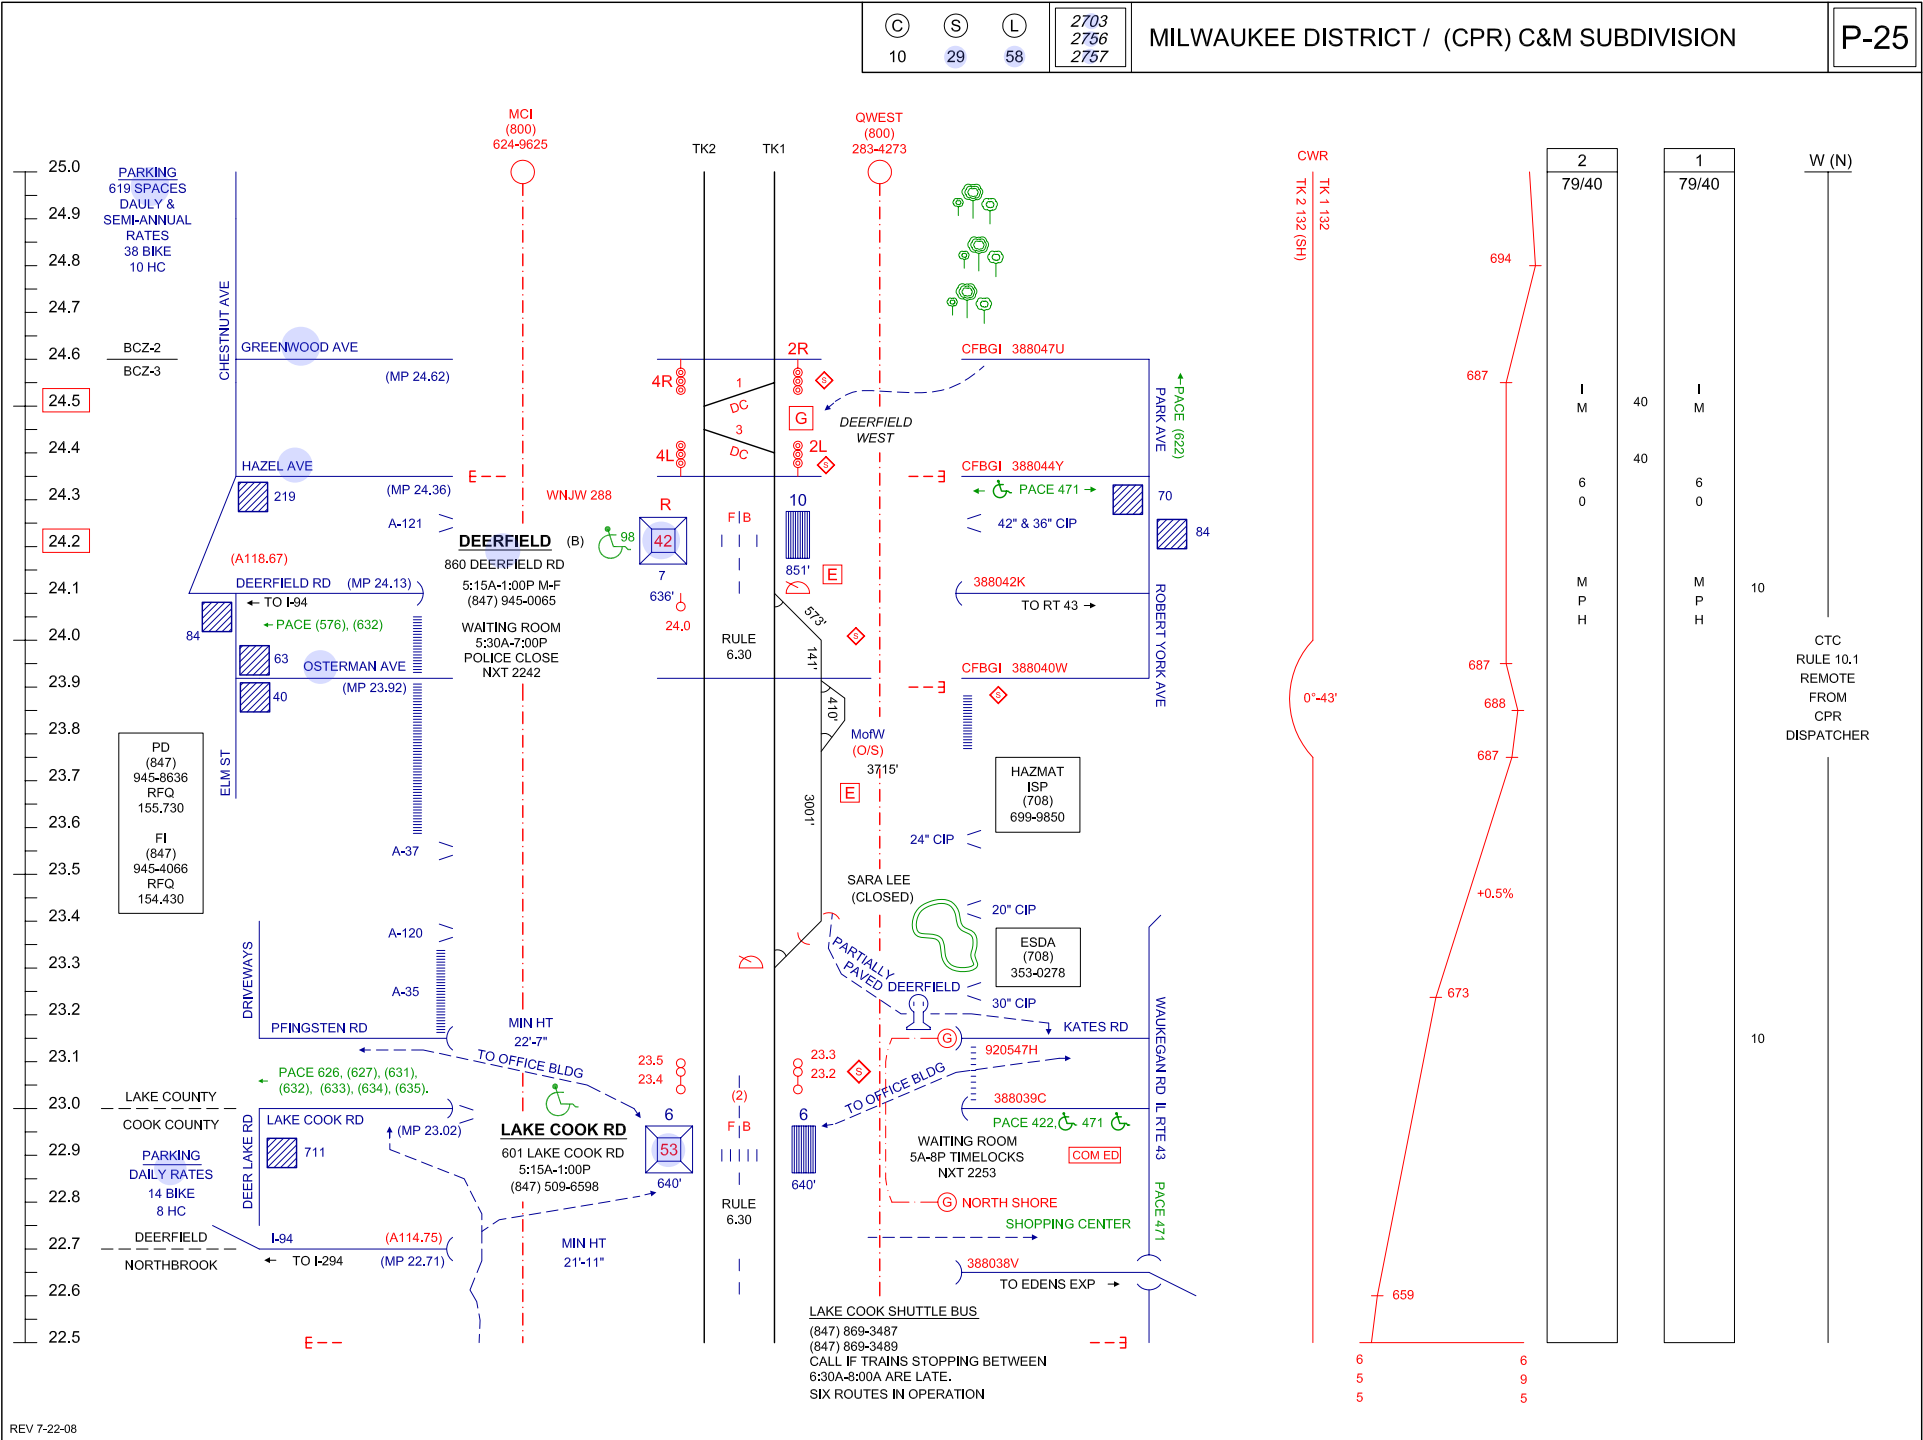

REV 7-22-08

CONTROL POINT PHONE NUMBERS
 CUS YARDMASTER (312) 322-8946-47-48
 CPR DISPATCHER (612) 904-5830
 (877) 588-9129

RFQ 160,770 AAR 44

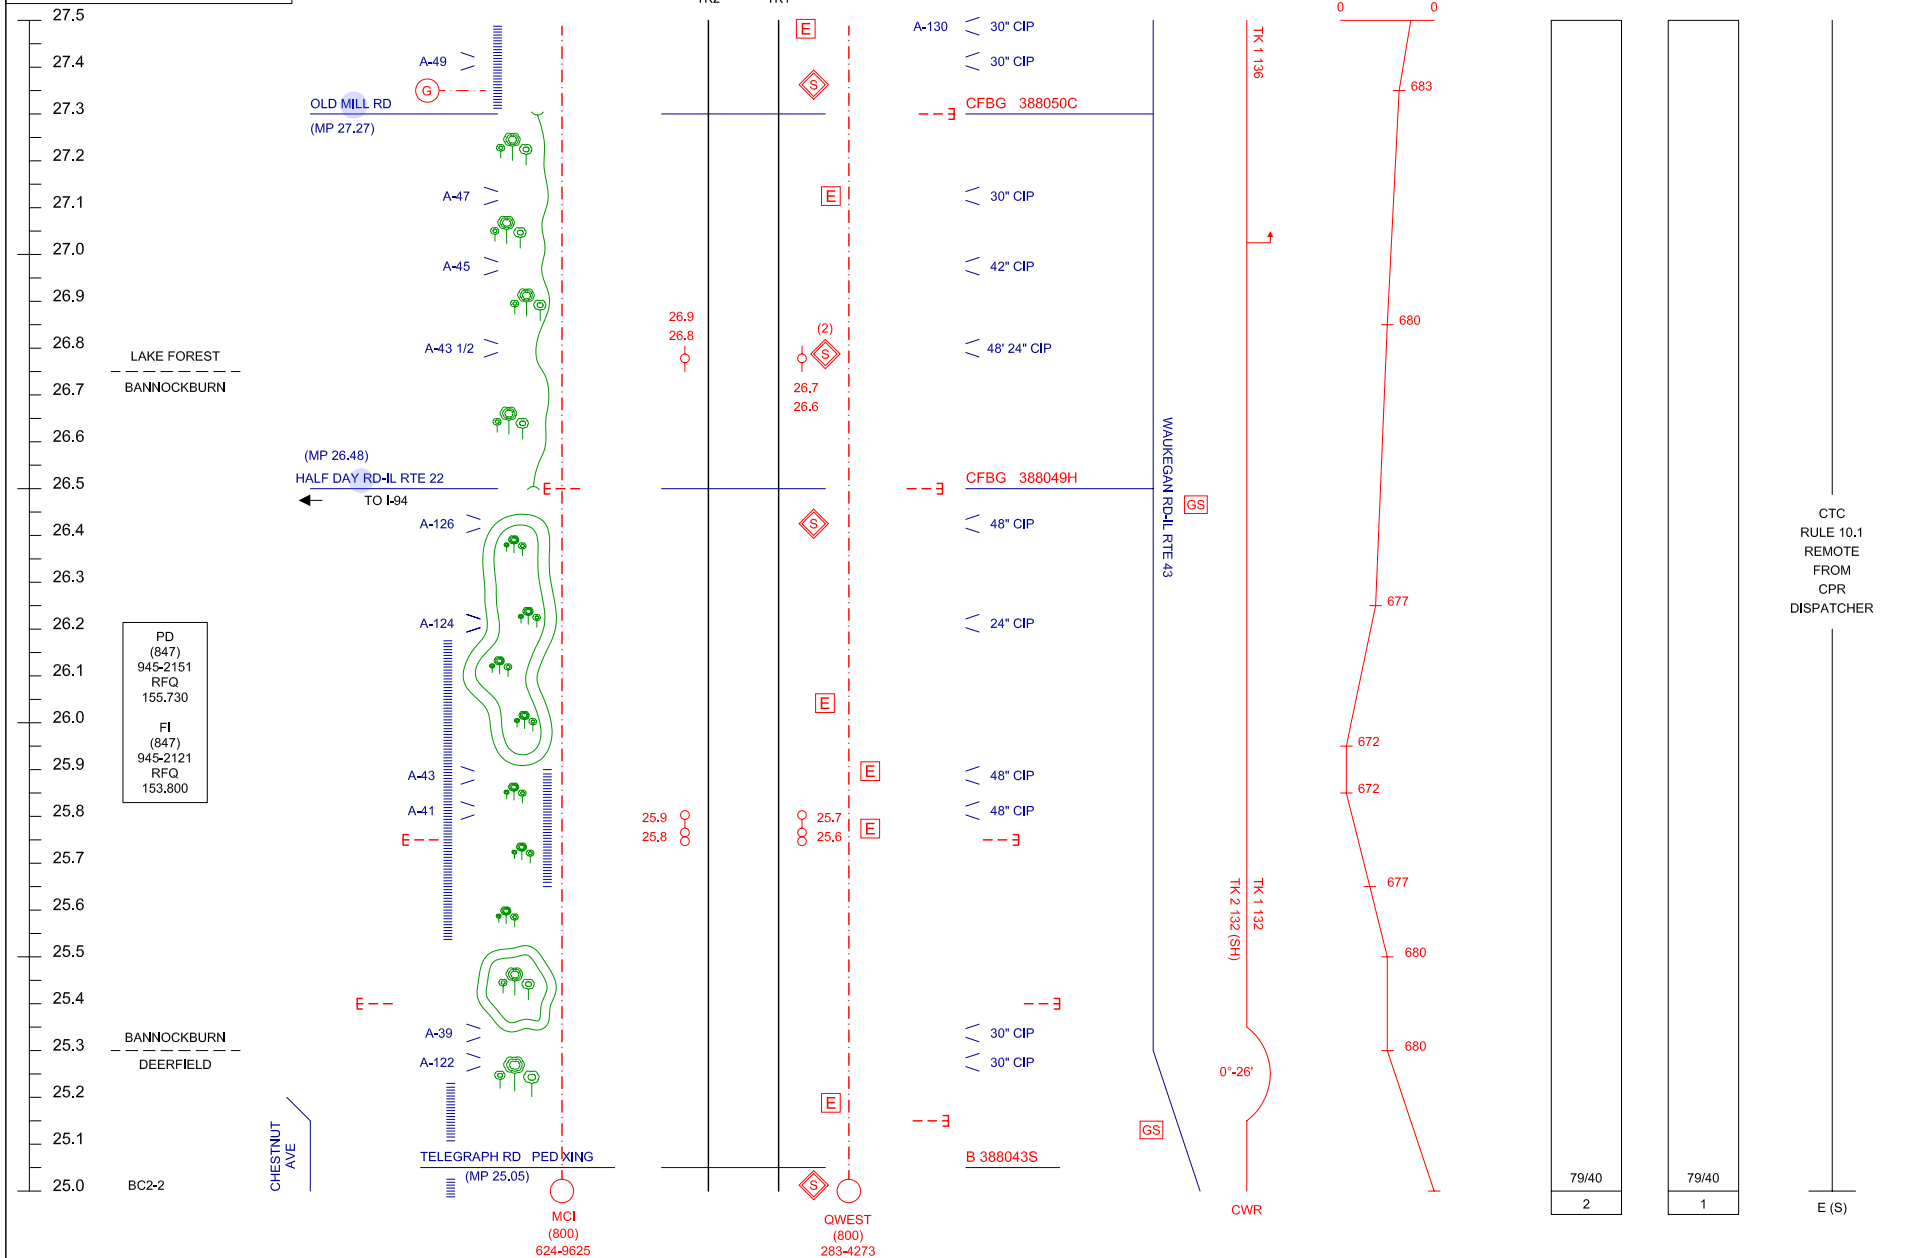


FARE ZONE F

REV 7-22-08

C 10 S 30,29 L 58 2703

MILWAUKEE DISTRICT / (CPR) C&M SUBDIVISION


P-26

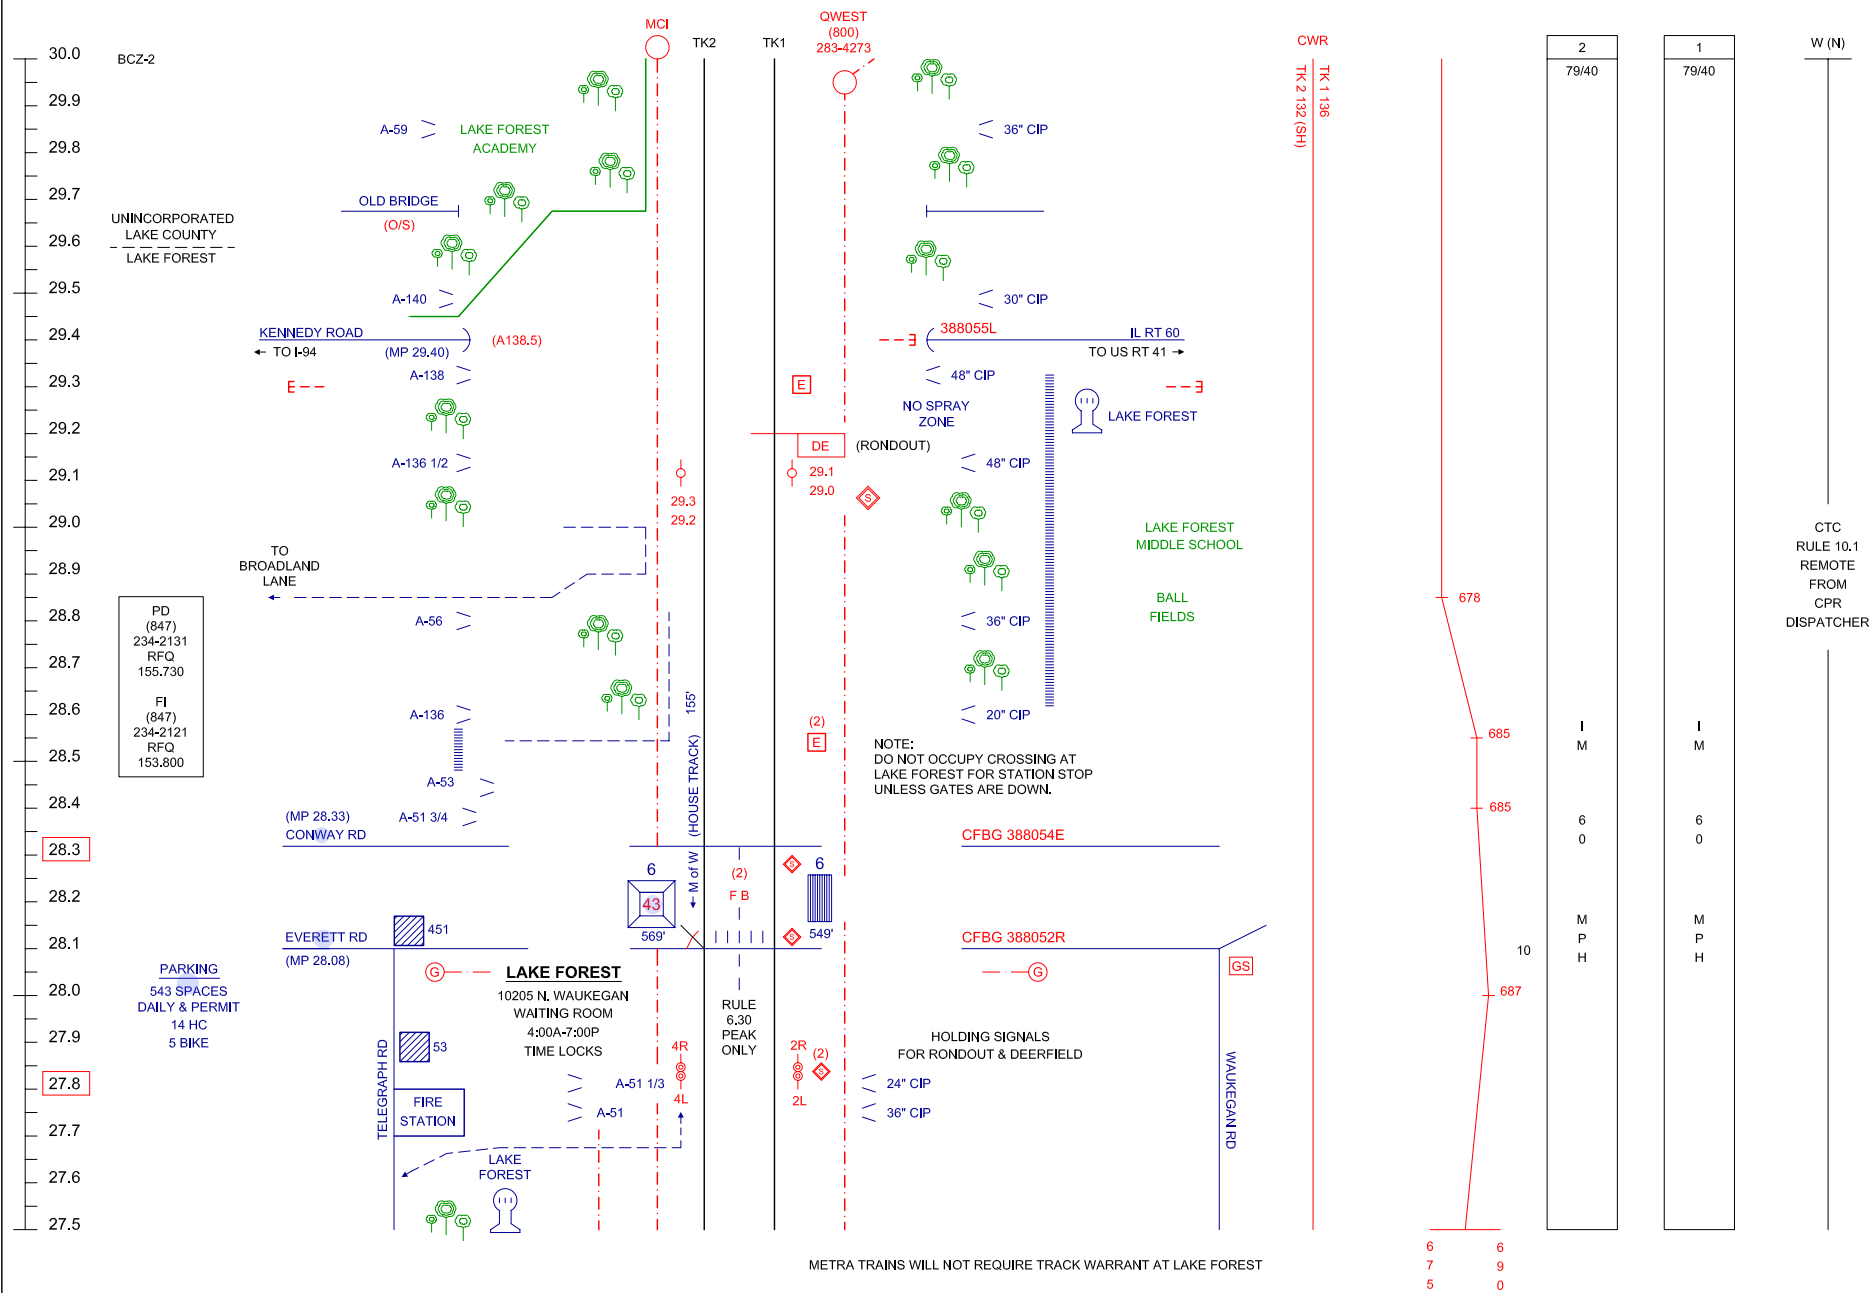

EASTWARD TRAINS ON NO 2 MT THAT HAVE STOPPED OR ARE MOVING AT A SPEED OF 10 MH OR LESS APPROACHING EASTWARD ABSOLUTE SIGNAL RONDOUT, MUST APPROACH ROCKLAND ROAD CROSSING PREPARED TO STOP UNTIL IT IS ASCERTAINED THAT AUTOMATIC CROSSING WARNING DEVICES ARE OPERATING. (2005-11-30)

CPR DIST
FAX
(612) 904-5882

RFQ 160.770 AAR 44


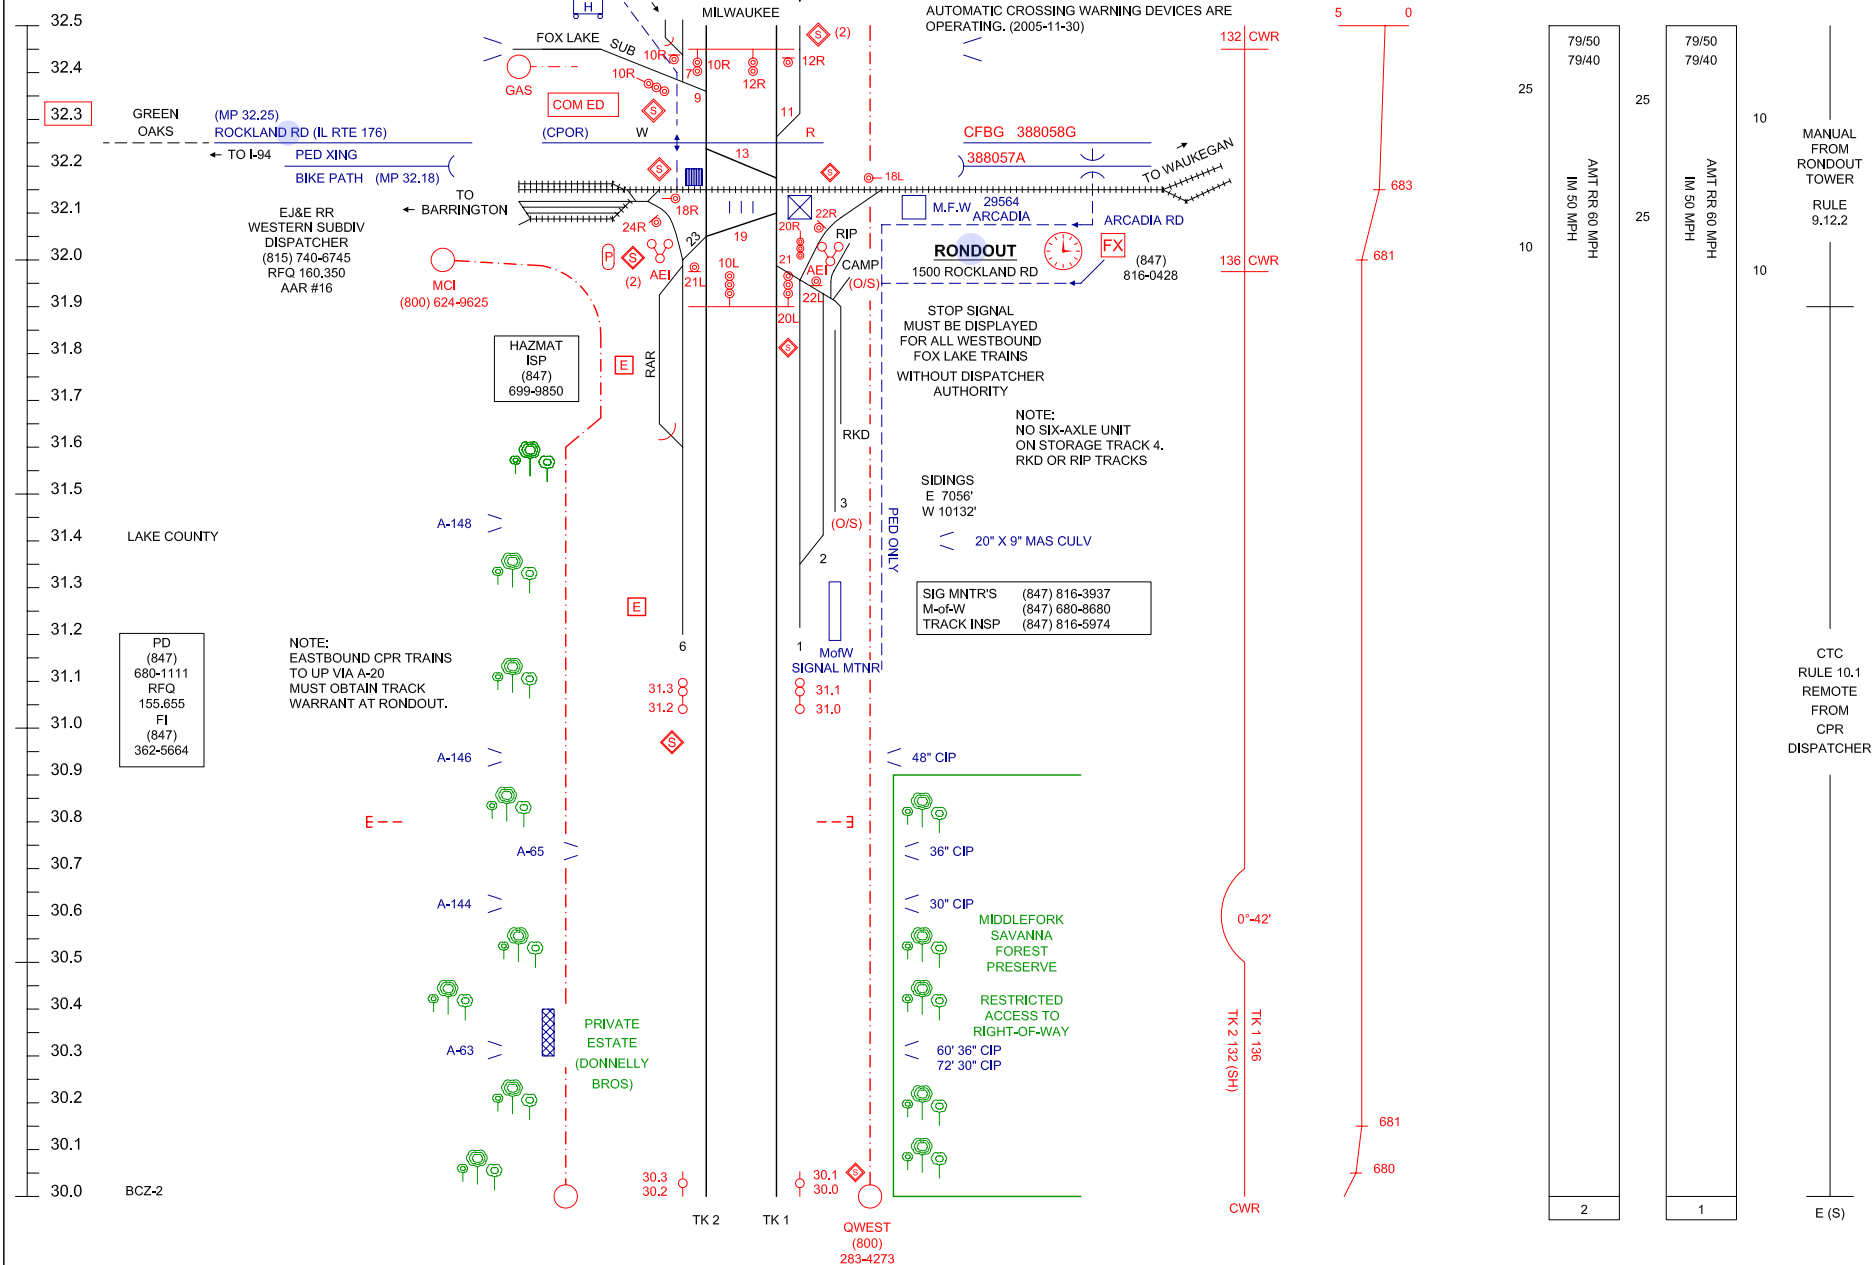


(C)	(S)	(L)	2592
10	30	59	

MILWAUKEE DISTRICT / (CPR) C&M SUBDIVISION

P-28

A vertical number line is shown, ranging from 35.0 to 37.5. Major tick marks are labeled every 0.1 units: 35.0, 35.1, 35.2, 35.3, 35.4, 35.5, 35.6, 35.7, 35.8, 35.9, 36.0, 36.1, 36.2, 36.3, 36.4, 36.5, 36.6, 36.7, 36.8, 36.9, 37.0, 37.1, 37.2, 37.3, 37.4, and 37.5. The tick mark for 35.5 is highlighted with a red rectangular box.

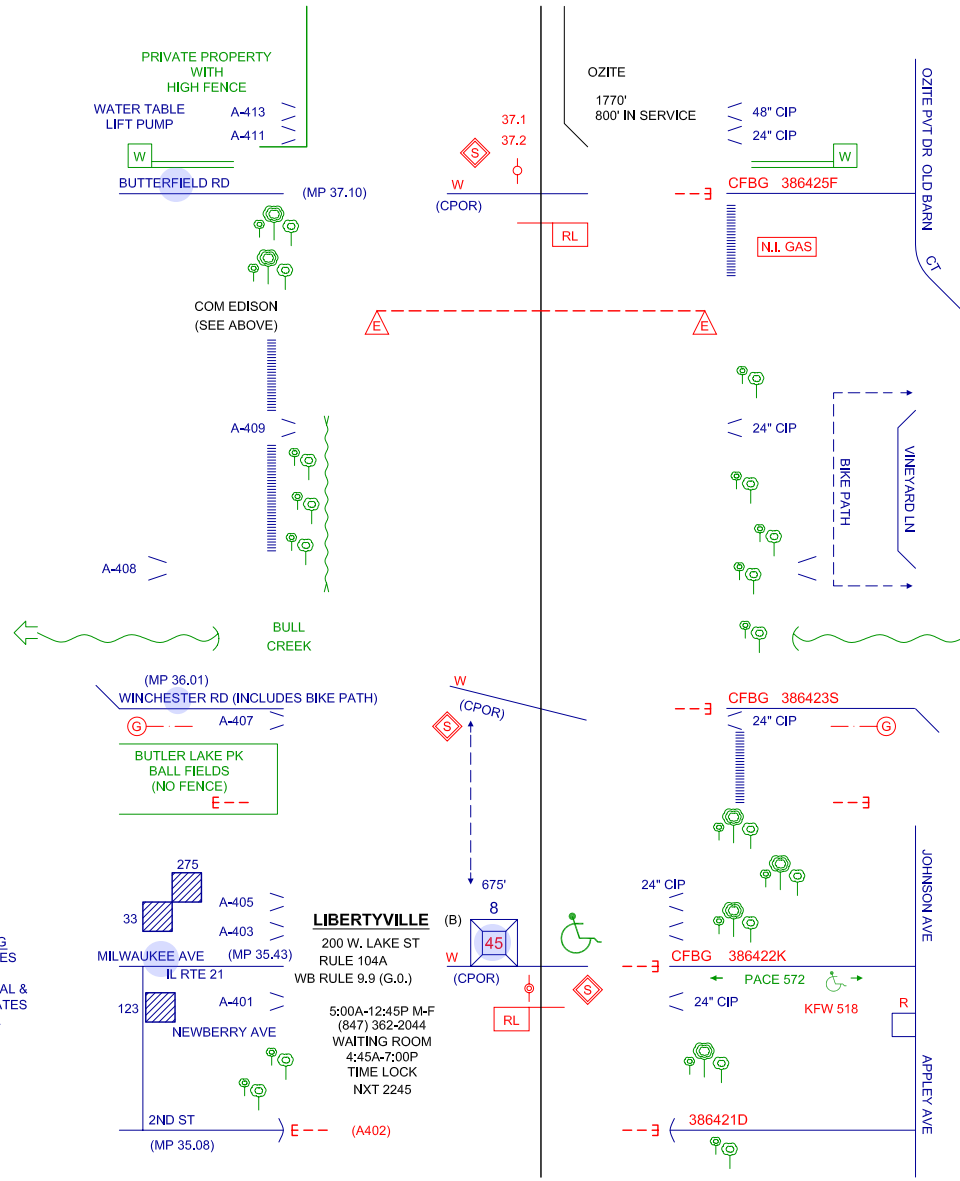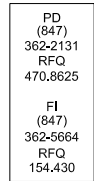


ABS
MOVEMENT
AUTHORITY
REQUIRED
PRIOR TO
MAIN TRACK
OCCUPANCY

60/35
45/30


45/30


E

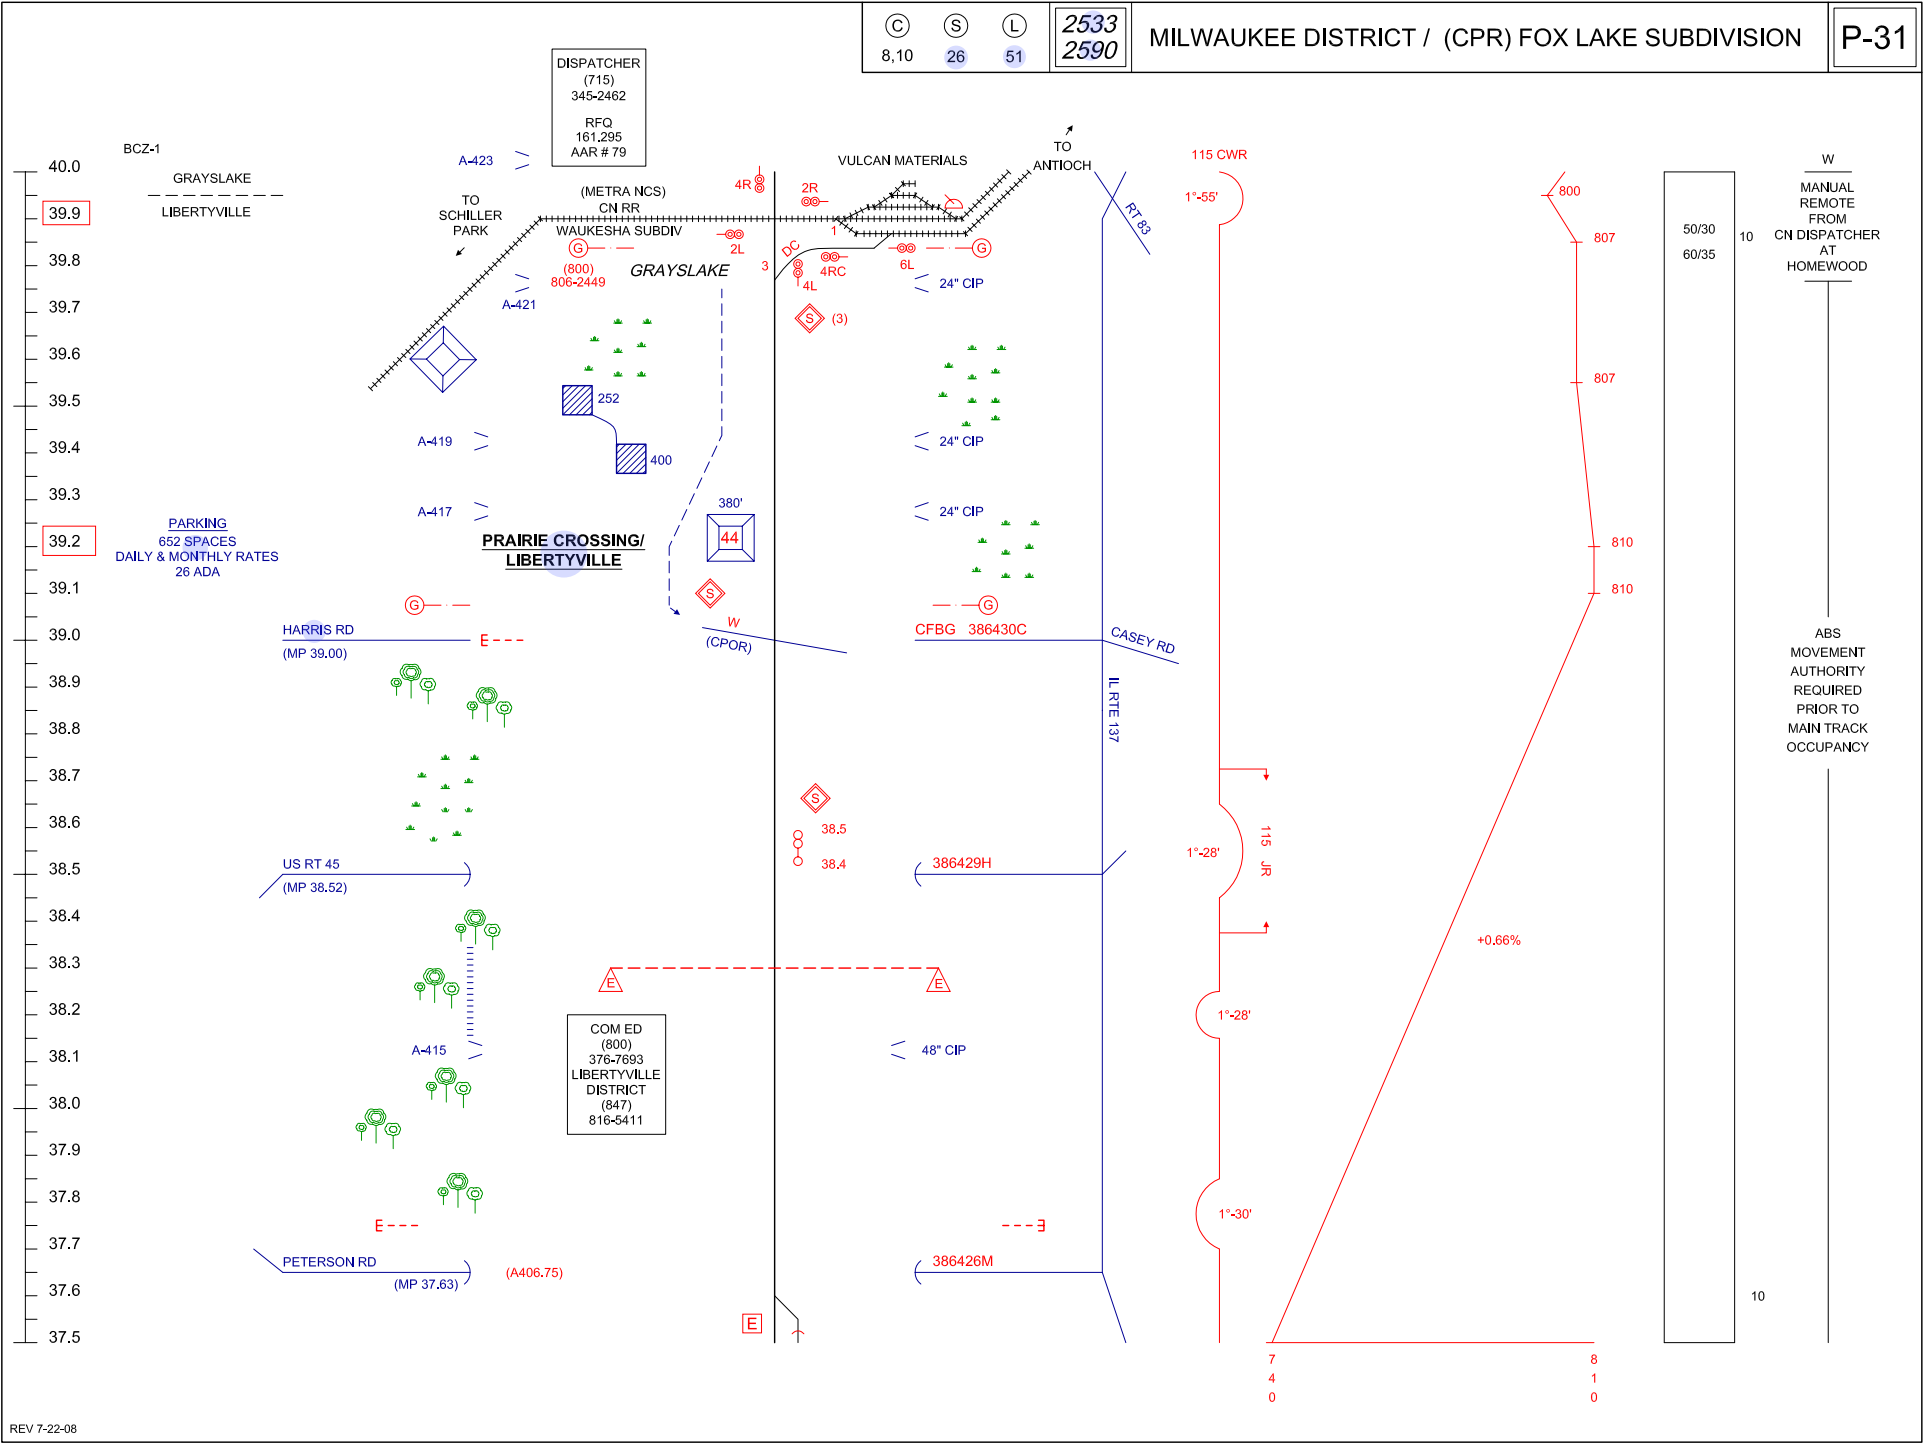


CONTROL POINT PHONE NUMBERS
CPR DISPATCHER (312) 904-5830
(877) 588-9129

RFQ 160.770 AAR 44

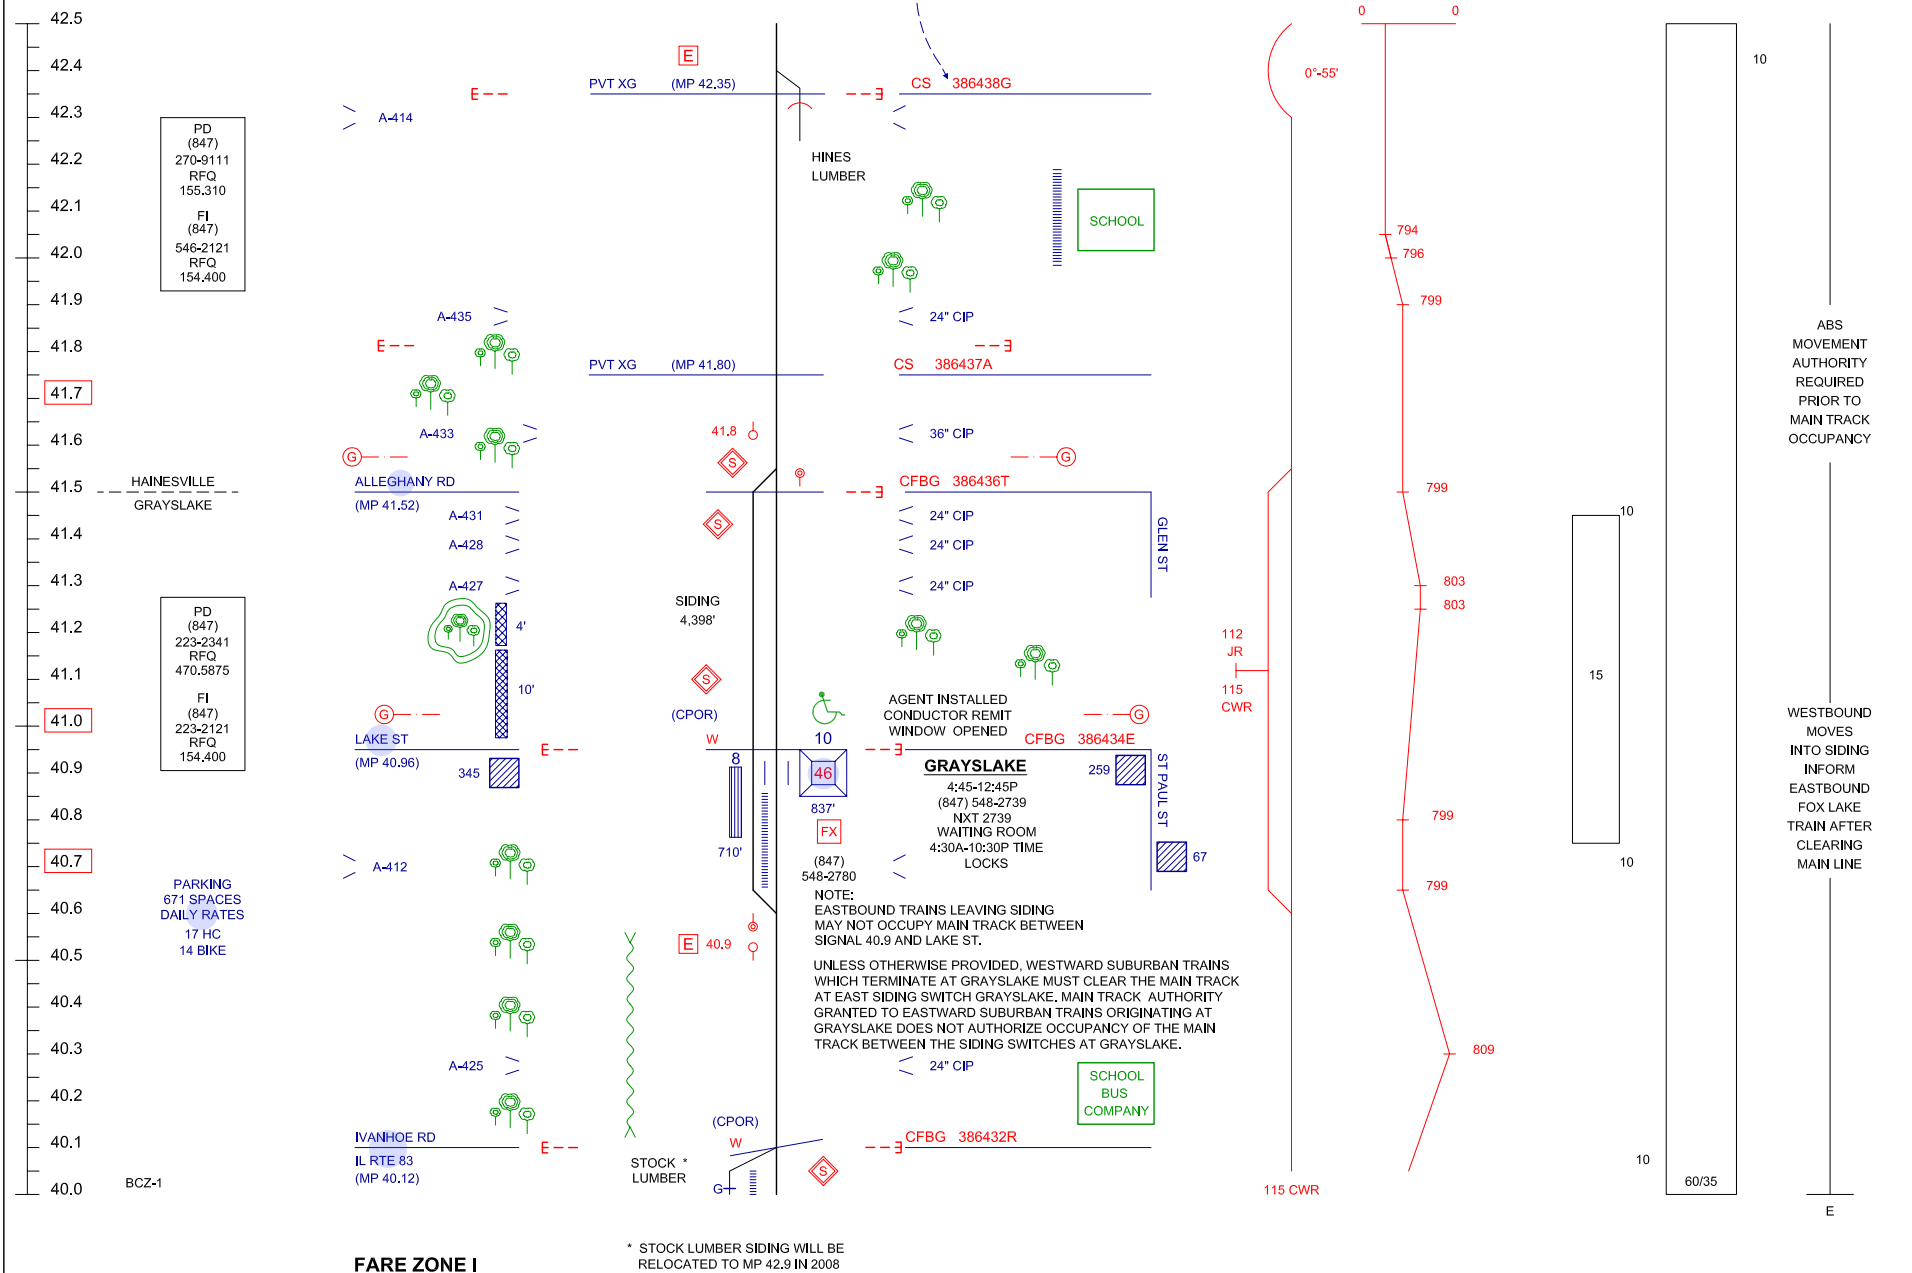

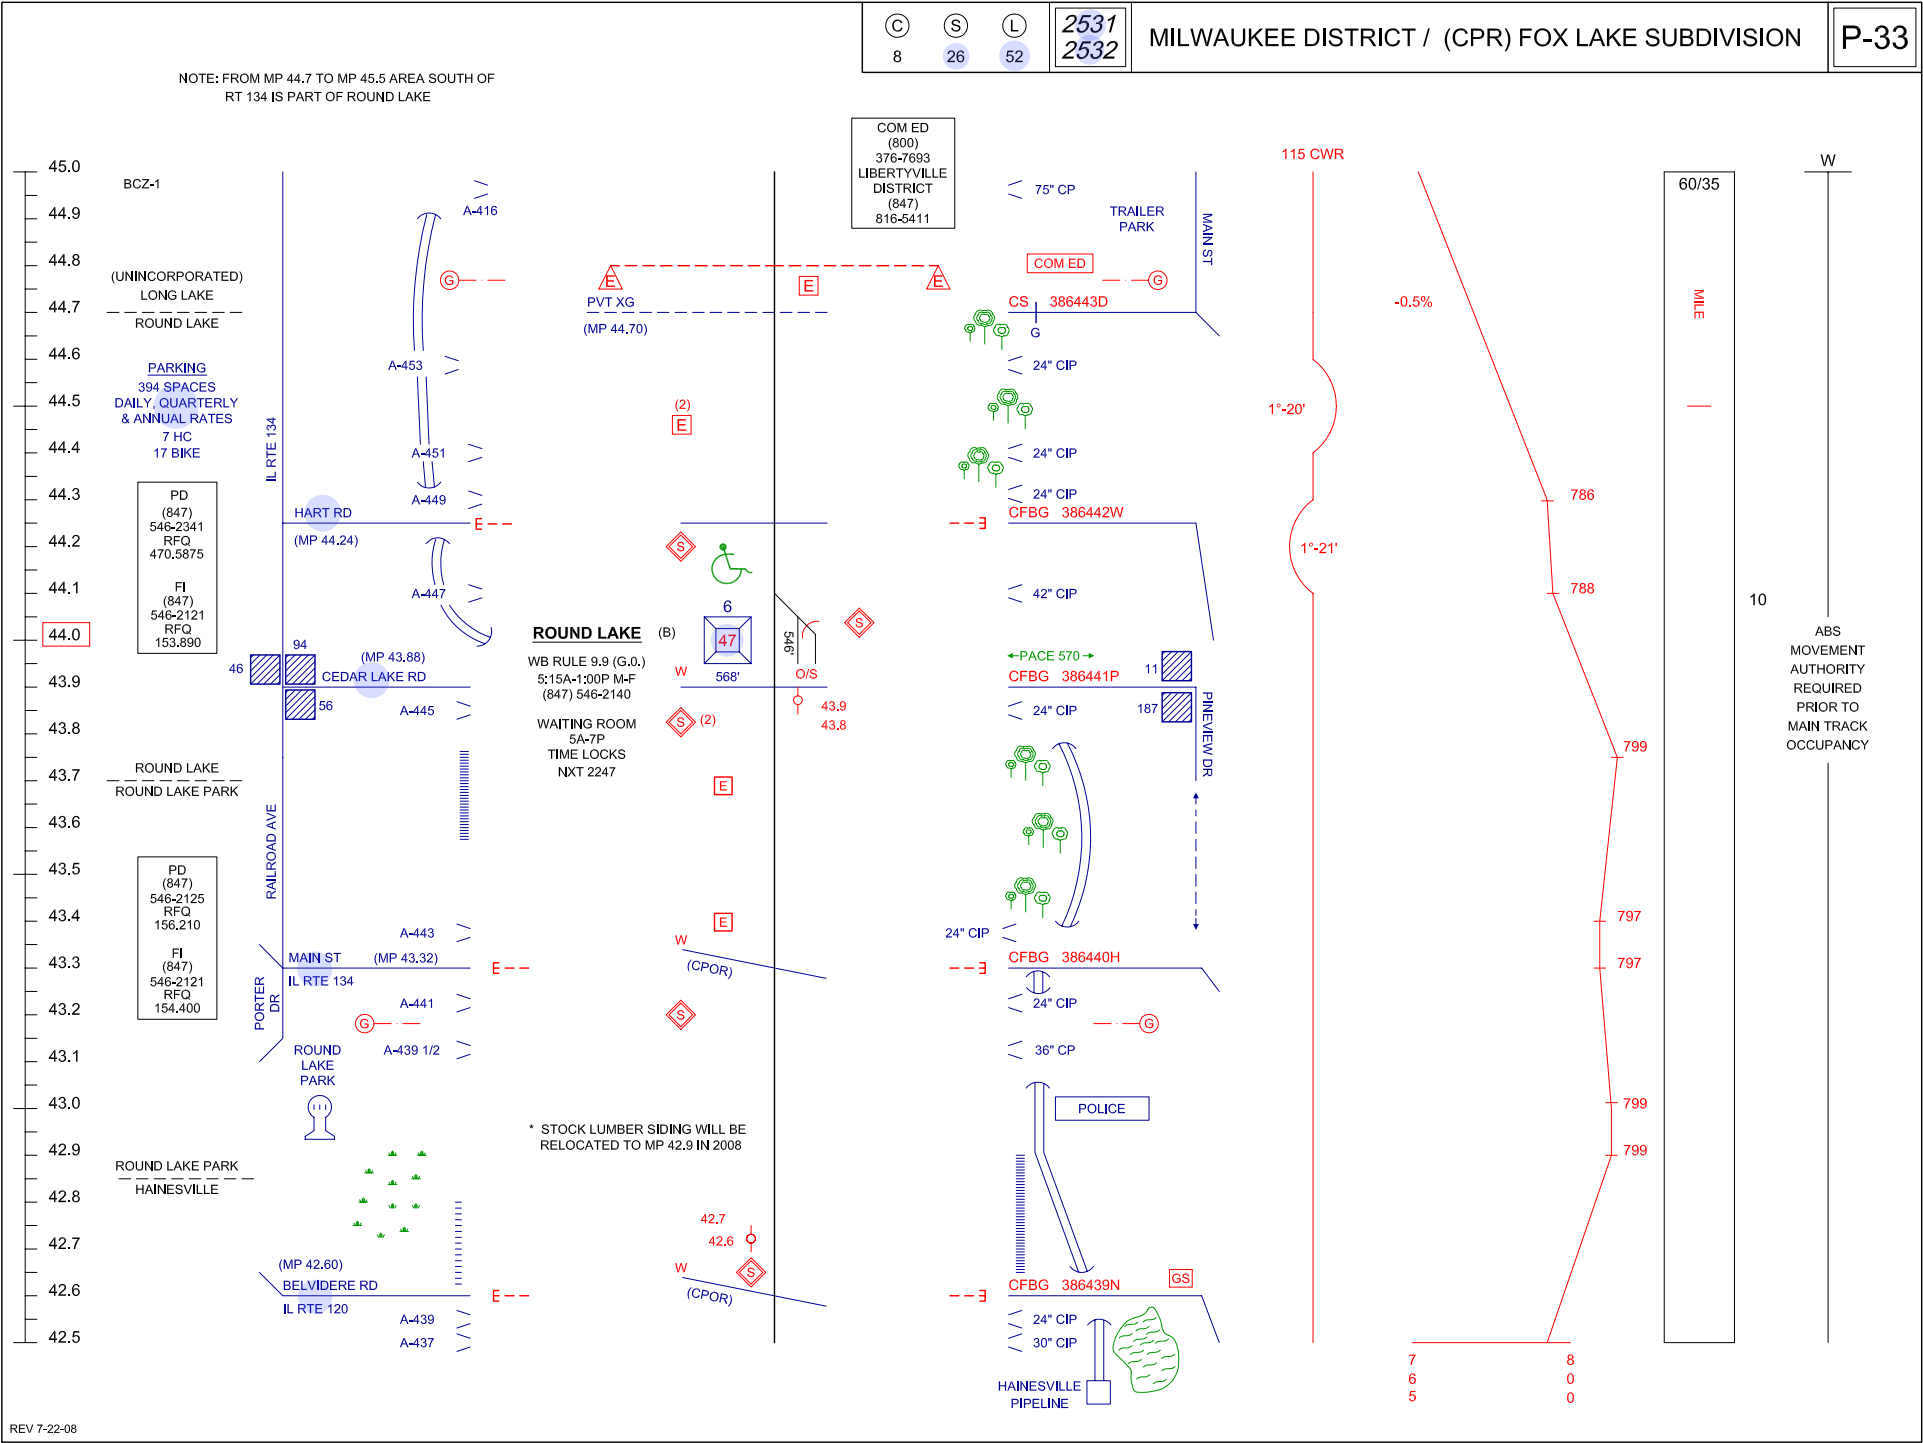

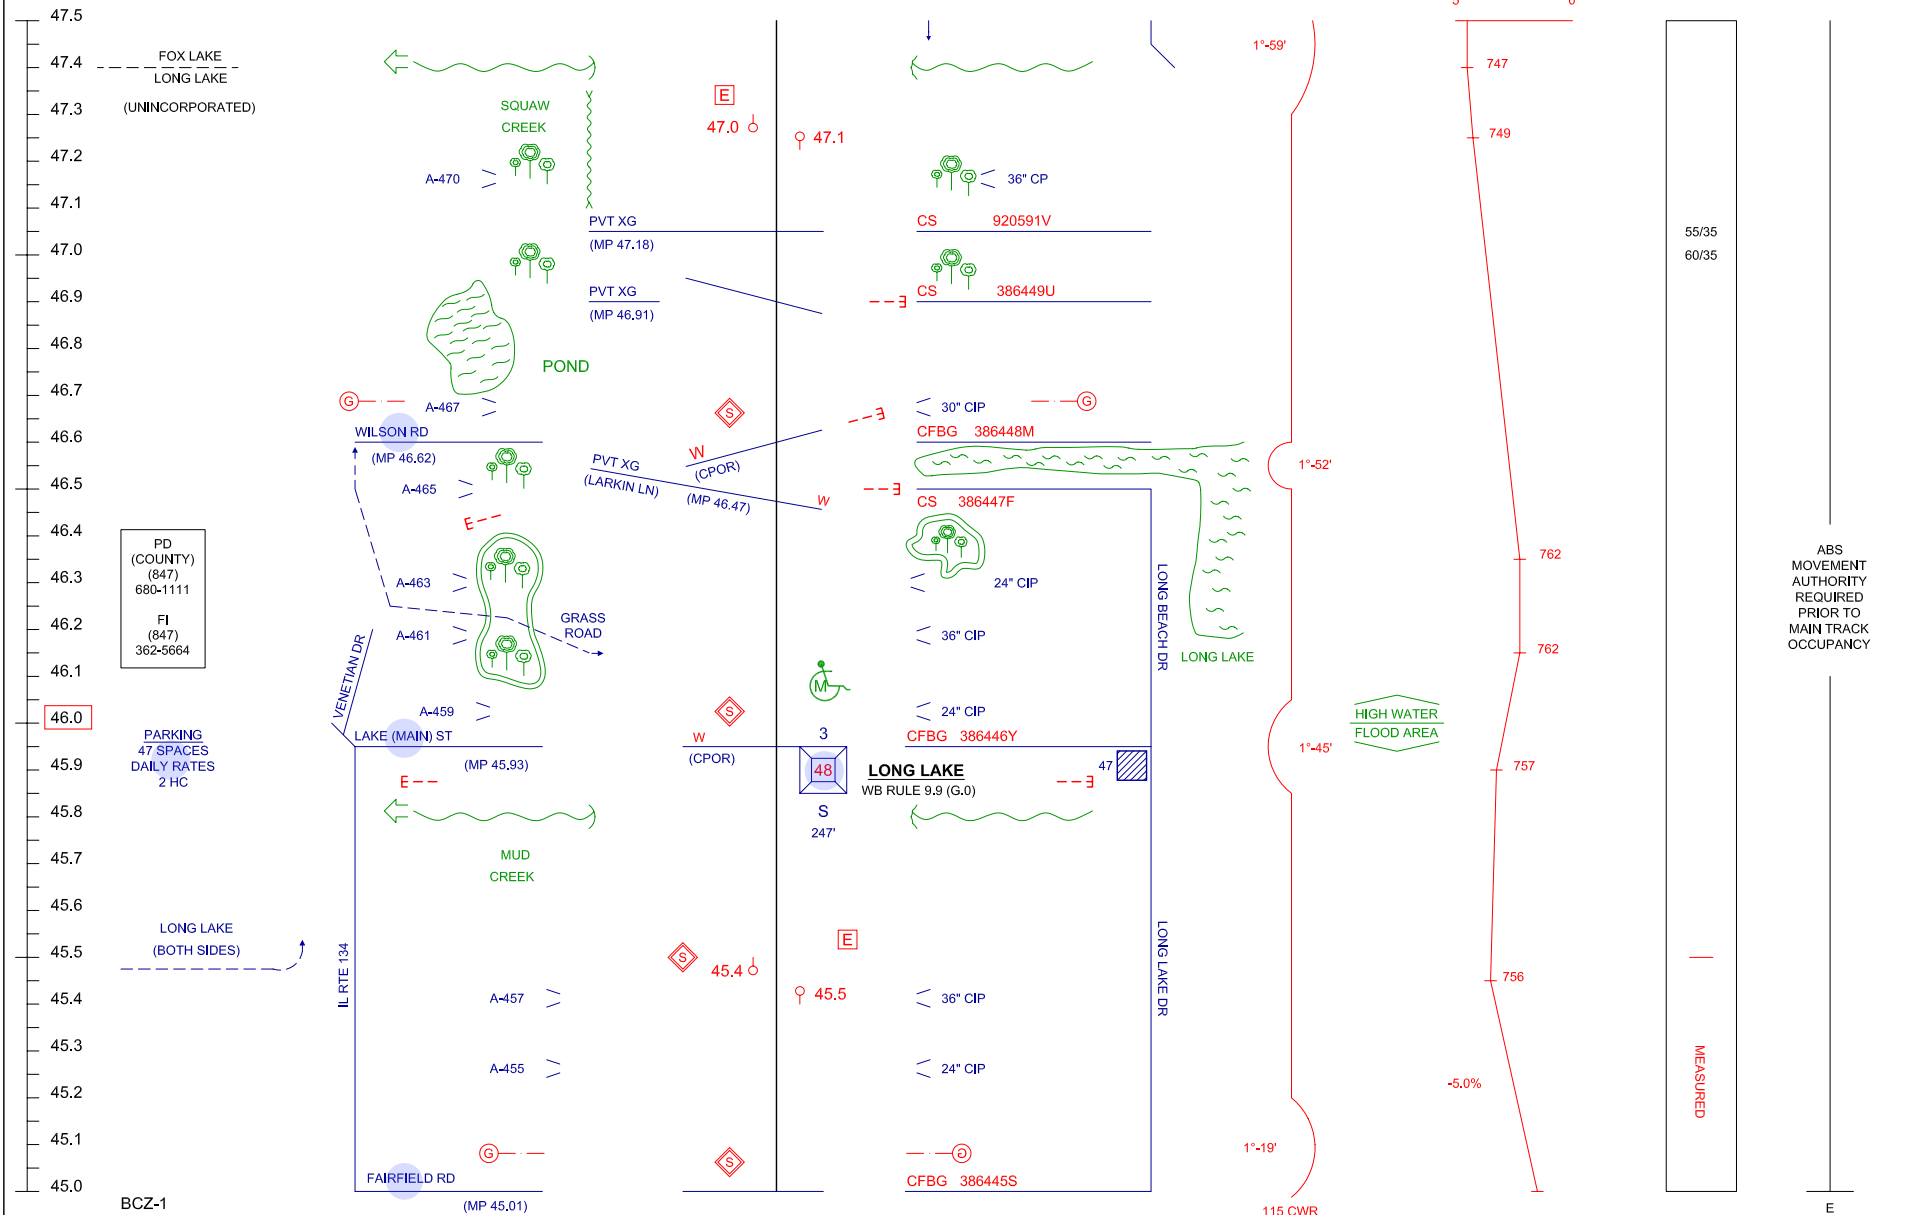


CONTROL POINT PHONE NUMBERS	
CPR DISPATCHER	(612) 904-6830
WSOR DISPATCHER	(262) 438-8837

(C)	(S)	(L)
8	26	52

2473

MILWAUKEE DISTRICT / (CPR) FOX SUBDIVISION


P-35

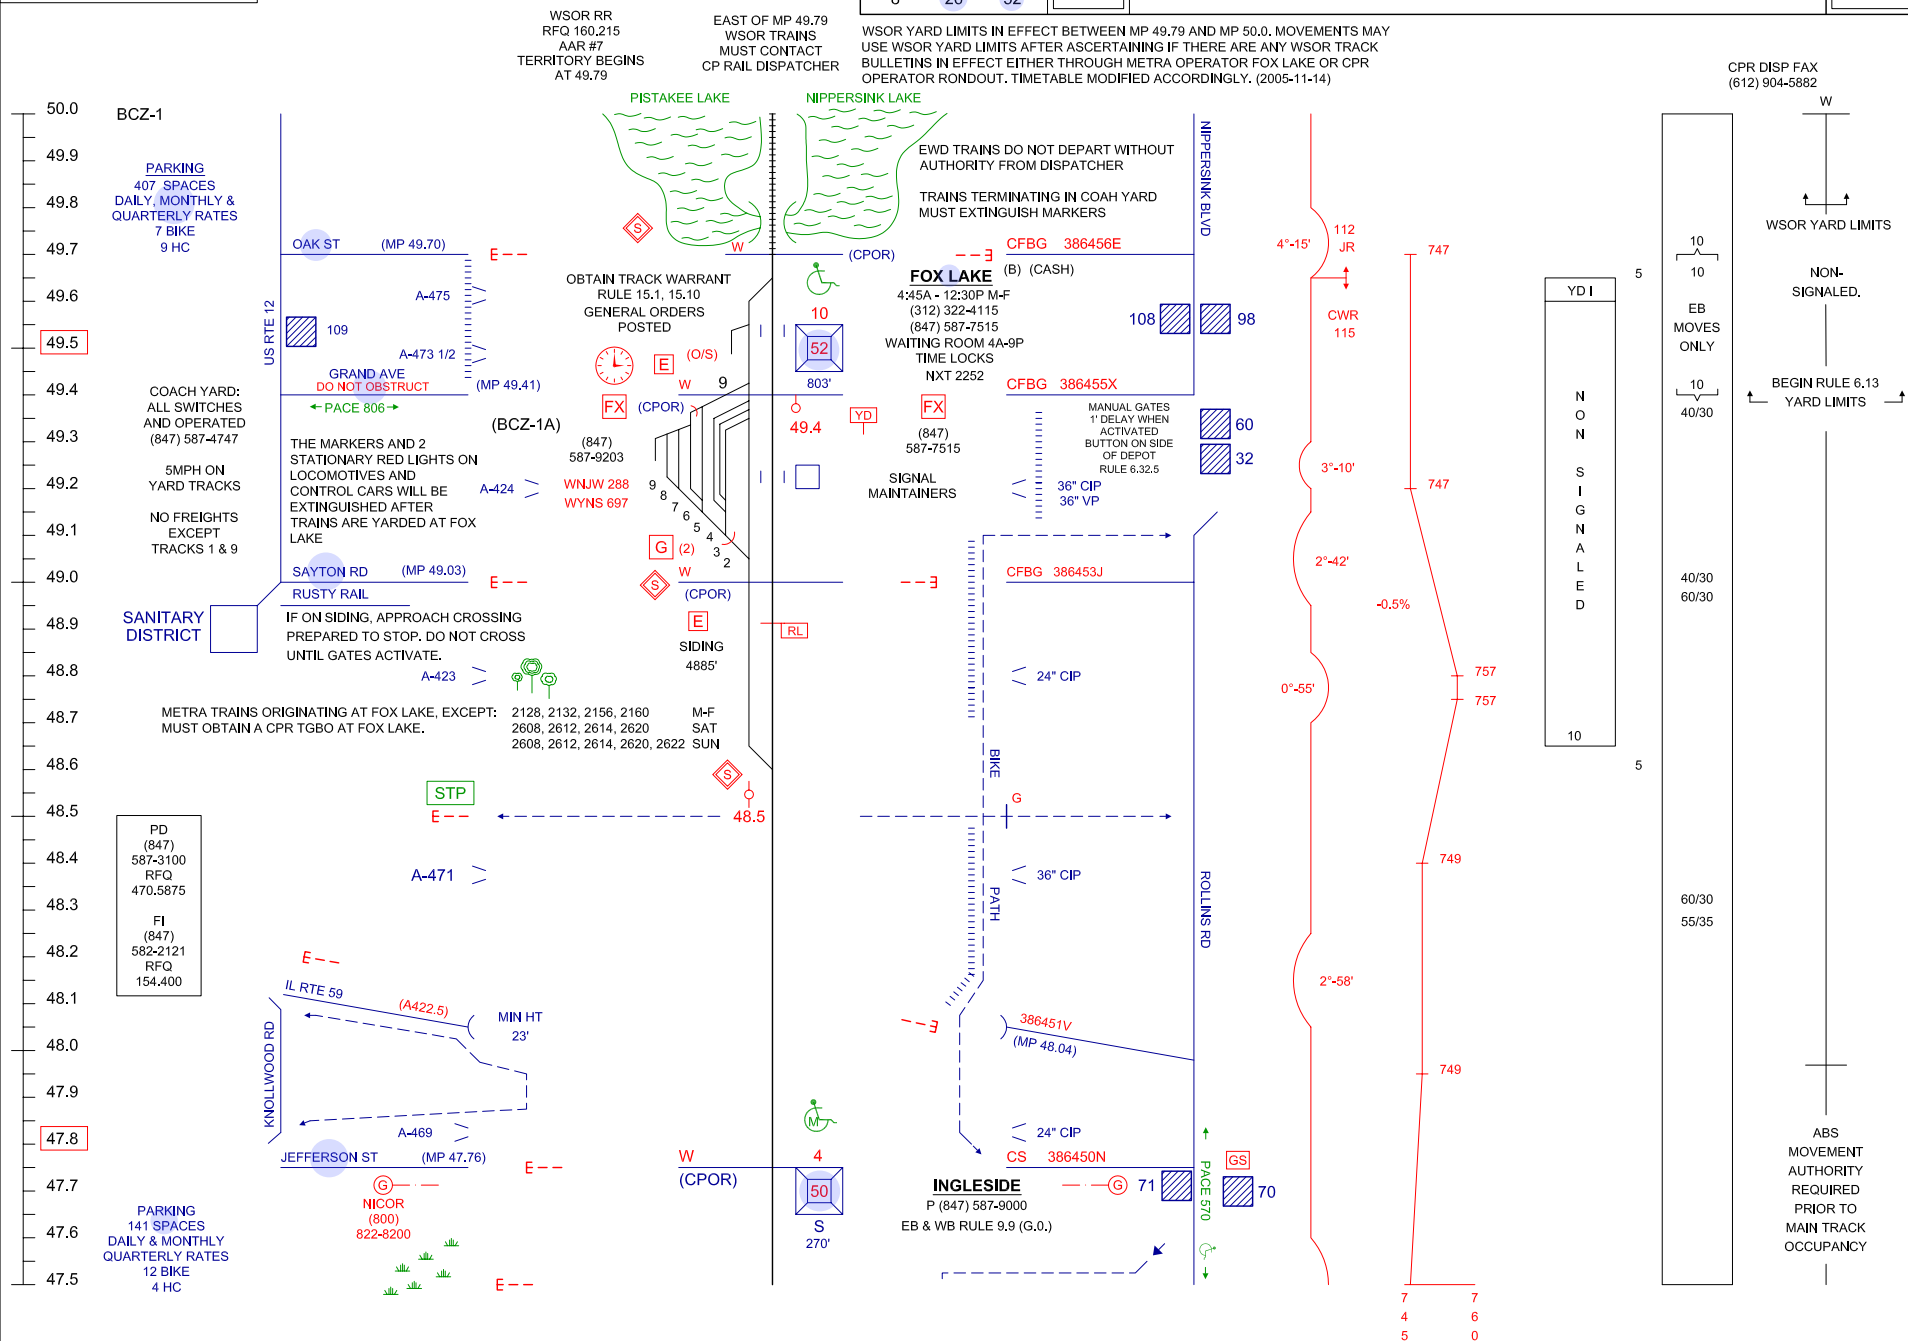

FARE ZONE B

10

E

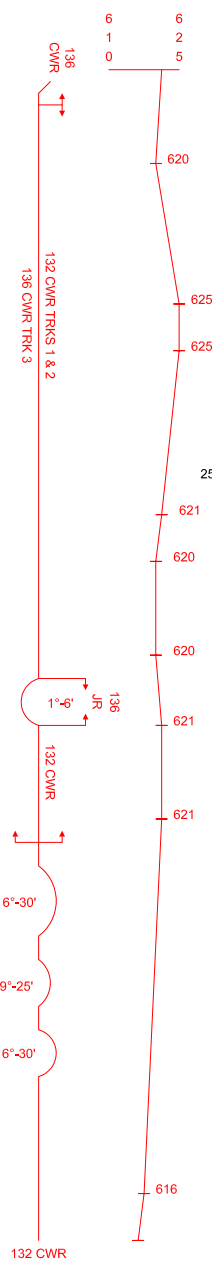


3	70/40 15	10 10	25 25
2	70/40 15	10 10	25 25
1	70/40 15	10 10 10	25 25

P-36

CONTROL POINT PHONE NUMBERS
 CUS YARDMASTER (312) 322-8946-47-48
 CPR DISPATCHER (612) 904-5834
 (800) 874-7635
 SWS/B-12 DISPATCHER (312) 322-2846

RFQ 161.520 AAR 94

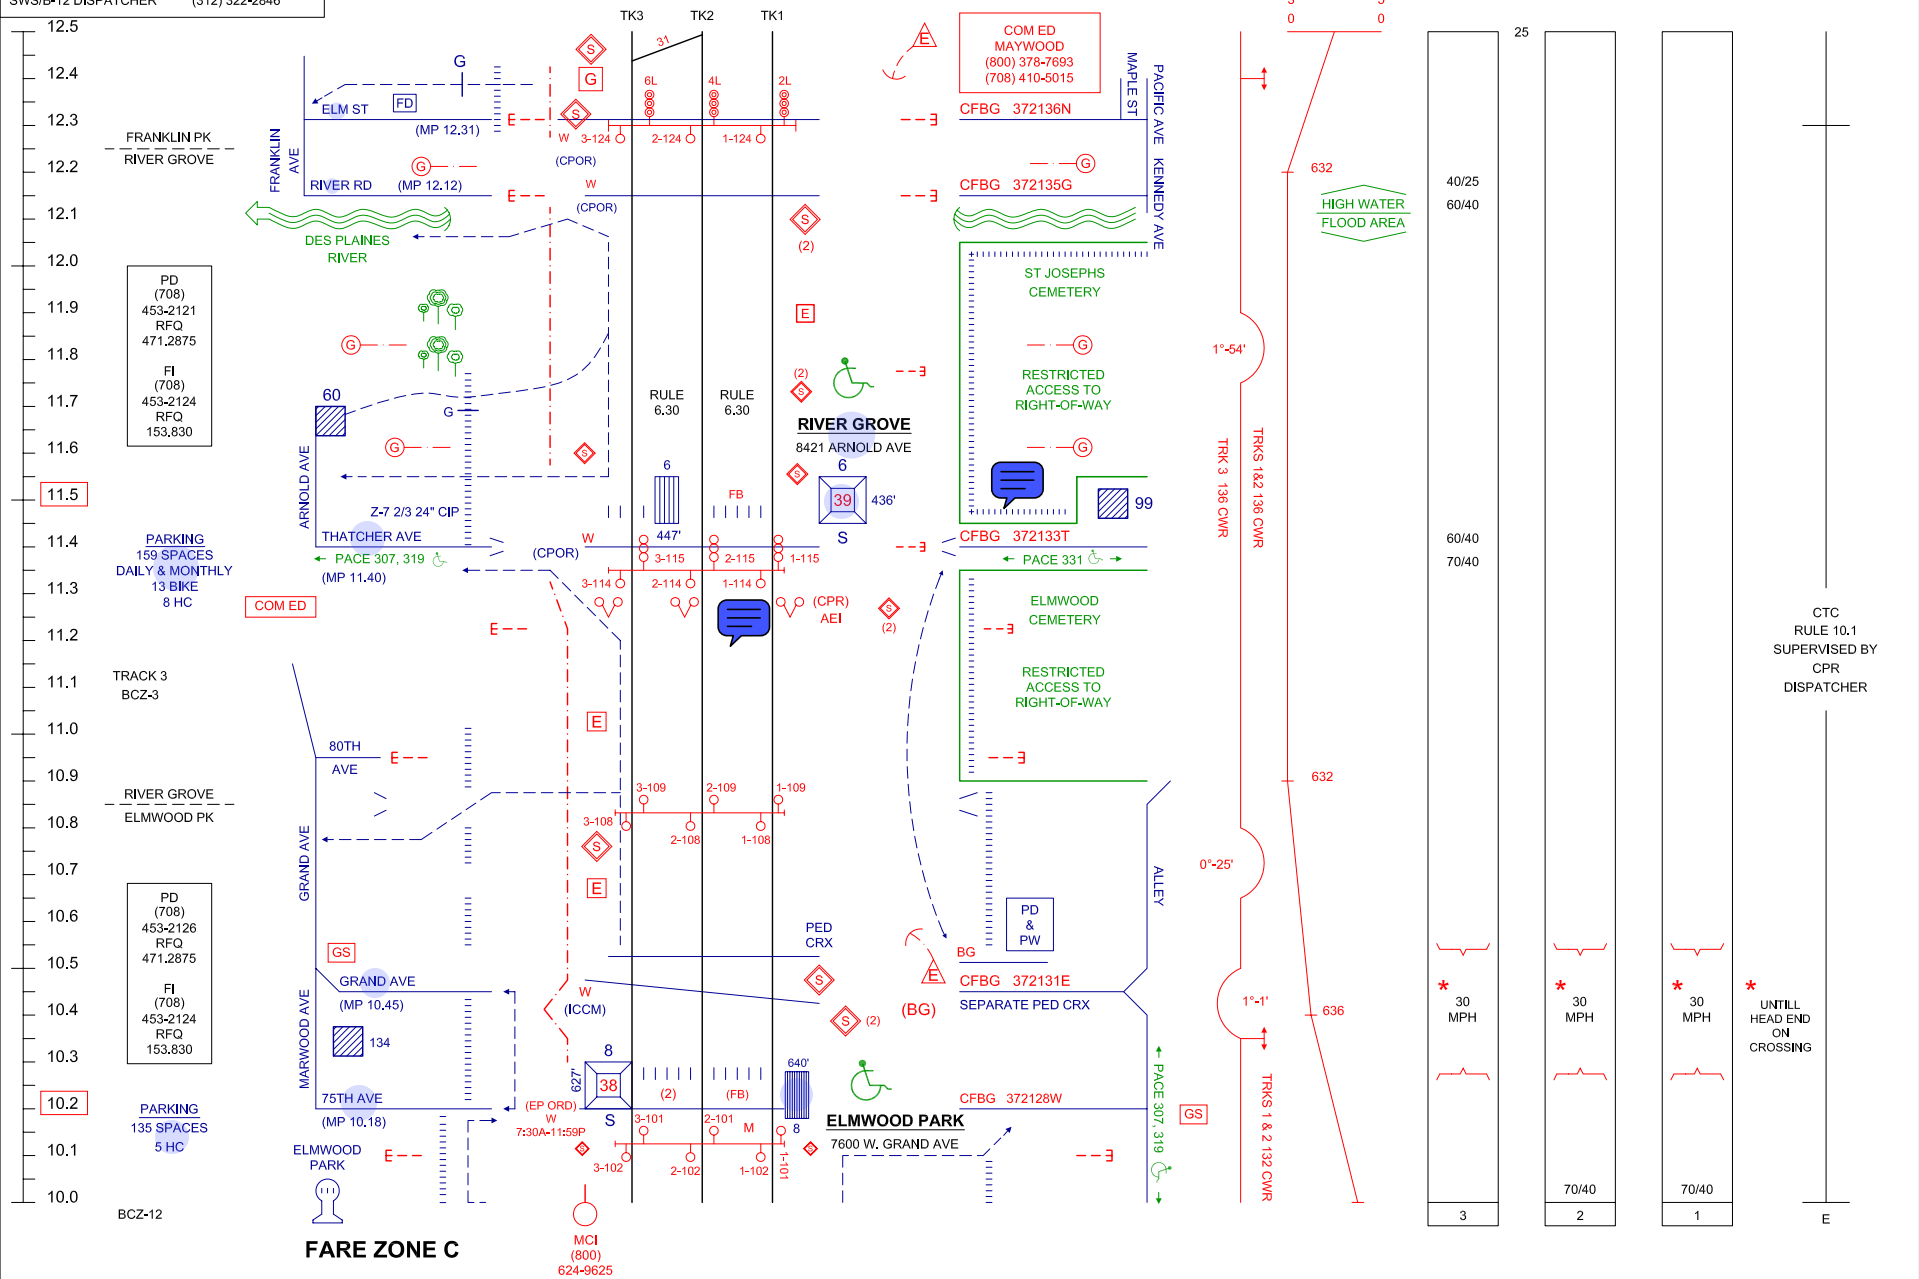

REV 7-22-08

C 5
 S 39
 L 77
 2973
 2974

MILWAUKEE DISTRICT / (CPR) ELGIN SUBDIVISION

P-38

* TRAIN OR ENGINE MOVEMENTS ON 3 LEAD APPROACHING FRANKLIN PARK STATION WILL MONITOR RADIO # 94 UNTIL STATION IS PASSED.




SIGNAL ASPECT 9.1.9 RED OVER RED OVER YELLOW AND ASPECT 9.1.10 RED OVER RED OVER GREEN WILL BE FOR 25 MPH CROSSOVERS EAST OF CN CROSSING ON THE CN MAIN TRACK. SIGNAL ASPECT 9.1.9 RED OVER RED OVER YELLOW OVER RED AND ASPECT 9.1.10 RED OVER GREEN OVER RED WILL BE FOR 40 MPH CROSSOVERS JUST WEST OF CN CROSSING.

THE SWITCHES AT THE JUNCTION WITH THE IHB ARE INTERLOCKED AND OPERATED FROM THE METRA CONTROL CENTER CHICAGO. WHEN SIGNAL DISPLAYS A STOP INDICATION FOR AN APPROACHING TRAIN OR ENGINE AND NO CONFLICTING MOVEMENT IS EVIDENT, A MEMBER OF THE CREW MUST COMMUNICATE WITH METRA CONTROL OPERATOR AND BE GOVERNED BY INSTRUCTIONS RECEIVED.

METRA TRAINS WILL NOT REQUIRE TRACK WARRANT AT FRANKLIN PARK

WHEN EASTWARD ABSOLUTE SIGNAL AT TOWER B-12 GOVERNING EASTWARD MOVEMENTS DISPLAYS A STOP INDICATION, STOP MUST BE MADE WEST OF EDGINGTON ST UNTIL SIGNAL DISPLAYS A PROCEED IS RECEIVED. IF VERBAL PERMISSION TO PROCEED IS RECEIVED PAST SIGNAL DISPLAYING STOP, EDGINGTON ST CROSSING MUST BE PROTECTED PER RULE 6.32.2

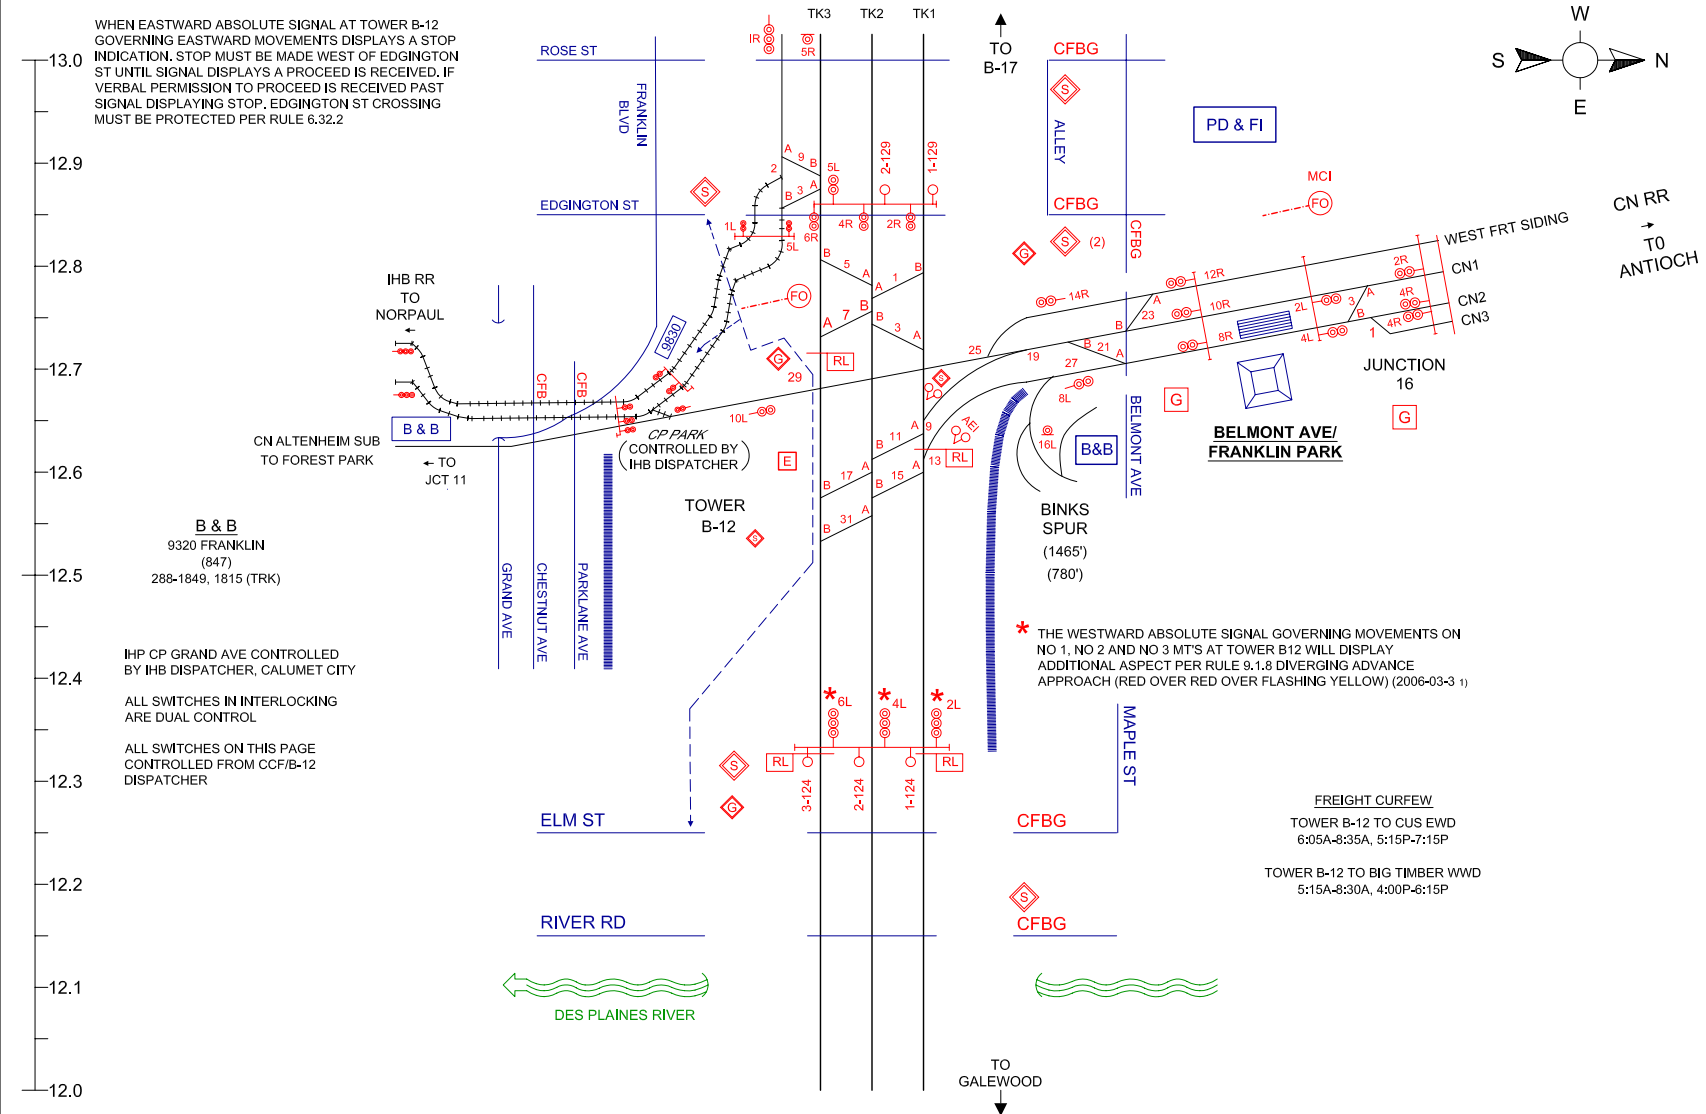


DETAIL VIEW OF TOWER B-12 INTERLOCKING



CONTROL POINT PHONE NUMBERS
 CPR DISPATCHER (612) 904-5834
 (800) 874-7635
 TOWER B-17 (630) 860-4401

RFQ 161.520 AAR 94

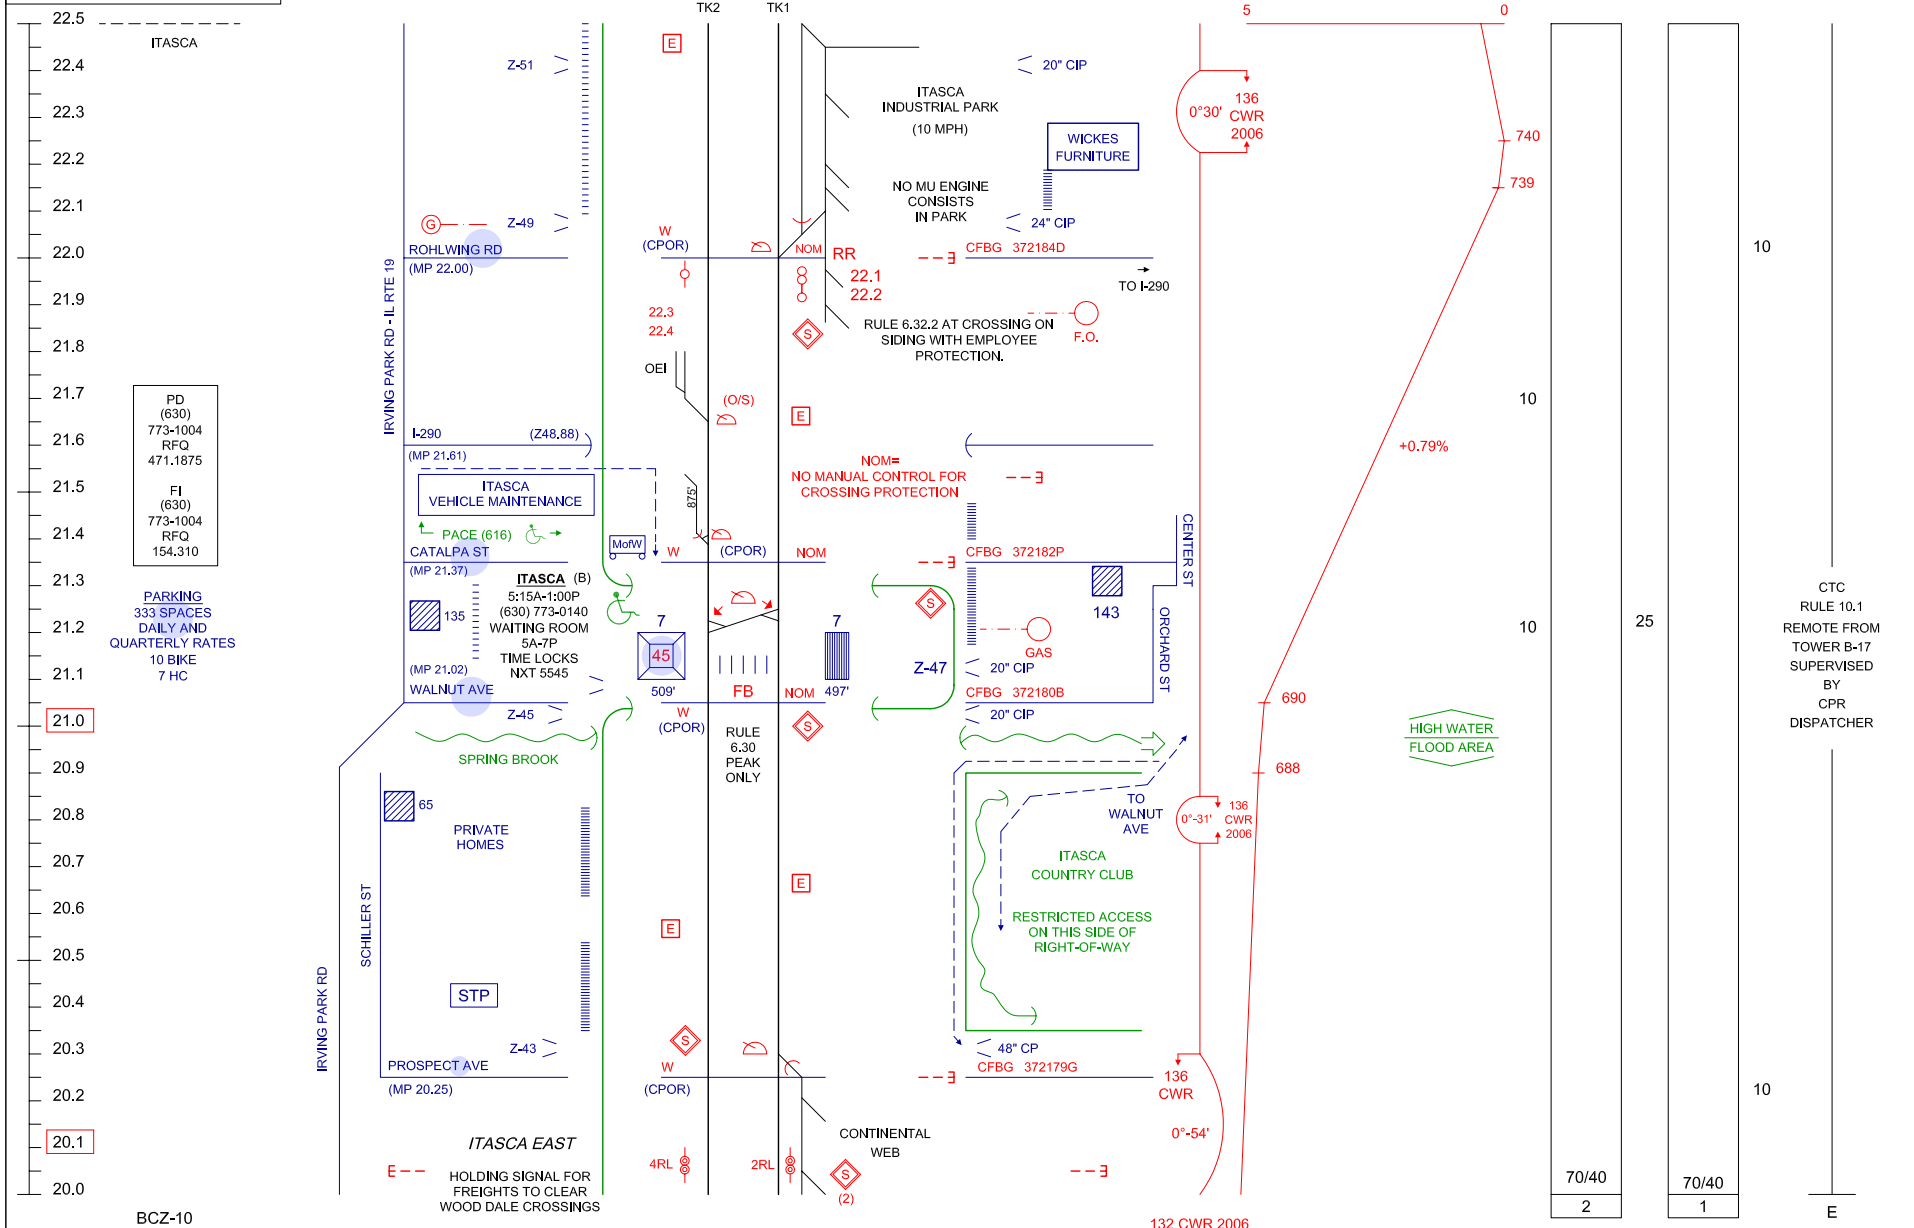


REV 7-22-08

C 6 S 23 L 46 2914

MILWAUKEE DISTRICT / (CPR) ELGIN SUBDIVISION


P-44

BCZ-10

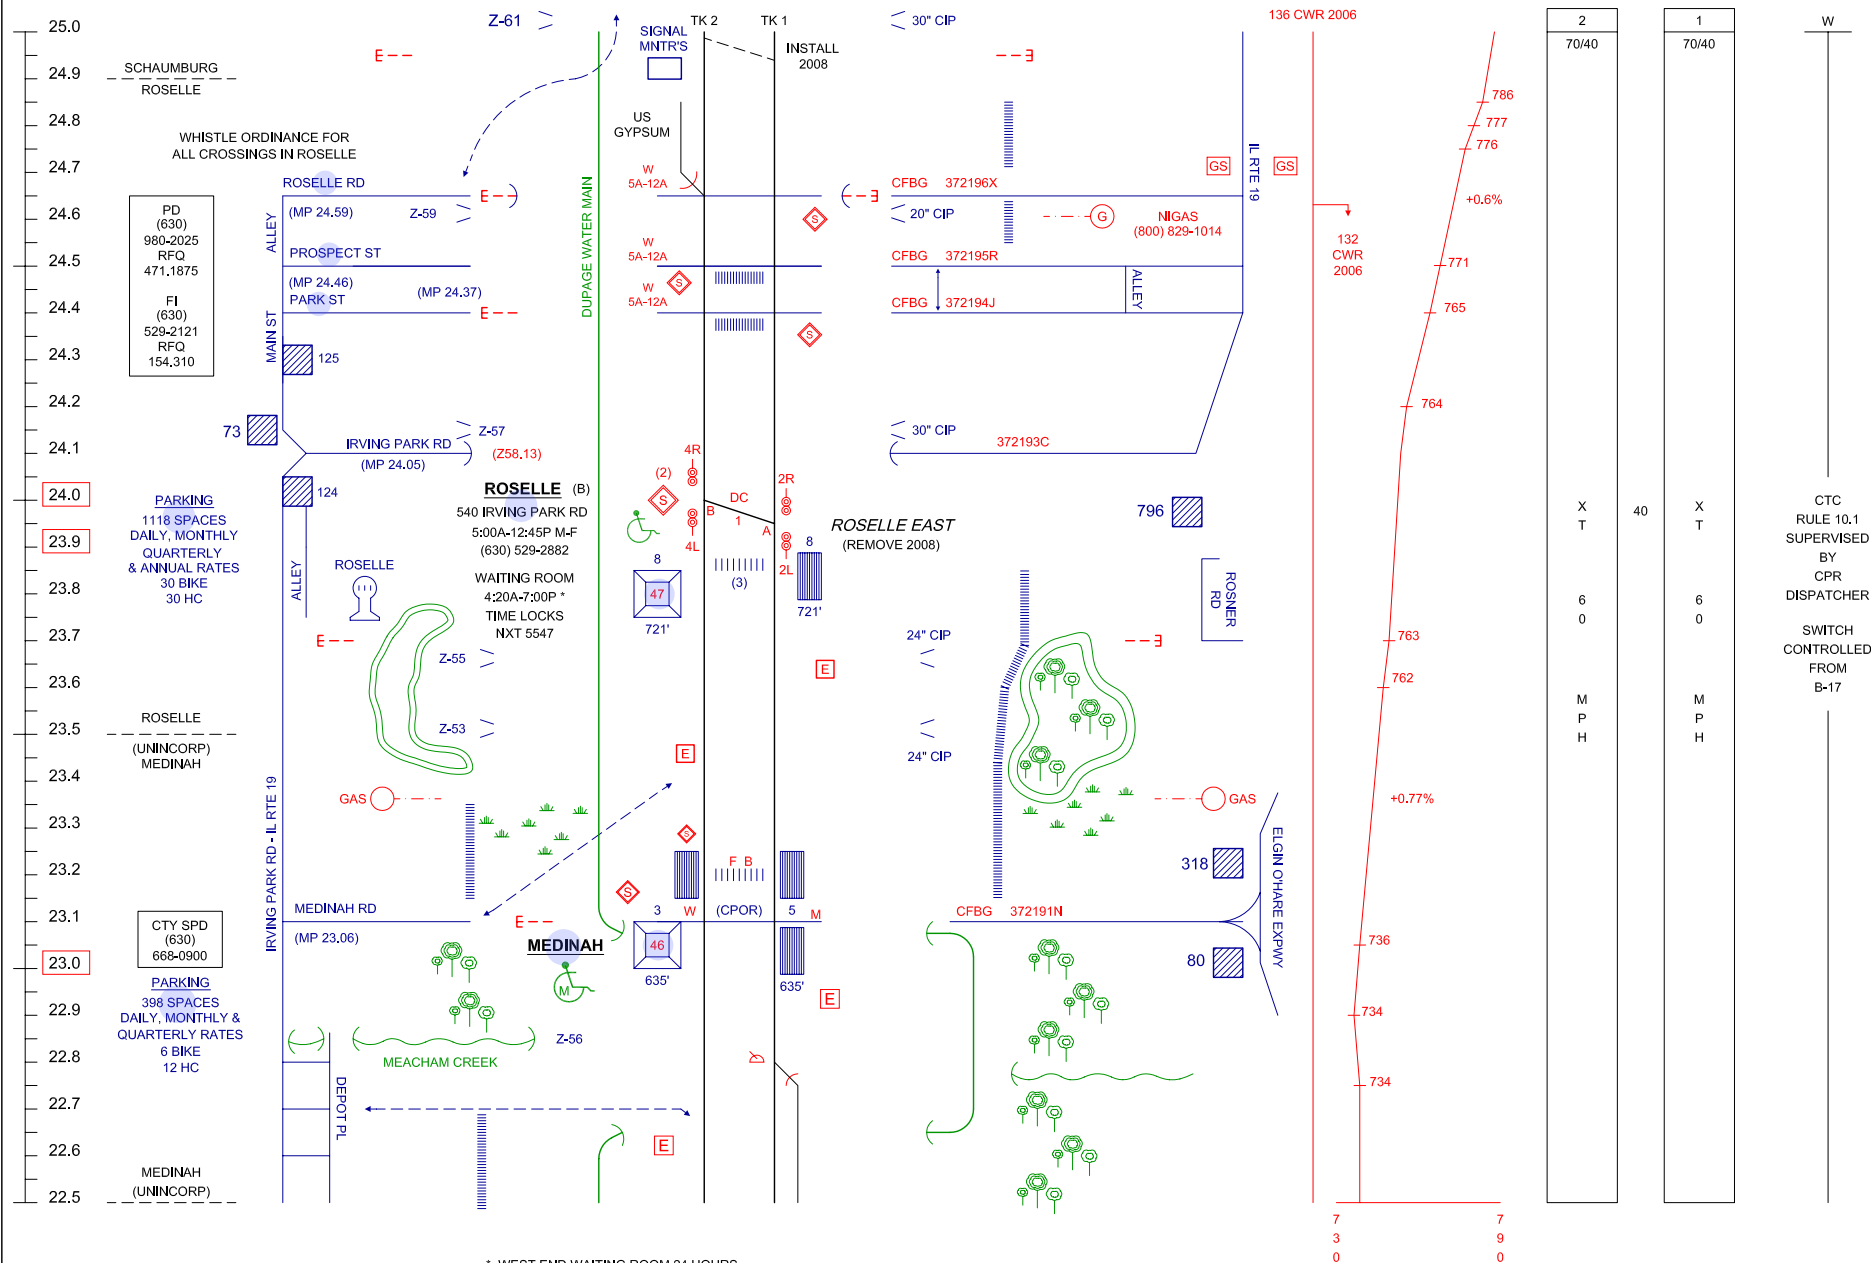

CONTROL POINT PHONE NUMBERS
 CPR DISPATCHER (612) 904-5834
 (800) 874-7635
 TOWER B-17 (630) 860-4401

RFQ 161.520 AAR 94

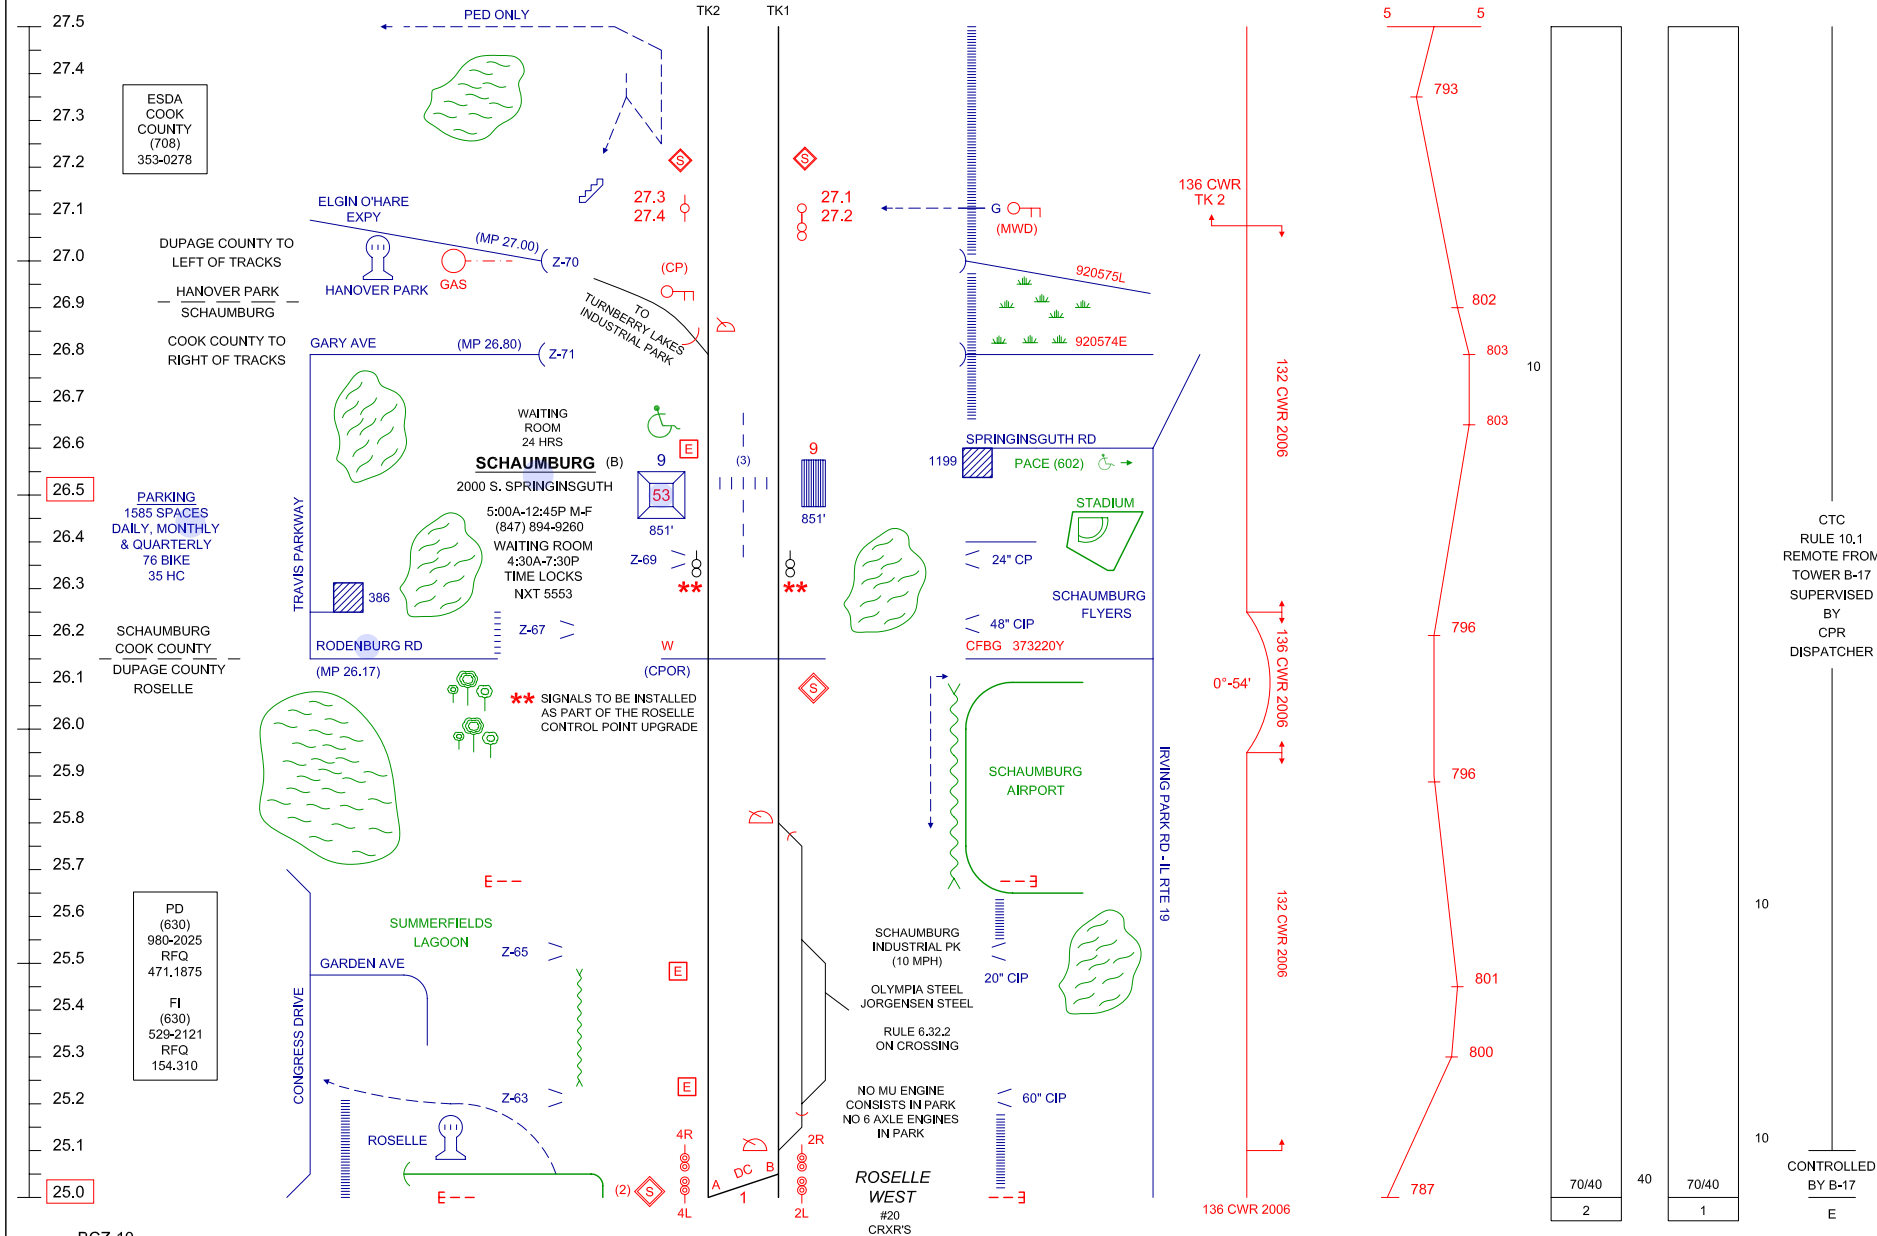


BCZ-10

FARE ZONE F

REV 7-22-08


(C) 6	(S) 28	(L) 56	2912	MILWAUKEE DISTRICT / (CPR) ELGIN SUBDIVISION	P-46
----------	-----------	-----------	------	--	------



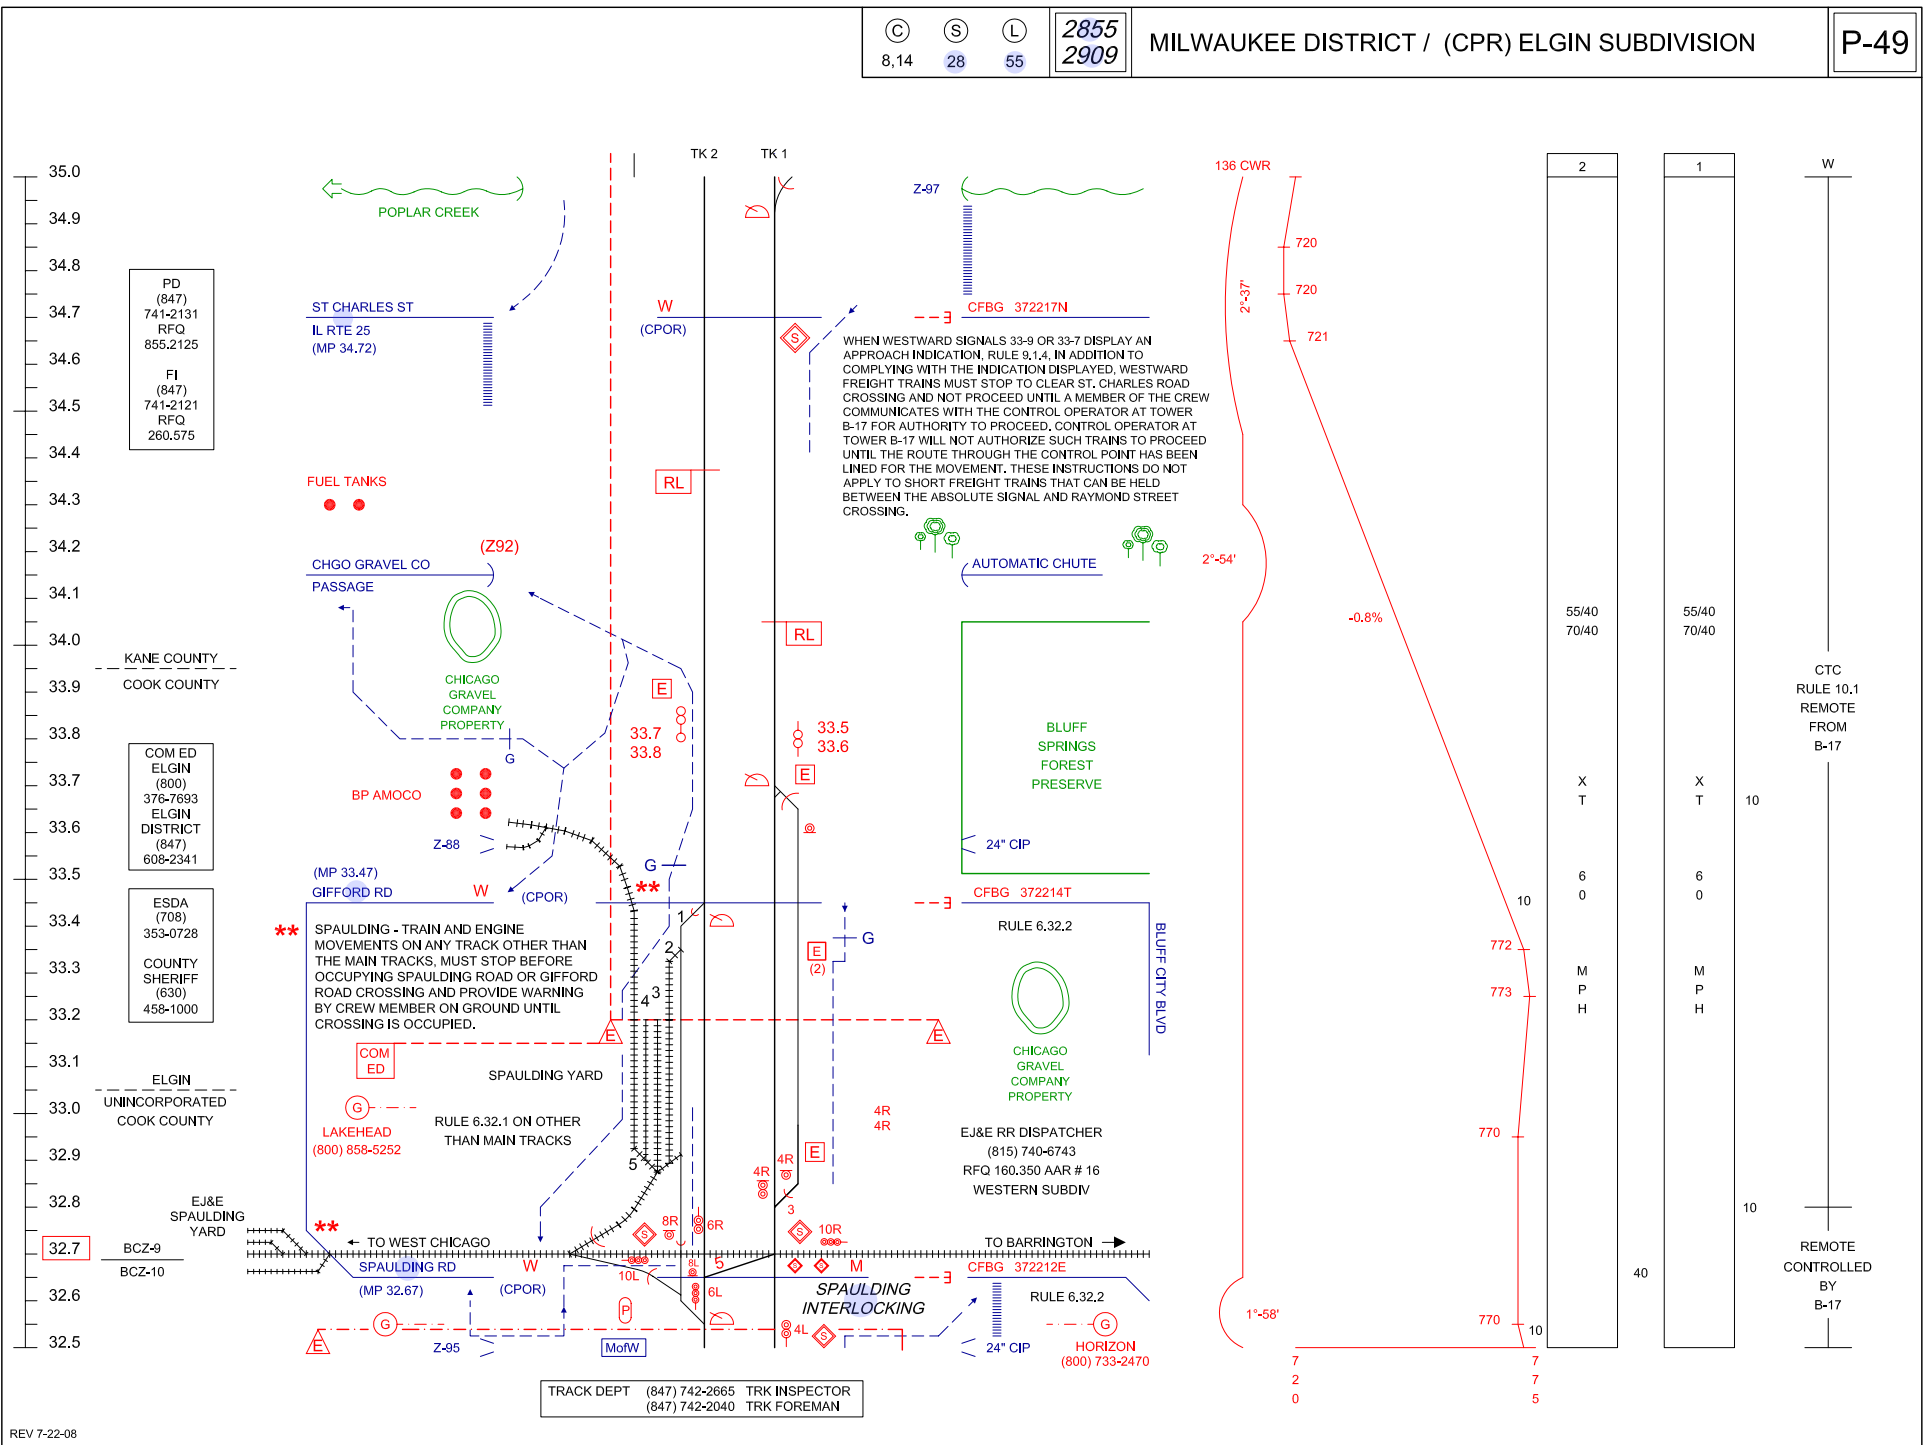


REV 7-22-08

CREWS GOING ON-DUTY AT ELGIN AND RELIEVING WWD CREWS ON TRAINS FOR BIG TIMBER RD WILL BE GOVERNED BY A TGBO RECEIVED IN CHGO FOR THE ORIGINAL MOVEMENT. DUPLICATE COPY OF OUTBOUND TGBO WILL BE FAXED FROM CHGO. OUTBOUND CREW MUST CHECK WITH RELIEVING CREW FOR ANY CHANGES.

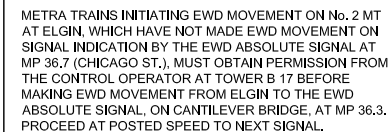

MILWAUKEE DISTRICT / (CPR) ELGIN SUBDIVISION
REV 7-22-08

Page 42 of 44

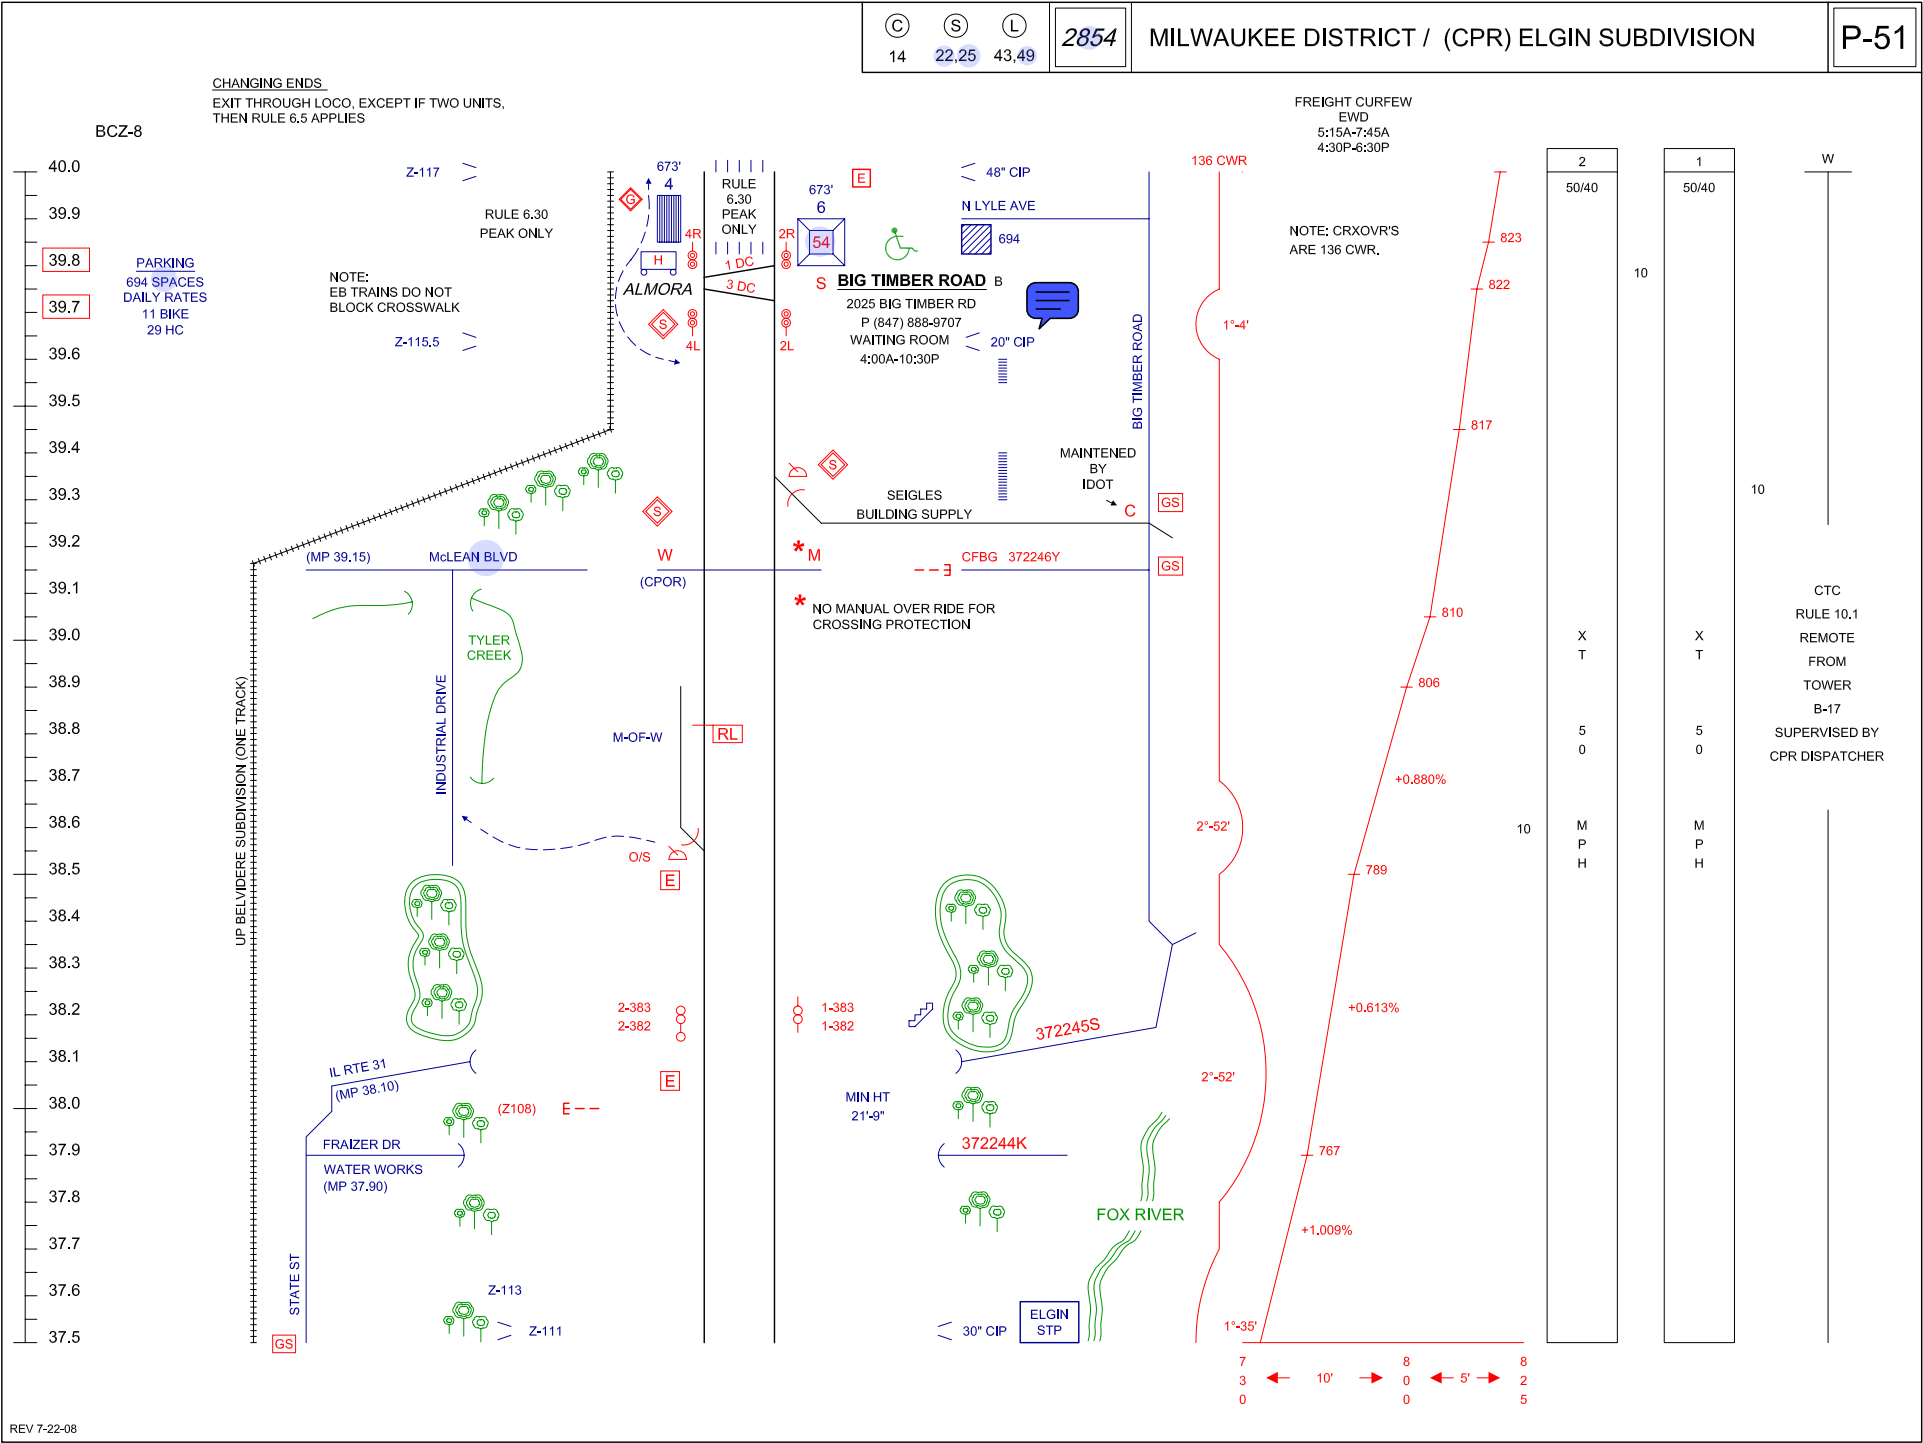

NOTE:
WB TRAINS DO NOT PROCEED BEYOND
MP 40.1 DUE TO NOISE PROBLEMS AT
HINCKLEY & SCHMITT PLANT UNTIL
READY TO RETURN TO BIG TIMBER

UNDER JURISDICTION OF
IOWA
CHICAGO & EASTERN RR
TO
HAMPSHIRE
DISPATCHER
(605) 782-1421

