

Metra

OPERATIONS PROFILE

NOTICE:

BLUE DOT INDICATES A LINK



W.K. TUPPER Deputy Executive Director, Operations
G.L. HARDWIDGE Chief Transportation Officer
S.A. AUSTIN Sr. Director, Customer Affair/Training

ROCK ISLAND DISTRICT

TABLE OF CONTENTS

● ROCK ISLAND DISTRICT	8
Joliet Sub District	10
Beverly Sub District	29
Blue Island Area Detail	32
● INDEX	34

SEPTEMBER 1, 2009

PROJECT MANAGER & CHIEF DESIGNER:

J.M. GOTTLIEB

OPERATING RULES DATA:

L.C. MICHAEL

COMPLIANCE, EDITING & REORGANIZATION:

T.G. PITZEN, L.G. GOMM, K. RABE, M.T. HUSAR

FIELD VERIFICATION TEAM:

J.S. TALLYN

T.G. PITZEN

J. TREMPER

GRADE CROSSING DATA:

S.C. LAFFEY - ICC


PARKING LOT DATA:


L.G. GOMM

Operations Profile represents Metra's compliance with **49CFR239** governing emergency preparedness specific to geographic locations on specific line segments.

CONTROL POINT PHONE NUMBERS 16TH ST TOWER (312) 322-8958
 ROOT ST TOWER (312) 322-7775 RID TERMINAL DISPATCHER (312) 322-2854

UPON ARRIVAL AT LASALLE ST ALL TRAINS
 SCHEDULED TO GO TO COACH YARD OR STAY
 AT DEPOT WILL CLOSE ALL DOORS PRIOR TO
 SHUT DOWN OF HEAD END POWER.

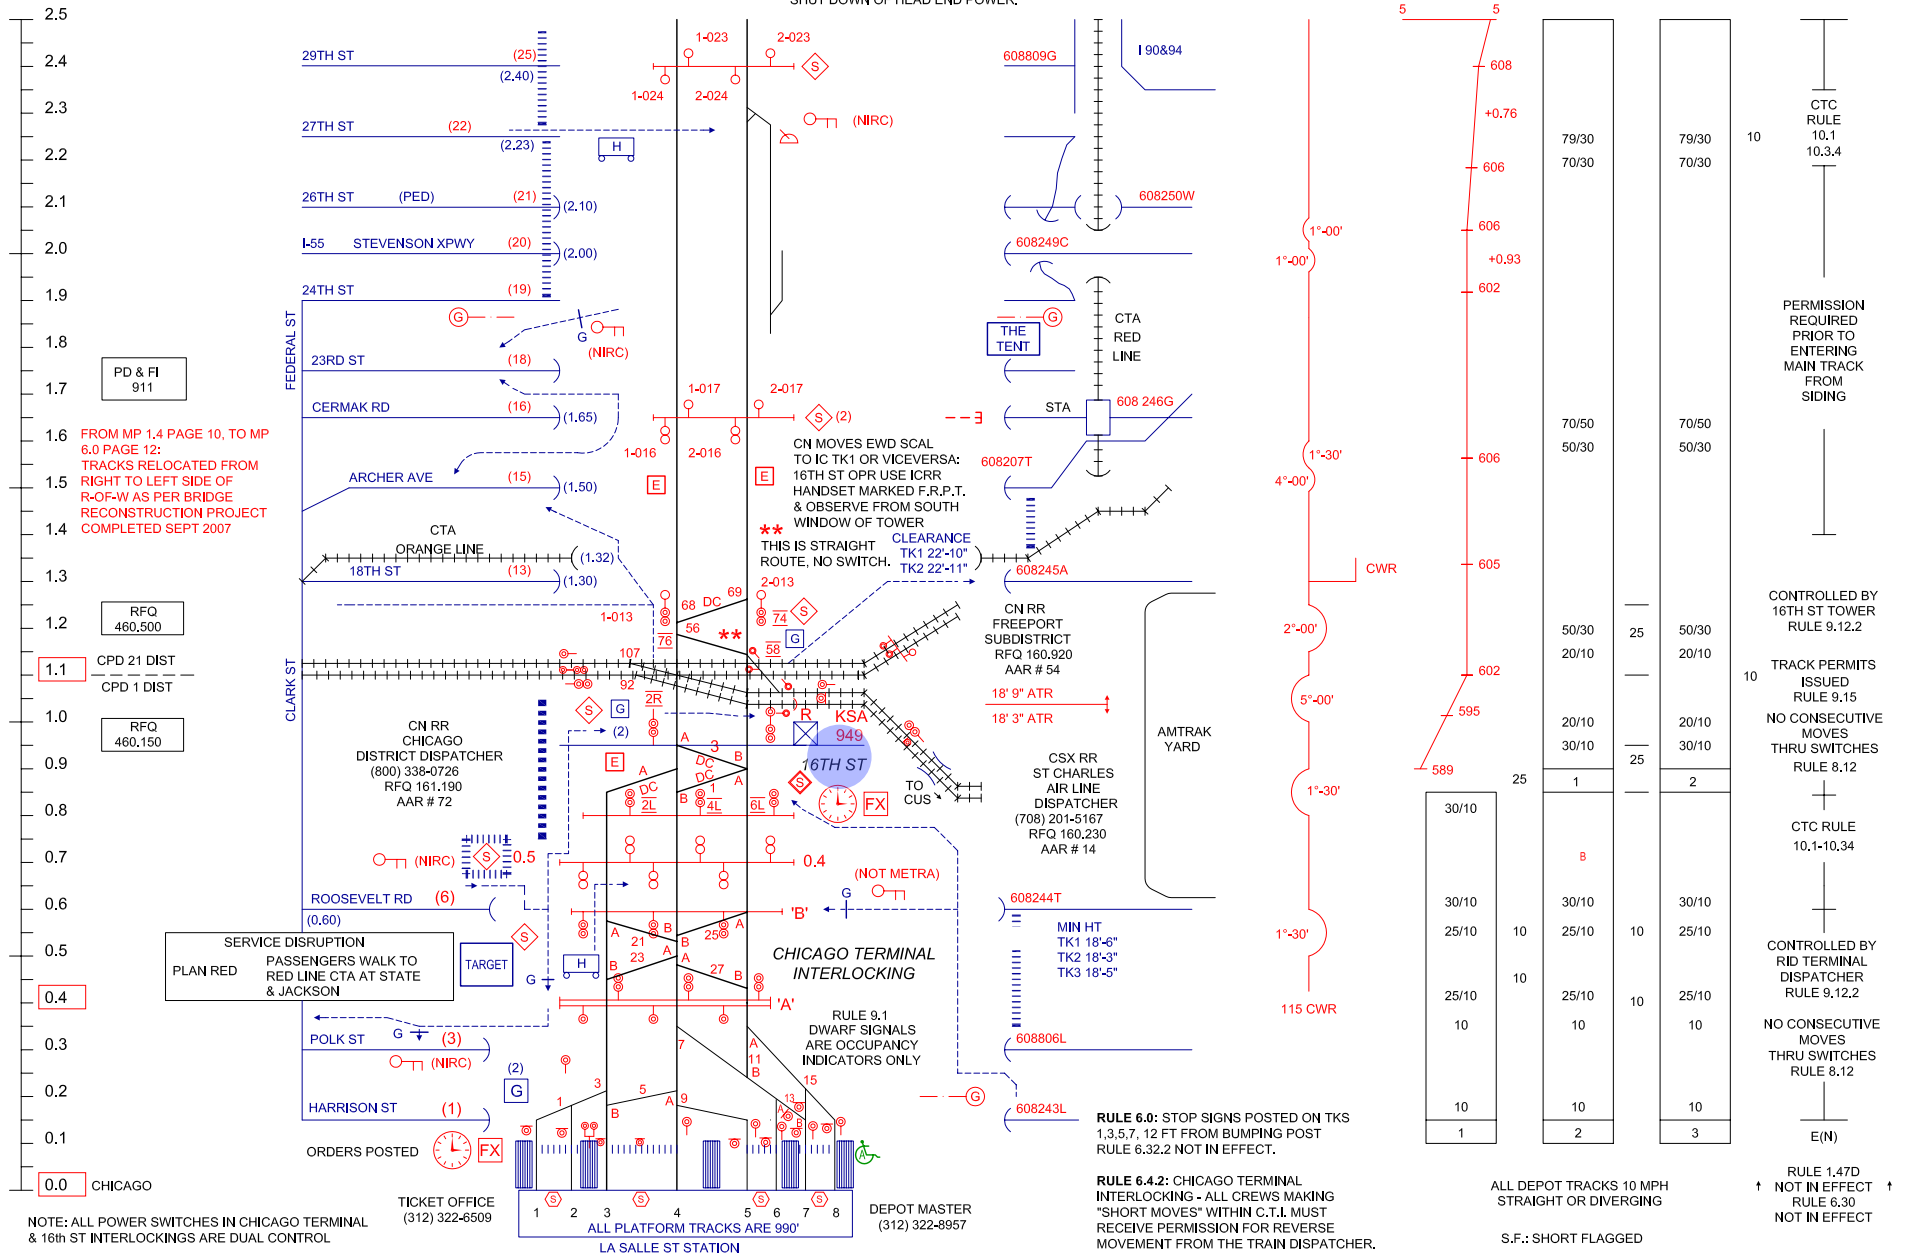


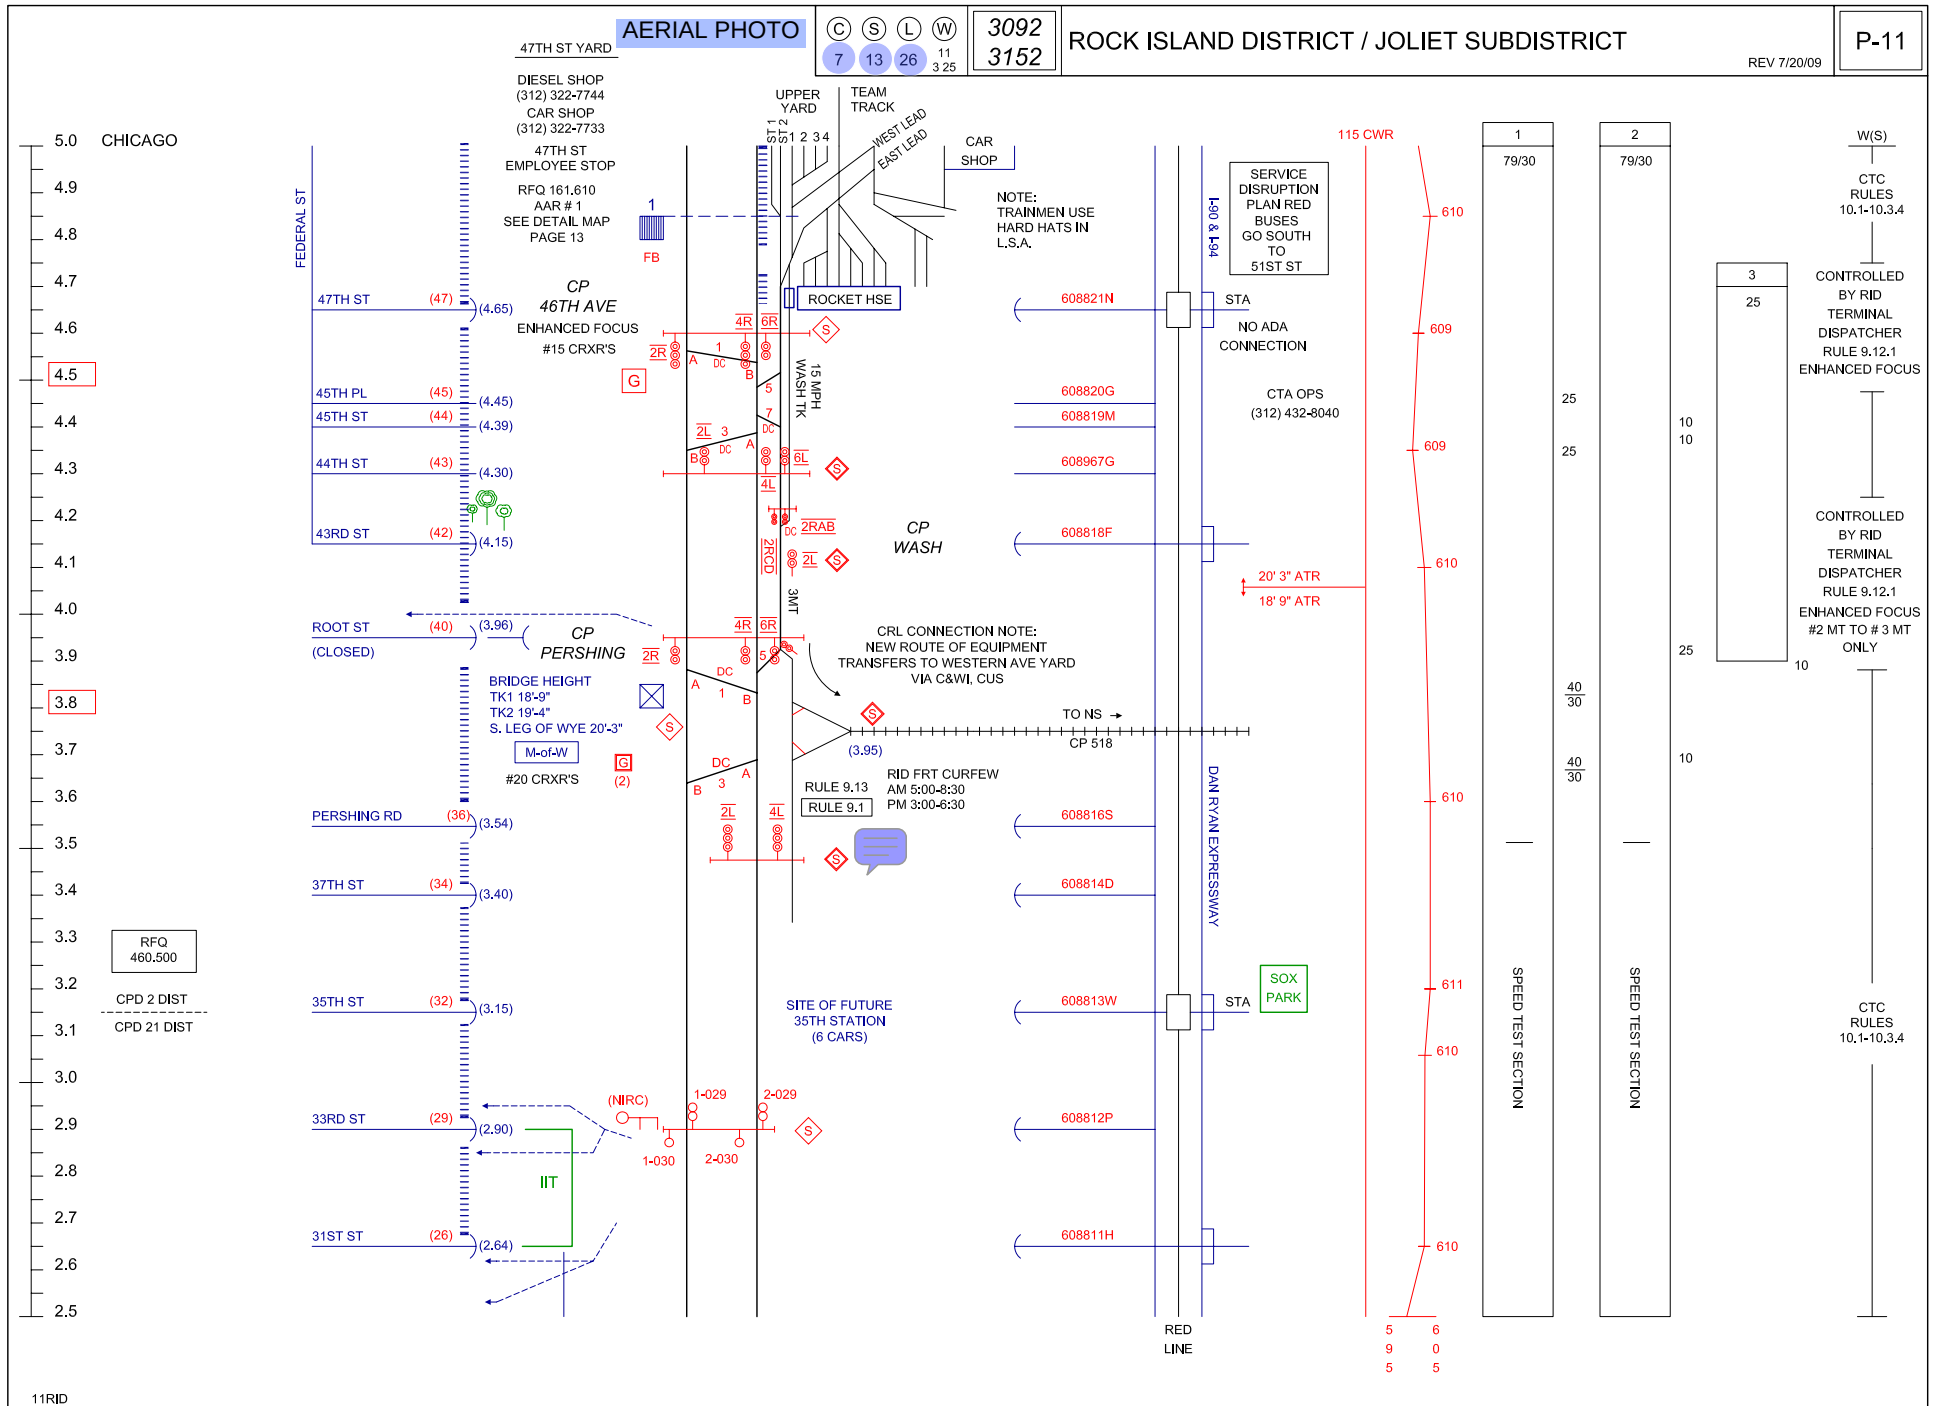

CONTROL POINT
PHONE NUMBERS

ROOT STREET TOWER (312) 322-7775
NSRR DISPATCHER (313) 323-5030-50-5868
GRESHAM TOWER (312) 322-7995
RID TERMINAL DISPATCHER (312) 322-2854

RFQ 161.340 AAR 82

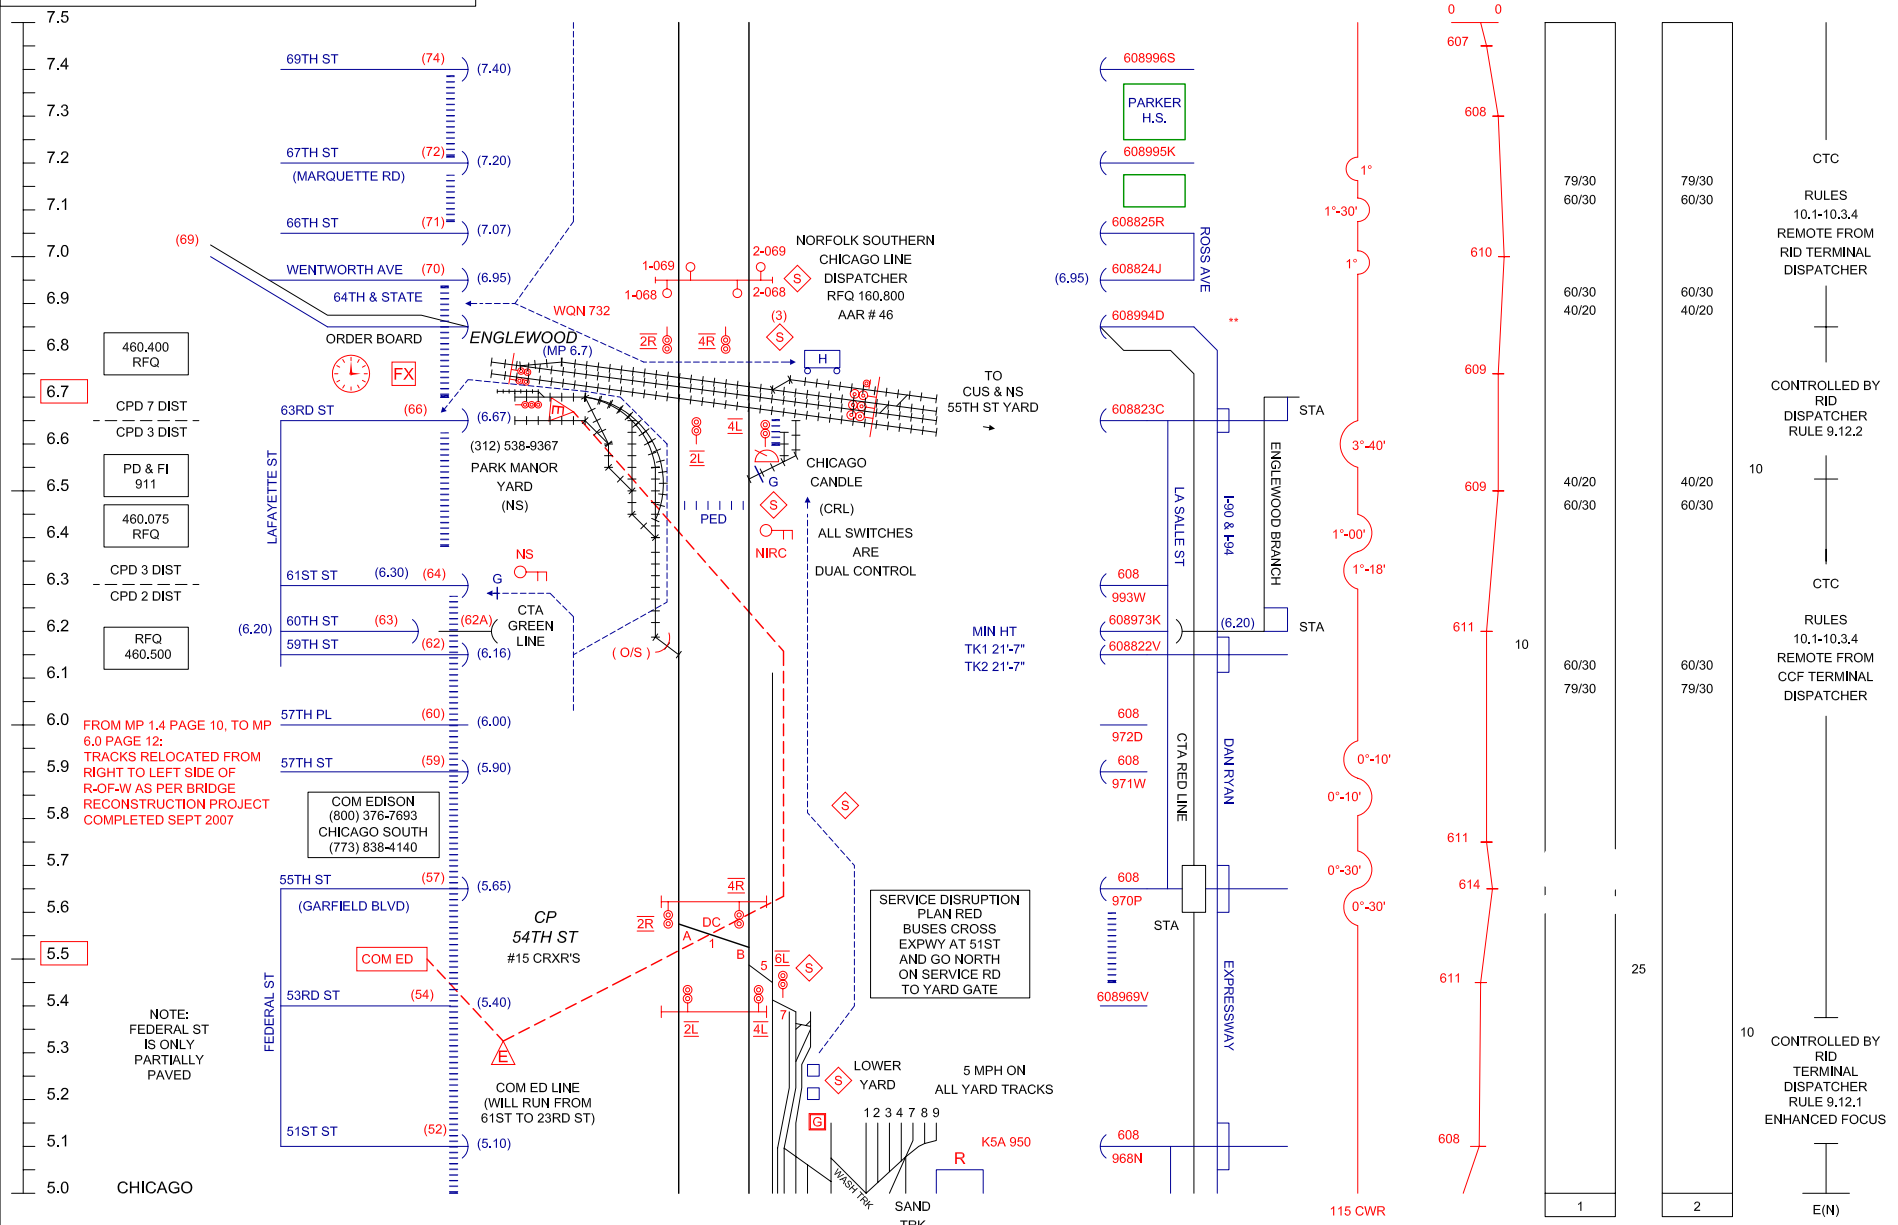

FARE ZONE B

12RID



C S L W
7 13 26 30
3152

ROCK ISLAND DISTRICT / JOLIET SUBDISTRICT

REV 7/20/09

P-12

SHOP RFQ 161.610 AA #1

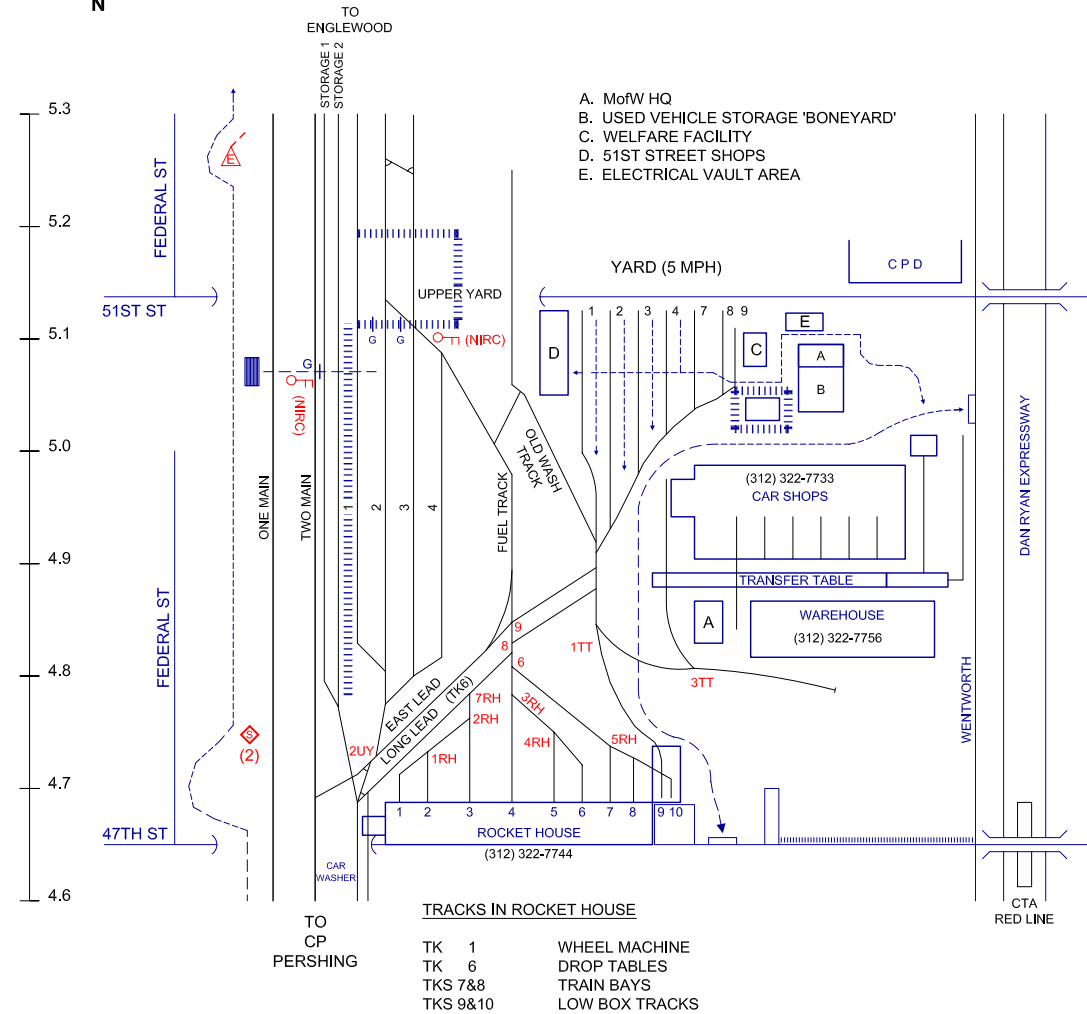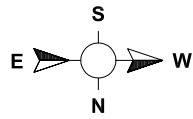

IT WILL BE THE RESPONSIBILITY OF TRAIN CREW AND CAR MEN TO GET A SET & RELEASE ON ALL EQUIPMENT TRAINS DEPARTING 51ST ST YARD FOR LSS. IF NO CAR MAN, TRAIN CREW MUST PERFORM AIR TEST.


OPERATION THROUGH TRAIN WASHER AT 47TH STREET YARD :

THE TRAIN WASHER IS FULLY AUTOMATED WITH OPERATION CONTROLLED BY 2 SENSORS LOCATED ON WASH TRACK, AT MP 4.6, APPROXIMATELY 100 FEET (FIRST SENSOR) AND 50 FEET (SECOND SENSOR) EAST OF THE TRAIN WASHER BUILDING. TRAINS TO BE WASHED MUST APPROACH THE FIRST SENSOR NOT EXCEEDING 3 MPH AND MUST DETERMINE THAT THE PRECEDING TRAIN HAS CLEARED THE WEST END OF THE WASHER BEFORE FOULING THE FIRST SENSOR. THE FIRST SENSOR WILL ACTIVATE THE BUILDING DOORS AND A GREEN LIGHT WILL BE DISPLAYED INDICATING THAT THE MOVEMENT CAN ENTER THE BUILDING, AS THE MOVEMENT PASSES THE SECOND SENSOR, THE WASHING CYCLE WILL BE ACTIVATED. WASHING SPEED IS 2 MPH. THE FOLLOWING LIGHT SIGNALS AND INDICATIONS MAY BE DISPLAYED, INSIDE THE BUILDING, DURING THE WASHING CYCLE:


- **GREEN** - THE MOVEMENT IS OPERATING AT THE PROPER WASHING SPEED OF 2 MPH.
- **FLASHING YELLOW** - THE MOVEMENT HAS REACHED 3 MPH AND SPEED MUST BE REDUCED.
- **RED** - THE MOVEMENT HAS REACHED 4 MPH AND MUST STOP. - 5 MPH IF WASHER IS CLOSED

THE WASHING CYCLE WILL AUTOMATICALLY STOP WHEN THE MOVEMENT'S SPEED REACHES 4 MPH. TO RESTART THE WASHING CYCLE, THE MOVEMENT MUST REMAIN STOPPED AND WAIT FOR A YELLOW LIGHT TO BE DISPLAYED INDICATING THAT THE WASHER HAS RESET. DISPLAY OF THE YELLOW LIGHT INDICATES THAT THE MOVEMENT CAN PROCEED. A REVERSE MOVEMENT MUST NOT BE MADE AFTER ENTERING THE TRAIN WASHER UNLESS PERMISSION IS RECEIVED FROM THE MECHANICAL DEPARTMENT.

NOTE: THERE IS NO CLEARANCE FOR ANYONE TO RIDE ON THE SIDE OF THE EQUIPMENT FOR TRAINS ENTERING OR EXITING THE CAR WASH FACILITY.

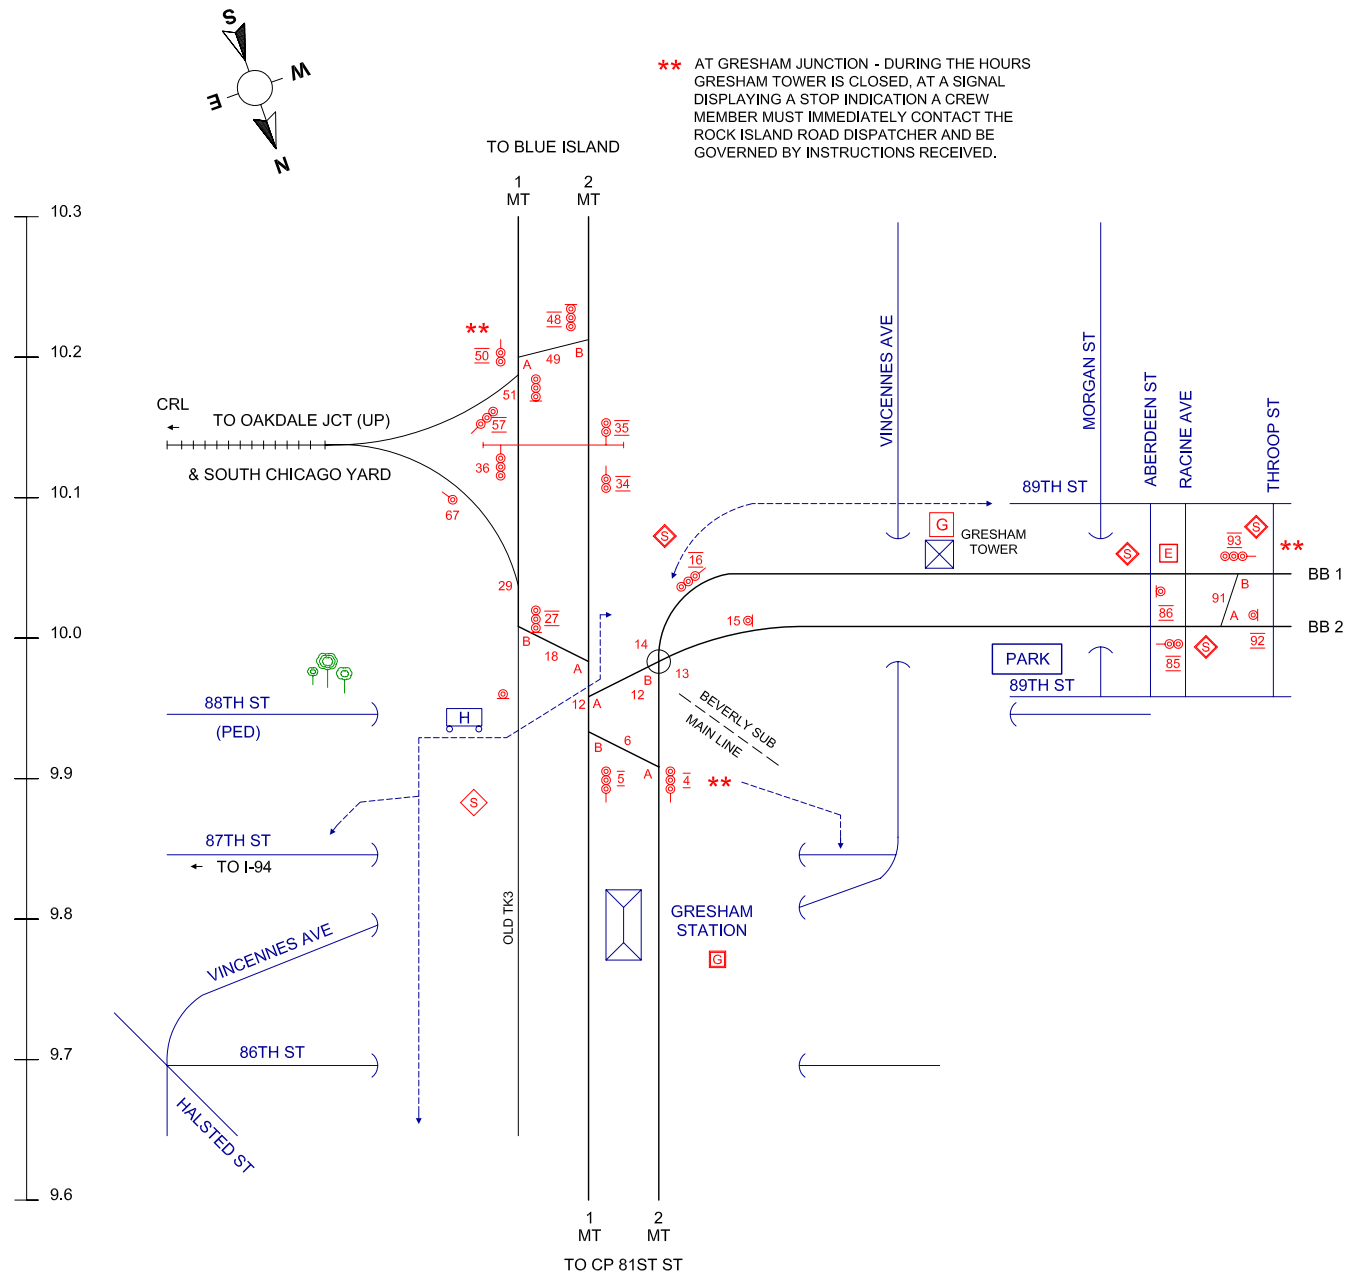


*** AT GRESHAM JUNCTION - DURING THE HOURS GRESHAM TOWER IS CLOSED, AT A SIGNAL DISPLAYING A STOP INDICATION A CREW MEMBER MUST IMMEDIATELY CONTACT THE ROCK ISLAND ROAD DISPATCHER AND BE GOVERNED BY INSTRUCTIONS RECEIVED.

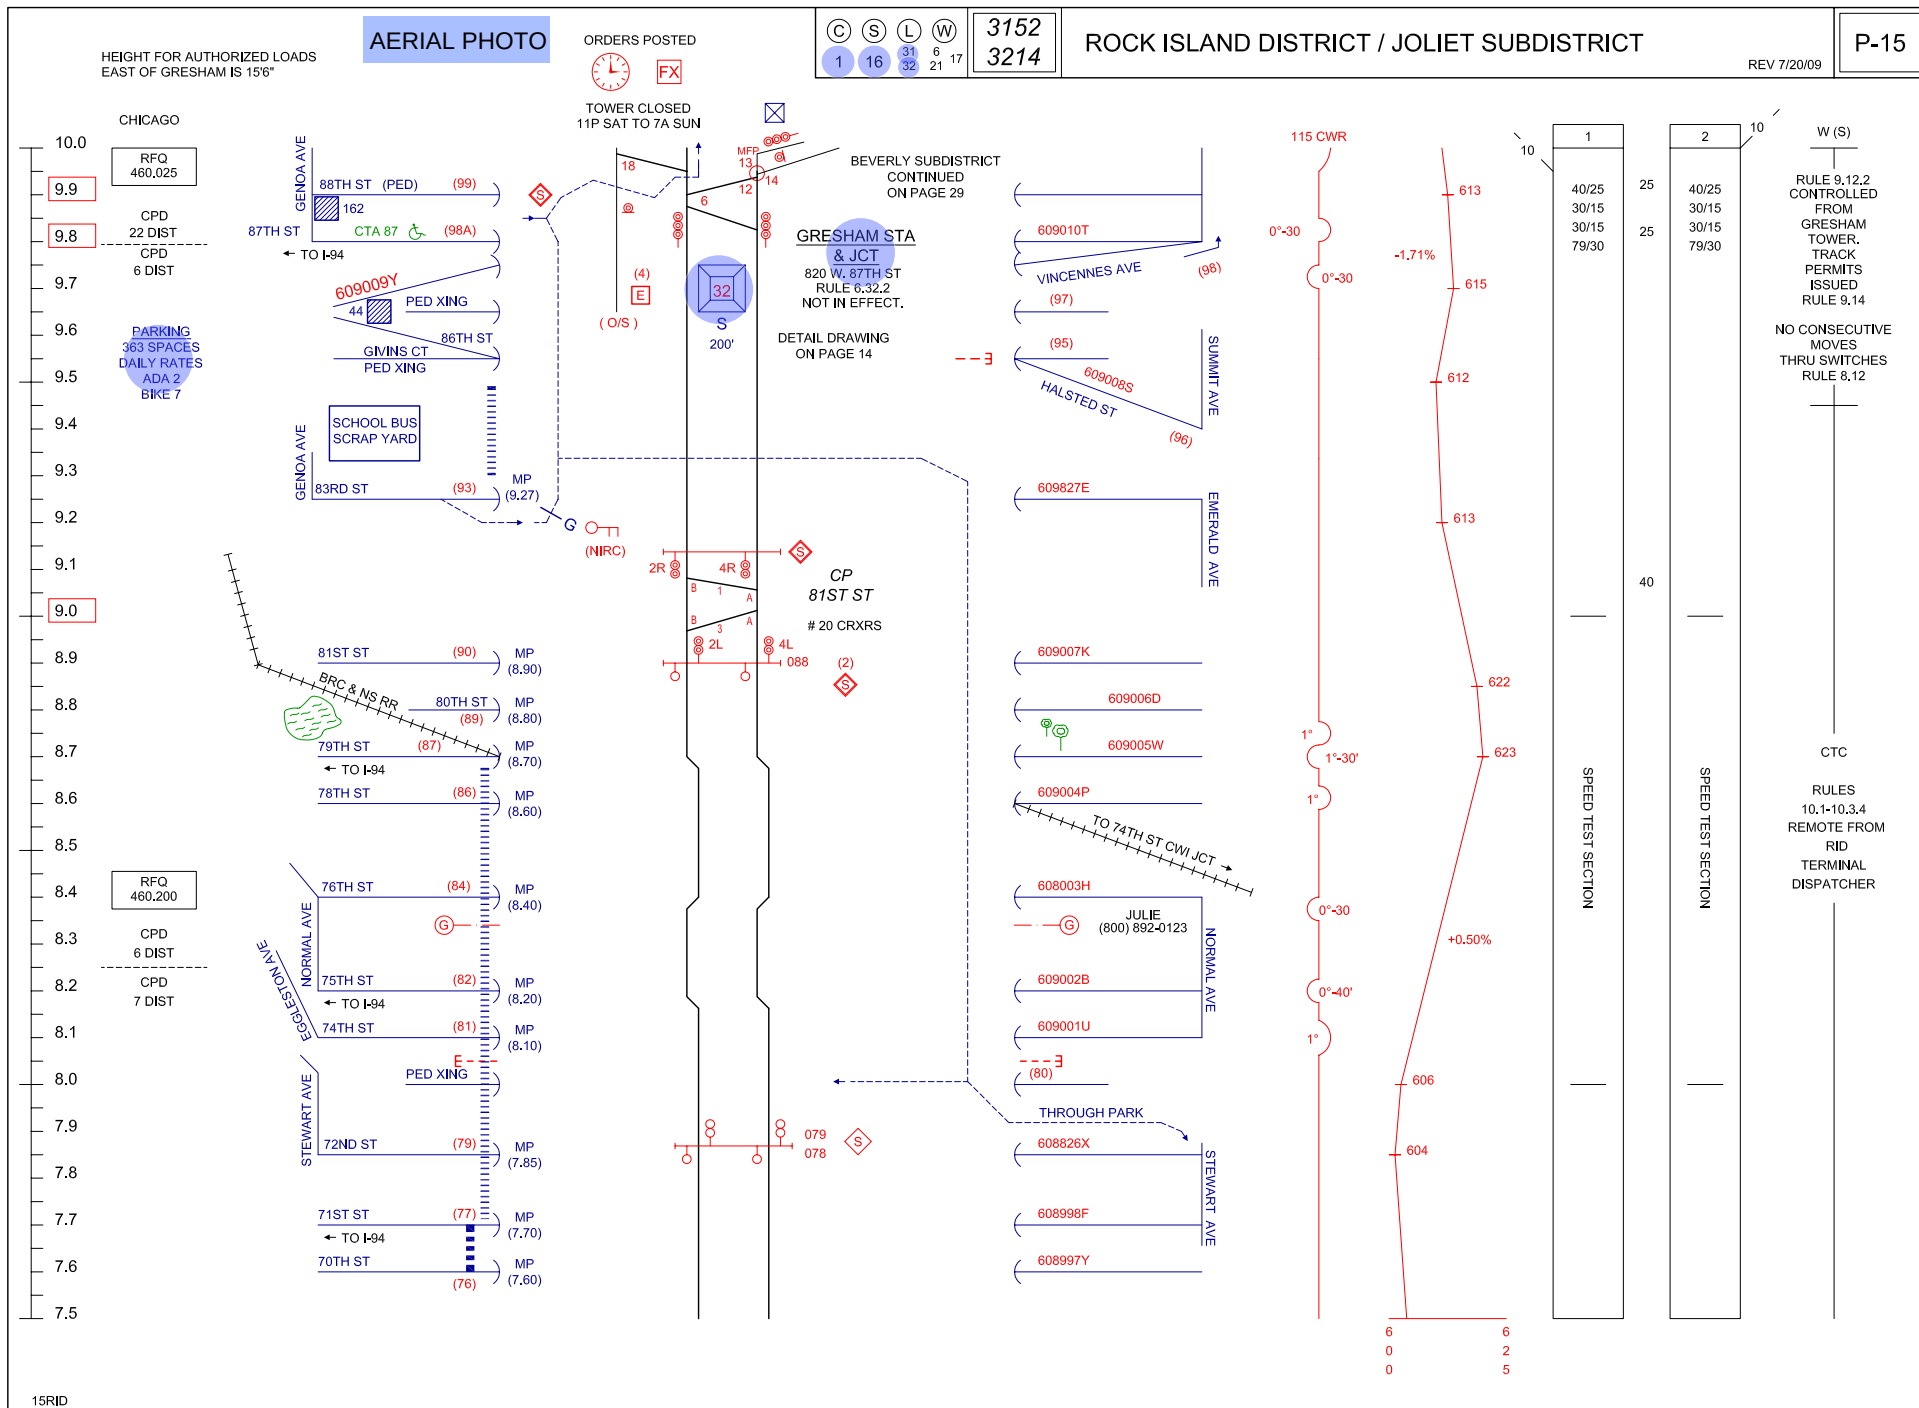

CONTROL POINT PHONE NUMBERS
 GRESHAM TOWER (312) 322-7995
 RID ROAD DISPATCHER (312) 322-2856
 BLUE ISLAND TOWER (CTC) (312) 322-7780

RFQ 161,340 AAR 82

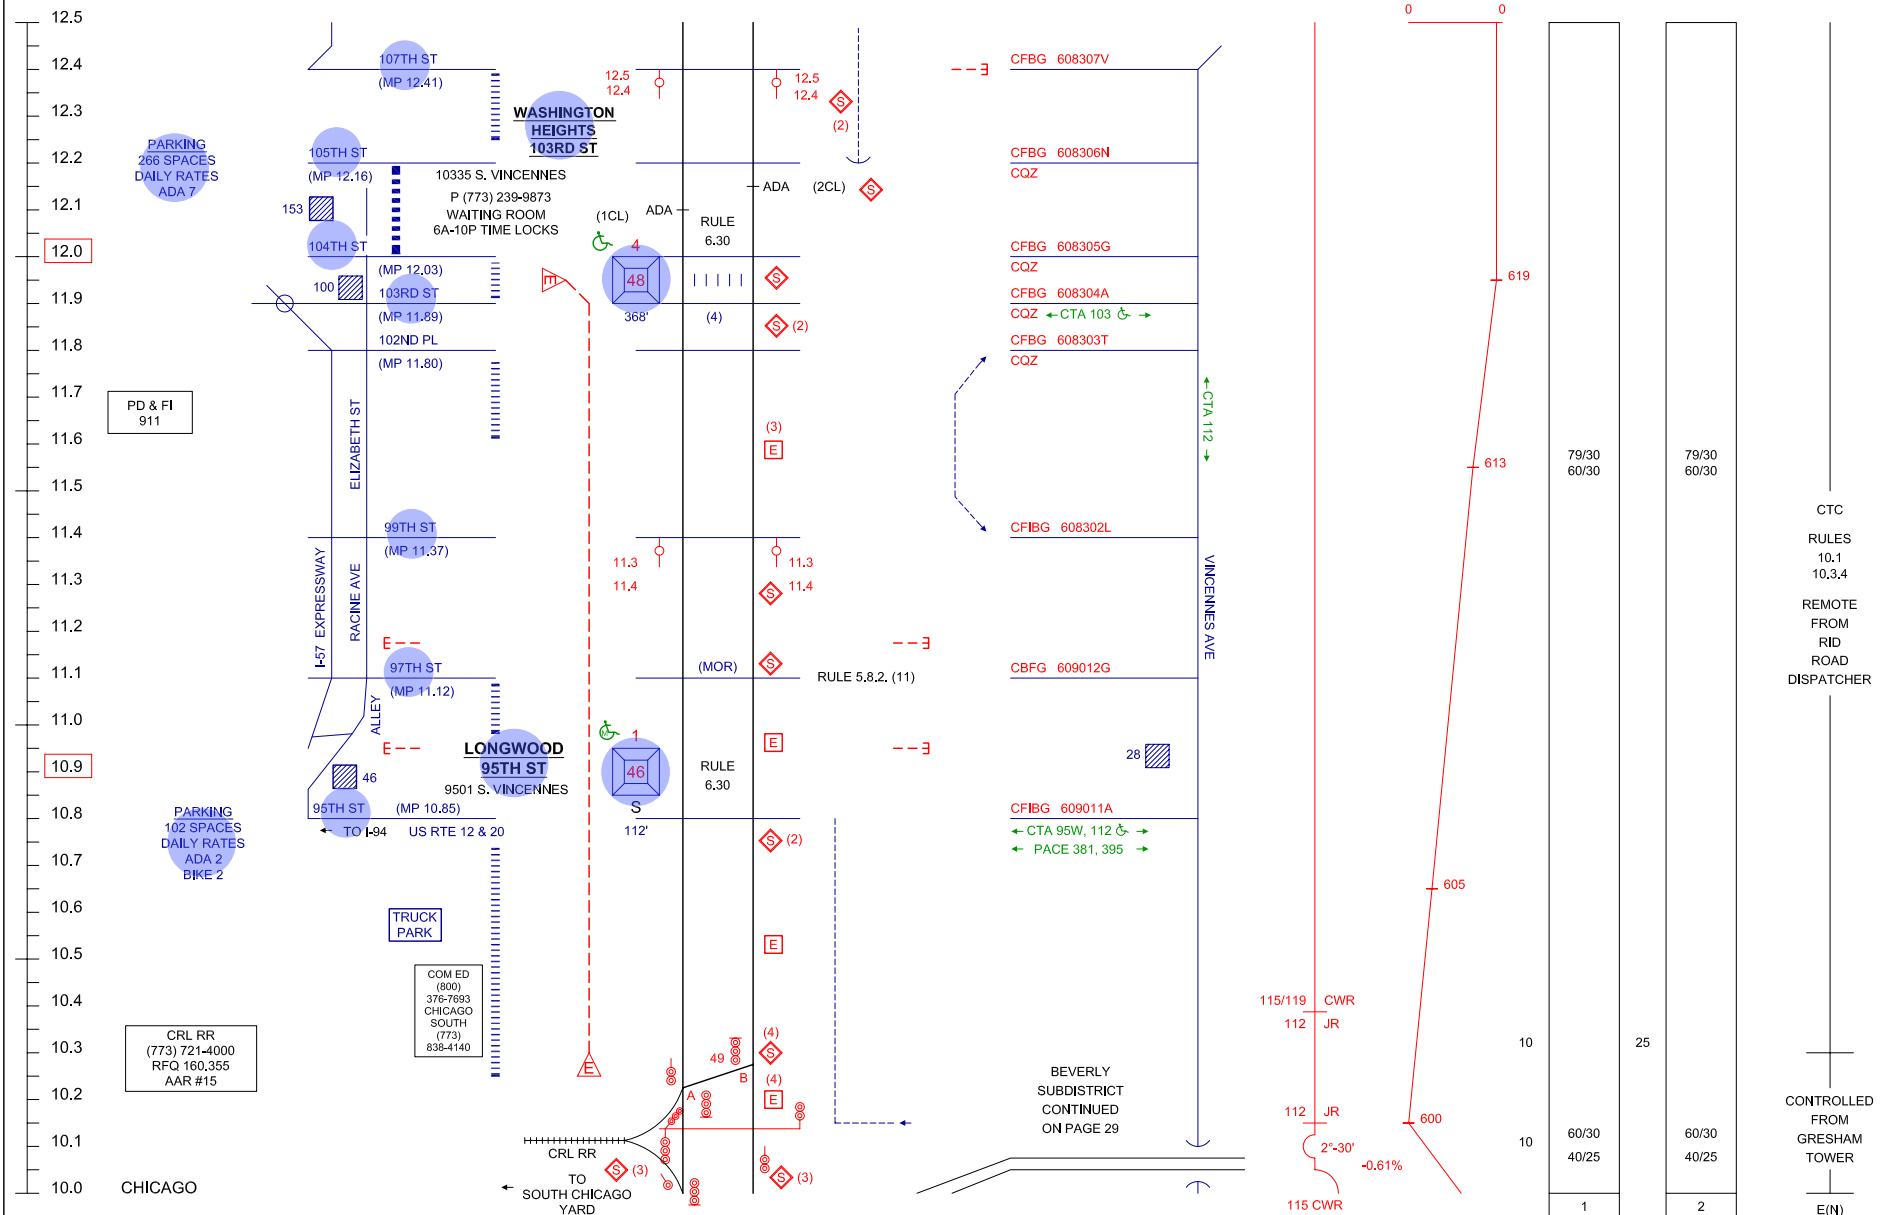

FARE ZONE C

AUTHORIZED HEIGHT FOR
 LOADS WEST OF GRESHAM IS 18'6"

C S L W
 1 14 27 21

3213
 3214
 3277

ROCK ISLAND DISTRICT / JOLIET SUBDISTRICT

REV 7/20/09

P-16

AERIAL PHOTO


C S L W
1 14 27 19
34

3277

ROCK ISLAND DISTRICT / JOLIET SUBDISTRICT

REV 7/20/09

P-17

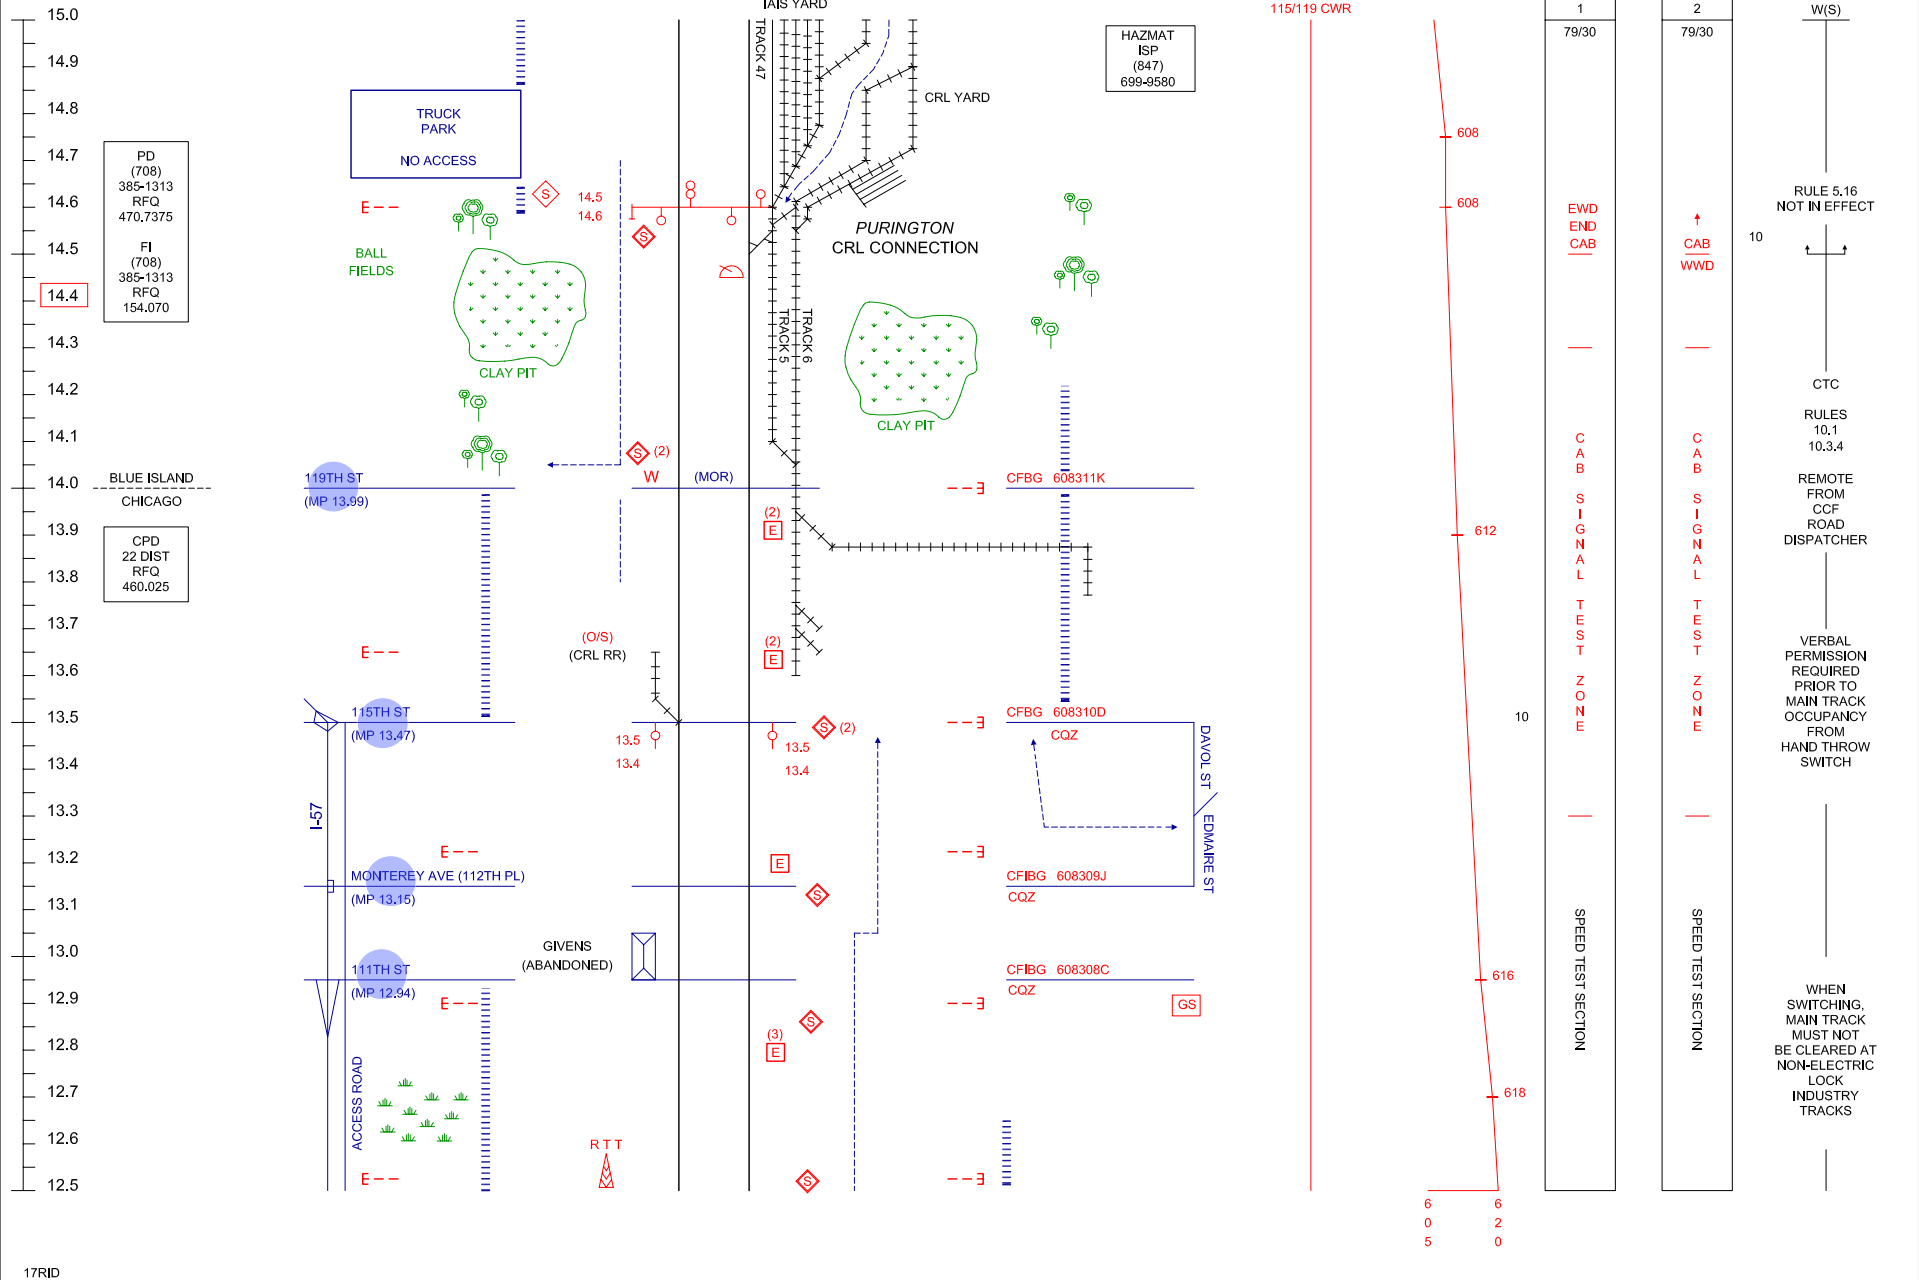

TRAINMASTER FAX (708) 293-6170
RID ROAD DISPATCHER (312) 322-2856


[illegible]


**NOTE:
RULE 6.32.2
BI OPERATOR CAN REMOTELY CONTROL
CROSSING GATES AT VERMONT
& GROVE STREETS**

(C)	(S)	(L)	3227
1	14	28	3348
	15	30	3349

P-18

REV 7/20/09

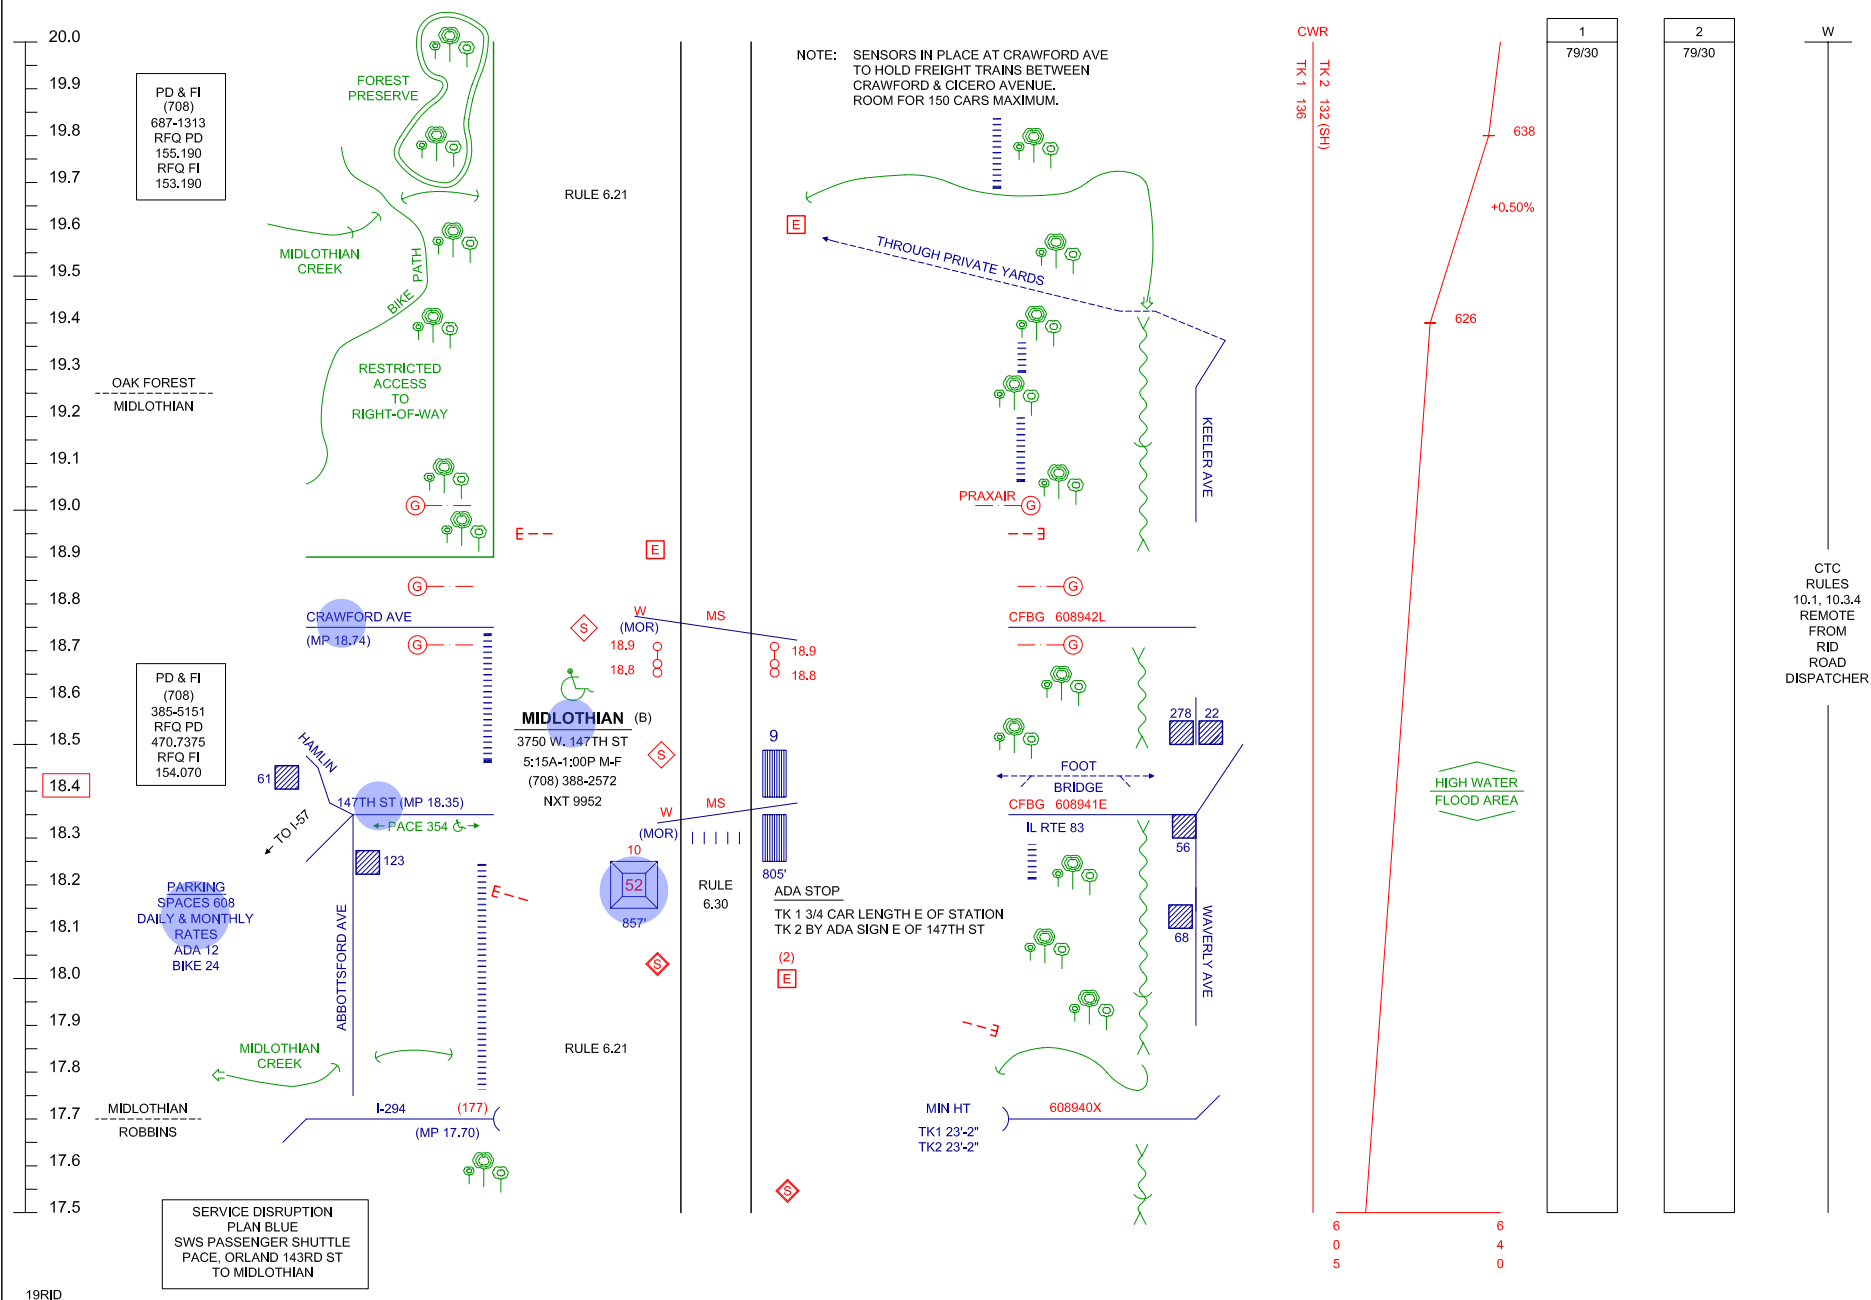

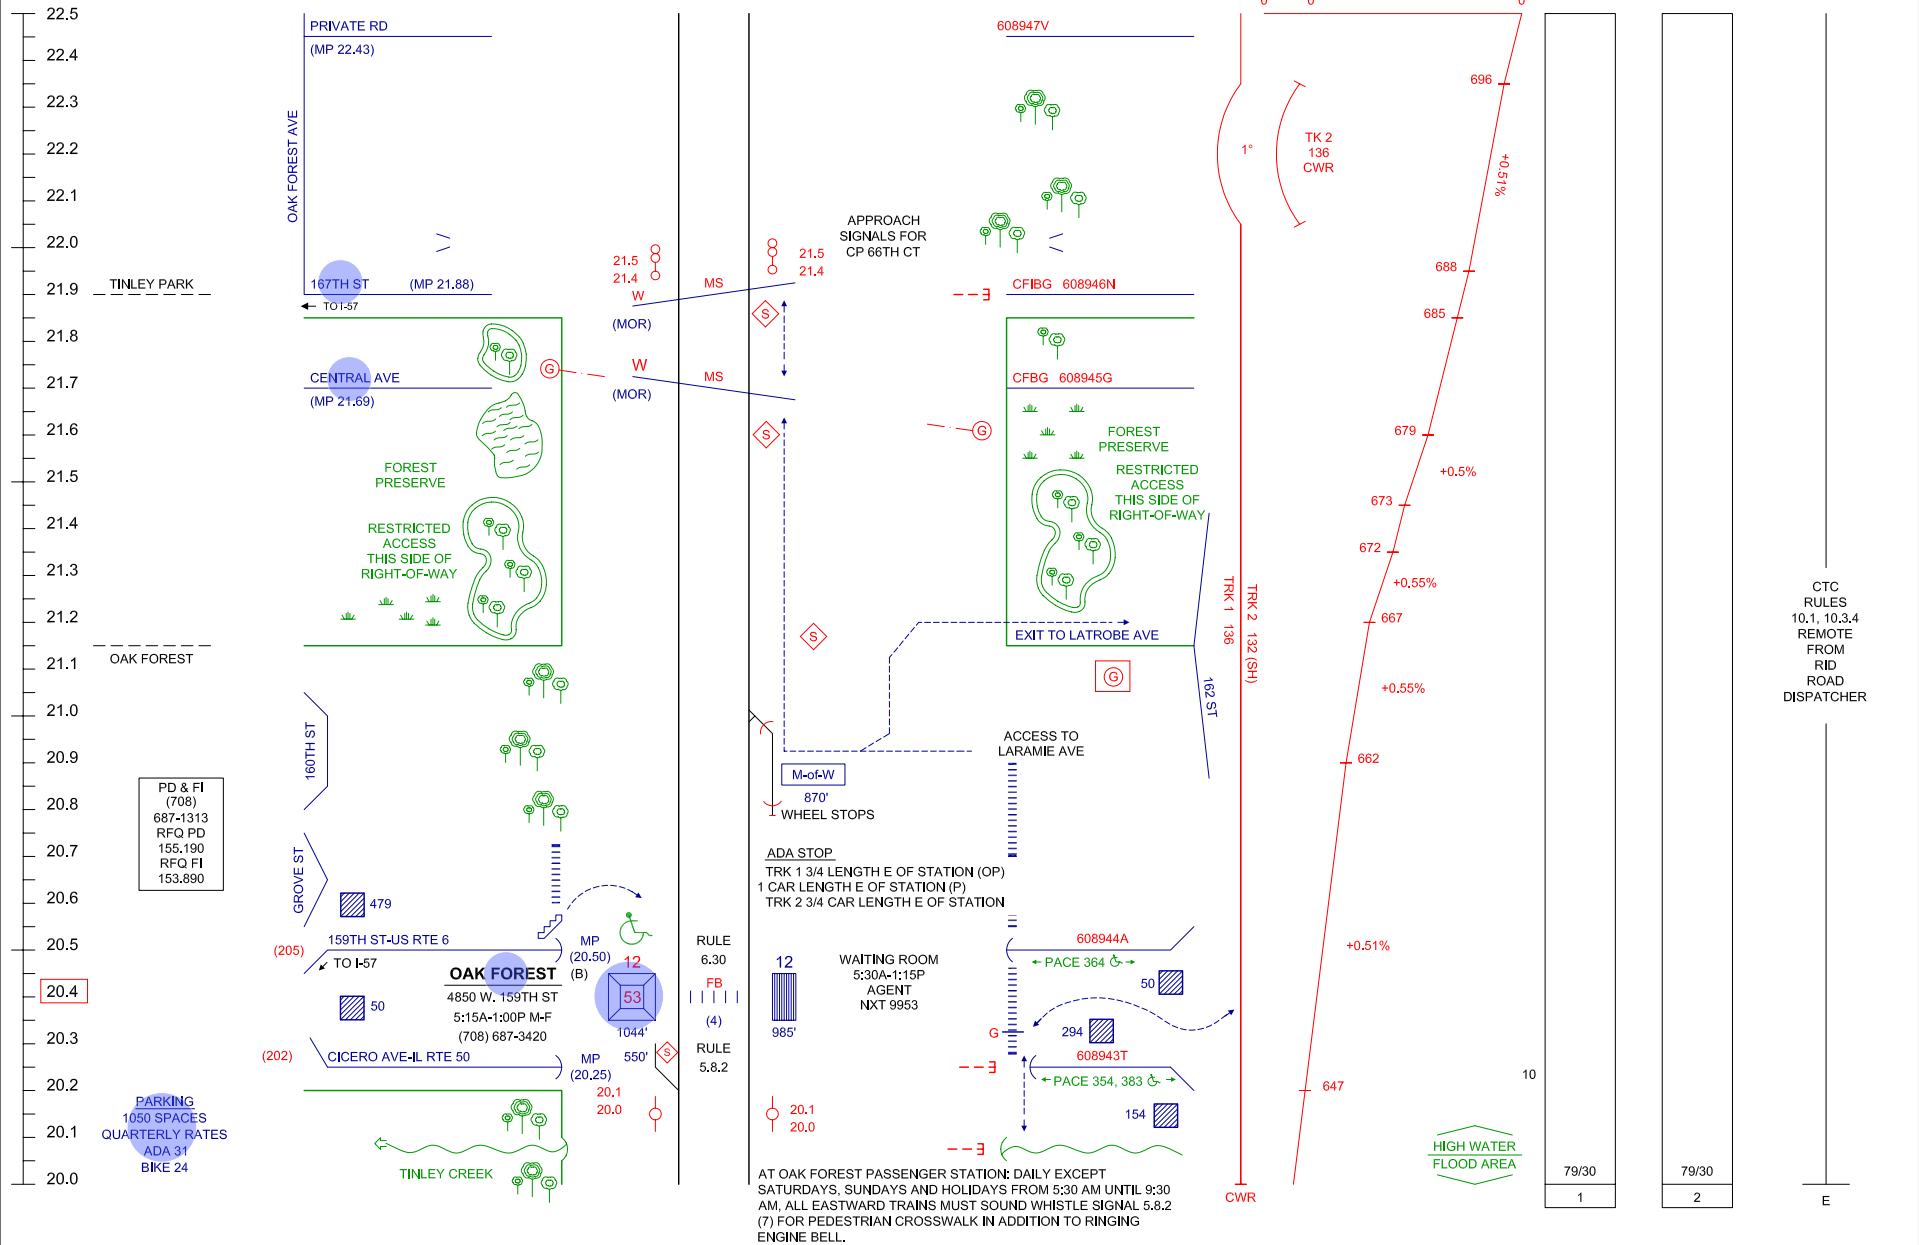

FARE ZONE E


20RID


C	S	L	3348
1	15	37	3425
	19		3426

ROCK ISLAND DISTRICT / JOLIET SUBDISTRICT

REV 7/20/09

P-20

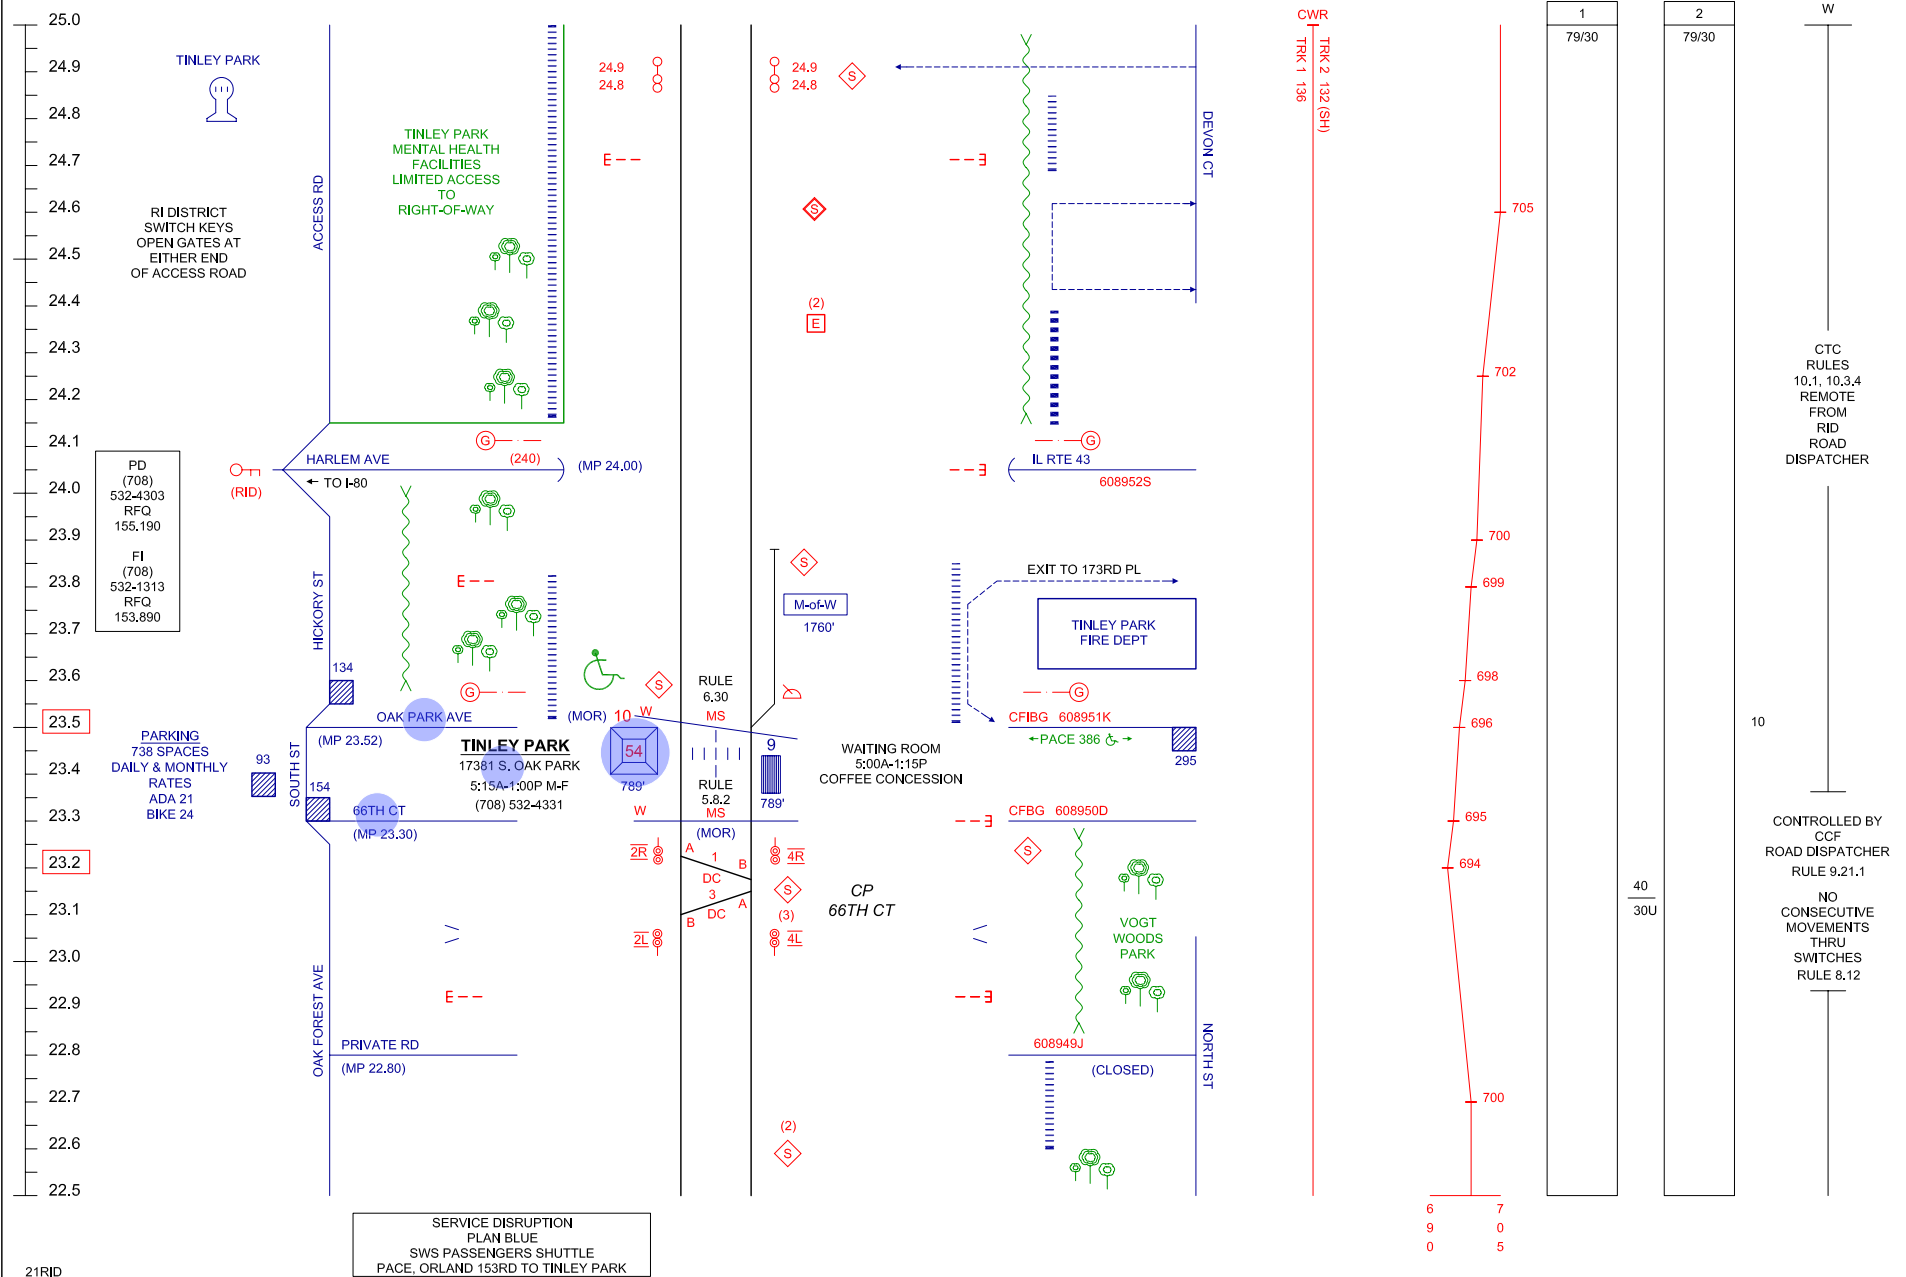

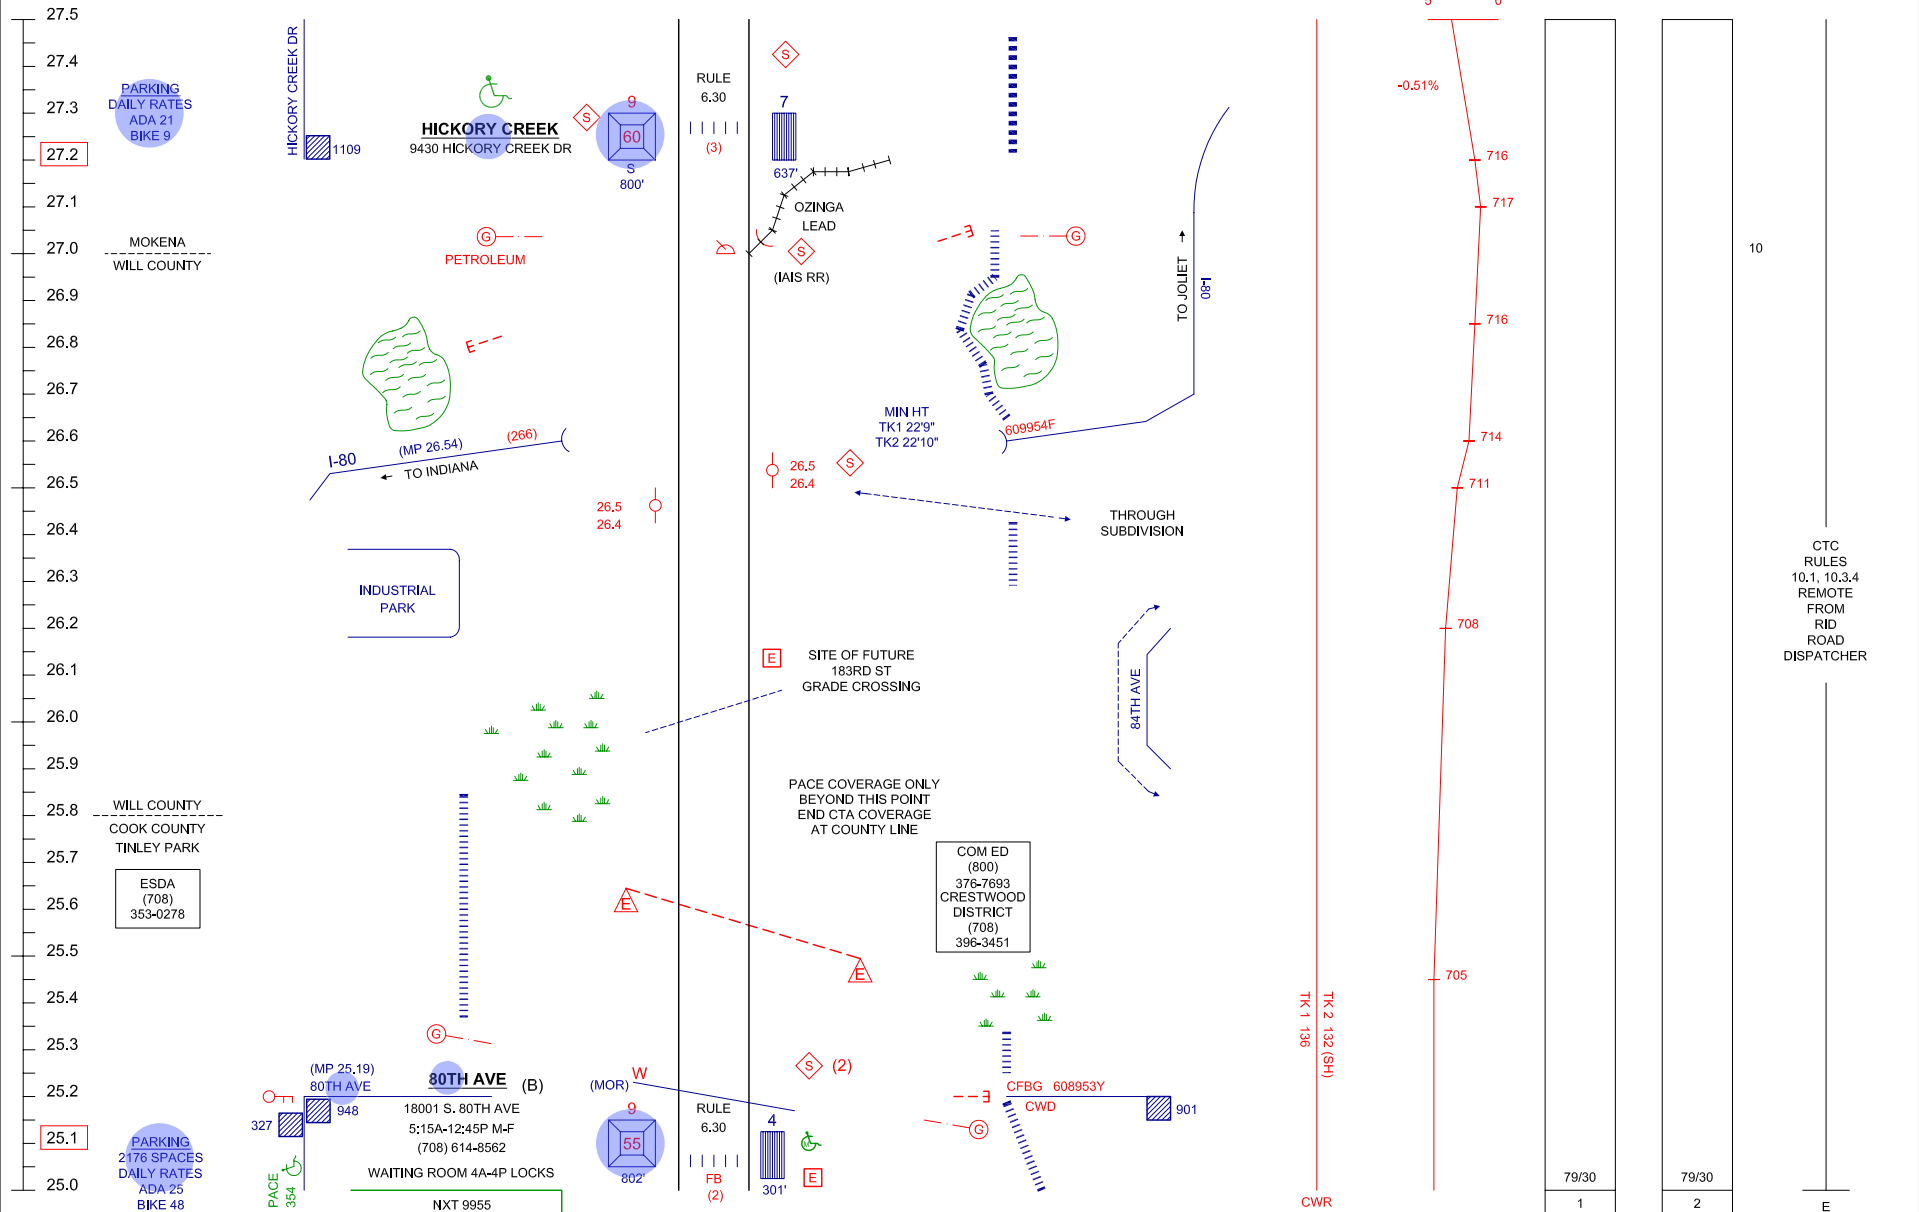

FARE ZONE F


22RID


C S L
13 41 37
81

ROCK ISLAND DISTRICT / JOLIET SUBDISTRICT

REV 7/20/09

P-22

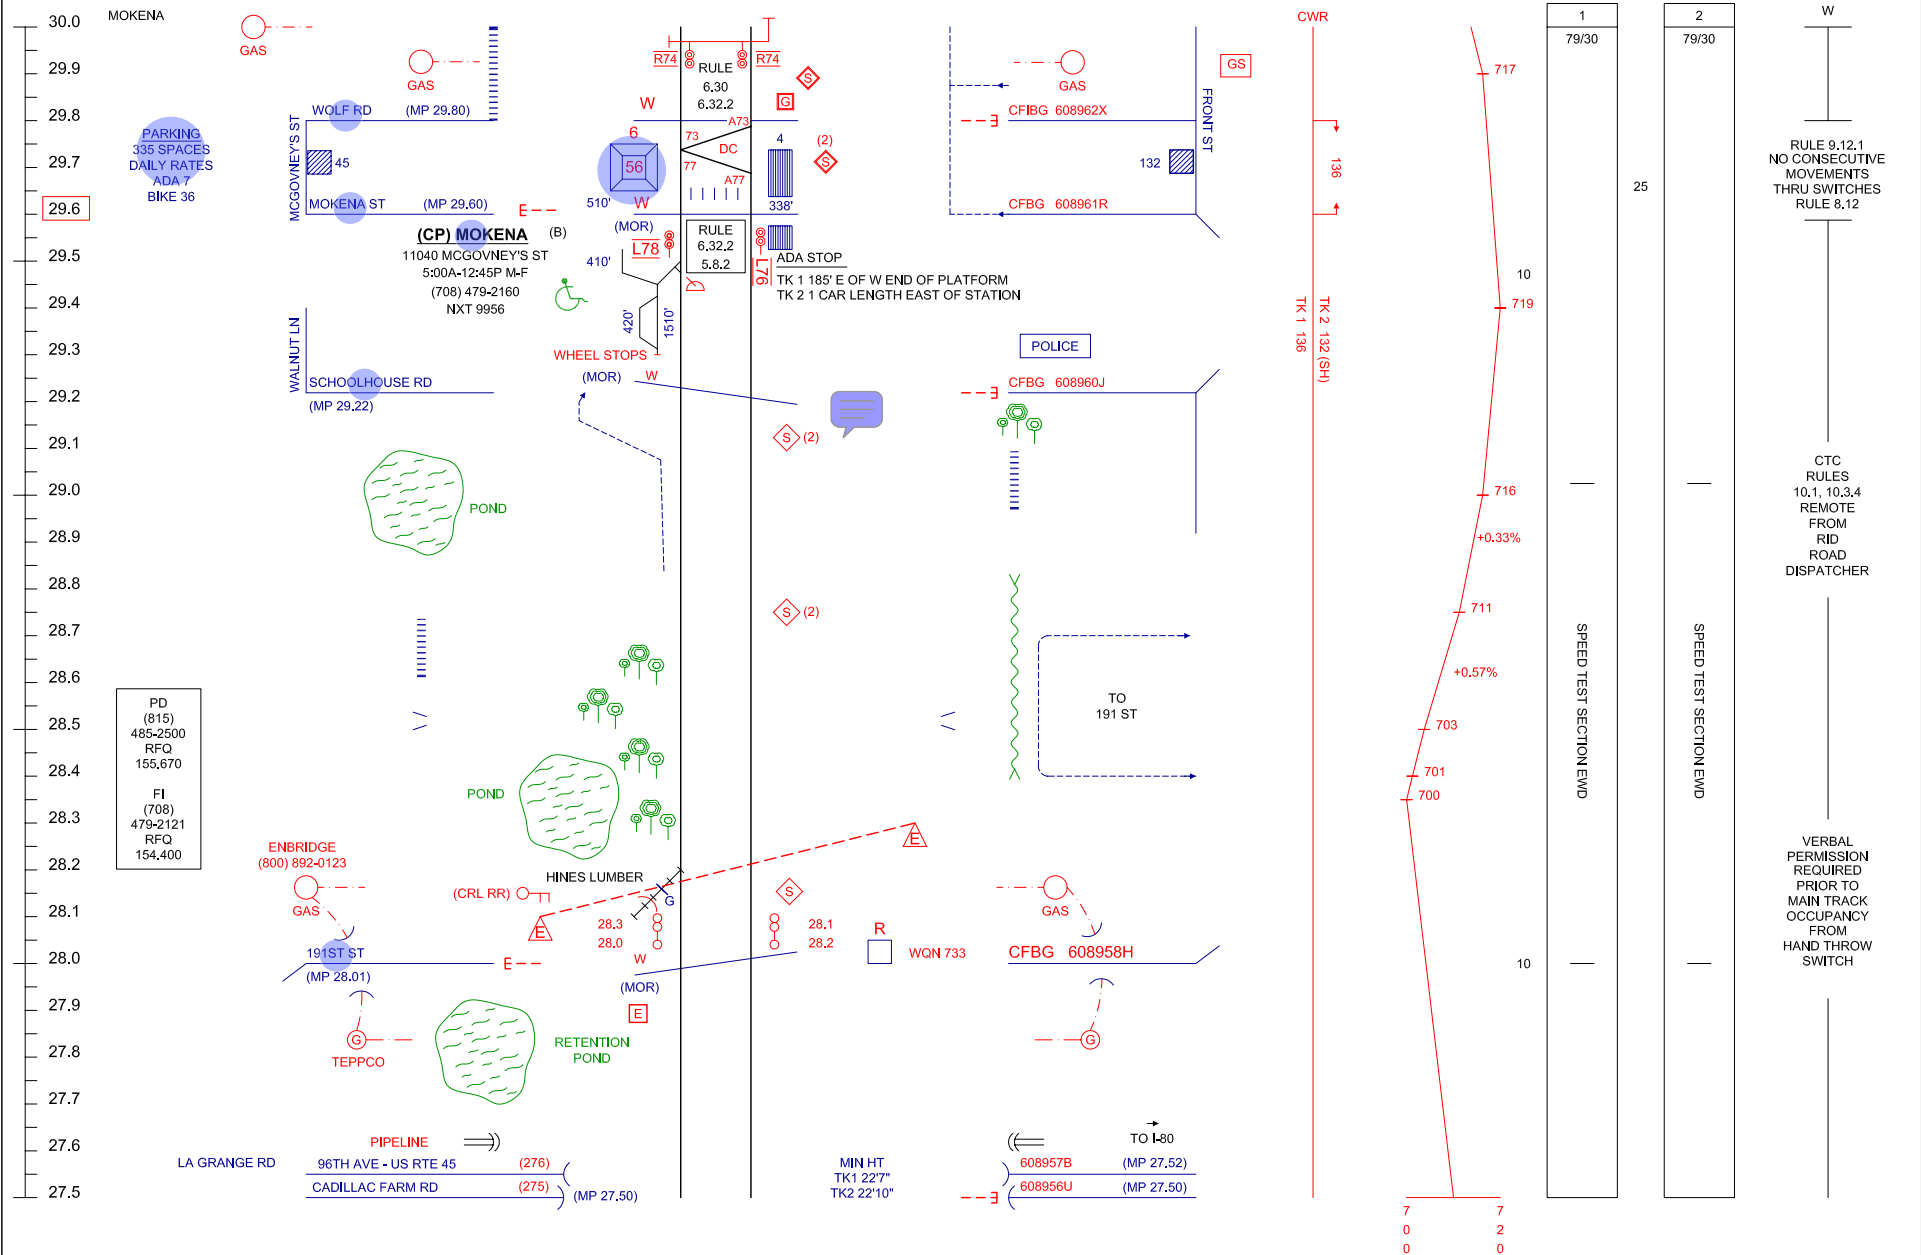

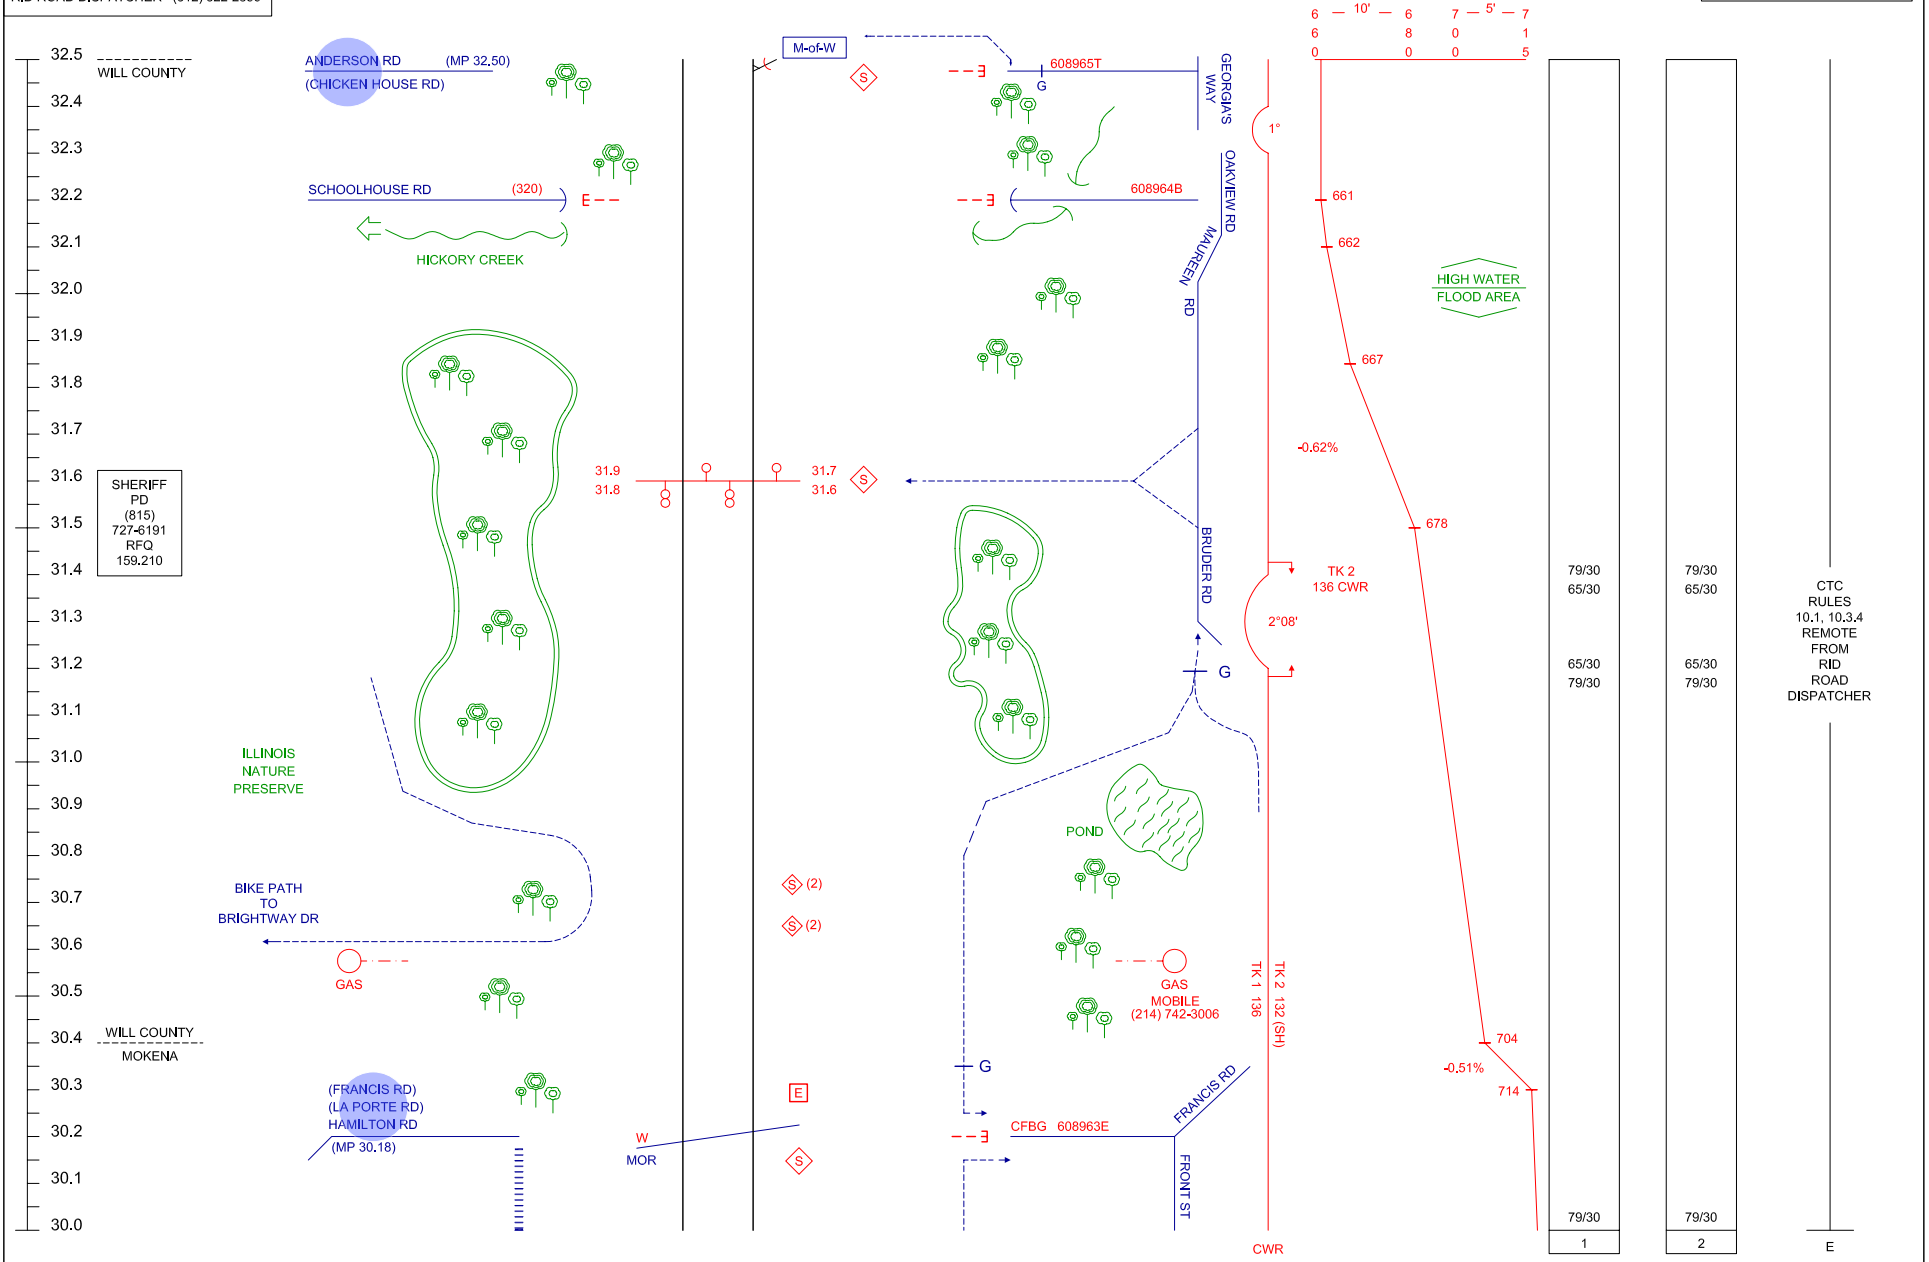

FARE ZONE G

24RID


C S L
11 41 81


3502

ROCK ISLAND DISTRICT / JOLIET SUBDISTRICT

REV 7/20/09


P-24

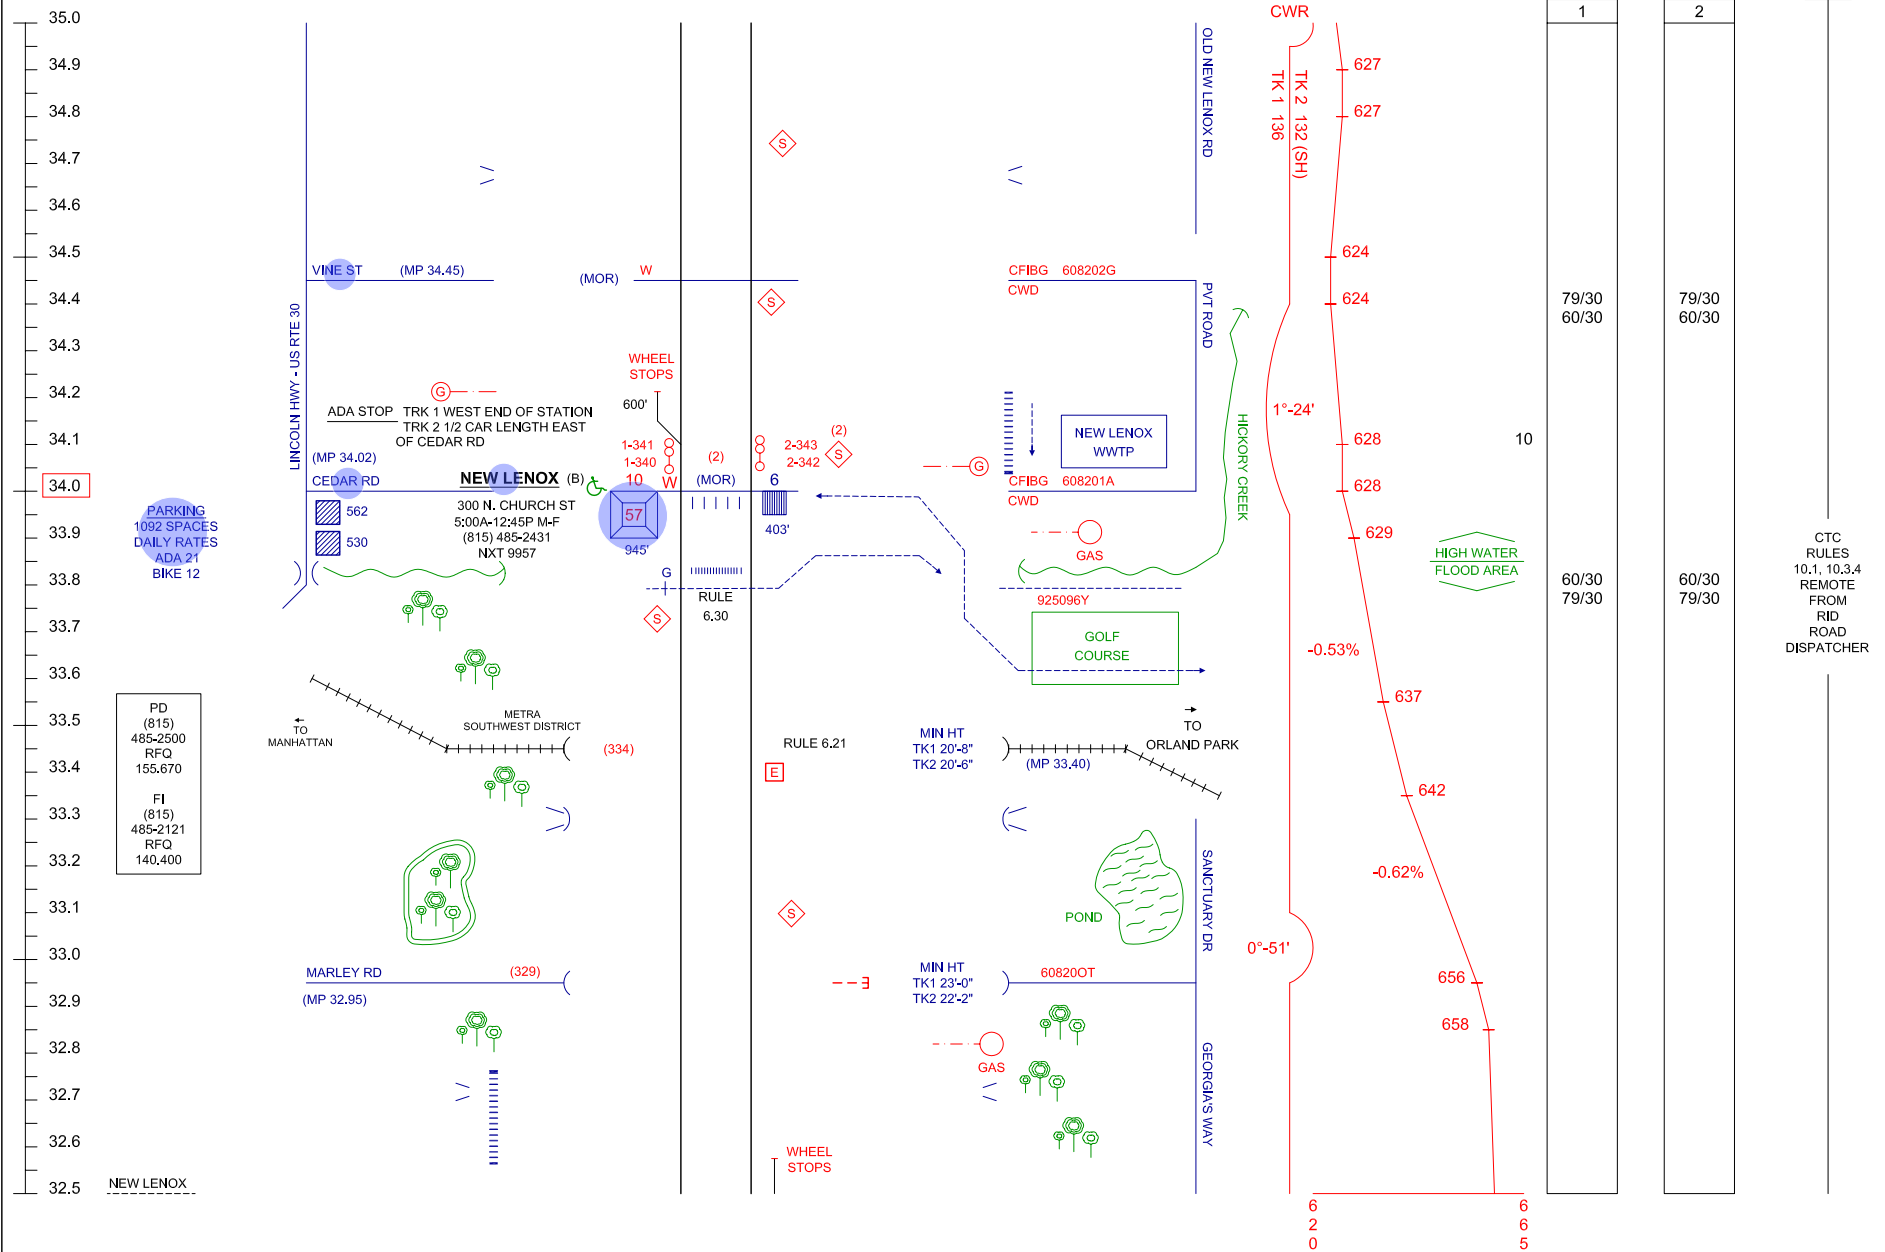

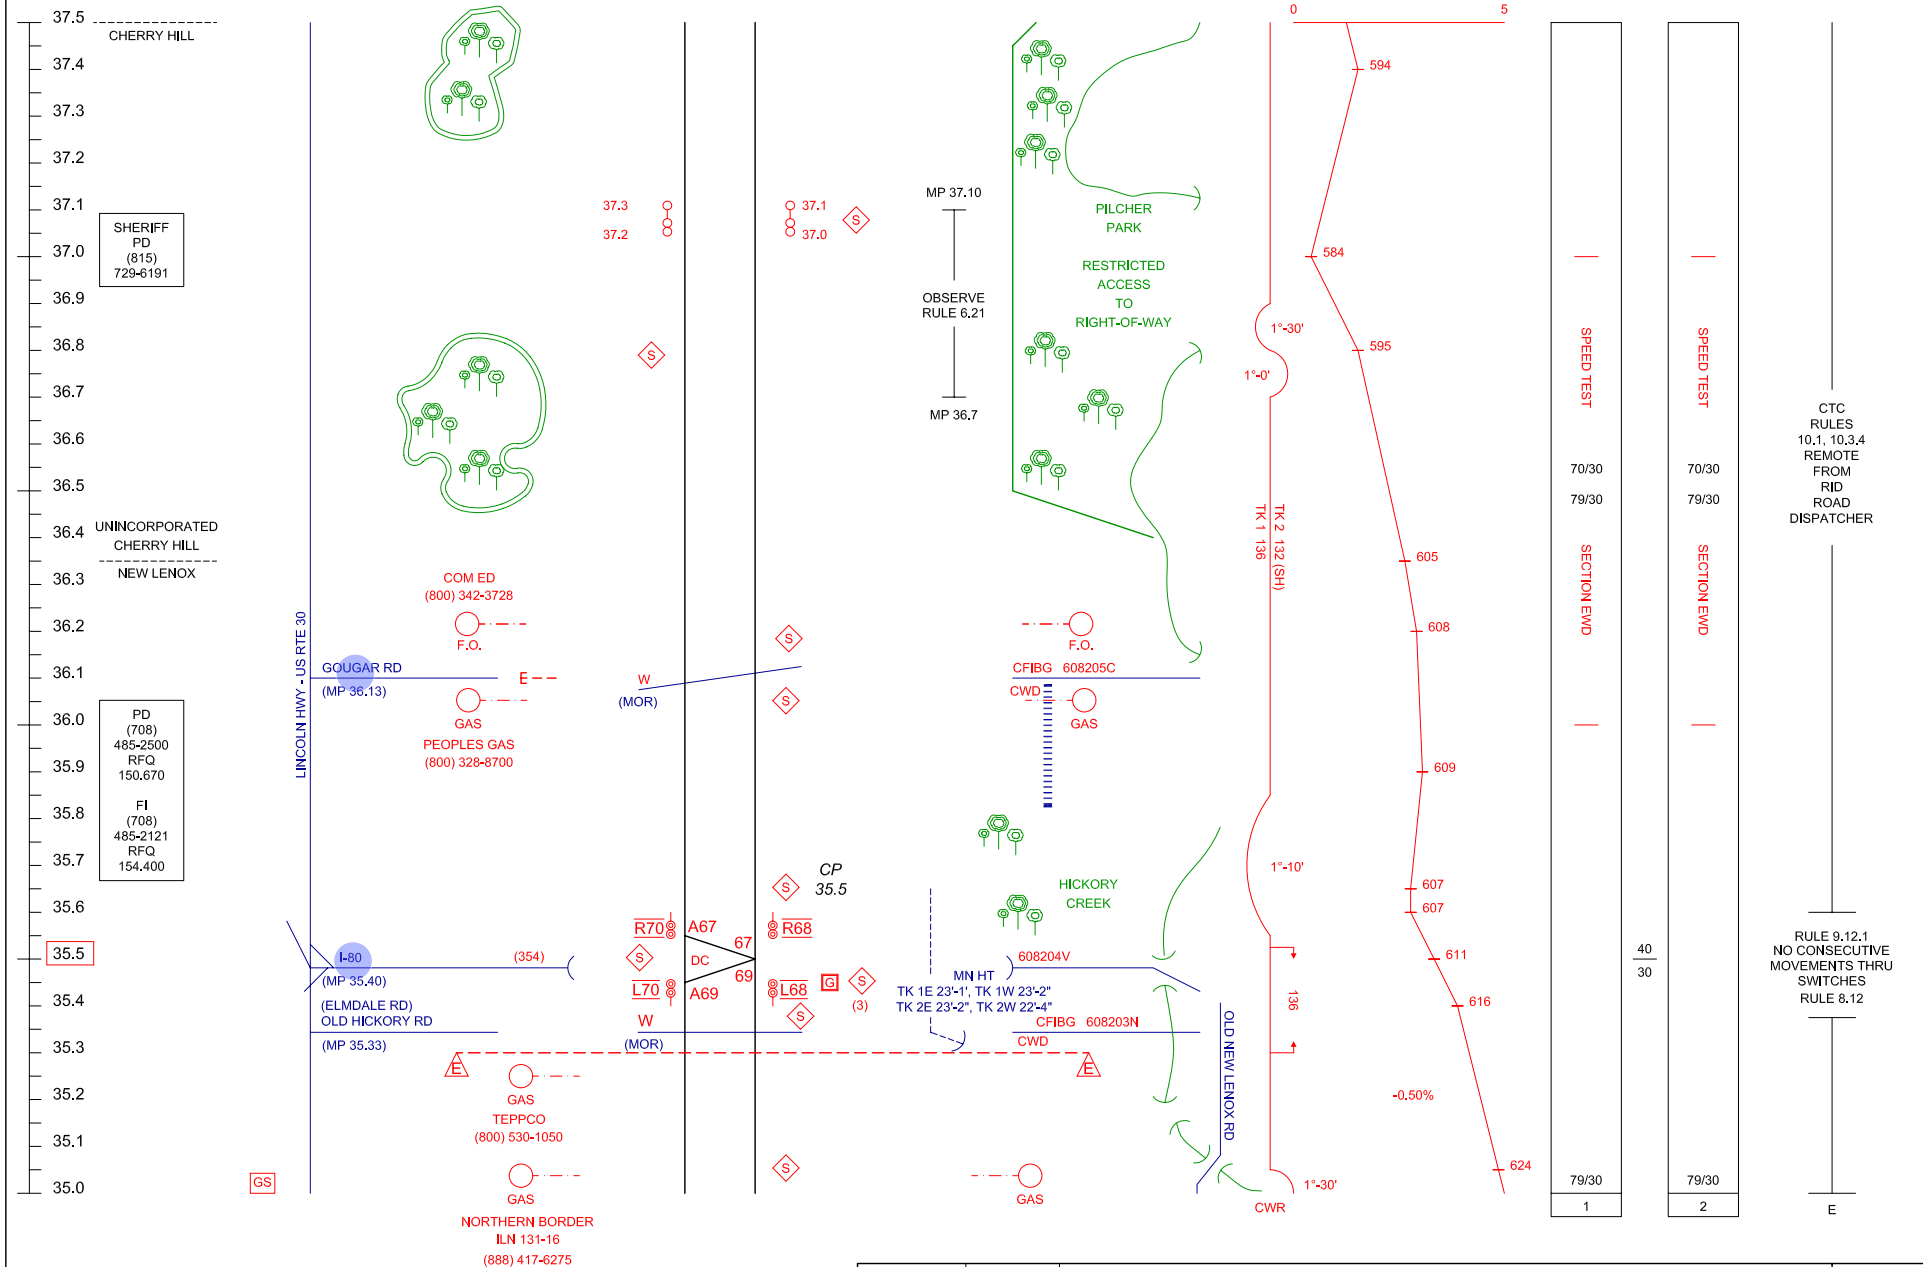

AUTHORIZED HEIGHT FOR LOADS EAST OF
JOLIET IS 18'6"



YARD GATE OPENED

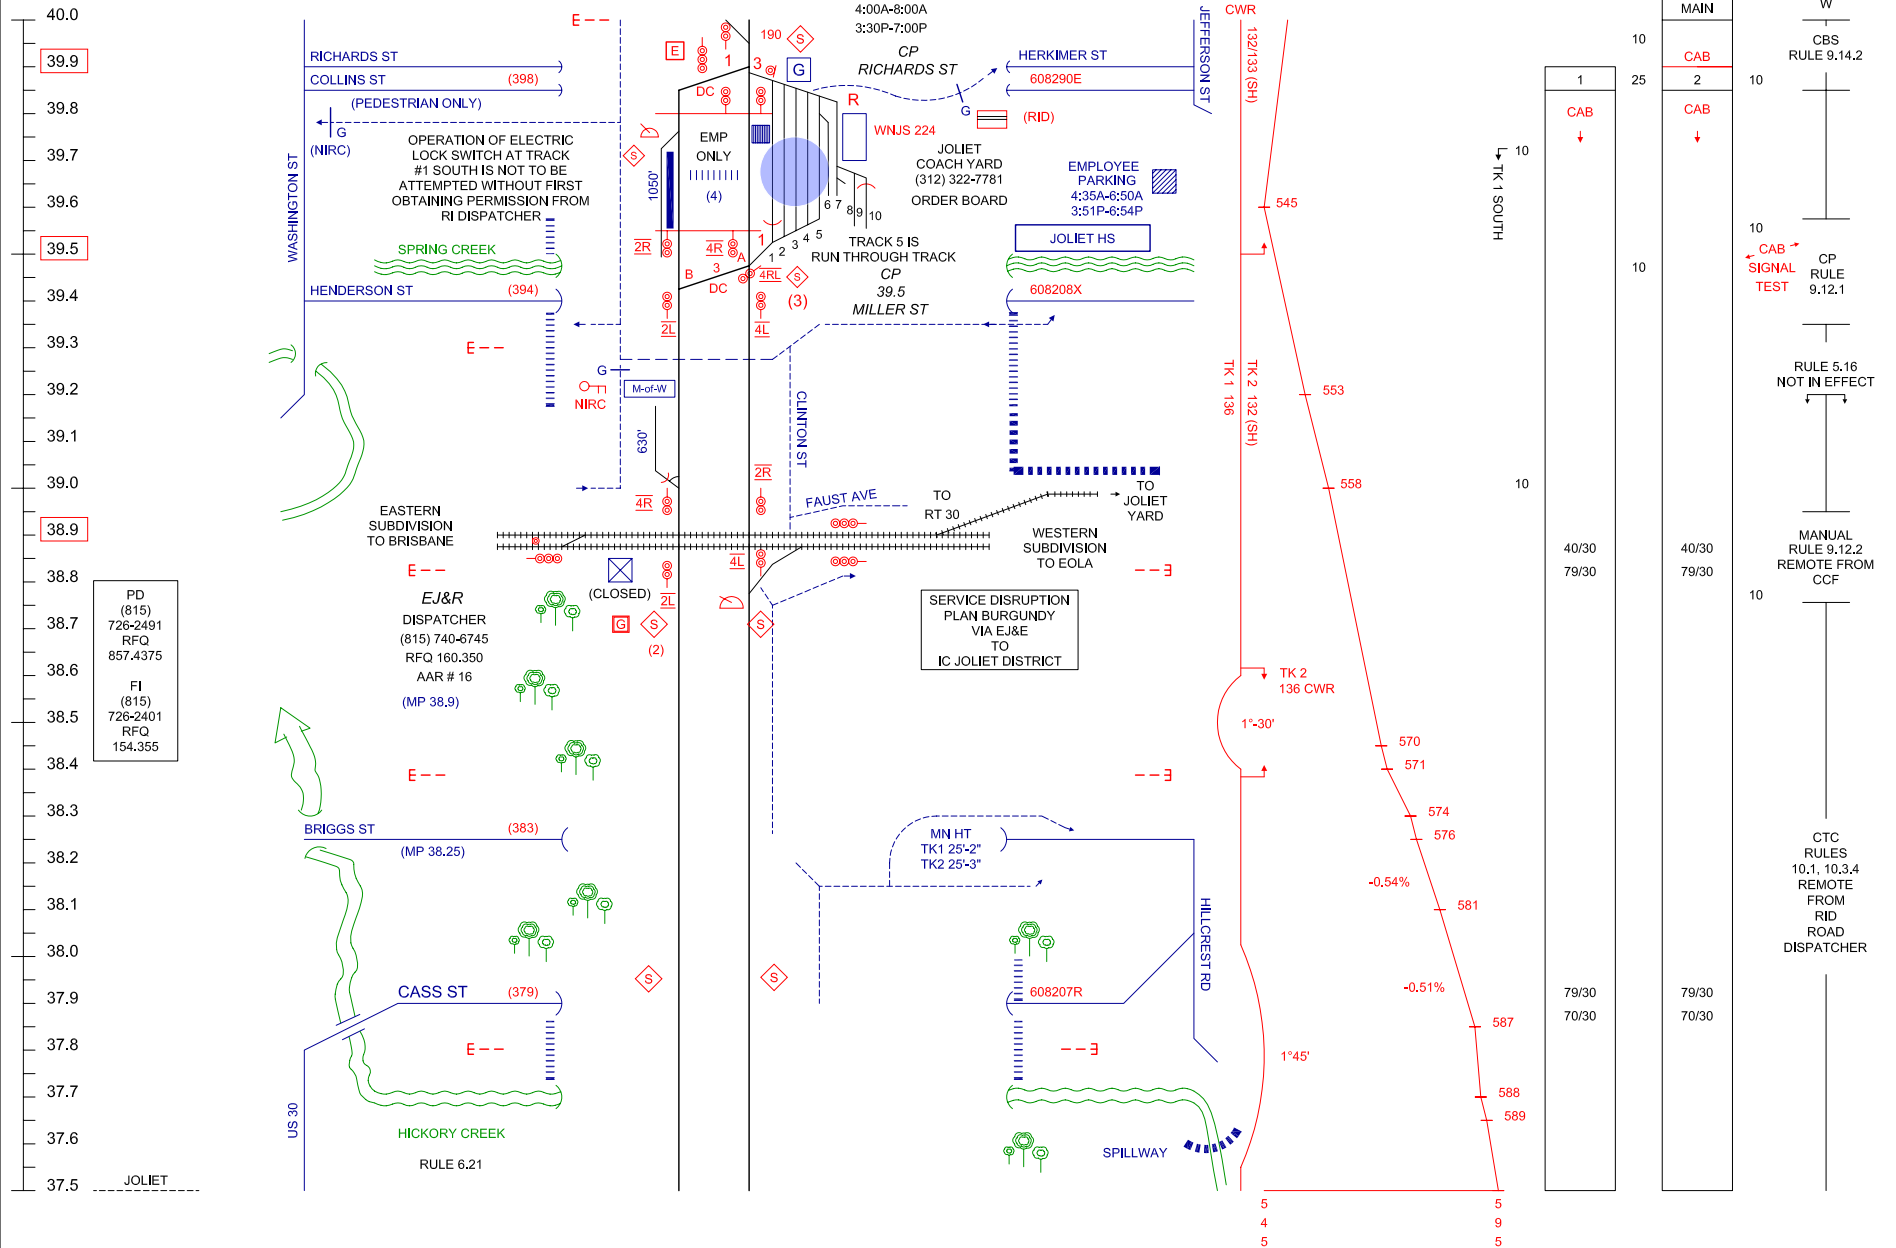

UD TOWER	(312) 322-7779	(815) 726-8751
UP DISPATCHER	(800) 726-1103	RFQ 161.280
BNSF DISPATCHER	(817) 352-2601	RFQ 160.650
CN DISPATCHER	(800) 338-0726	RFQ 160.920
BRIDGE TENDER	(815) 723-8413	

UP DISPATCHER MUST CONTACT UD TOWER TO ADVISE TRAINS HAVE BEEN GIVEN AUTHORITY TO ENTER CN 512B TERRITORY BEFORE DISPLAYING SIGNAL FOR TRAIN MOVING THROUGH UD TO CN JOLIET DISTRICT. INSTRUCTIONS FROM TRAIN CREW NOT TO BE USED AS AUTHORIZATION FOR ROUTING.

ALL WESTBOUND TRAINS ARRIVING AT JOLIET WITH PATRONS USING ADA LIFT MUST FIRST PULL COMPLETELY INTO THE STATION, UNLOAD ALL CARS EAST OF THE ADA CAR AND THEN BACK UP TO UNLOAD AT THE PROPER SPOT. LOAD ADA PASSENGERS 2' PRIOR TO DEPARTURE

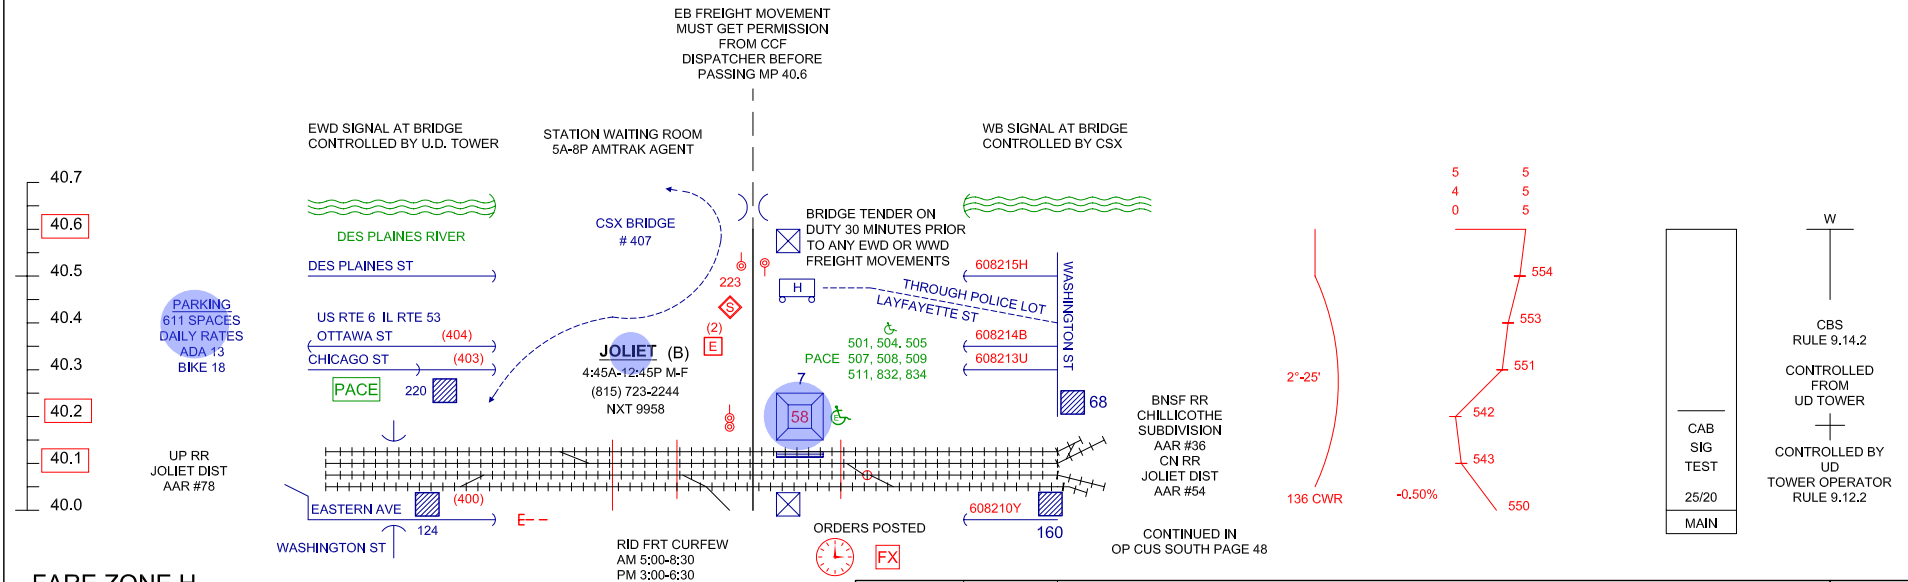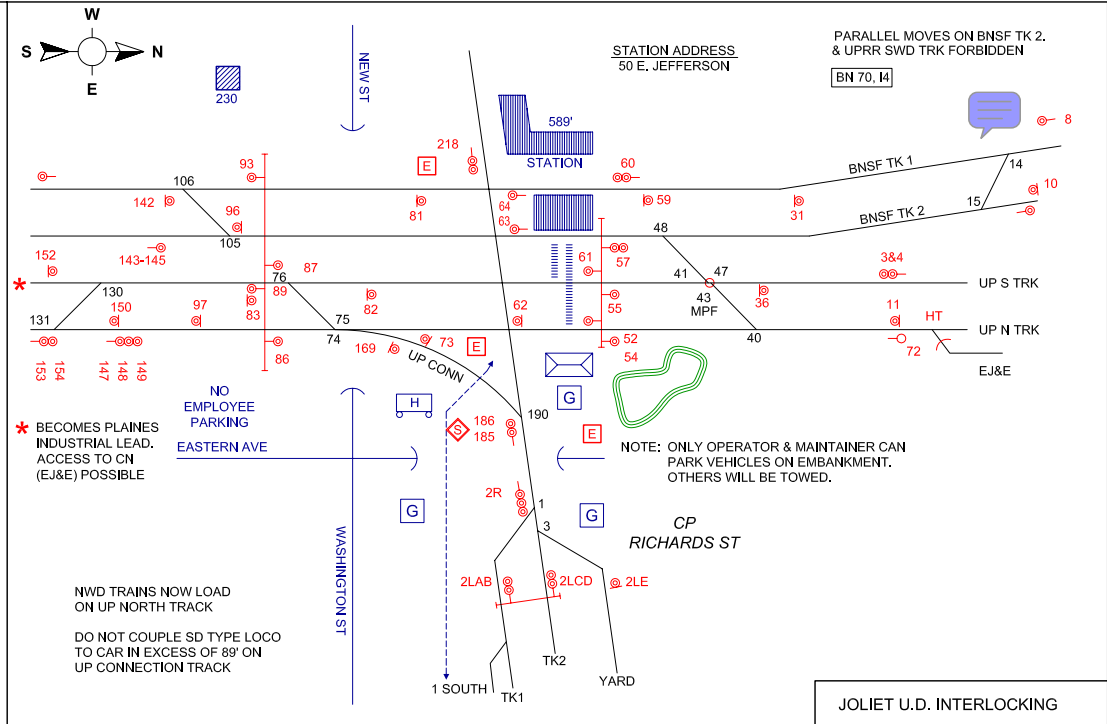

28RID

AERIAL PHOTO

(C)	(S)	(L)	3498
11	43	86	3499

ROCK ISLAND DISTRICT / JOLIET SUBDISTRICT

P-28

REV 7/20/09

AERIAL PHOTO

SERVICE DISRUPTION - PLAN BLUE
SWS PASSENGER SHUTTLE
CTA, WRIGHTWOOD, ASHBURN } 95TH STREET
PACE, OAK LAWN, CHICAGO RIDGE }


C	S	L	W
1	14	27	19 21


3213
3214

ROCK ISLAND DISTRICT / BEVERLY SUBDISTRICT

REV 7/20/09

P-29

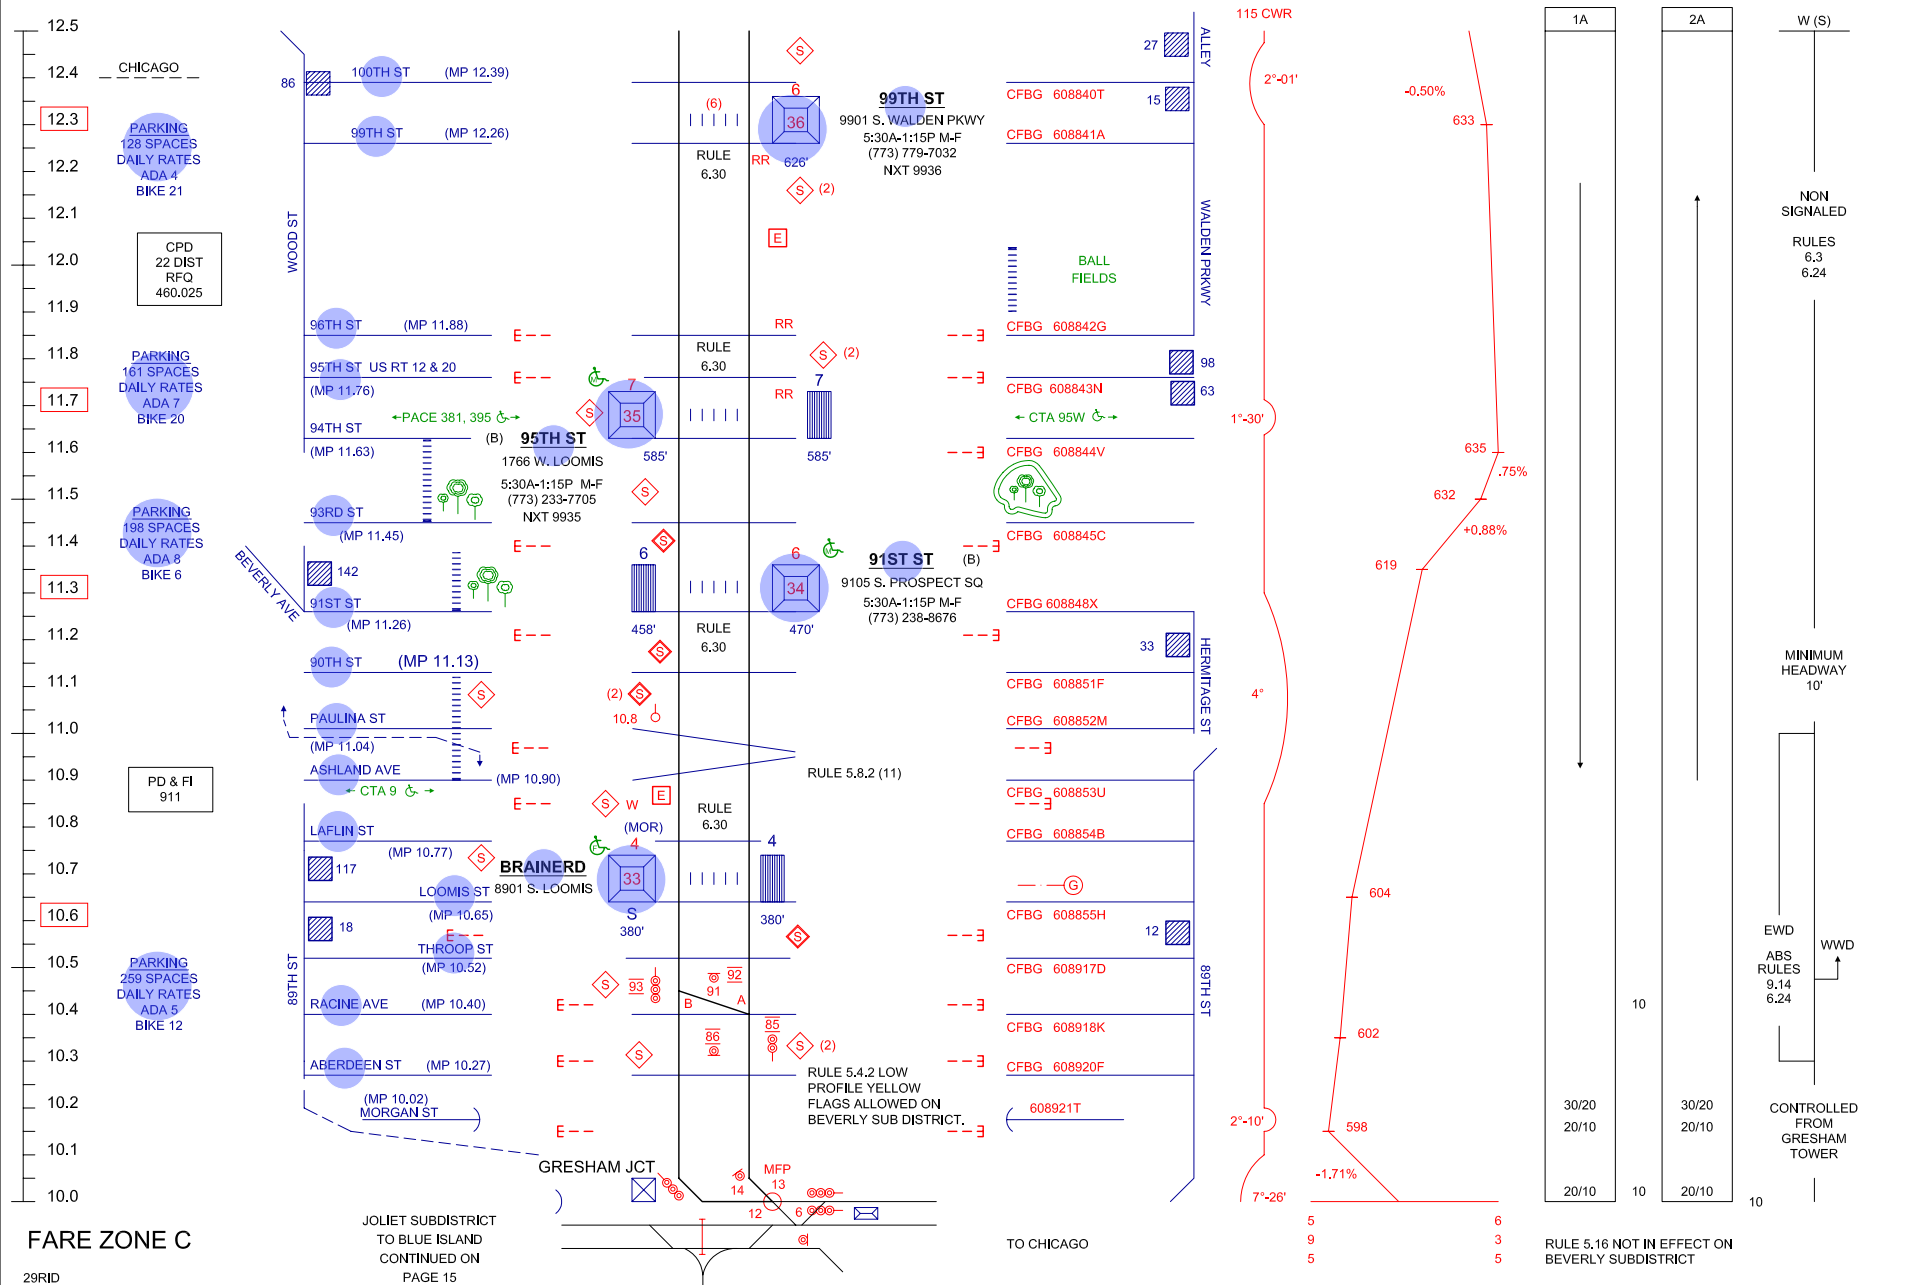

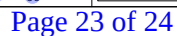

BLUE ISLAND TOWER	(708) 293-6180
MED SOUTH DISPATCHER	(312) 322-2860
TRAINMASTER'S OFFICE	(708) 293-6170
RID ROAD DISPATCHER	(312) 322-2856
RID ROAD MASTER	(708) 293-6171

(C)	(S)	(L)	3227
1	14	28	3349

REV 7/20/09

TRAINS BACKING INTO THE SOUTH END OF BLUE ISLAND YARD, FROM VERMONT STREET, MUST NOT RETURN HAND THROW SWITCH, FROM 1A TO YARD, TO NORMAL POSITION UNTIL THE LAST SET OF TRAILING WHEELS OF LOCOMOTIVE PASS THE YELLOW PAINTED TIE LOCATED IN THE END LEAD APPROXIMATELY 80 FEET EAST OF #1 SWITCH.

RULE 5.4.2 LOW PROFILE YELLOW FLAGS ALLOWED ON BEVERLY SUBDISTRICT.

RULE 5.16 NOT IN EFFECT ON BEVERLY SUBDISTRICT

NOTE: JOLIET SUBDISTRICT TRAINS REROUTED VIA BEVERLY

SUBDISTRICT OPERATE AT RESTRICTED SPEED BETWEEN MP 15.6 & MP 10.5

CLEARANCES RESTRICTIONS 18'6" ATR

NOTE:
DETAIL LAYOUT OF
BLUE ISLAND AREA
ON PAGES 32, 33

CONTINUED IN
MED OPS PRO
PAGE 35

JOLIET
SUBDISTRICT
CONTINUED
ON PAGE 18

