



----- EAST WEST ----->

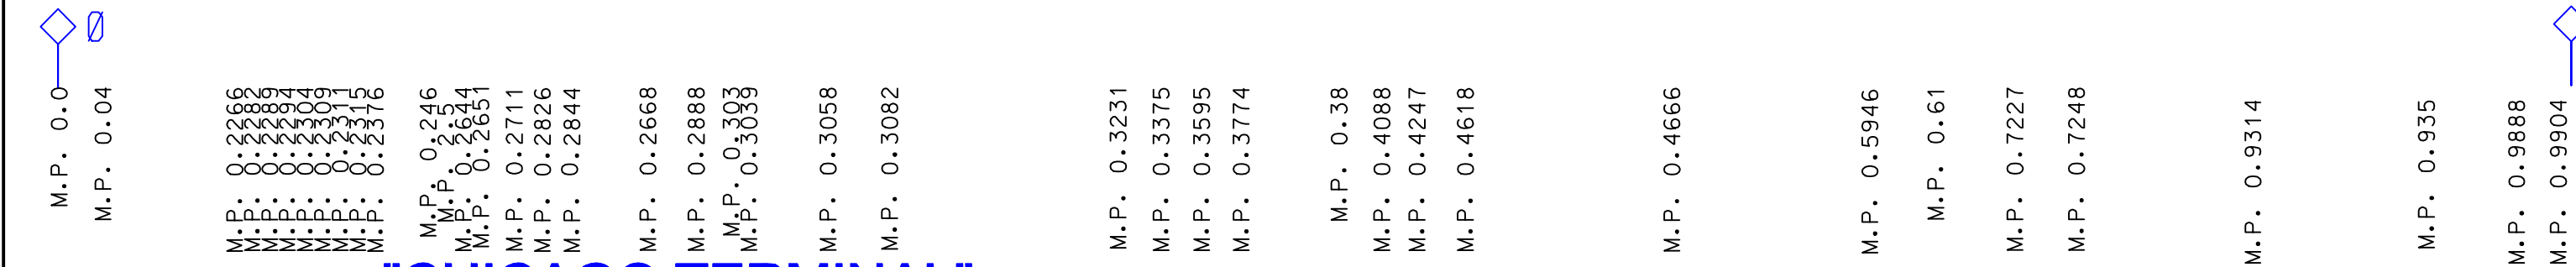

# "CHICAGO TERMINAL" (Chicago Term)

# "16TH ST"

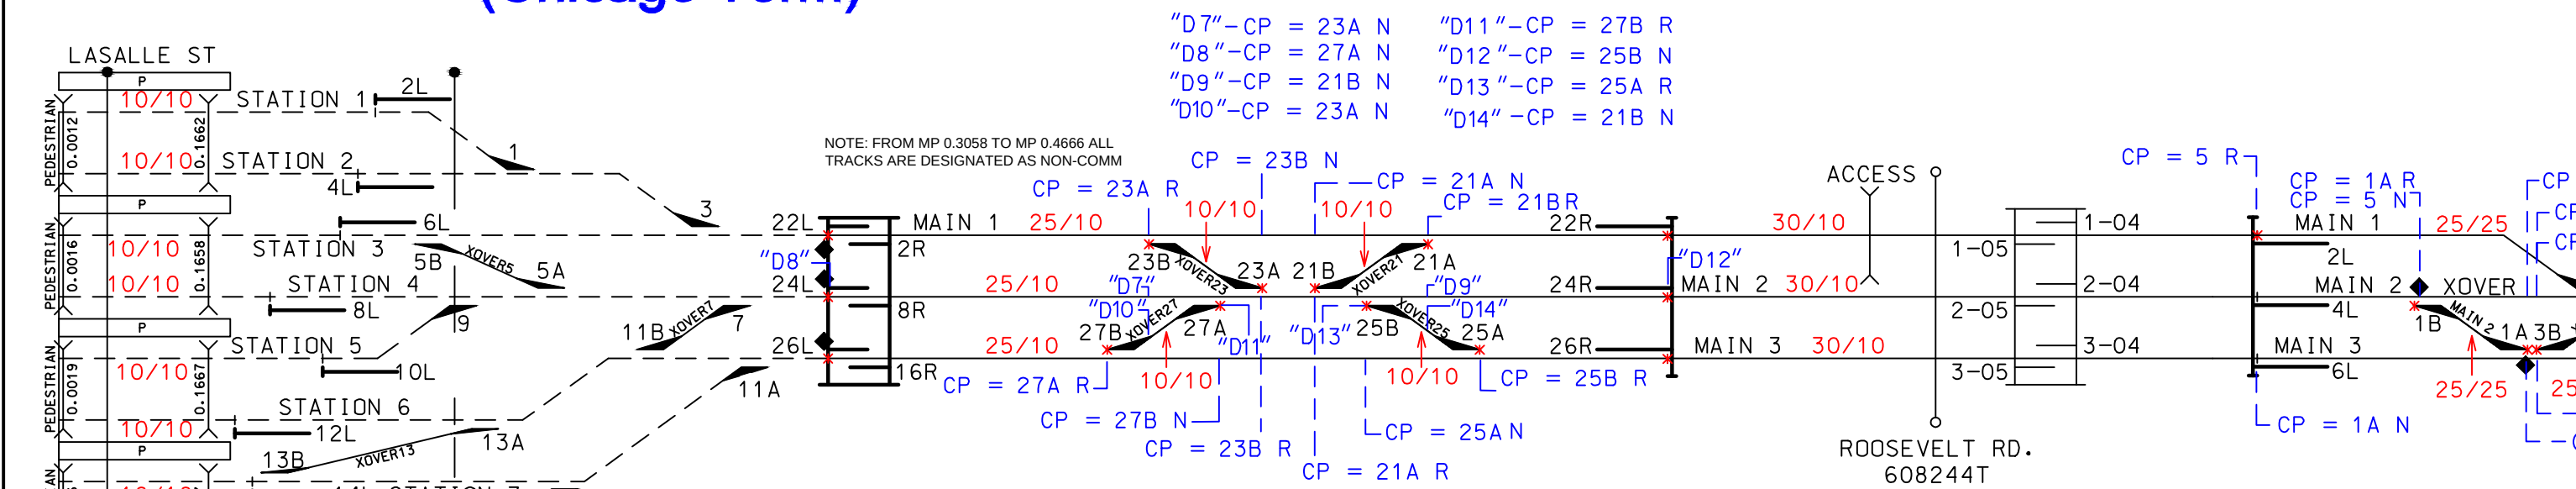

NOTE: FROM MP 0.3058 TO MP 0.4666 ALL TRACKS ARE DESIGNATED AS NON-COMM

**LEGEND:**

**CROSSINGS:**

- OVERHEAD
- AT GRADE
- UNDERPASS

**SWITCHES:**

- HANDTHROW
- SPRING
- ELECTRIC LOCK
- POWER

**LINESTYLES:**

- PTC
- PTC ENTRY
- NON PTC
- FOREIGN RR
- YARD TRACK
- Metra Subdiv/Metra Maintained
- Metra Subdiv/Not Metra Maintained
- Not In Metra Subdiv/Metra Maintained
- Not In Metra Subdiv

**SIGNALS:**

- ABSOLUTE
- AUTOMATIC
- DWARF
- VIRTUAL

**WIRELESS APPROACH CIRCUIT**

- SUBDIVISION CHANGE POINT
- TRACK NAME CHANGE
- DERAIL
- FUTURE PERMANENT DERAIL
- ADVANCE WARNING
- RESUME SPEED

**NOTE:**

1. PSS = PASSENGER
2. FR = FREIGHT
3. CP = CLEARANCE POINT
4. MAXIMUM SPEEDS PER METRA TIME TABLE ARE SHOWN IN (GREEN).
5. SPEED RESTRICTIONS ARE SHOWN IN RED.
6. \* = INDICATES SPEED CHANGE
7. SPEEDS SHOWN PSS/FR
8. CROSSING MILEPOSTS ARE THE BEGINNING MILEPOSTS ON THE MAIN TRACK.
9. "D#" = INDICATES CLEARANCE POINT DETAIL

| REV. | DATE     | BY | DESCRIPTION                                                    | REV. | DATE     | BY | DESCRIPTION                                                     | DISCLOSURE:<br>CHARTS ARE A VISUAL REPRESENTATION OF THE SUBDIV AND ARE TO BE USED FOR PTC SUBDIV PURPOSES ONLY | <br>547 W. JACKSON BLVD.<br>CHICAGO, IL. 60661 | METRA SUBDIV FILE<br>MASTER DRAWING<br>JOLIET SUB<br>ILLINOIS<br>MP 0.0 -1.0 | SHEET NO. 1 |
|------|----------|----|----------------------------------------------------------------|------|----------|----|-----------------------------------------------------------------|---|---|------------------------------------------------------------------------------|-------------|
| 29   | 10/05/22 | JA | REVISED PER CHANGES TO CP WESTERN, INTERCHANGE AND ROBBINS     | 34   | 09/17/24 | JE | REVISED PER 16TH ST DIAMOND REPLACEMENT                         |   |   |                                                                              |             |
| 30   | 12/21/22 | JE | REVISED PER CHANGES TO SPEED OF XOVER 115 AT WESTERN           | 35   | 11/11/24 | JE | REVISED PER SPEED CHANGE TO 10 MPH ACROSS UD TOWER DIAMONDS     |   |   |                                                                              |             |
| 31   | 05/05/23 | JA | REVISED NONCOMM TRACK AT CHI TERM & SPEED AT WESTERN 115 XOVER | 36   | 01/08/25 | JE | REVISED PER AUDIT RUN CHANGES, CRs for PEDs and PLATFORMS       |   |   |                                                                              |             |
| 32   | 01/08/24 | JE | REVISED PER CF AUDIT CHANGES AT 80TH AVE AND 105TH ST          | 37   | 02/04/25 | ES | REVISED TO UPDATE SWITCHES TO ELECTRIC LOCK                     |   |   |                                                                              |             |
| 33   | 01/08/24 | JA | REVISED PER REMOVAL OF CON1SCAL TRACK AT 16TH ST               | 38   | 02/06/25 | JE | REVISED TO UPDATE FREIGHT SPEEDS TO 40MPH BETWEEN ROBBINS & EJA |   |   |                                                                              |             |

<----- EAST

WEST ----->

M.P. 0.9314

M.P. 0.935

M.P. 0.9888

M.P. 0.9904

M.P. 1.0109

M.P. 1.043

M.P. 1.0474

M.P. 1.0525

M.P. 1.1872

M.P. 1.2404

M.P. 1.2467

M.P. 1.2484

M.P. 1.26

M.P. 1.32

M.P. 1.47

M.P. 1.60


M.P. 1.7014

M.P. 1.7018

M.P. 1.74


M.P. 2.02

"16TH STREET INTERLOCKING"  
(16th)

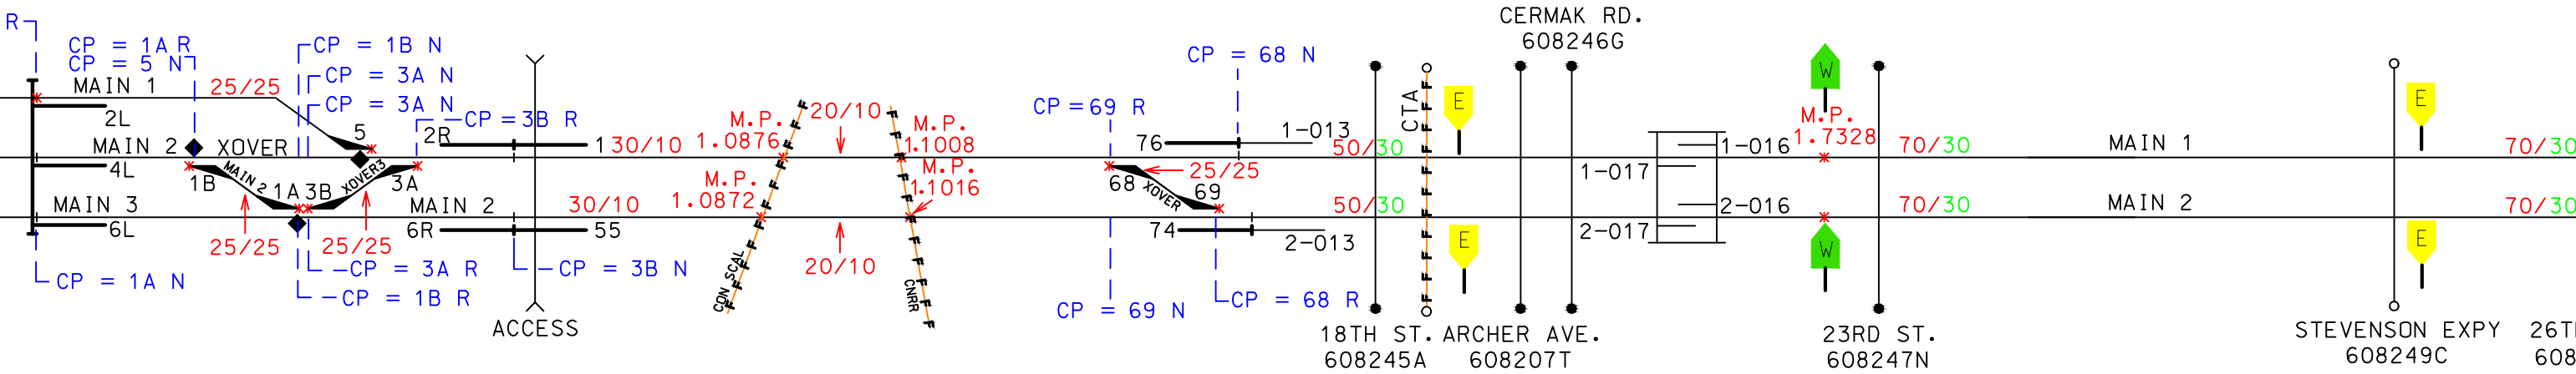

<----- EAST

WEST ----->

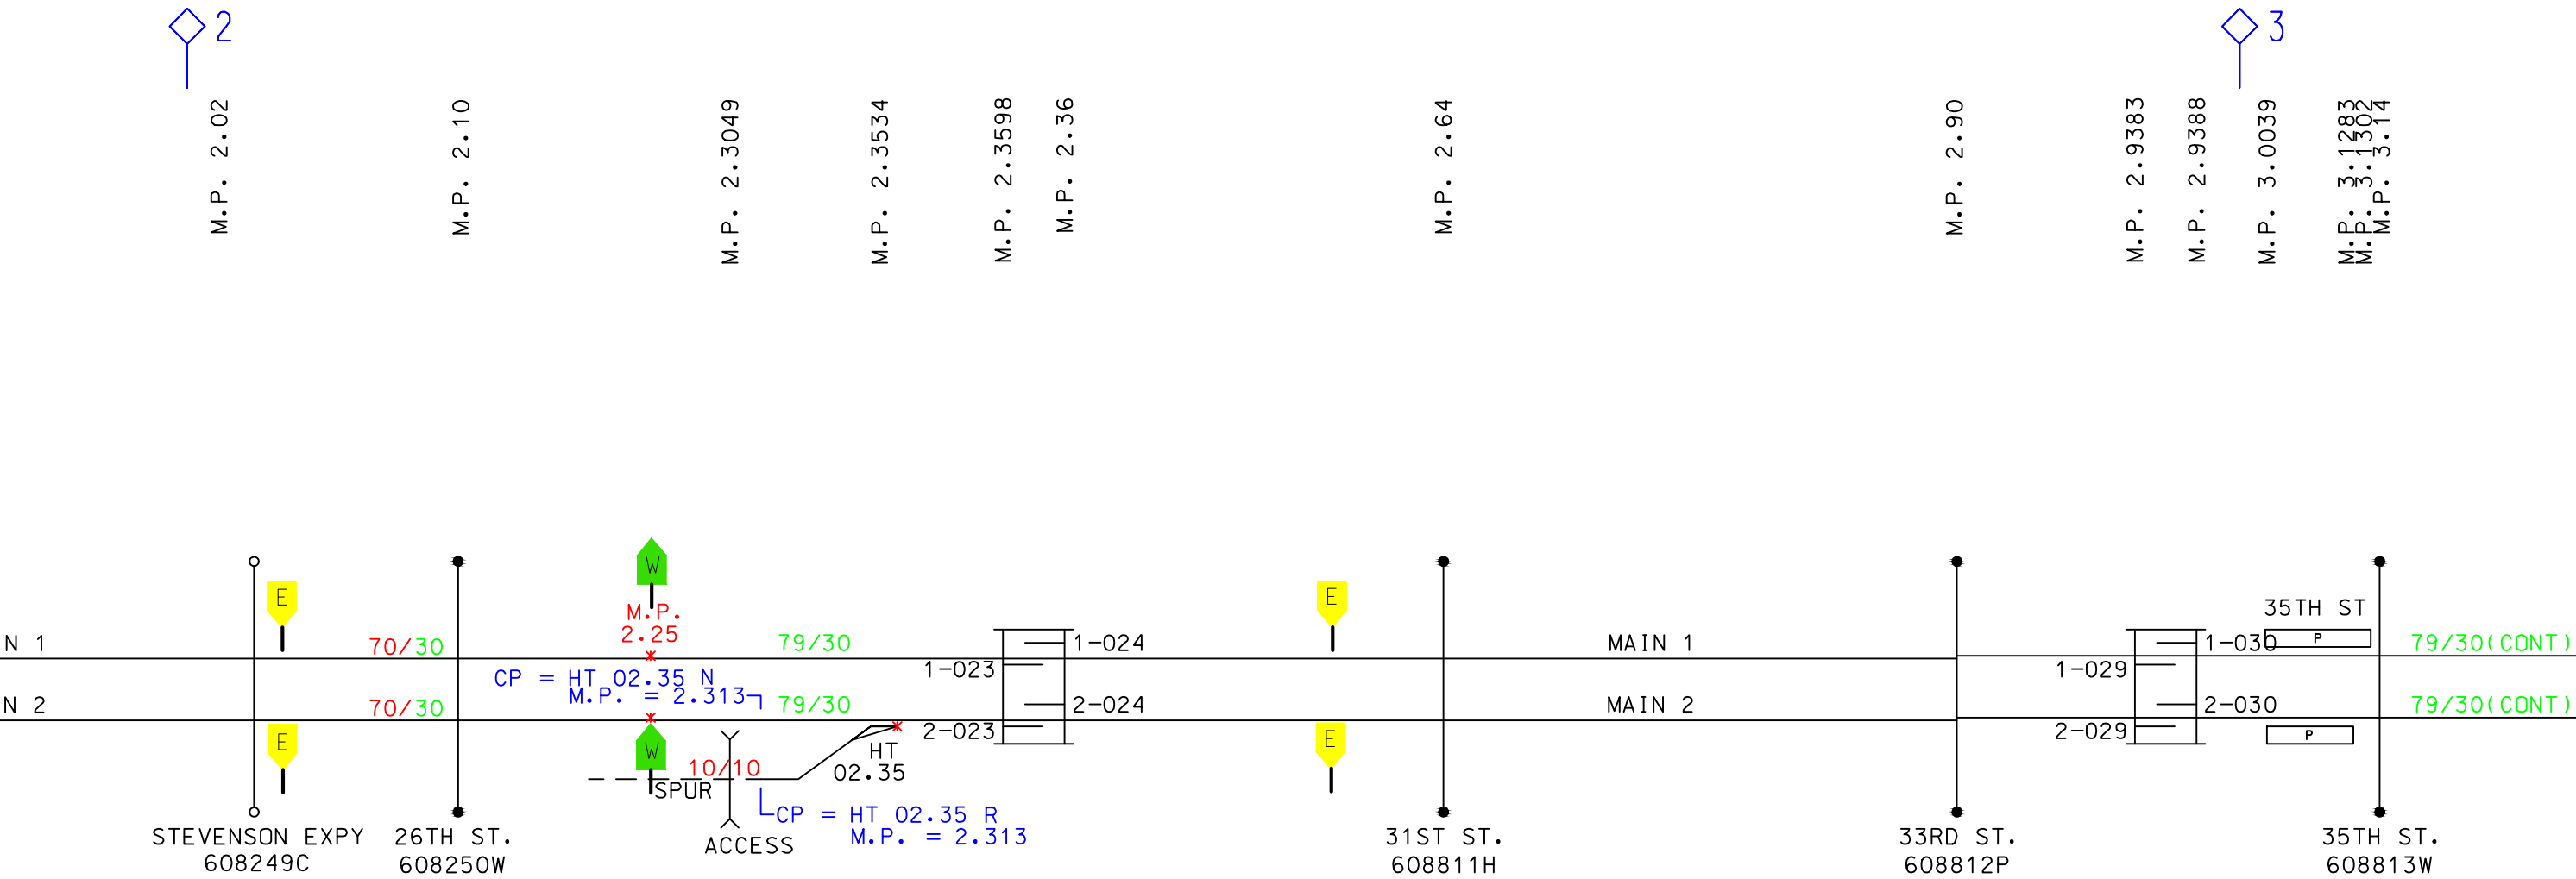

| REV. | DATE     | BY | DESCRIPTION                                                    | REV. | DATE     | BY | DESCRIPTION                                                     |
|------|----------|----|----------------------------------------------------------------|------|----------|----|-----------------------------------------------------------------|
| 29   | 10/05/22 | JA | REVISED PER CHANGES TO CP WESTERN, INTERCHANGE AND ROBBINS     | 34   | 09/17/24 | JE | REVISED PER 16TH ST DIAMOND REPLACEMENT                         |
| 30   | 12/21/22 | JE | REVISED PER CHANGES TO SPEED OF XOVER 115 AT WESTERN           | 35   | 11/11/24 | JE | REVISED PER SPEED CHANGE TO 10 MPH ACROSS UD TOWER DIAMONDS     |
| 31   | 05/05/23 | JA | REVISED NONCOMM TRACK AT CHI TERM & SPEED AT WESTERN 115 XOVER | 36   | 01/08/25 | JE | REVISED PER AUDIT RUN CHANGES, CRs for PEDs and PLATFORMS       |
| 32   | 01/08/24 | JE | REVISED PER CF AUDIT CHANGES AT 80TH AVE AND 105TH ST          | 37   | 02/04/25 | ES | REVISED TO UPDATE SWITCHES TO ELECTRIC LOCK                     |
| 33   | 01/08/24 | JA | REVISED PER REMOVAL OF CON1SCAL TRACK AT 16TH ST               | 38   | 02/06/25 | JE | REVISED TO UPDATE FREIGHT SPEEDS TO 40MPH BETWEEN ROBBINS & EJA |



DISCLOSURE:  
CHARTS ARE A VISUAL REPRESENTATION OF  
THE SUBDIV AND ARE TO BE USED FOR PTC  
SUBDIV PURPOSES ONLY




METRA SUBDIV FILE  
MASTER DRAWING  
JOLIET SUB  
ILLINOIS  
MP 2.0 - 3.0

<----- EAST

WEST ----->

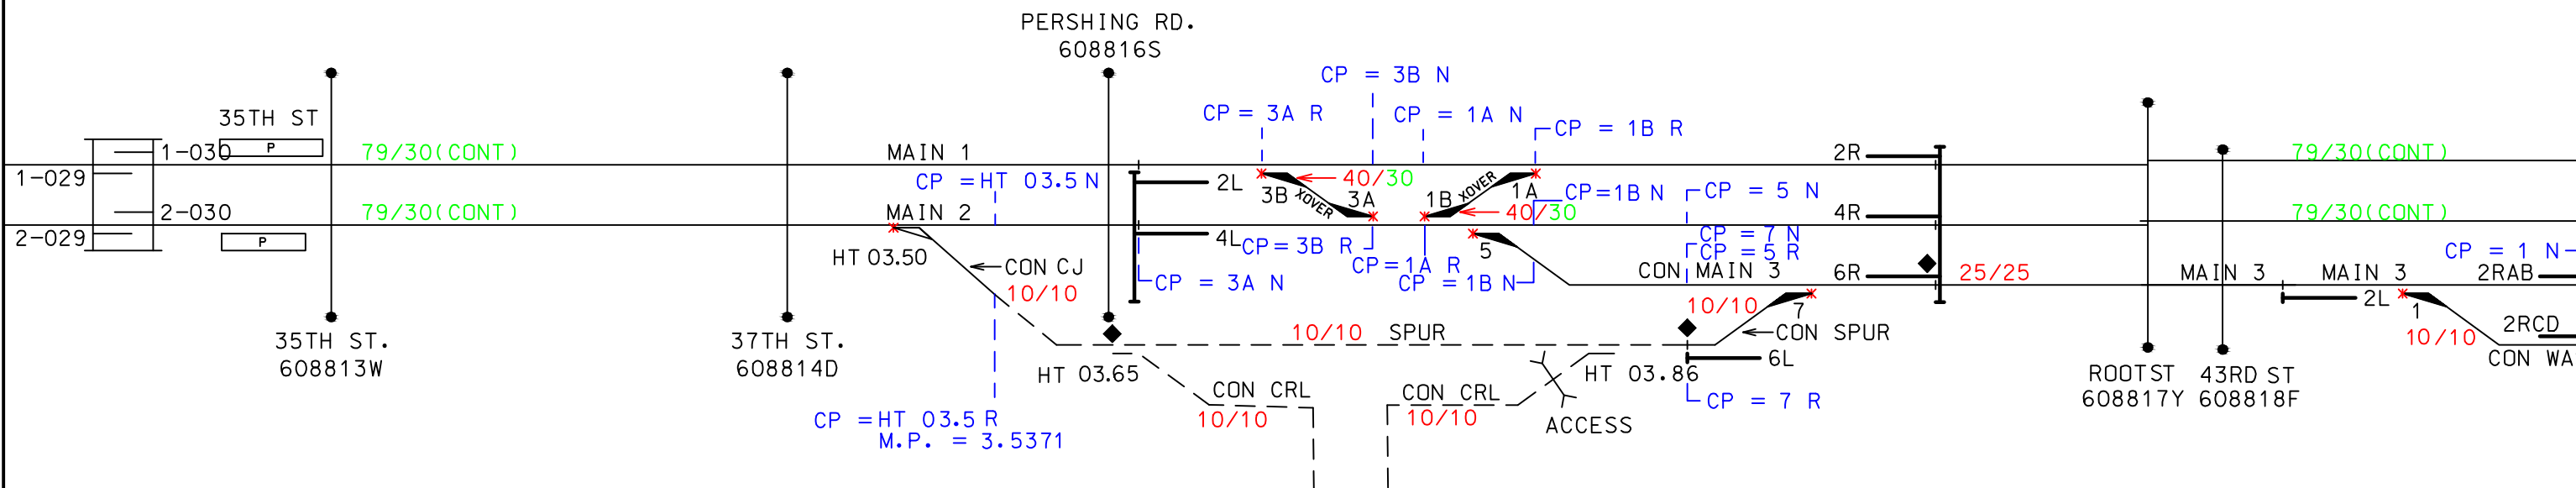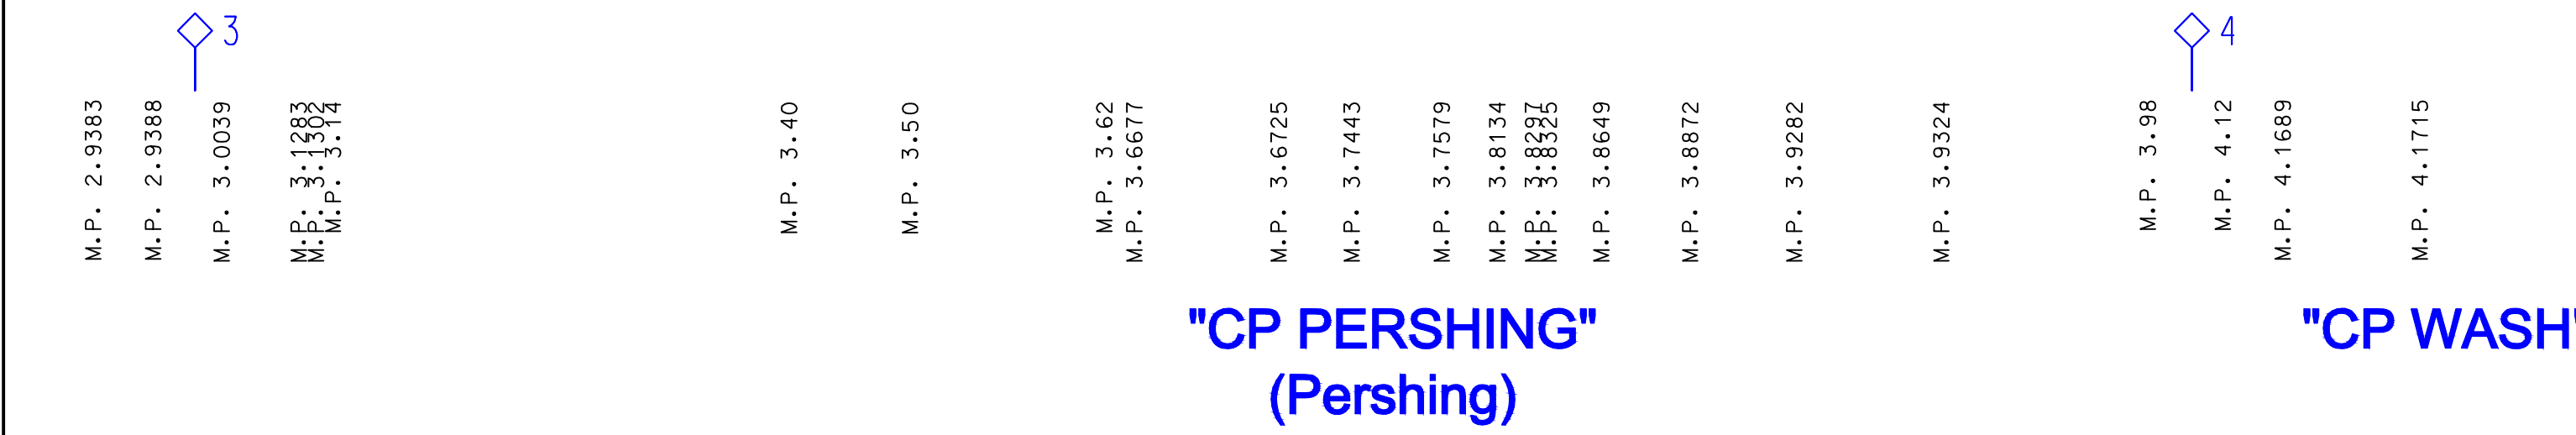


WEST-----&gt;

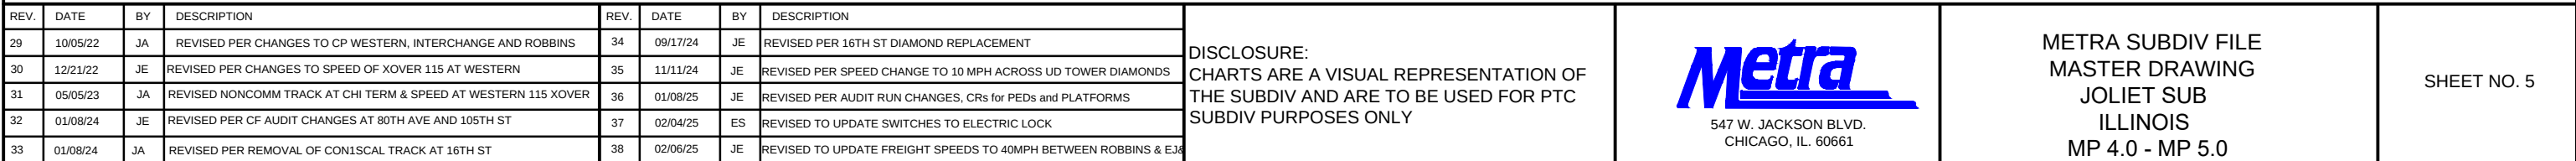

<----- EAST


WEST ----->

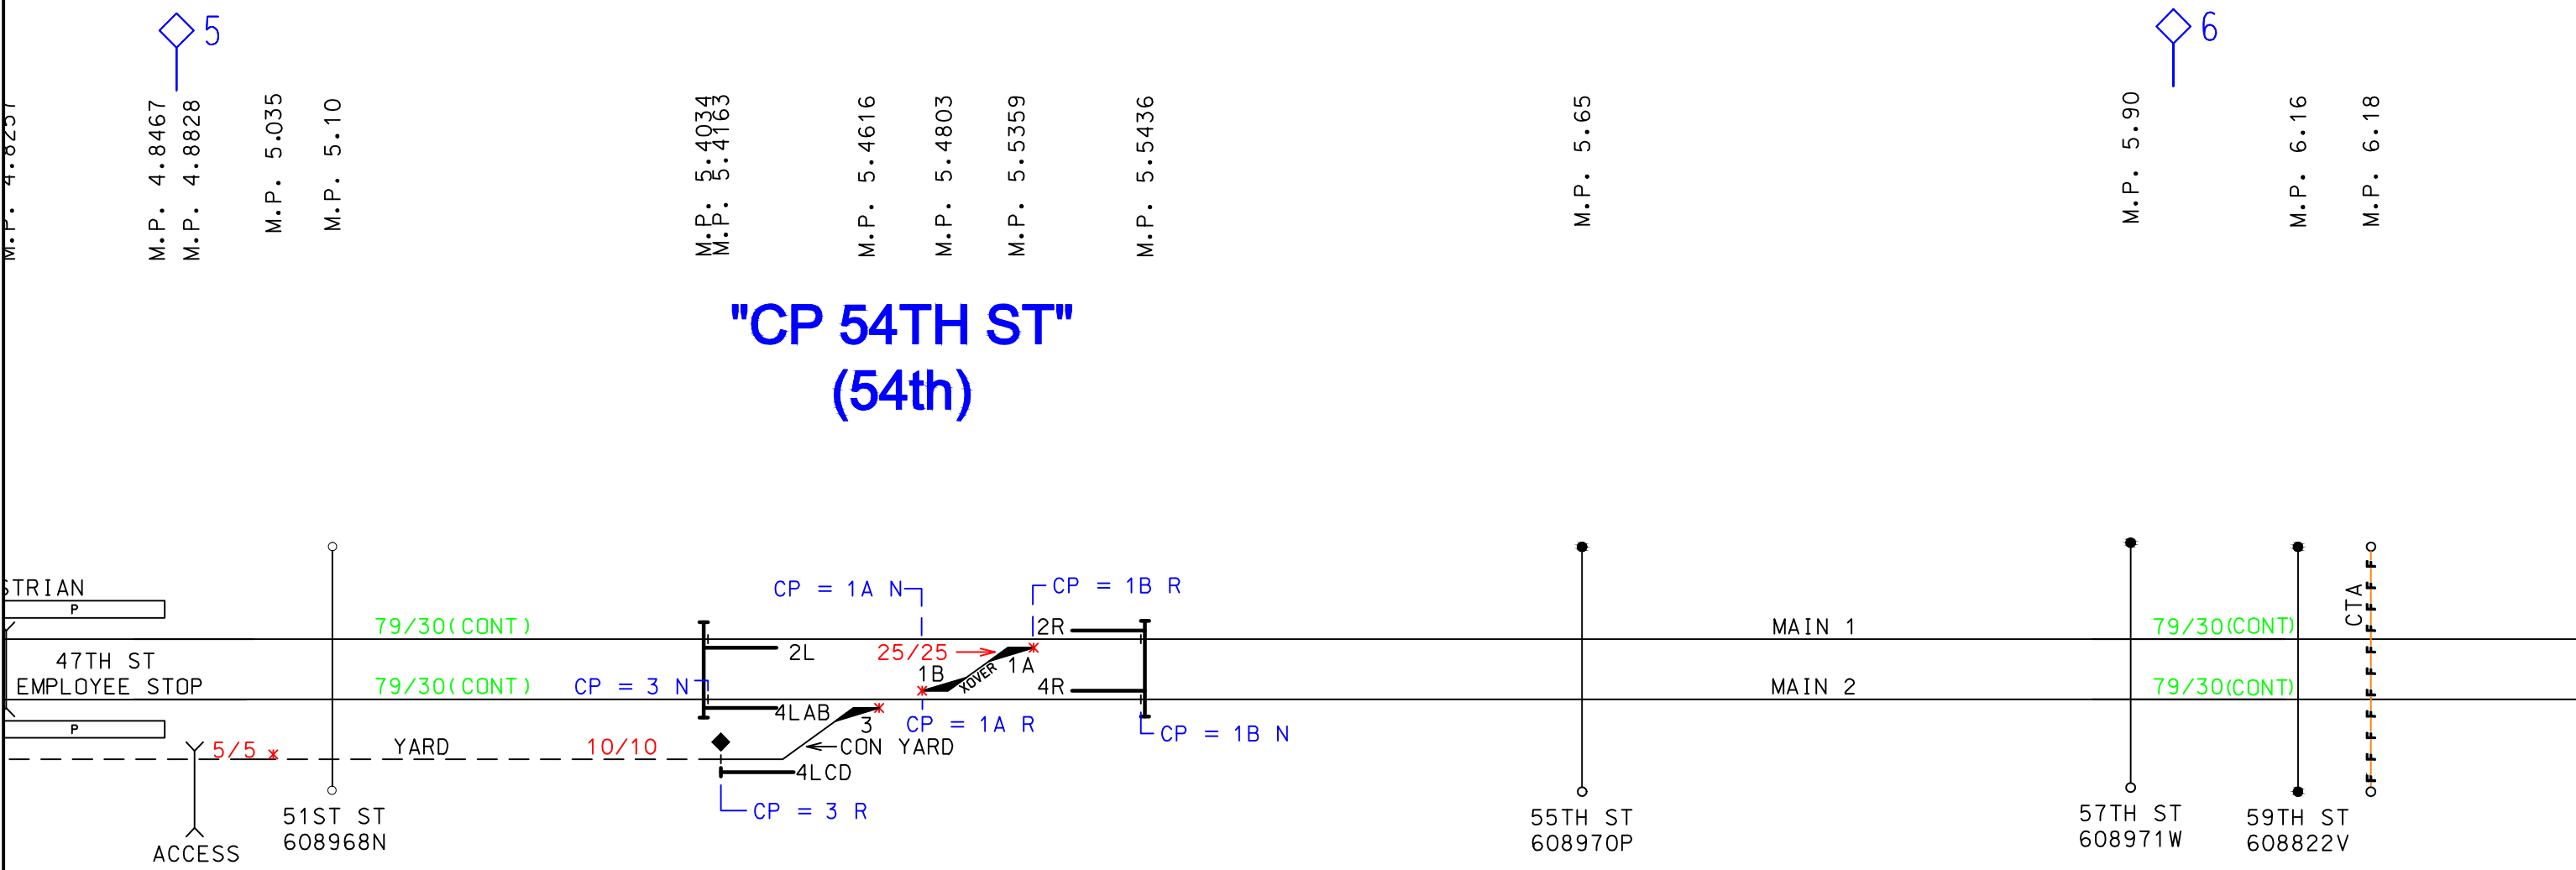



<----- EAST


WEST ----->

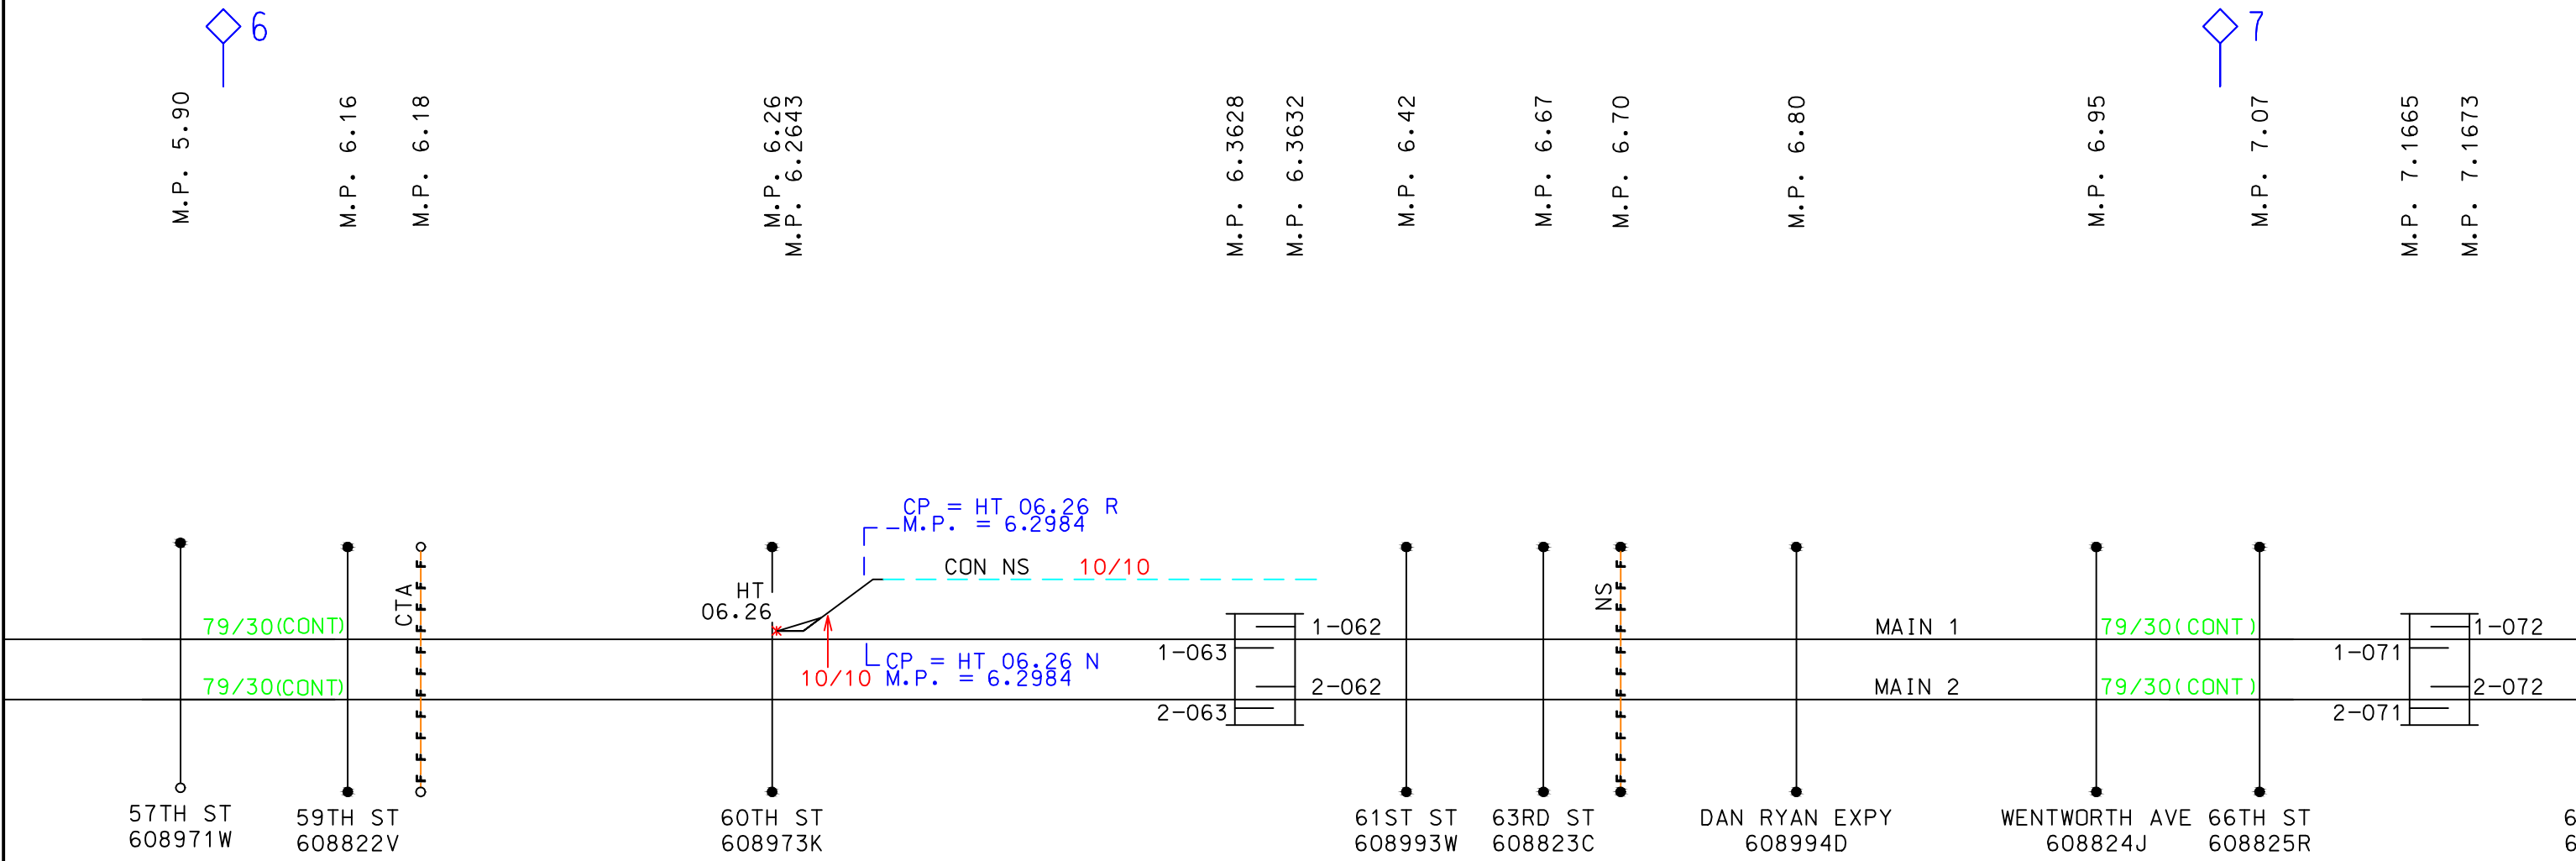

| REV. | DATE     | BY | DESCRIPTION                                                    | REV. | DATE     | BY | DESCRIPTION                                                    | DISCLOSURE:<br>CHARTS ARE A VISUAL REPRESENTATION OF<br>THE SUBDIV AND ARE TO BE USED FOR PTC<br>SUBDIV PURPOSES ONLY | <br>547 W. JACKSON BLVD.<br>CHICAGO, IL. 60661 | METRA SUBDIV FILE<br>MASTER DRAWING<br>JOLIET SUB<br>ILLINOIS<br>MP 6.0 - 7.0 | SHEET NO. 7 |
|------|----------|----|----------------------------------------------------------------|------|----------|----|----------------------------------------------------------------|---|---|-------------------------------------------------------------------------------|-------------|
| 29   | 10/05/22 | JA | REVISED PER CHANGES TO CP WESTERN, INTERCHANGE AND ROBBINS     | 34   | 09/17/24 | JE | REVISED PER 16TH ST DIAMOND REPLACEMENT                        |   |   |                                                                               |             |
| 30   | 12/21/22 | JE | REVISED PER CHANGES TO SPEED OF XOVER 115 AT WESTERN           | 35   | 11/11/24 | JE | REVISED PER SPEED CHANGE TO 10 MPH ACROSS UD TOWER DIAMONDS    |   |   |                                                                               |             |
| 31   | 05/05/23 | JA | REVISED NONCOMM TRACK AT CHI TERM & SPEED AT WESTERN 115 XOVER | 36   | 01/08/25 | JE | REVISED PER AUDIT RUN CHANGES, CRs for PEDs and PLATFORMS      |   |   |                                                                               |             |
| 32   | 01/08/24 | JE | REVISED PER CF AUDIT CHANGES AT 80TH AVE AND 105TH ST          | 37   | 02/04/25 | ES | REVISED TO UPDATE SWITCHES TO ELECTRIC LOCK                    |   |   |                                                                               |             |
| 33   | 01/08/24 | JA | REVISED PER REMOVAL OF CON1SCAL TRACK AT 16TH ST               | 38   | 02/06/25 | JE | REVISED TO UPDATE FREIGHT SPEEDS TO 40MPH BETWEEN ROBBINS & EJ |   |   |                                                                               |             |


<-----EAST

WEST----->

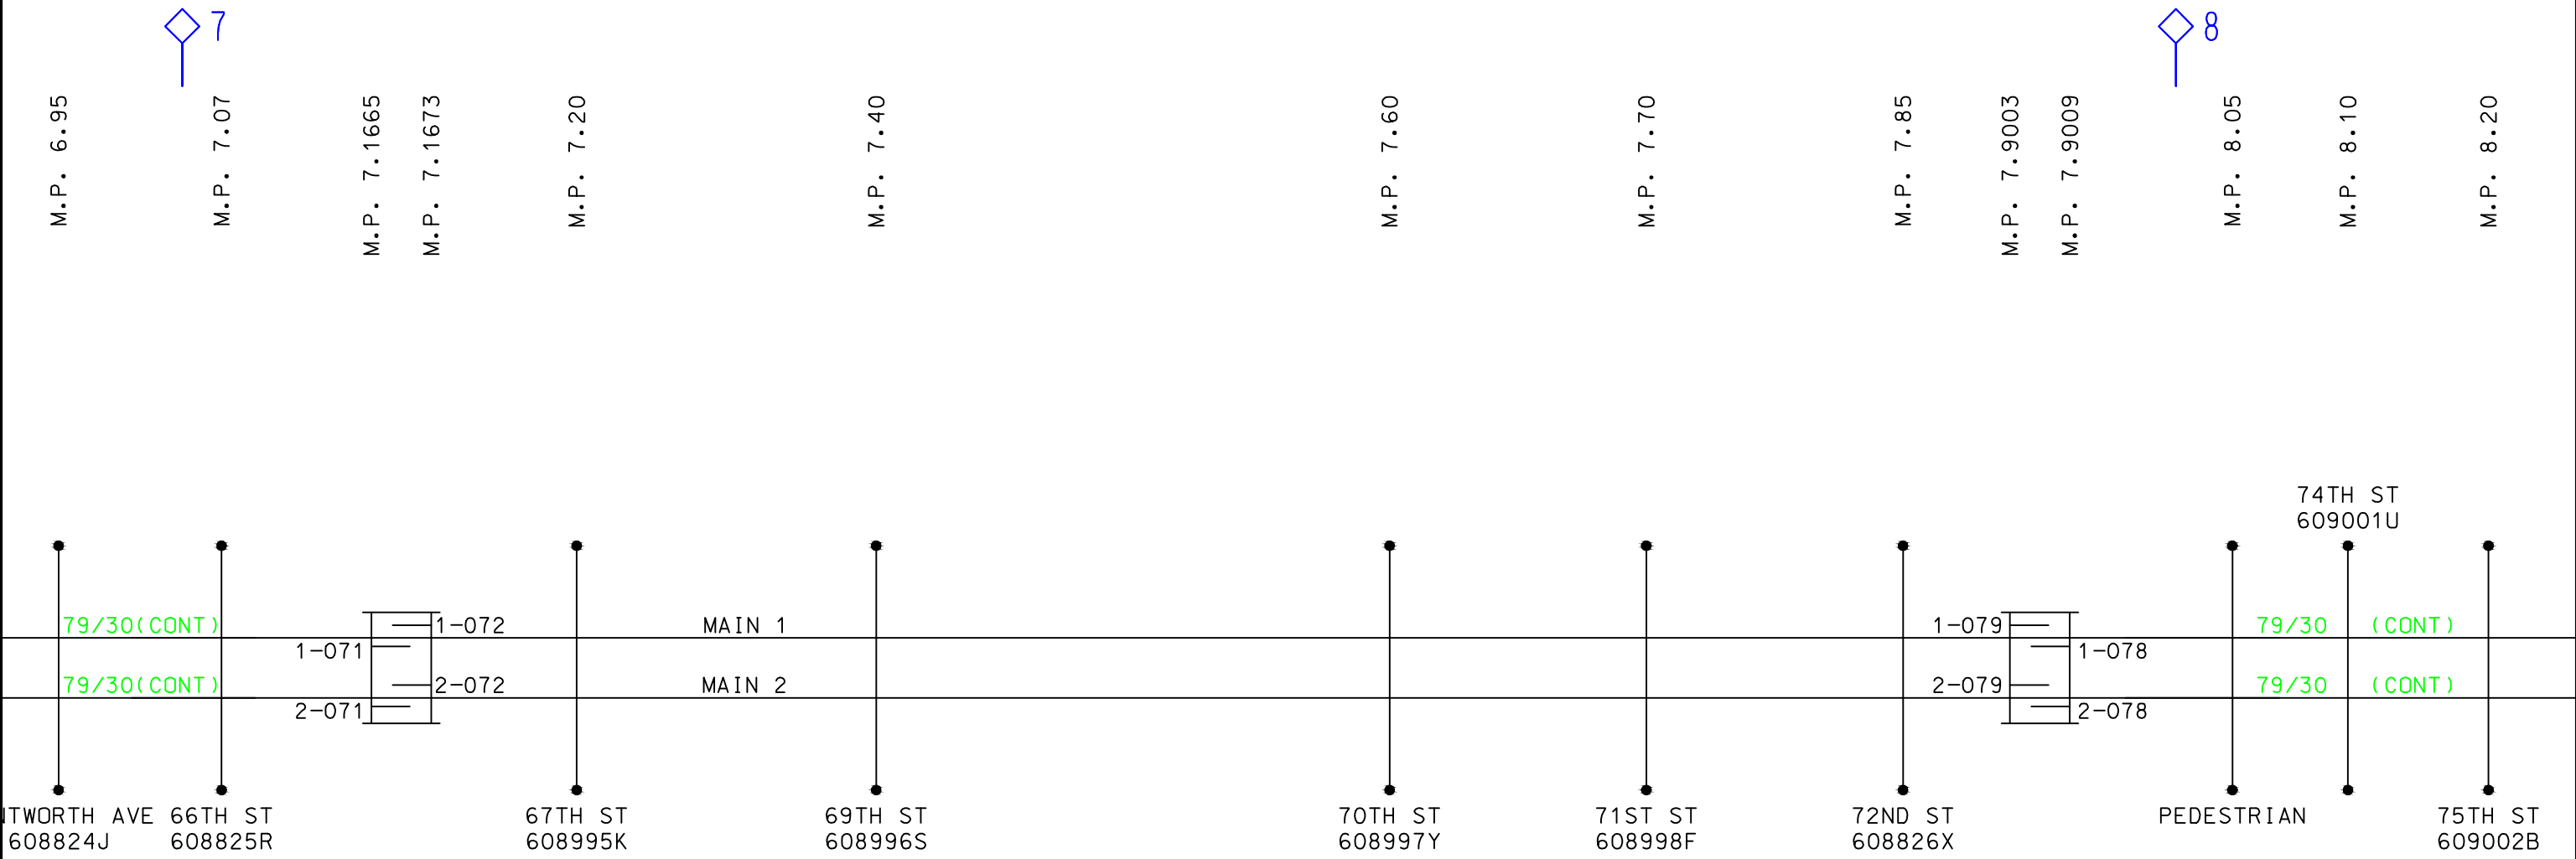


| REV. | DATE     | BY | DESCRIPTION                                                    | REV. | DATE     | BY | DESCRIPTION                                                     | DISCLOSURE:<br>CHARTS ARE A VISUAL REPRESENTATION OF<br>THE SUBDIV AND ARE TO BE USED FOR PTC<br>SUBDIV PURPOSES ONLY | <br>547 W. JACKSON BLVD.<br>CHICAGO, IL. 60661 | METRA SUBDIV FILE<br>MASTER DRAWING<br>JOLIET SUB<br>ILLINOIS<br>MP 7.0 - 8.0 | SHEET NO. 8 |
|------|----------|----|----------------------------------------------------------------|------|----------|----|-----------------------------------------------------------------|---|---|-------------------------------------------------------------------------------|-------------|
| 29   | 10/05/22 | JA | REVISED PER CHANGES TO CP WESTERN, INTERCHANGE AND ROBBINS     | 34   | 09/17/24 | JE | REVISED PER 16TH ST DIAMOND REPLACEMENT                         |   |   |                                                                               |             |
| 30   | 12/21/22 | JE | REVISED PER CHANGES TO SPEED OF XOVER 115 AT WESTERN           | 35   | 11/11/24 | JE | REVISED PER SPEED CHANGE TO 10 MPH ACROSS UD TOWER DIAMONDS     |   |   |                                                                               |             |
| 31   | 05/05/23 | JA | REVISED NONCOMM TRACK AT CHI TERM & SPEED AT WESTERN 115 XOVER | 36   | 01/08/25 | JE | REVISED PER AUDIT RUN CHANGES, CRs for PEDs and PLATFORMS       |   |   |                                                                               |             |
| 32   | 01/08/24 | JE | REVISED PER CF AUDIT CHANGES AT 80TH AVE AND 105TH ST          | 37   | 02/04/25 | ES | REVISED TO UPDATE SWITCHES TO ELECTRIC LOCK                     |   |   |                                                                               |             |
| 33   | 01/08/24 | JA | REVISED PER REMOVAL OF CON1SCAL TRACK AT 16TH ST               | 38   | 02/06/25 | JE | REVISED TO UPDATE FREIGHT SPEEDS TO 40MPH BETWEEN ROBBINS & EJA |   |   |                                                                               |             |



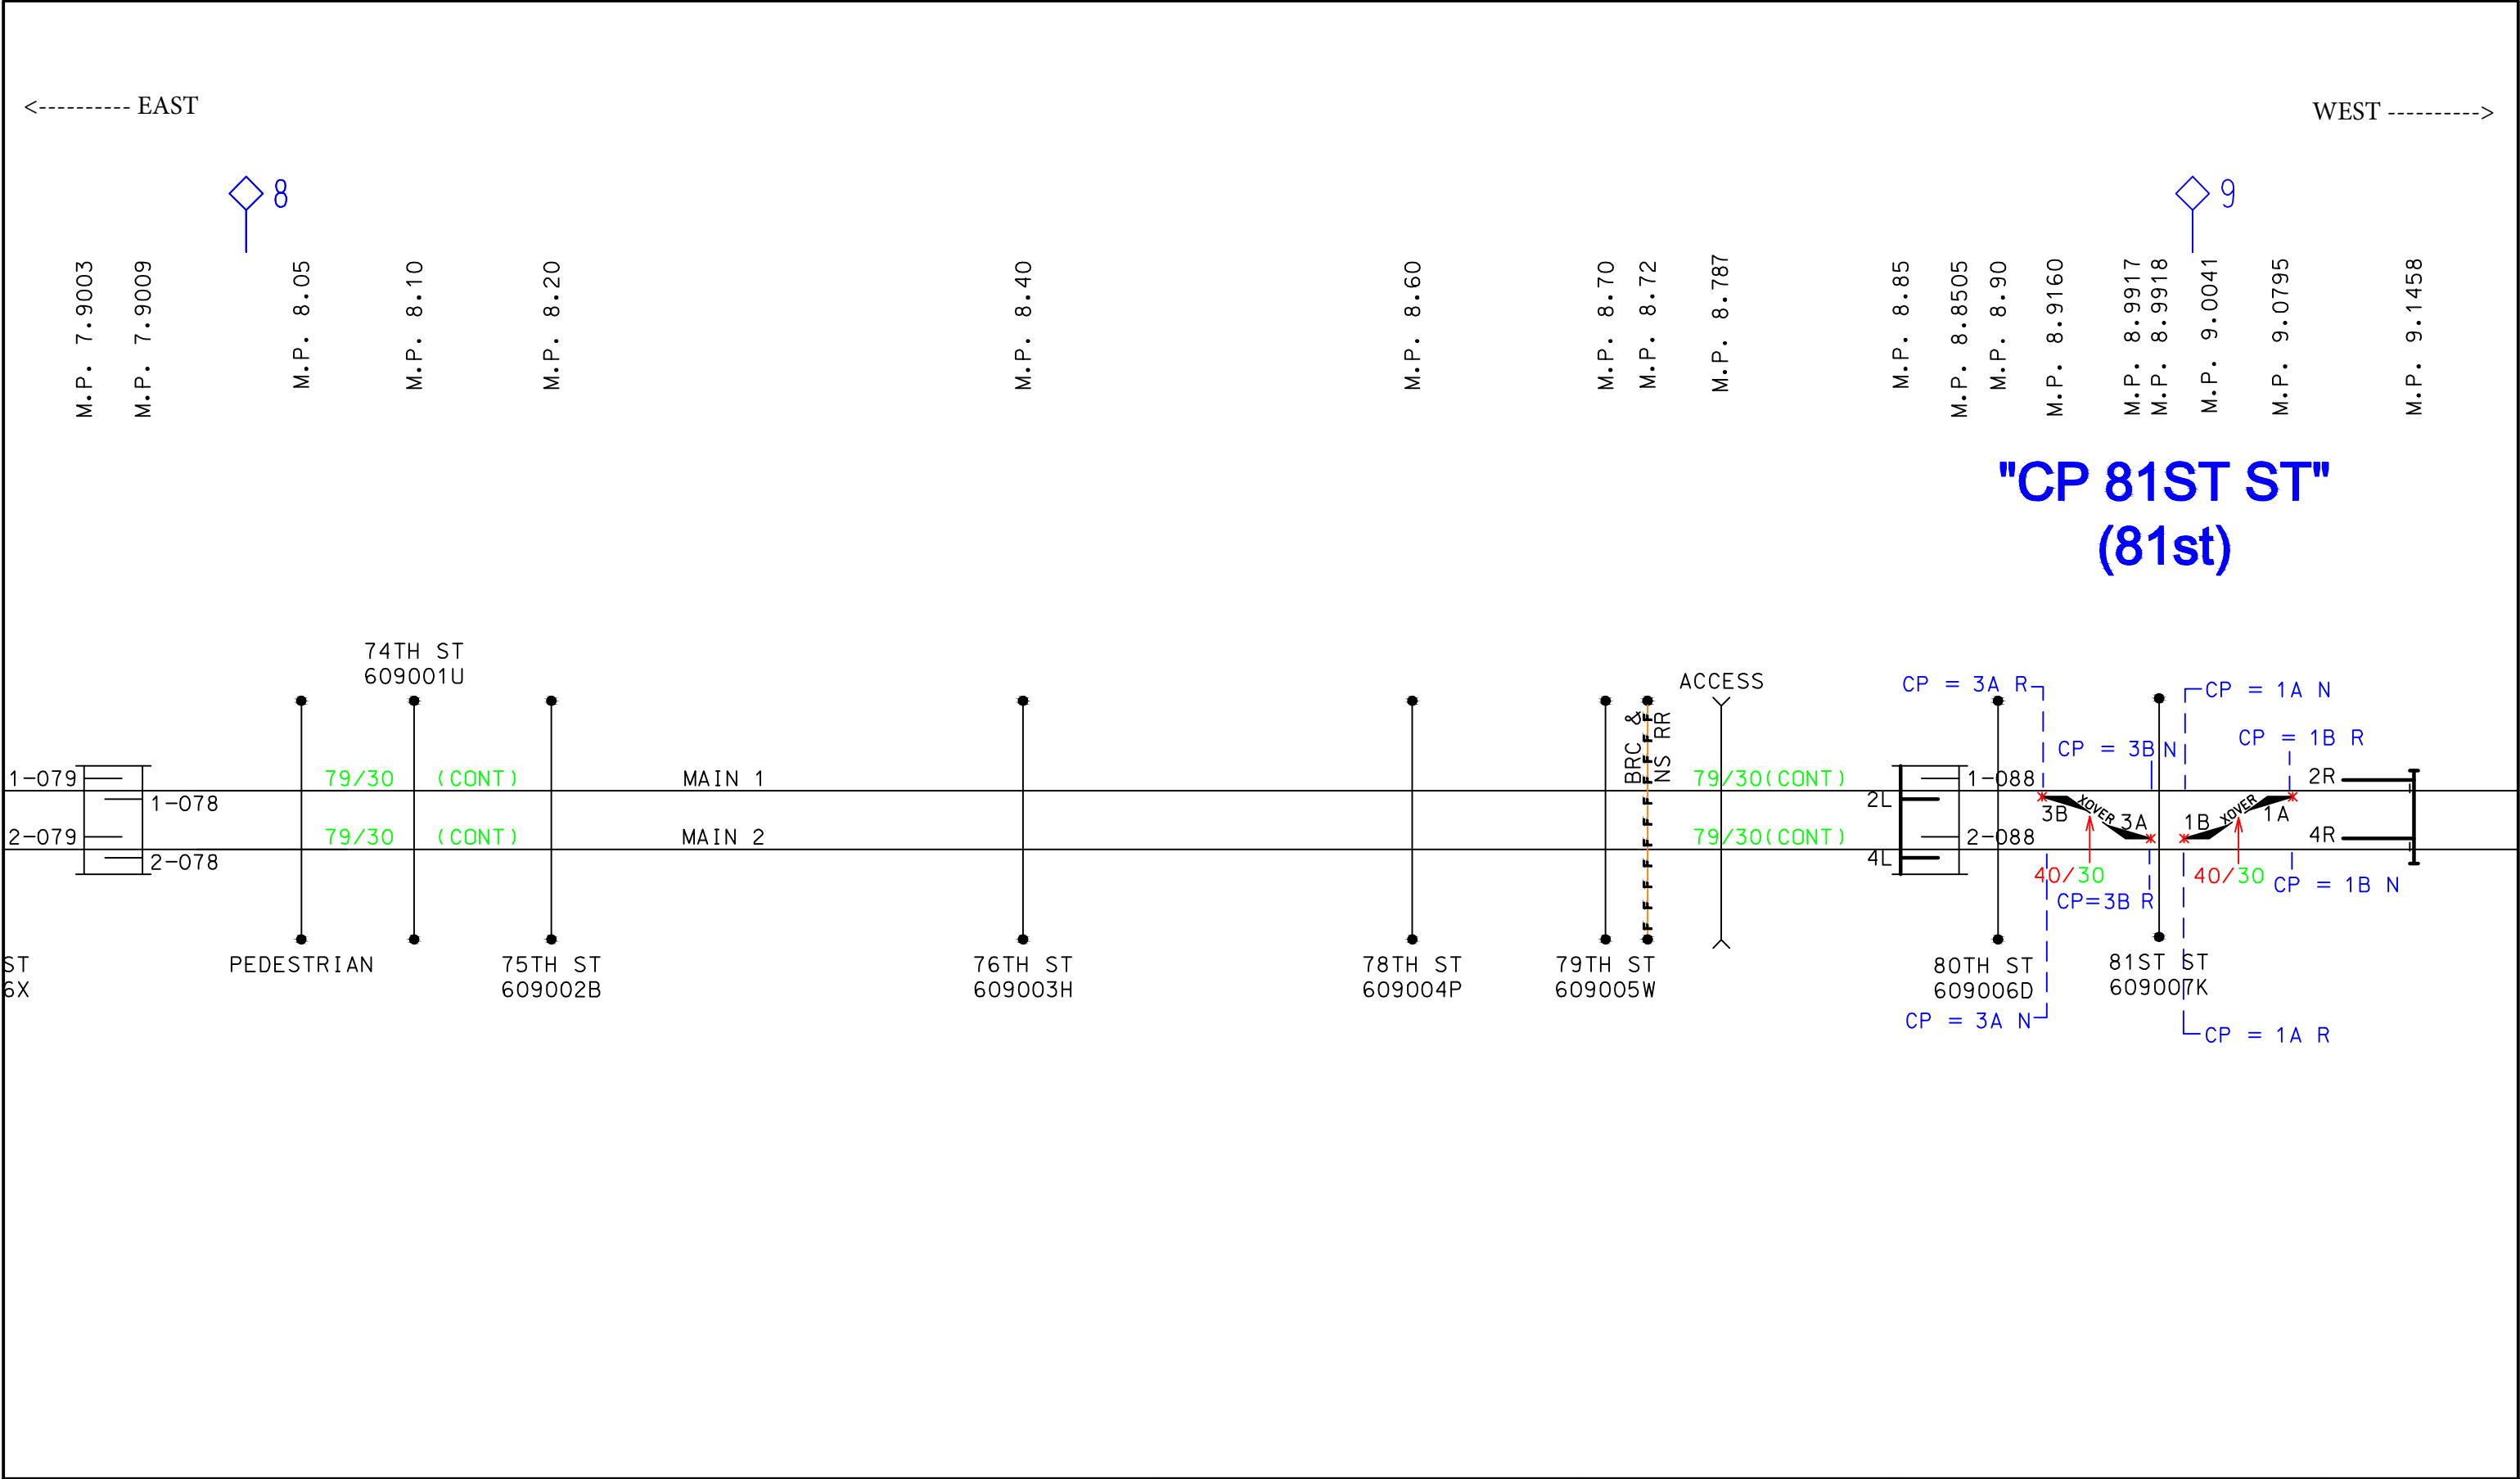

| REV. | DATE     | BY | DESCRIPTION                                                    | REV. | DATE     | BY | DESCRIPTION                                                     | DISCLOSURE:<br>CHARTS ARE A VISUAL REPRESENTATION OF<br>THE SUBDIV AND ARE TO BE USED FOR PTC<br>SUBDIV PURPOSES ONLY | <div>Metra</div> <div>547 W. JACKSON BLVD.<br/>CHICAGO, IL. 60661</div> | METRA SUBDIV FILE<br>MASTER DRAWING<br>JOLIET SUB<br>ILLINOIS<br>MP 8.0 - 9.0 | SHEET NO. 9 |
|------|----------|----|----------------------------------------------------------------|------|----------|----|-----------------------------------------------------------------|---|-------------------------------------------------------------------------|-------------------------------------------------------------------------------|-------------|
| 29   | 10/05/22 | JA | REVISED PER CHANGES TO CP WESTERN, INTERCHANGE AND ROBBINS     | 34   | 09/17/24 | JE | REVISED PER 16TH ST DIAMOND REPLACEMENT                         |   |                                                                         |                                                                               |             |
| 30   | 12/21/22 | JE | REVISED PER CHANGES TO SPEED OF XOVER 115 AT WESTERN           | 35   | 11/11/24 | JE | REVISED PER SPEED CHANGE TO 10 MPH ACROSS UD TOWER DIAMONDS     |   |                                                                         |                                                                               |             |
| 31   | 05/05/23 | JA | REVISED NONCOMM TRACK AT CHI TERM & SPEED AT WESTERN 115 XOVER | 36   | 01/08/25 | JE | REVISED PER AUDIT RUN CHANGES, CRs for PEDs and PLATFORMS       |   |                                                                         |                                                                               |             |
| 32   | 01/08/24 | JE | REVISED PER CF AUDIT CHANGES AT 80TH AVE AND 105TH ST          | 37   | 02/04/25 | ES | REVISED TO UPDATE SWITCHES TO ELECTRIC LOCK                     |   |                                                                         |                                                                               |             |
| 33   | 01/08/24 | JA | REVISED PER REMOVAL OF CON1SCAL TRACK AT 16TH ST               | 38   | 02/06/25 | JE | REVISED TO UPDATE FREIGHT SPEEDS TO 40MPH BETWEEN ROBBINS & EJA |   |                                                                         |                                                                               |             |

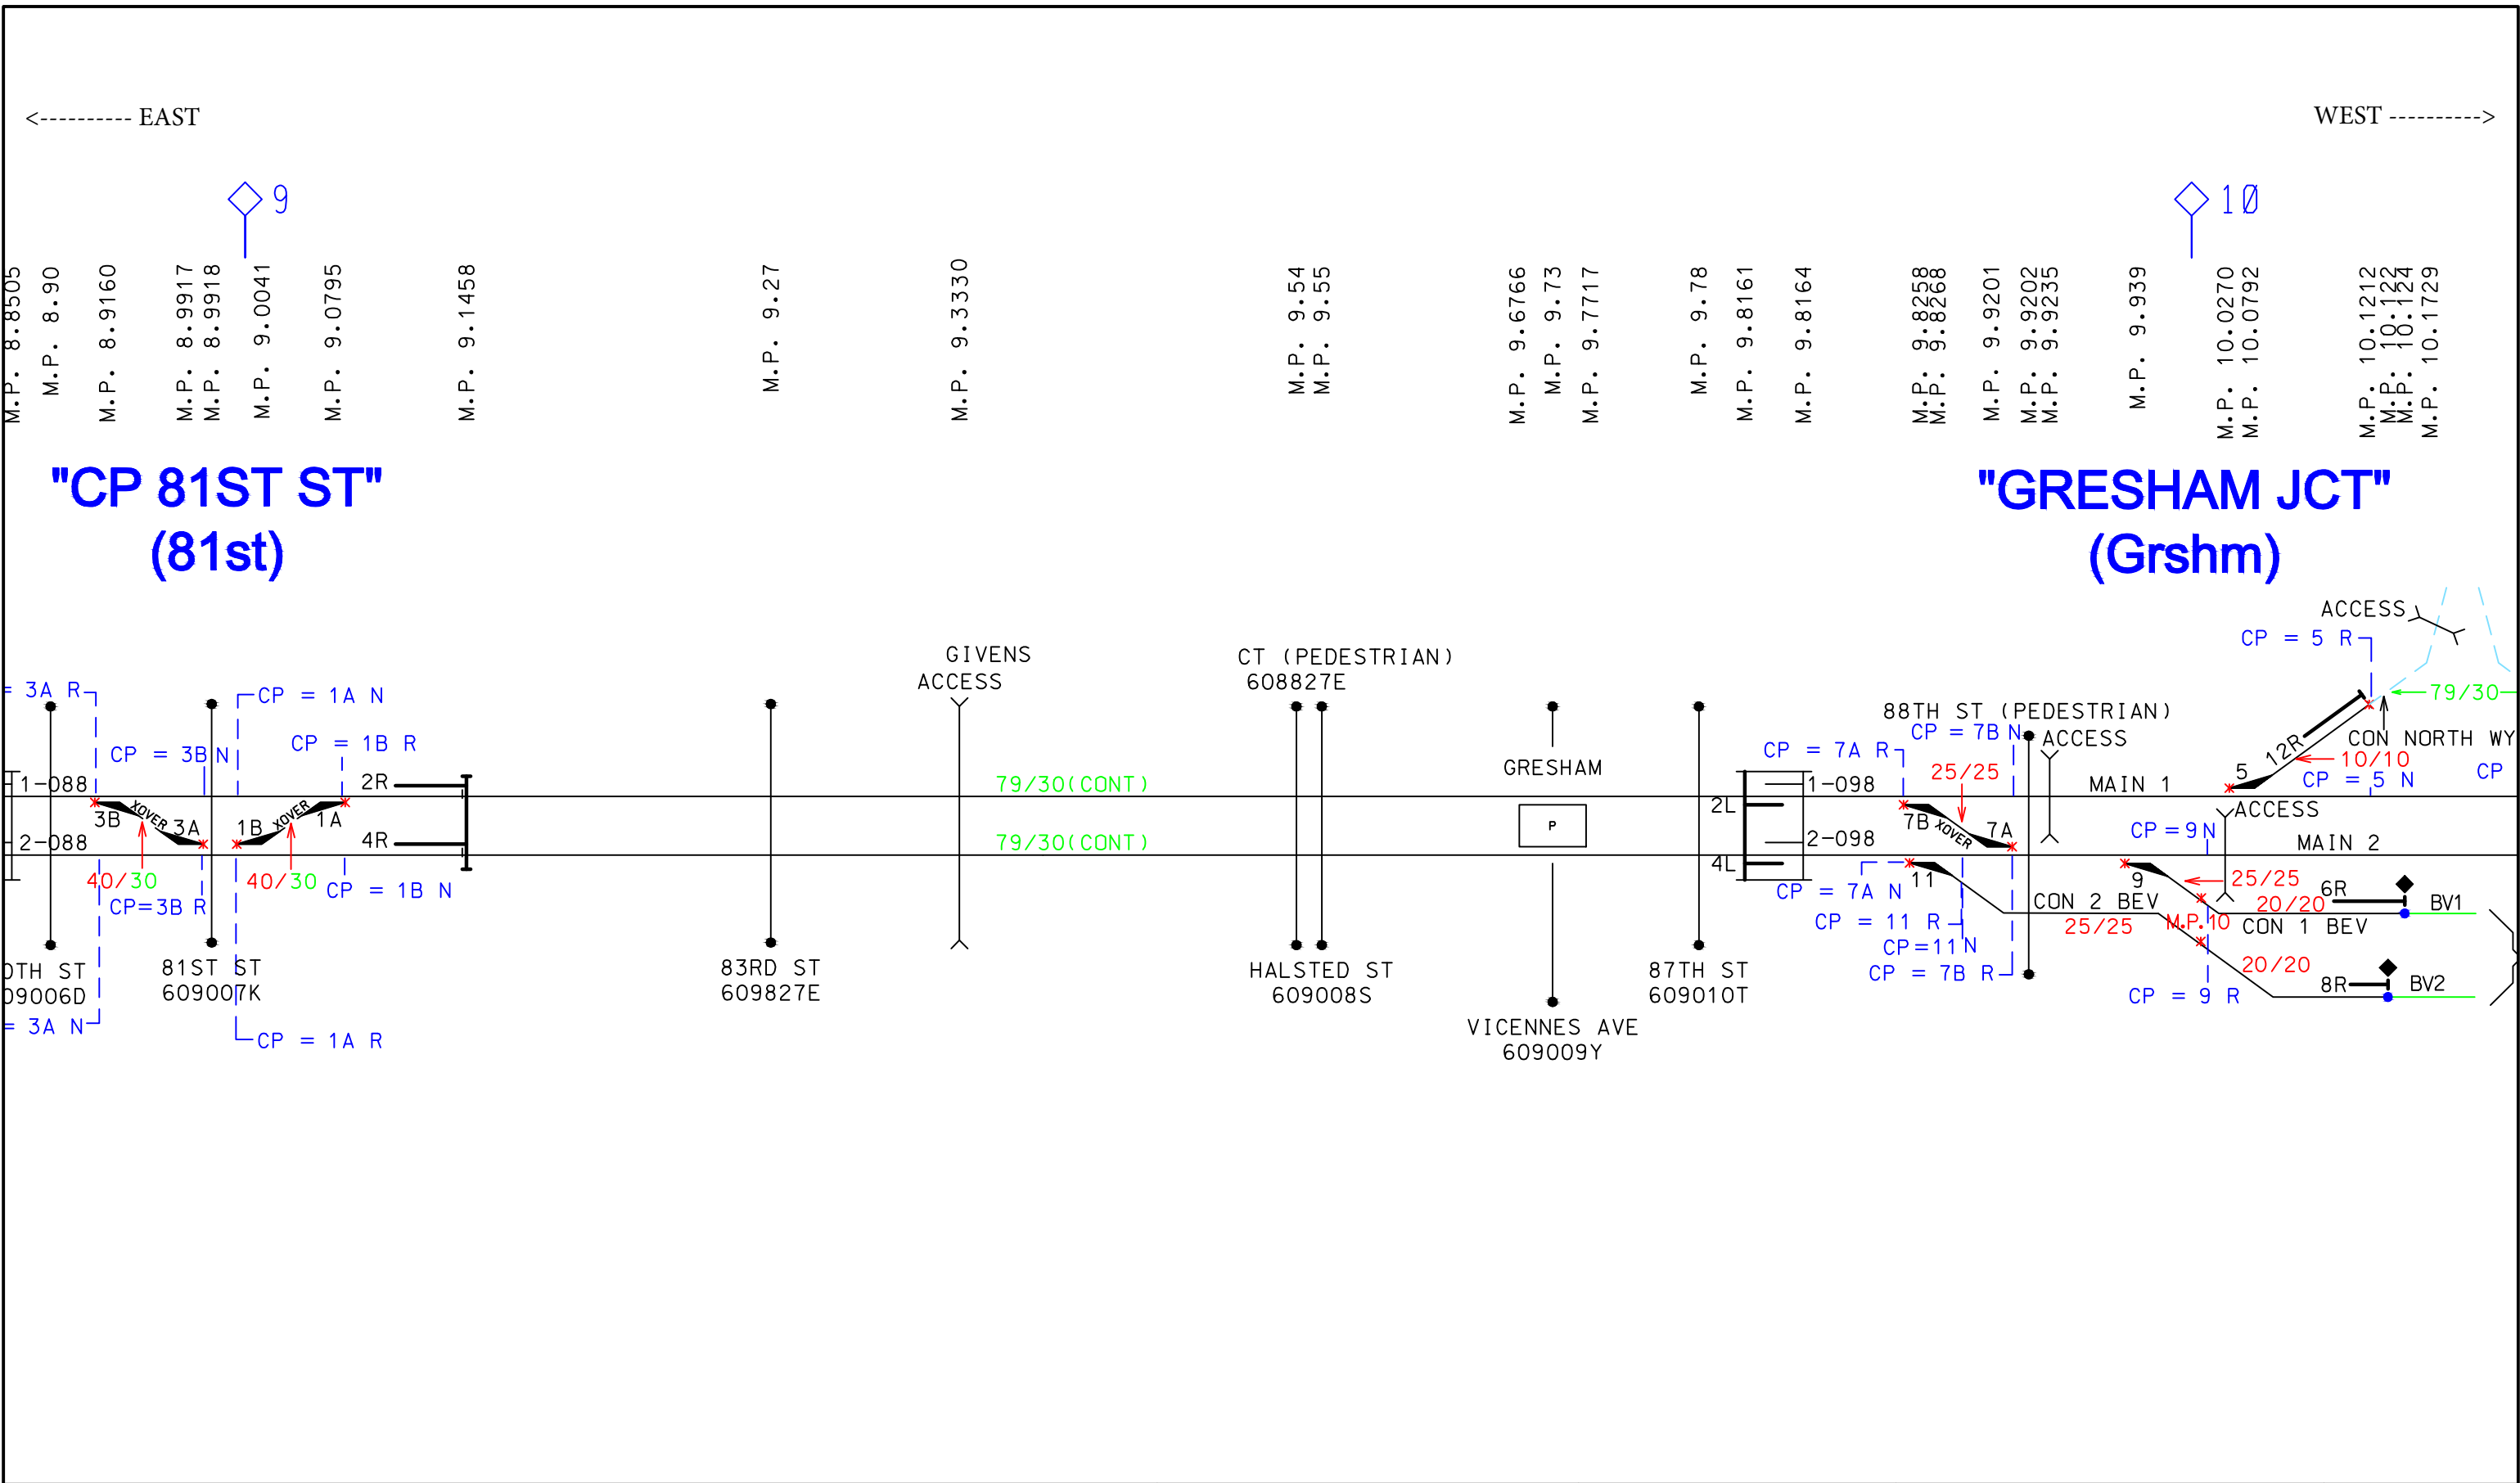

| REV. | DATE     | BY | DESCRIPTION                                                    | REV. | DATE     | BY | DESCRIPTION                                                    | DISCLOSURE:<br>CHARTS ARE A VISUAL REPRESENTATION OF<br>THE SUBDIV AND ARE TO BE USED FOR PTC<br>SUBDIV PURPOSES ONLY | <br>547 W. JACKSON BLVD.<br>CHICAGO, IL. 60661 | METRA SUBDIV FILE<br>MASTER DRAWING<br>JOLIET SUB,<br>ILLINOIS<br>M.P. 9.0 - 10.0 | SHEET NO. 10 |
|------|----------|----|----------------------------------------------------------------|------|----------|----|----------------------------------------------------------------|---|---|-----------------------------------------------------------------------------------|--------------|
| 29   | 10/05/22 | JA | REVISED PER CHANGES TO CP WESTERN, INTERCHANGE AND ROBBINS     | 34   | 09/17/24 | JE | REVISED PER 16TH ST DIAMOND REPLACEMENT                        |   |   |                                                                                   |              |
| 30   | 12/21/22 | JE | REVISED PER CHANGES TO SPEED OF XOVER 115 AT WESTERN           | 35   | 11/11/24 | JE | REVISED PER SPEED CHANGE TO 10 MPH ACROSS UD TOWER DIAMONDS    |   |   |                                                                                   |              |
| 31   | 05/05/23 | JA | REVISED NONCOMM TRACK AT CHI TERM & SPEED AT WESTERN 115 XOVER | 36   | 01/08/25 | JE | REVISED PER AUDIT RUN CHANGES, CRs for PEDs and PLATFORMS      |   |   |                                                                                   |              |
| 32   | 01/08/24 | JE | REVISED PER CF AUDIT CHANGES AT 80TH AVE AND 105TH ST          | 37   | 02/04/25 | ES | REVISED TO UPDATE SWITCHES TO ELECTRIC LOCK                    |   |   |                                                                                   |              |
| 33   | 01/08/24 | JA | REVISED PER REMOVAL OF CON1SCAL TRACK AT 16TH ST               | 38   | 02/06/25 | JE | REVISED TO UPDATE FREIGHT SPEEDS TO 40MPH BETWEEN ROBBINS & EJ |   |   |                                                                                   |              |

<----- EAST

WEST ----->

M.P. 9.8161

M.P. 9.8164

M.P. 9.8258

M.P. 9.8268

M.P. 9.9201

M.P. 9.9202

M.P. 9.9235

M.P. 9.939

M.P. 10.0270

M.P. 10.0792

M.P. 10.1212

M.P. 10.122

M.P. 10.124

M.P. 10.1729

M.P. 10.29

M.P. 10.3951

M.P. 10.4308

M.P. 10.4834

M.P. 10.4971

M.P. 10.4978

M.P. 10.805

M.P. 10.838

M.P. 10.8390


M.P. 10.8612

M.P. 10.8822

10


11


"GRESHAM JCT"  
(Grshm)

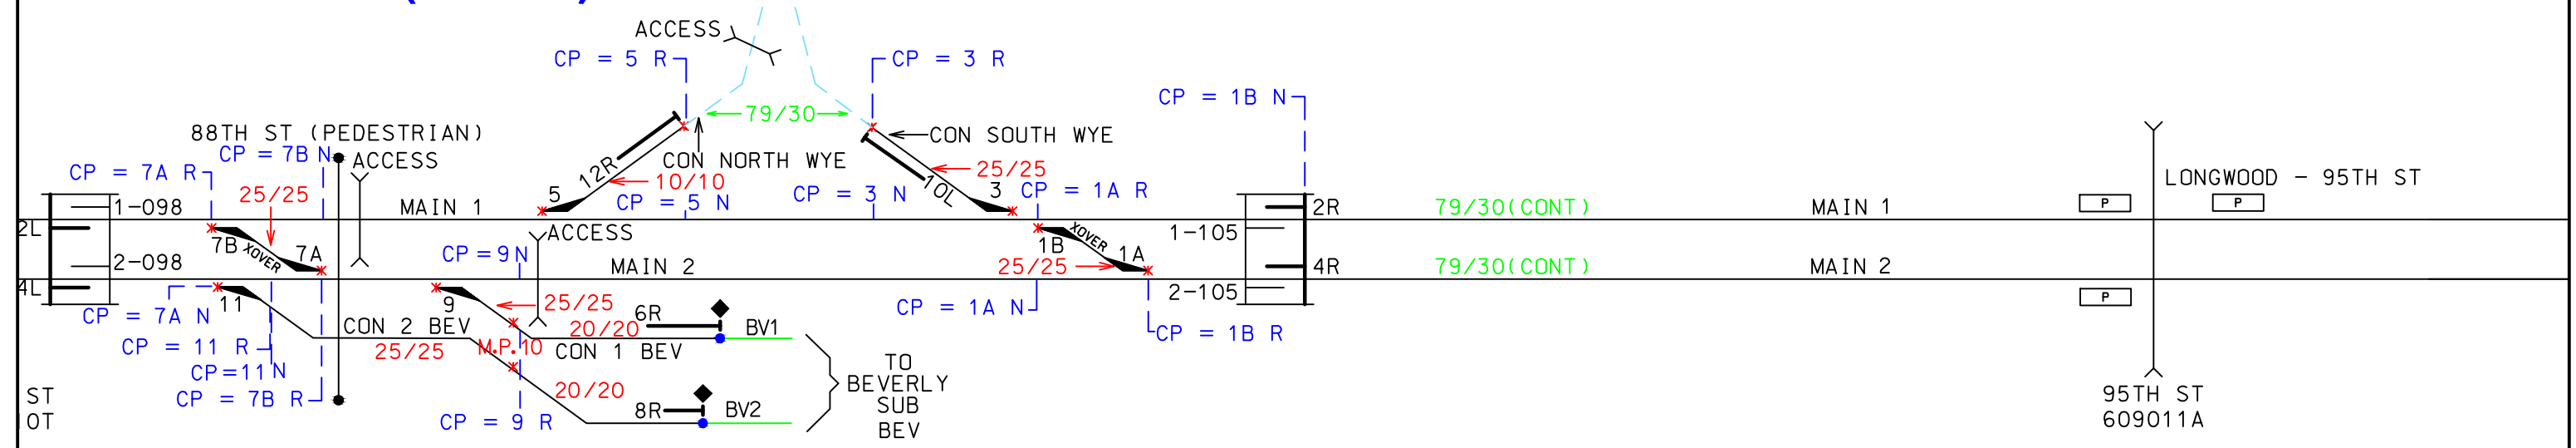


<----- EAST

WEST ----->

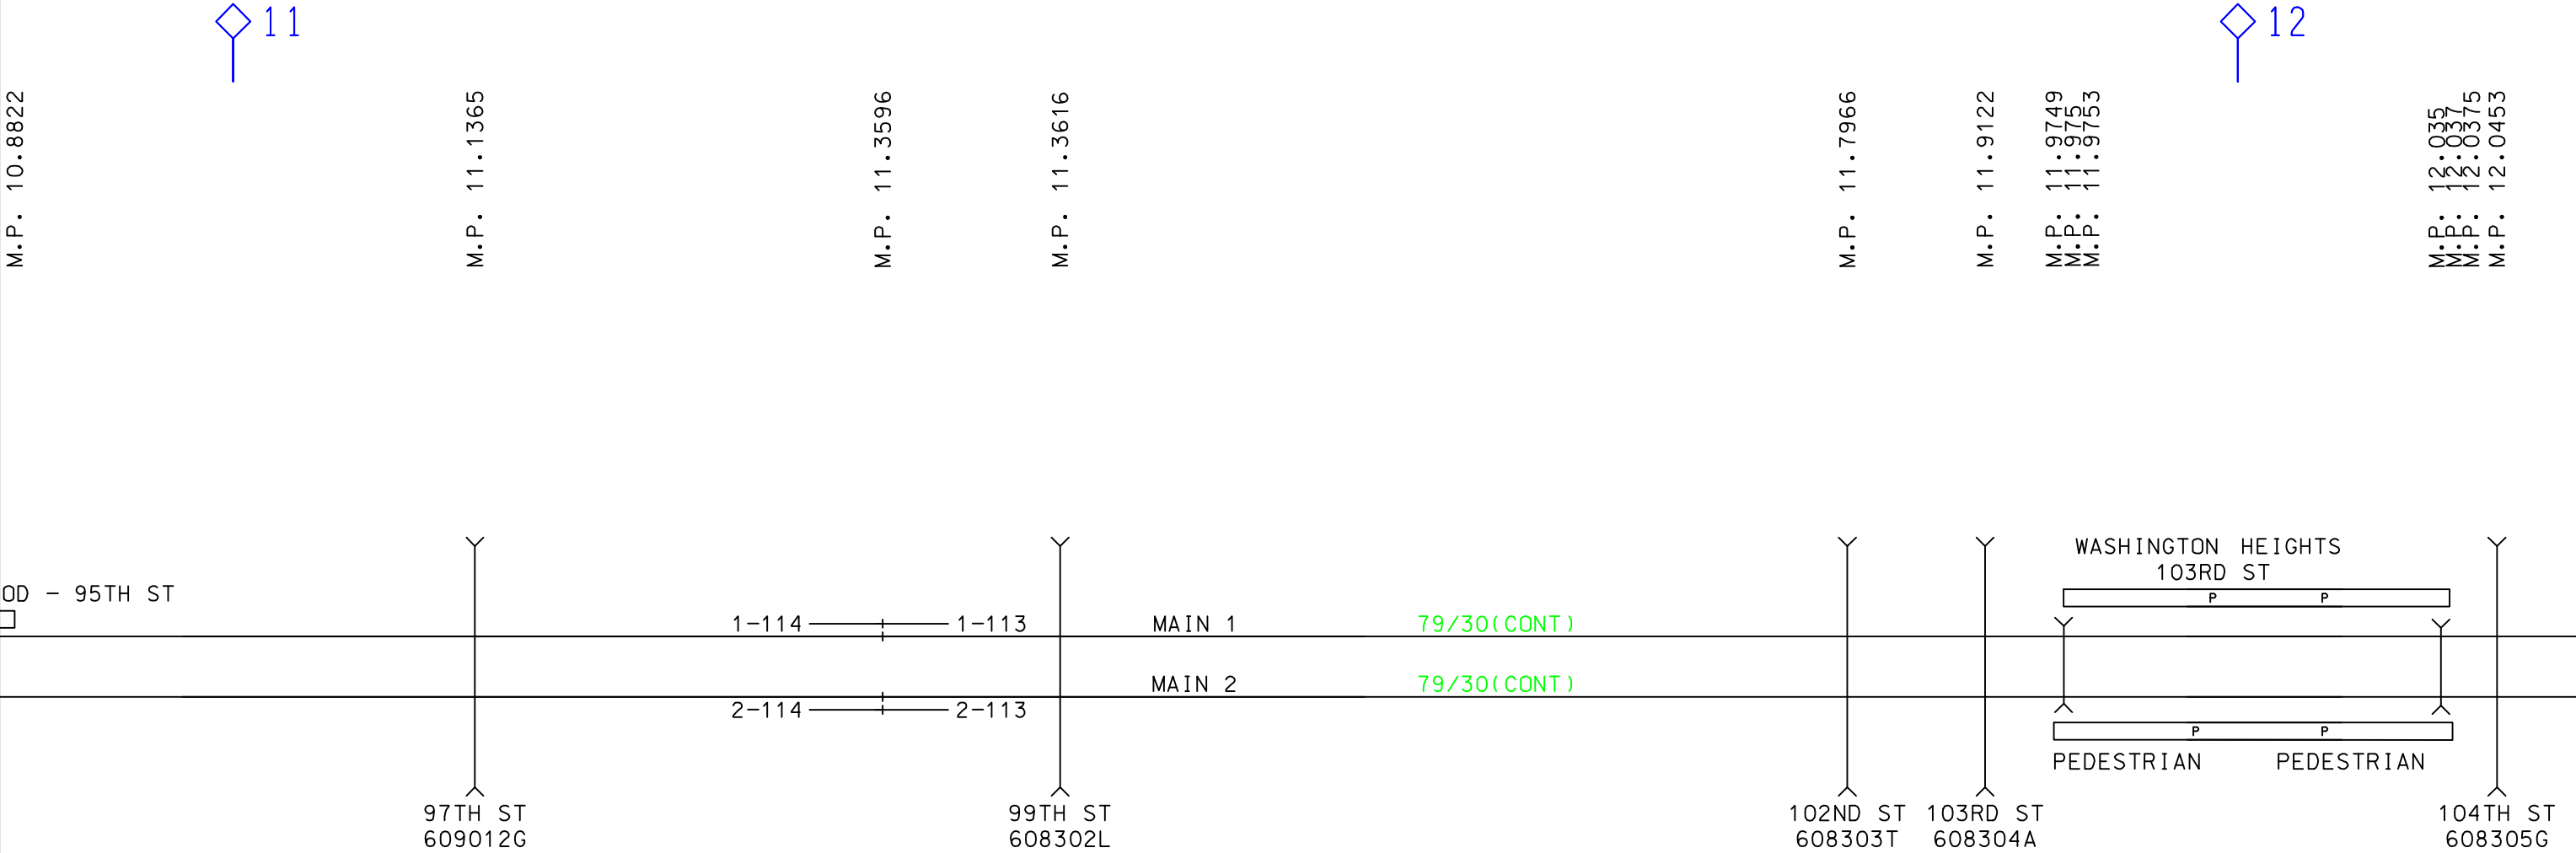

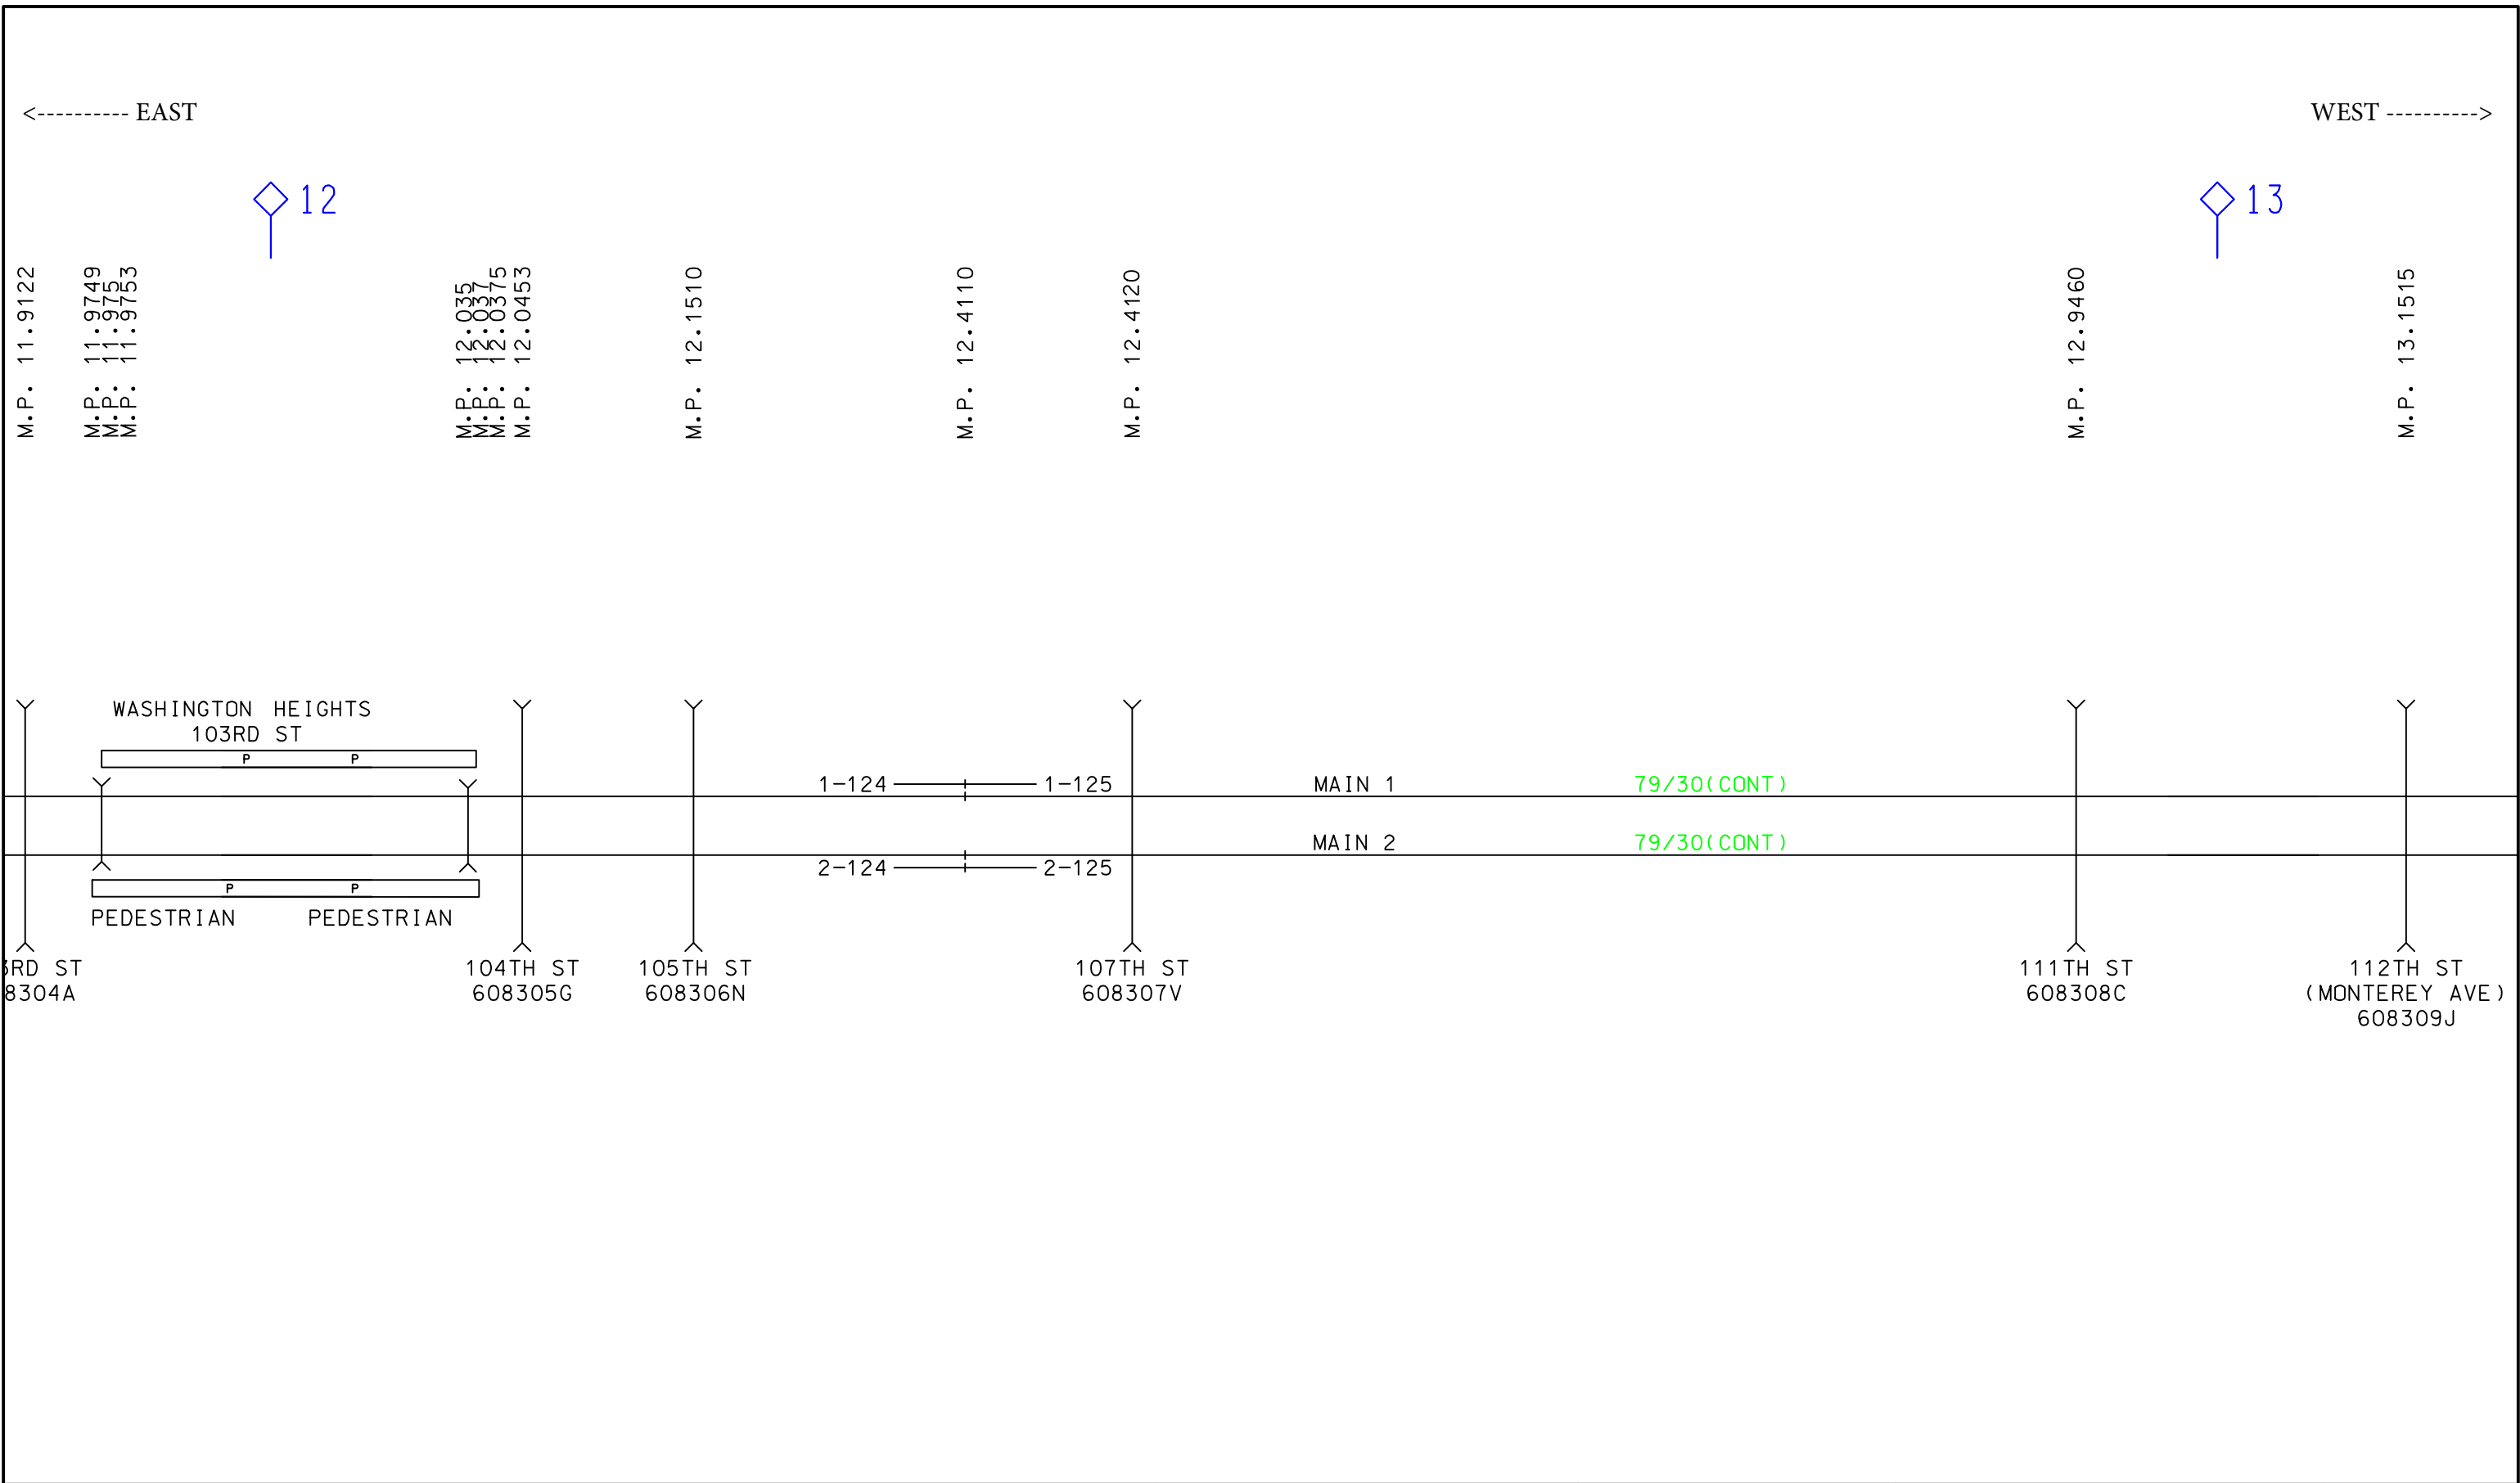


| REV. | DATE     | BY | DESCRIPTION                                                    | REV. | DATE     | BY | DESCRIPTION                                                    | DISCLOSURE:<br>CHARTS ARE A VISUAL REPRESENTATION OF<br>THE SUBDIV AND ARE TO BE USED FOR PTC<br>SUBDIV PURPOSES ONLY | <br>547 W. JACKSON BLVD.<br>CHICAGO, IL. 60661 | METRA SUBDIV FILE<br>MASTER DRAWING<br>JOLIET SUB,<br>ILLINOIS<br>M.P. 12.0 - 13.0 | SHEET NO. 13 |
|------|----------|----|----------------------------------------------------------------|------|----------|----|----------------------------------------------------------------|---|---|------------------------------------------------------------------------------------|--------------|
| 29   | 10/05/22 | JA | REVISED PER CHANGES TO CP WESTERN, INTERCHANGE AND ROBBINS     | 34   | 09/17/24 | JE | REVISED PER 16TH ST DIAMOND REPLACEMENT                        |   |   |                                                                                    |              |
| 30   | 12/21/22 | JE | REVISED PER CHANGES TO SPEED OF XOVER 115 AT WESTERN           | 35   | 11/11/24 | JE | REVISED PER SPEED CHANGE TO 10 MPH ACROSS UD TOWER DIAMONDS    |   |   |                                                                                    |              |
| 31   | 05/05/23 | JA | REVISED NONCOMM TRACK AT CHI TERM & SPEED AT WESTERN 115 XOVER | 36   | 01/08/25 | JE | REVISED PER AUDIT RUN CHANGES, CRs for PEDs and PLATFORMS      |   |   |                                                                                    |              |
| 32   | 01/08/24 | JE | REVISED PER CF AUDIT CHANGES AT 80TH AVE AND 105TH ST          | 37   | 02/04/25 | ES | REVISED TO UPDATE SWITCHES TO ELECTRIC LOCK                    |   |   |                                                                                    |              |
| 33   | 01/08/24 | JA | REVISED PER REMOVAL OF CON1SCAL TRACK AT 16TH ST               | 38   | 02/06/25 | JE | REVISED TO UPDATE FREIGHT SPEEDS TO 40MPH BETWEEN ROBBINS & EJ |   |   |                                                                                    |              |

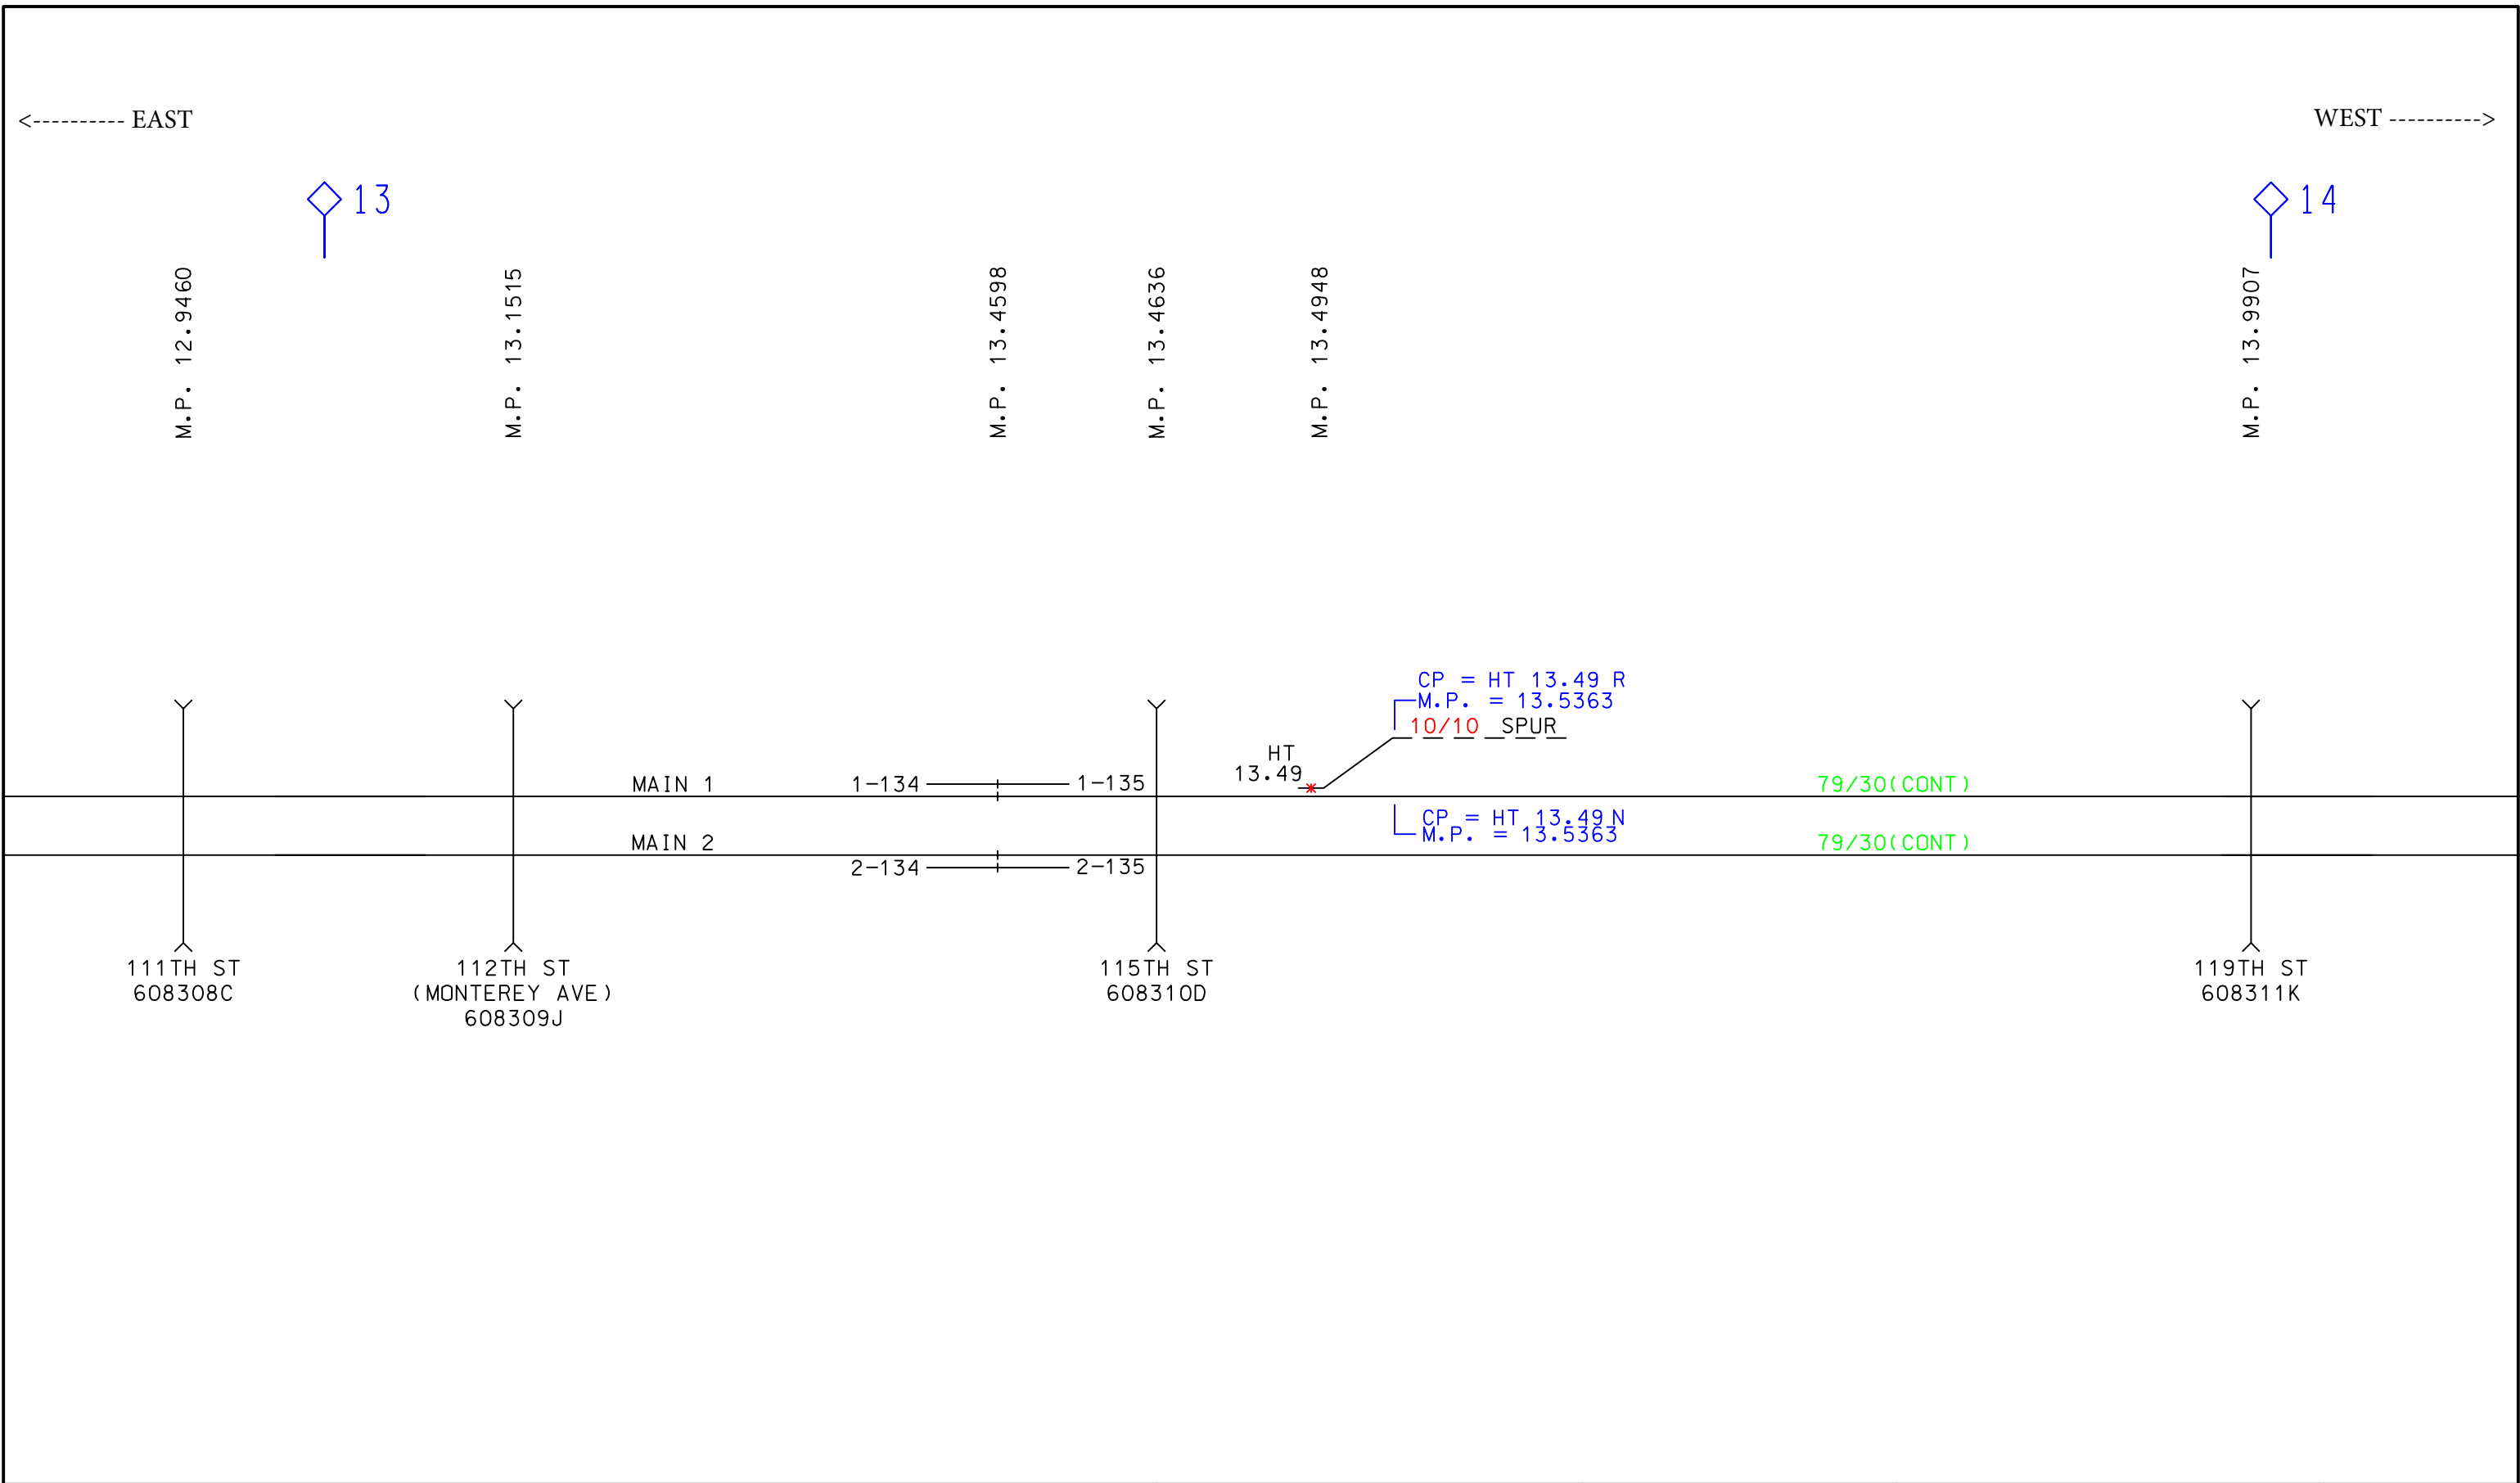

| REV. | DATE     | BY | DESCRIPTION                                                    | REV. | DATE     | BY | DESCRIPTION                                                     | DISCLOSURE:<br>CHARTS ARE A VISUAL REPRESENTATION OF<br>THE SUBDIV AND ARE TO BE USED FOR PTC<br>SUBDIV PURPOSES ONLY | <div>Metra</div> <div>547 W. JACKSON BLVD.<br/>CHICAGO, IL. 60661</div> | METRA SUBDIV FILE<br>MASTER DRAWING<br>JOLIET SUB,<br>ILLINOIS<br>M.P.13.0 - 14.0 | SHEET NO. 14 |
|------|----------|----|----------------------------------------------------------------|------|----------|----|-----------------------------------------------------------------|---|-------------------------------------------------------------------------|-----------------------------------------------------------------------------------|--------------|
| 29   | 10/05/22 | JA | REVISED PER CHANGES TO CP WESTERN, INTERCHANGE AND ROBBINS     | 34   | 09/17/24 | JE | REVISED PER 16TH ST DIAMOND REPLACEMENT                         |   |                                                                         |                                                                                   |              |
| 30   | 12/21/22 | JE | REVISED PER CHANGES TO SPEED OF XOVER 115 AT WESTERN           | 35   | 11/11/24 | JE | REVISED PER SPEED CHANGE TO 10 MPH ACROSS UD TOWER DIAMONDS     |   |                                                                         |                                                                                   |              |
| 31   | 05/05/23 | JA | REVISED NONCOMM TRACK AT CHI TERM & SPEED AT WESTERN 115 XOVER | 36   | 01/08/25 | JE | REVISED PER AUDIT RUN CHANGES, CRs for PEDs and PLATFORMS       |   |                                                                         |                                                                                   |              |
| 32   | 01/08/24 | JE | REVISED PER CF AUDIT CHANGES AT 80TH AVE AND 105TH ST          | 37   | 02/04/25 | ES | REVISED TO UPDATE SWITCHES TO ELECTRIC LOCK                     |   |                                                                         |                                                                                   |              |
| 33   | 01/08/24 | JA | REVISED PER REMOVAL OF CON1SCAL TRACK AT 16TH ST               | 38   | 02/06/25 | JE | REVISED TO UPDATE FREIGHT SPEEDS TO 40MPH BETWEEN ROBBINS & EJA |   |                                                                         |                                                                                   |              |



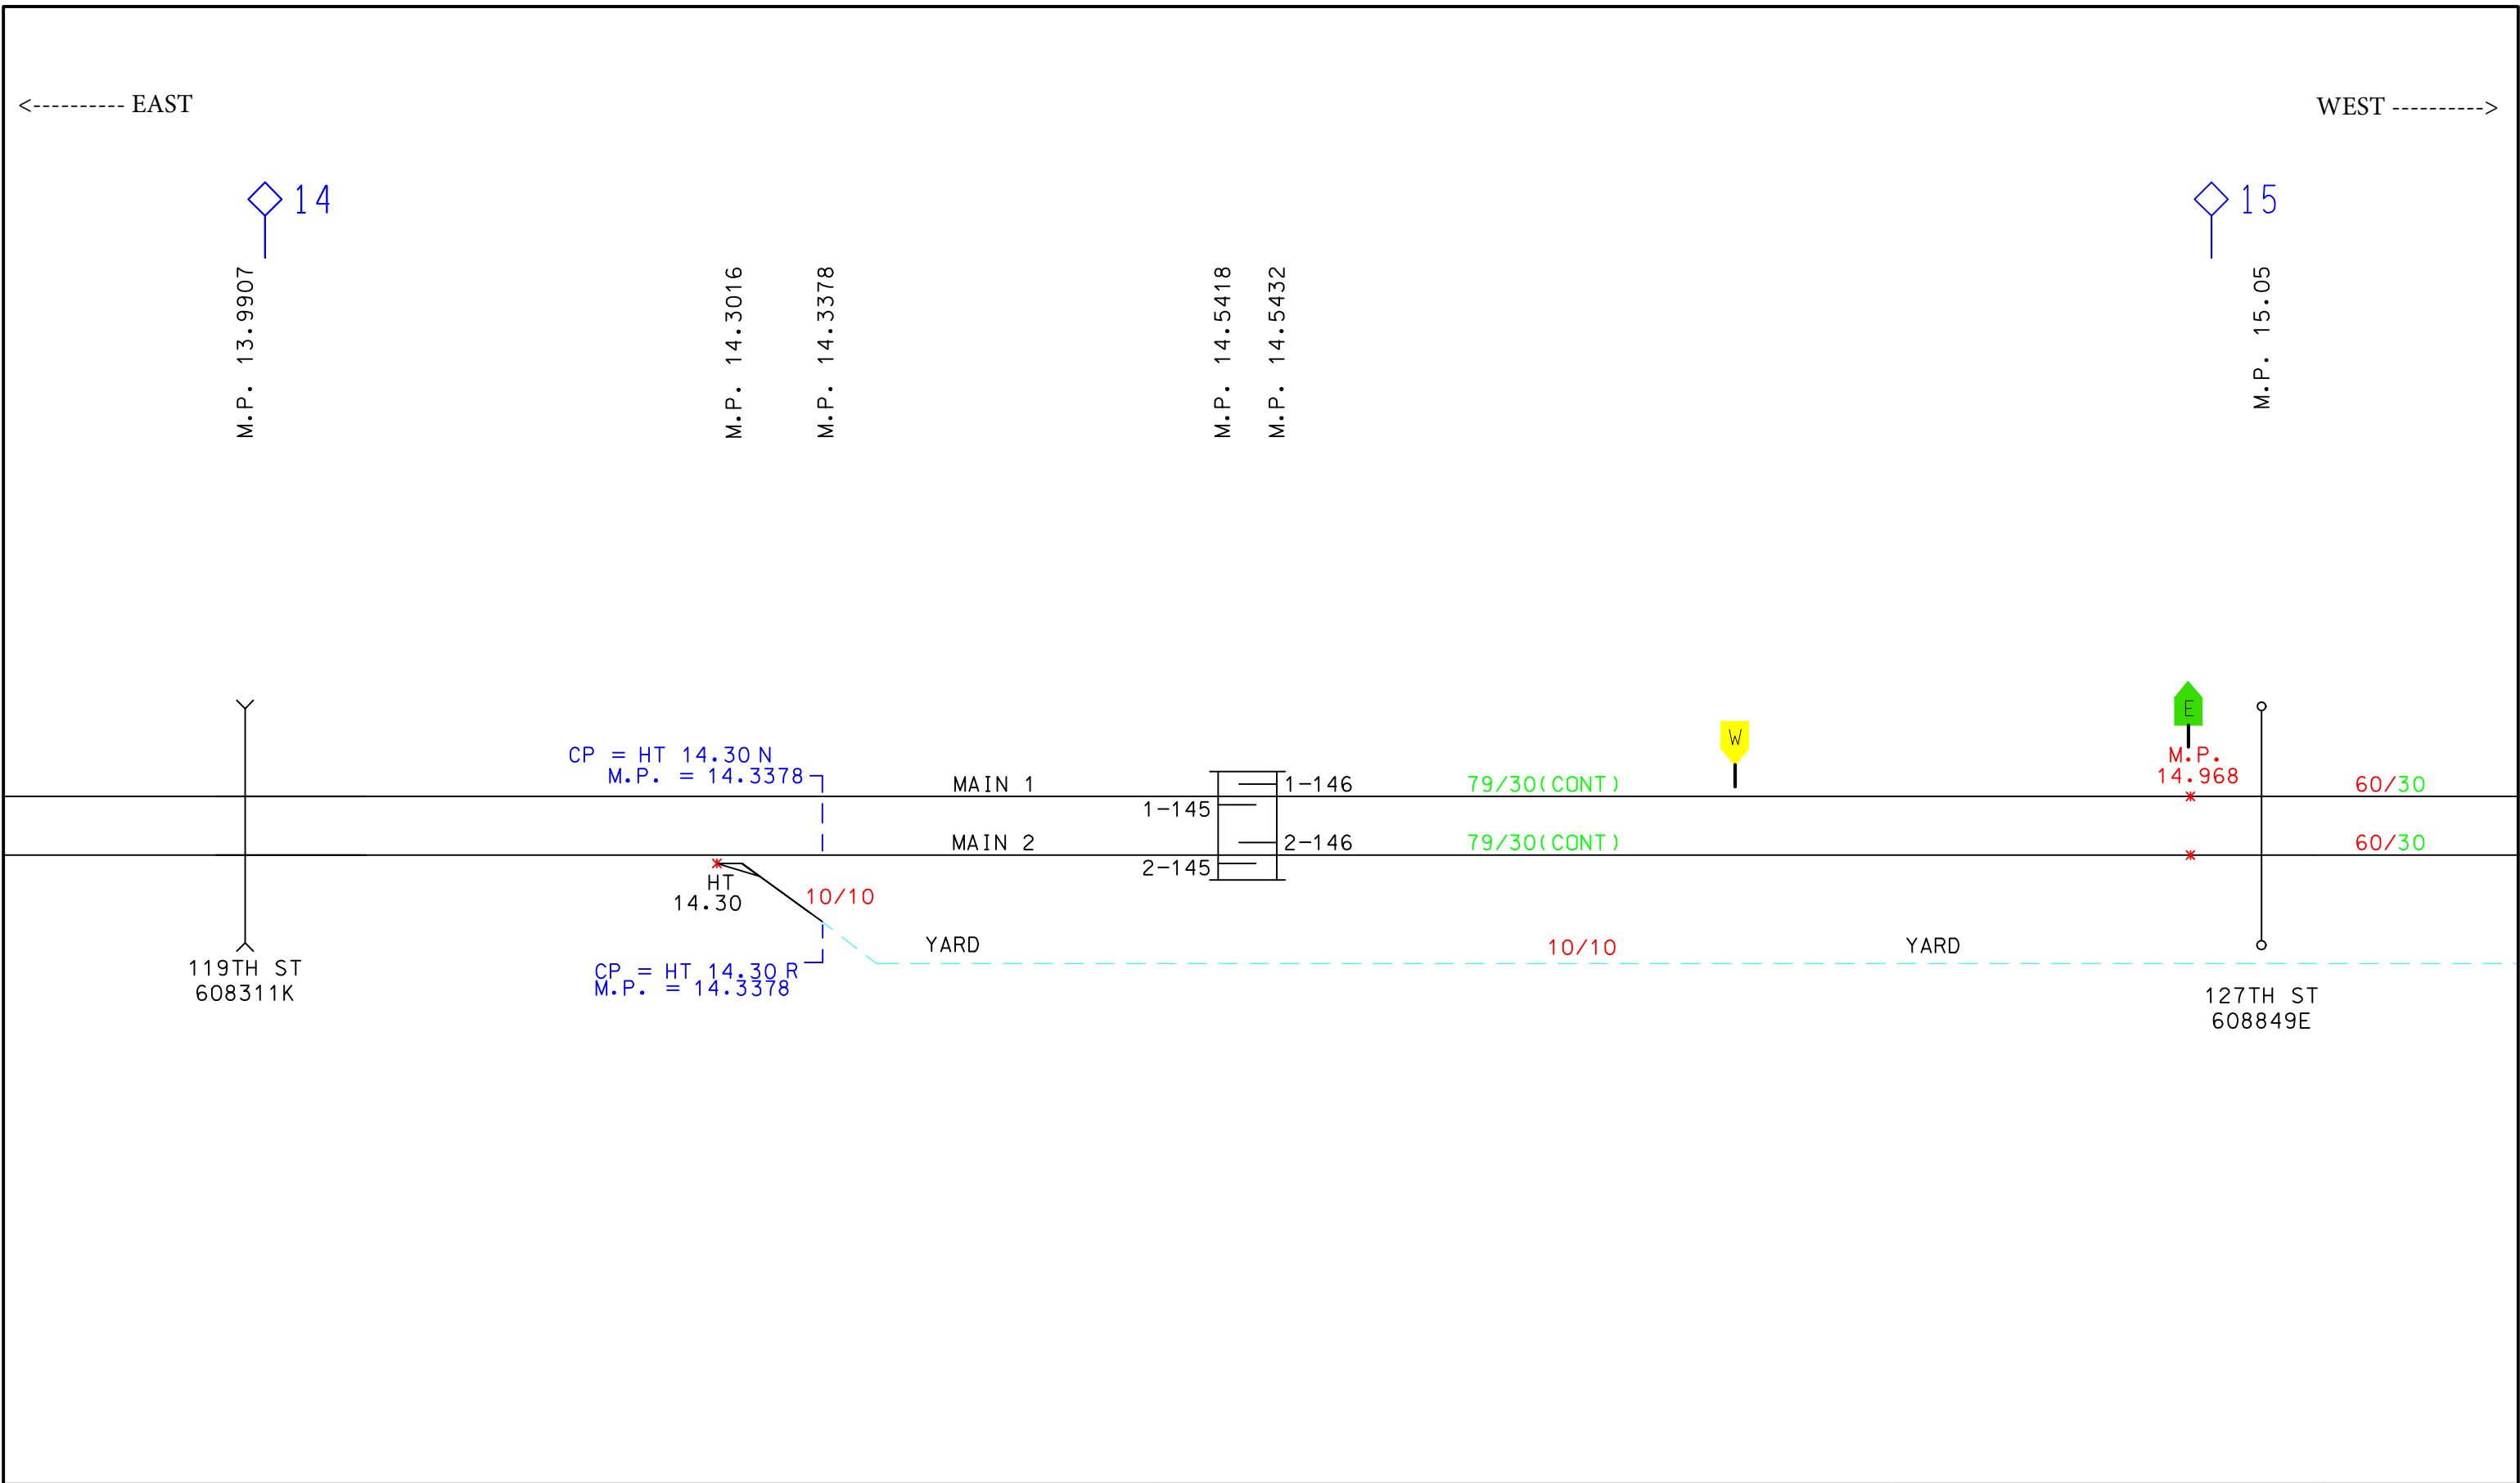

15

M.P. 15.05

M.P. 15.5300  
M.P. 15.5318  
M.P. 15.5320  
M.P. 15.5362

M.P. 15.5668

M.P. 15.5796

M.P. 15.5933

M.P. 15.5985  
M.P. 15.6000  
M.P. 15.6200  
M.P. 15.6215

M.P. 15.6695  
M.P. 15.6820  
M.P. 15.6869  
M.P. 15.6898  
M.P. 15.707  
M.P. 15.709  
M.P. 15.7156

M.P. 15.7612  
M.P. 15.7632  
M.P. 15.7719

M.P. 15.7775

M.P. 15.7924

M.P. 15.8103

M.P. 15.8115  
M.P. 15.8599  
M.P. 15.86

M.P. 15.8679  
M.P. 15.8688  
M.P. 15.8776

M.P. 15.8824

M.P. 15.9713

M.P. 15.9998  
M.P. 16.0352

M.P. 16.0361  
M.P. 16.0547


M.P. 16.06

M.P. 16.098

16

"CP BURR OAK"  
(BUR)

"CP WESTERN AVENUE"  
(WESTRN)

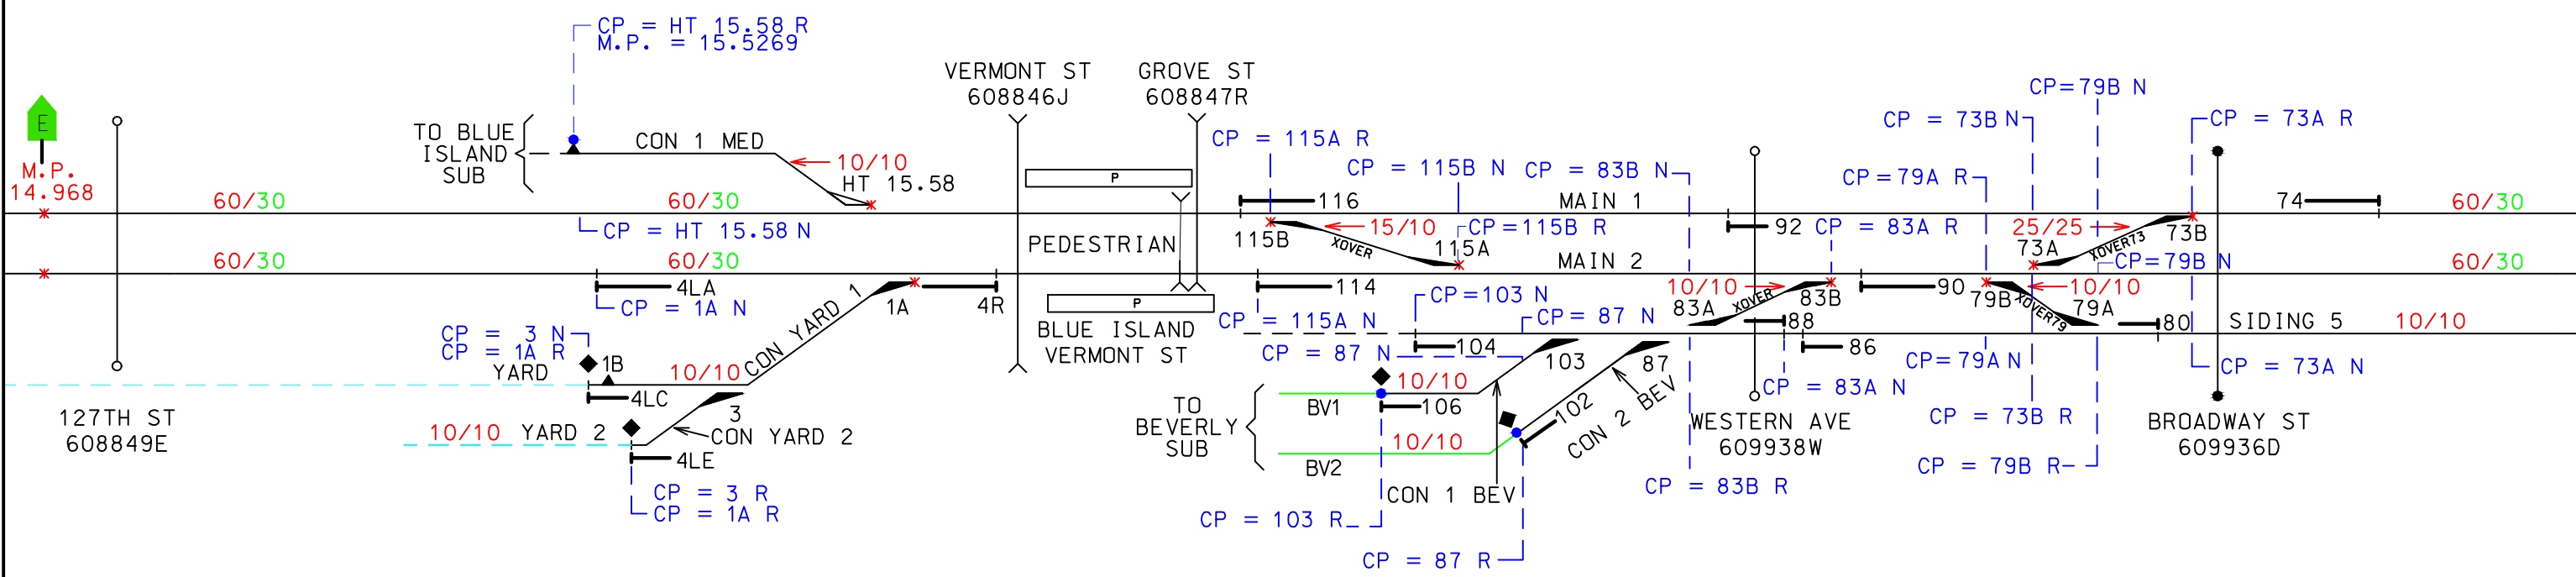



16

17 

|      |         |
|------|---------|
| M.P. | 16.67   |
| M.P. | 16.6841 |
| M.P. | 16.74   |
| M.P. | 16.7766 |
| M.P. | 16.786  |


|      |         |
|------|---------|
| M.P. | 16.9477 |
| M.P. | 16.9547 |
| M.P. | 16.9595 |
| M.P. | 16.9671 |
| M.P. | 16.9741 |
| M.P. | 16.9728 |

[illegible]

| REV. | DATE     | BY | DESCRIPTION                                                    | REV. | DATE     | BY | DESCRIPTION                                                     |
|------|----------|----|----------------------------------------------------------------|------|----------|----|-----------------------------------------------------------------|
| 29   | 10/05/22 | JA | REVISED PER CHANGES TO CP WESTERN, INTERCHANGE AND ROBBINS     | 34   | 09/17/24 | JE | REVISED PER 16TH ST DIAMOND REPLACEMENT                         |
| 30   | 12/21/22 | JE | REVISED PER CHANGES TO SPEED OF XOVER 115 AT WESTERN           | 35   | 11/11/24 | JE | REVISED PER SPEED CHANGE TO 10 MPH ACROSS UD TOWER DIAMONDS     |
| 31   | 05/05/23 | JA | REVISED NONCOMM TRACK AT CHI TERM & SPEED AT WESTERN 115 XOVER | 36   | 01/08/25 | JE | REVISED PER AUDIT RUN CHANGES, CRs for PEDs and PLATFORMS       |
| 32   | 01/08/24 | JE | REVISED PER CF AUDIT CHANGES AT 80TH AVE AND 105TH ST          | 37   | 02/04/25 | ES | REVISED TO UPDATE SWITCHES TO ELECTRIC LOCK                     |
| 33   | 01/08/24 | JA | REVISED PER REMOVAL OF CON1SCAL TRACK AT 16TH ST               | 38   | 02/06/25 | JE | REVISED TO UPDATE FREIGHT SPEEDS TO 40MPH BETWEEN ROBBINS & EJA |

**Metra**



SHEET NO. 17

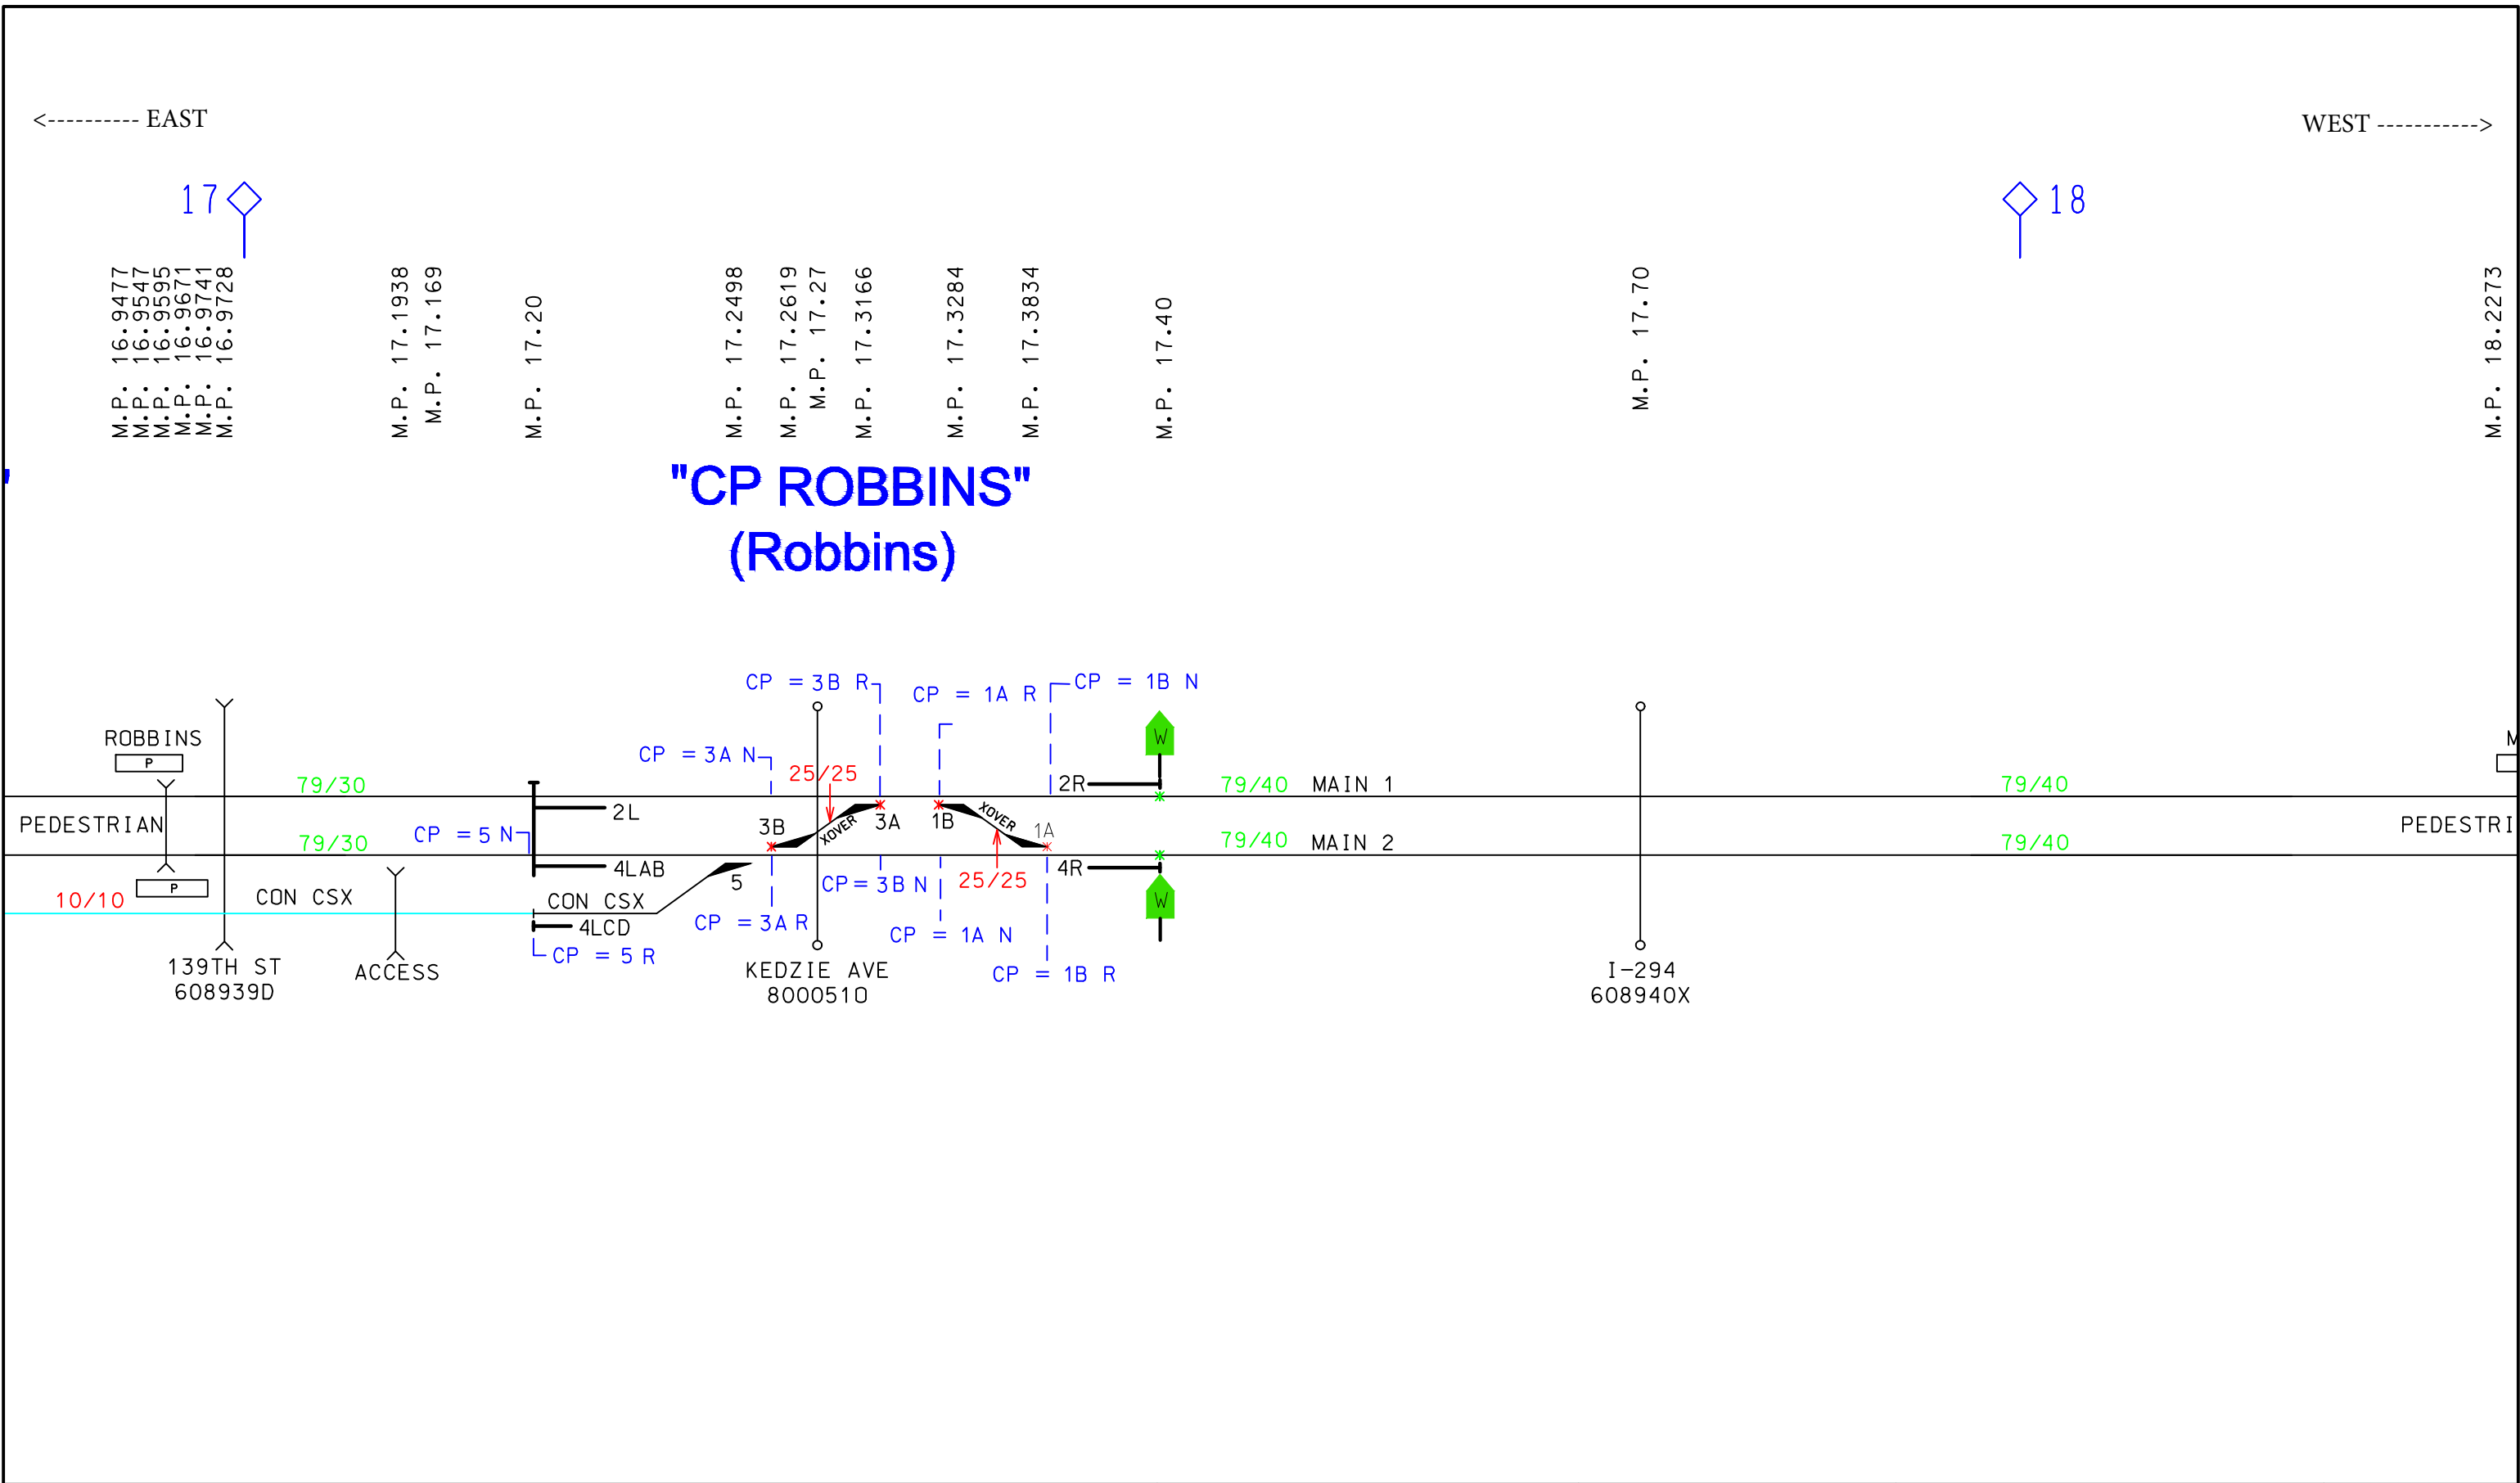

| REV. | DATE     | BY | DESCRIPTION                                                    | REV. | DATE     | BY | DESCRIPTION                                                    | DISCLOSURE:<br>CHARTS ARE A VISUAL REPRESENTATION OF<br>THE SUBDIV AND ARE TO BE USED FOR PTC<br>SUBDIV PURPOSES ONLY | <div>Metra</div> <div>547 W. JACKSON BLVD.<br/>CHICAGO, IL. 60661</div> | METRA SUBDIV FILE<br>MASTER DRAWING<br>JOLIET SUB<br>ILLINOIS<br>M.P.17.0 - 18.0 | SHEET NO. 18 |
|------|----------|----|----------------------------------------------------------------|------|----------|----|----------------------------------------------------------------|---|-------------------------------------------------------------------------|----------------------------------------------------------------------------------|--------------|
| 29   | 10/05/22 | JA | REVISED PER CHANGES TO CP WESTERN, INTERCHANGE AND ROBBINS     | 34   | 09/17/24 | JE | REVISED PER 16TH ST DIAMOND REPLACEMENT                        |   |                                                                         |                                                                                  |              |
| 30   | 12/21/22 | JE | REVISED PER CHANGES TO SPEED OF XOVER 115 AT WESTERN           | 35   | 11/11/24 | JE | REVISED PER SPEED CHANGE TO 10 MPH ACROSS UD TOWER DIAMONDS    |   |                                                                         |                                                                                  |              |
| 31   | 05/05/23 | JA | REVISED NONCOMM TRACK AT CHI TERM & SPEED AT WESTERN 115 XOVER | 36   | 01/08/25 | JE | REVISED PER AUDIT RUN CHANGES, CRs for PEDs and PLATFORMS      |   |                                                                         |                                                                                  |              |
| 32   | 01/08/24 | JE | REVISED PER CF AUDIT CHANGES AT 80TH AVE AND 105TH ST          | 37   | 02/04/25 | ES | REVISED TO UPDATE SWITCHES TO ELECTRIC LOCK                    |   |                                                                         |                                                                                  |              |
| 33   | 01/08/24 | JA | REVISED PER REMOVAL OF CON1SCAL TRACK AT 16TH ST               | 38   | 02/06/25 | JE | REVISED TO UPDATE FREIGHT SPEEDS TO 40MPH BETWEEN ROBBINS & EJ |   |                                                                         |                                                                                  |              |

<----- EAST

WEST ----->

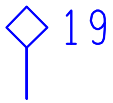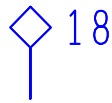

M.P. 18.2273

M.P. 18.332

M.P. 18.3372


M.P. 18.3883

M.P. 18.3890

M.P. 18.4903

M.P. 18.7501

M.P. 18.7589

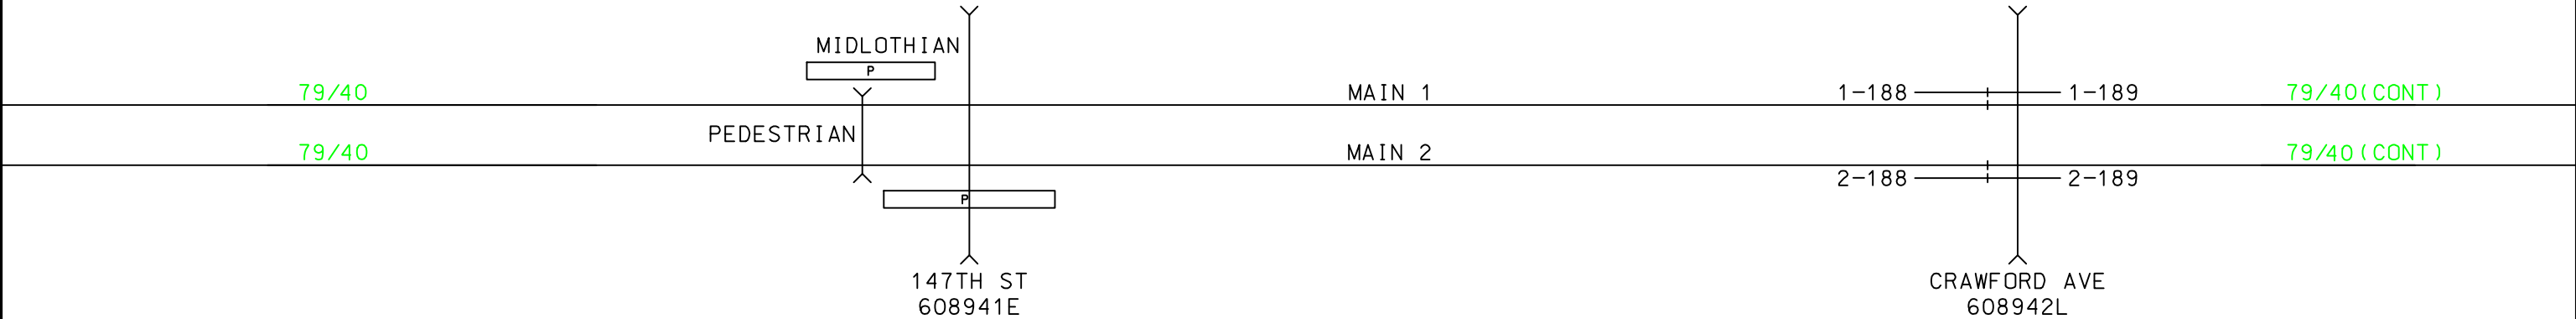

<----- EAST

WEST ----->

19

20

189

79/40 (CONT )

MAIN 1

79/40 (CONT )

189

79/40 (CONT )

MAIN 2

79/40 (CONT )

E

| REV. | DATE     | BY | DESCRIPTION                                                    | REV. | DATE     | BY | DESCRIPTION                                                     |
|------|----------|----|----------------------------------------------------------------|------|----------|----|-----------------------------------------------------------------|
| 29   | 10/05/22 | JA | REVISED PER CHANGES TO CP WESTERN, INTERCHANGE AND ROBBINS     | 34   | 09/17/24 | JE | REVISED PER 16TH ST DIAMOND REPLACEMENT                         |
| 30   | 12/21/22 | JE | REVISED PER CHANGES TO SPEED OF XOVER 115 AT WESTERN           | 35   | 11/11/24 | JE | REVISED PER SPEED CHANGE TO 10 MPH ACROSS UD TOWER DIAMONDS     |
| 31   | 05/05/23 | JA | REVISED NONCOMM TRACK AT CHI TERM & SPEED AT WESTERN 115 XOVER | 36   | 01/08/25 | JE | REVISED PER AUDIT RUN CHANGES, CRs for PEDs and PLATFORMS       |
| 32   | 01/08/24 | JE | REVISED PER CF AUDIT CHANGES AT 80TH AVE AND 105TH ST          | 37   | 02/04/25 | ES | REVISED TO UPDATE SWITCHES TO ELECTRIC LOCK                     |
| 33   | 01/08/24 | JA | REVISED PER REMOVAL OF CON1SCAL TRACK AT 16TH ST               | 38   | 02/06/25 | JE | REVISED TO UPDATE FREIGHT SPEEDS TO 40MPH BETWEEN ROBBINS & EJE |

DISCLOSURE:  
CHARTS ARE A VISUAL REPRESENTATION OF  
THE SUBDIV AND ARE TO BE USED FOR PTC  
SUBDIV PURPOSES ONLY




547 W. JACKSON BLVD.  
CHICAGO, IL. 60661

METRA SUBDIV FILE  
MASTER DRAWING  
JOLIET SUB  
ILLINOIS  
M.P.19.0 - 20.0

SHEET NO. 20

<----- EAST

WEST ----->

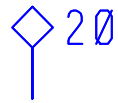

M.P. 20.20

M.P. 20.2341

M.P. 20.2992

M.P. 20.3893

M.P. 20.5279

M.P. 20.328


M.P. 20.3772

M.P. 20.4564

M.P. 20.5026


M.P. 20.5157

M.P. 20.9518

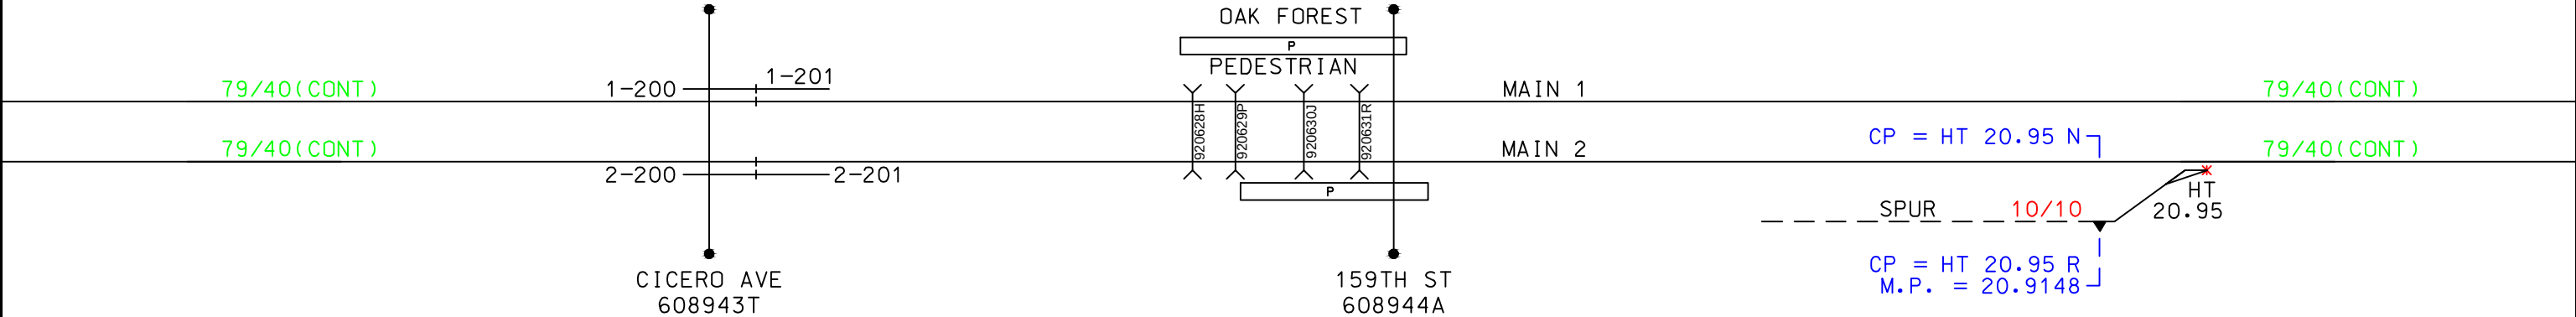


<----- EAST

WEST ----->

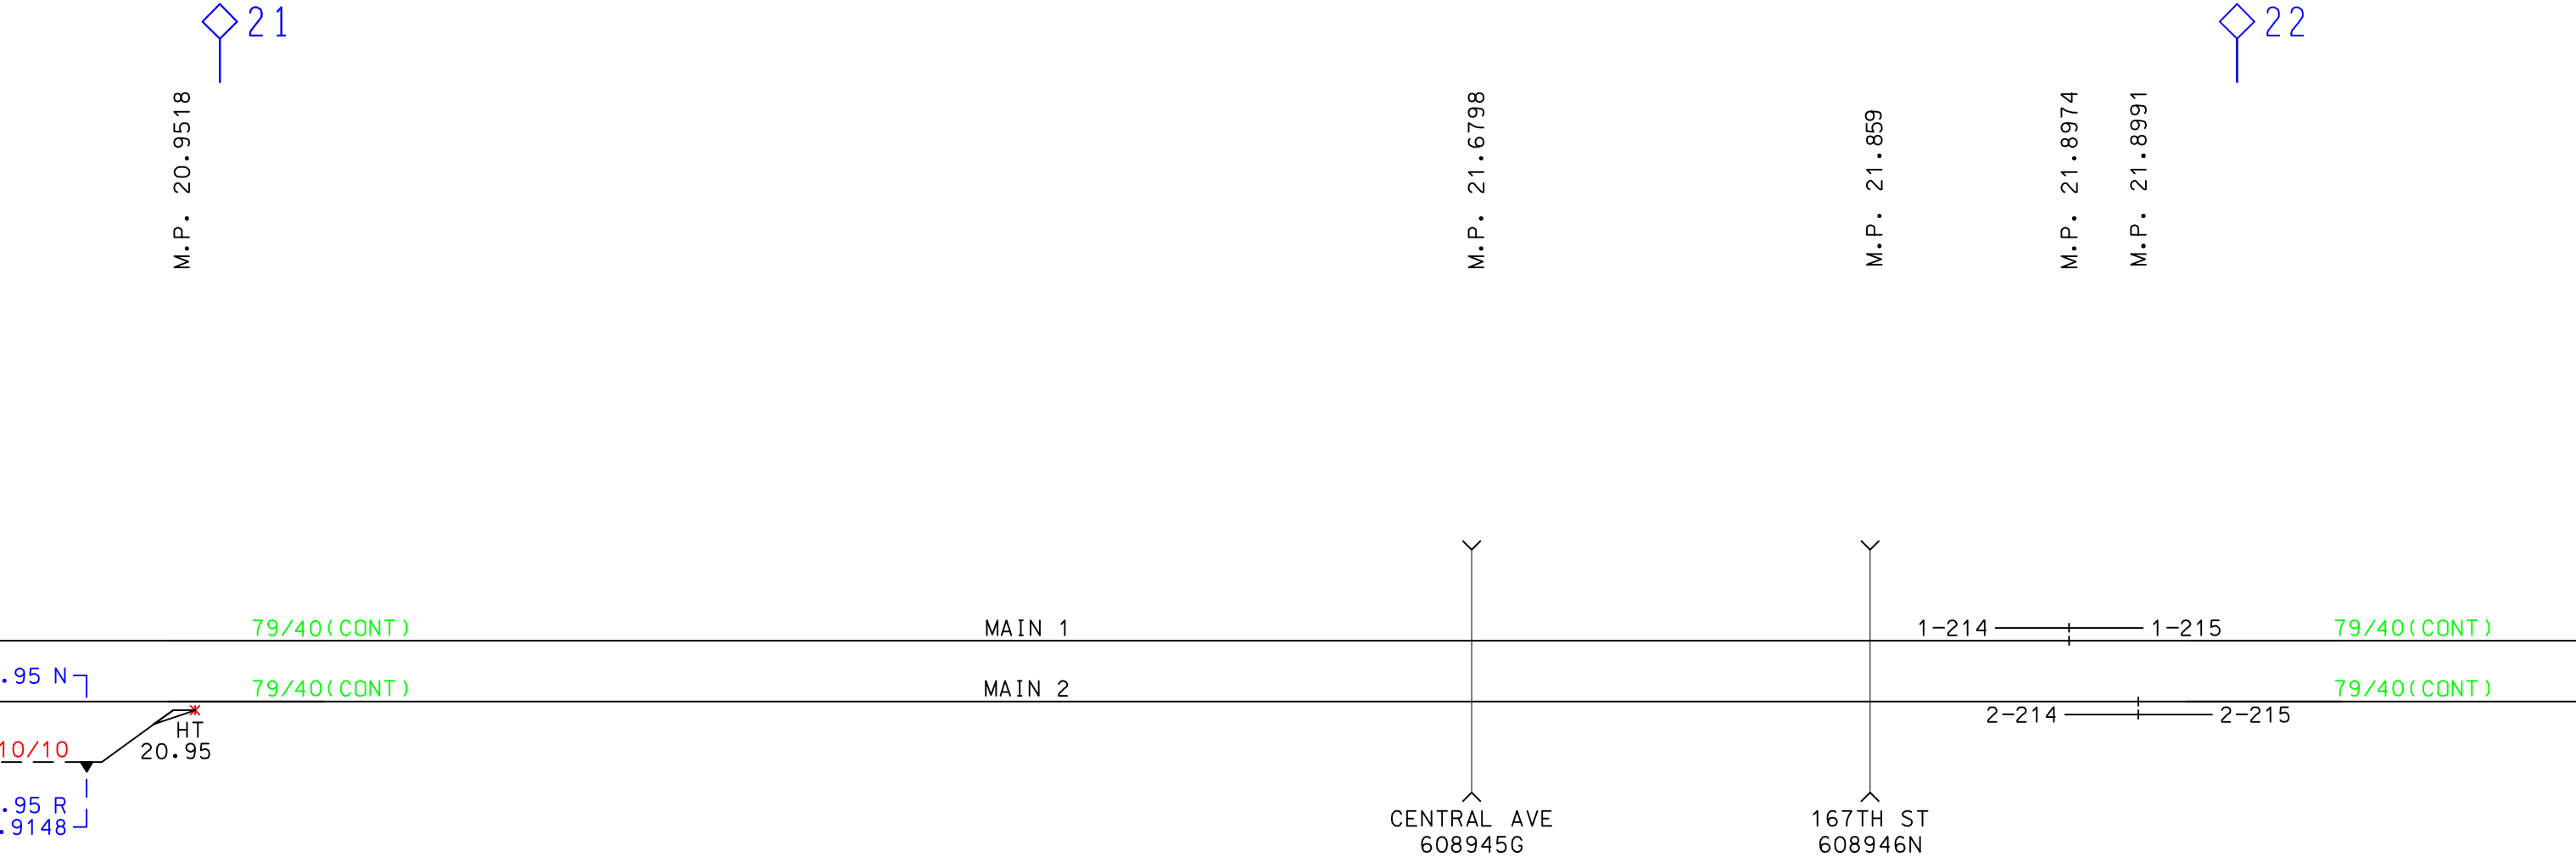



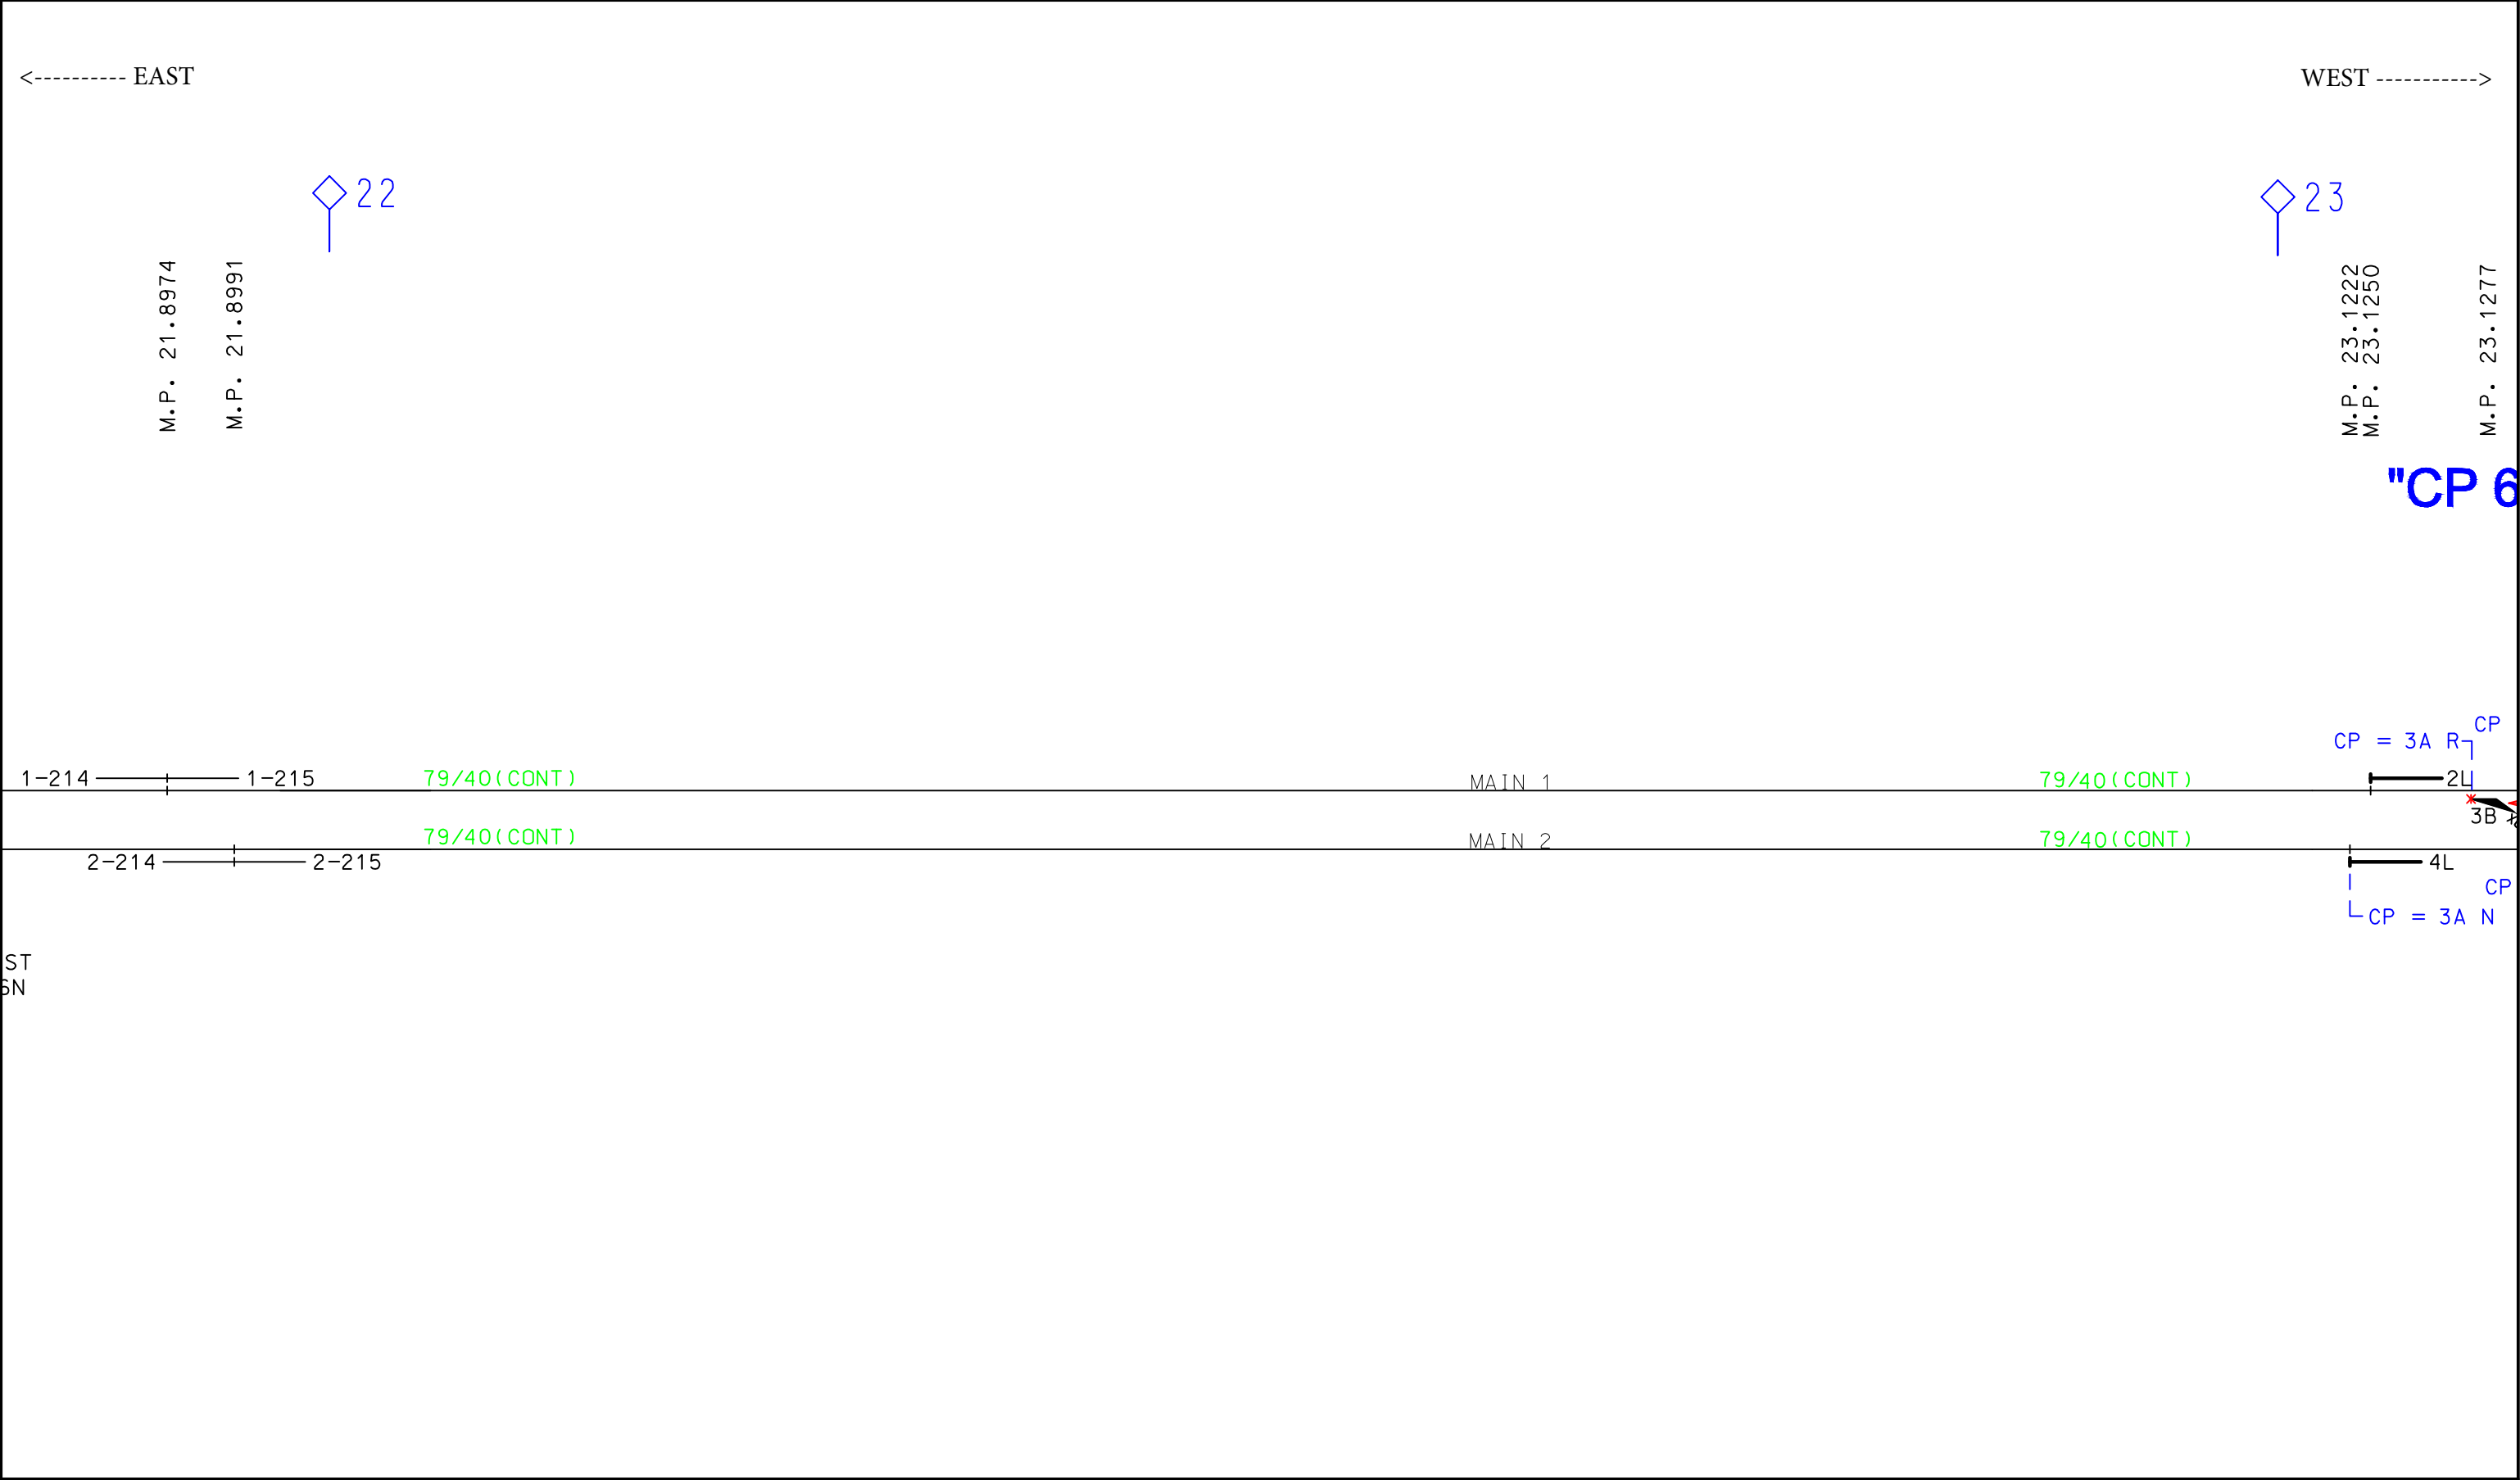

<----- EAST

WEST ----->

23

24

M.P. 23.1222  
M.P. 23.1250

M.P. 23.1277

M.P. 23.1971

M.P. 23.2143

M.P. 23.2836

M.P. 23.2944

M.P. 23.3001  
M.P. 23.3081


M.P. 23.4054

M.P. 23.4824  
M.P. 23.4820  
M.P. 23.4845

M.P. 23.5436

M.P. 24.00


"CP 66TH COURT"  
(66th)

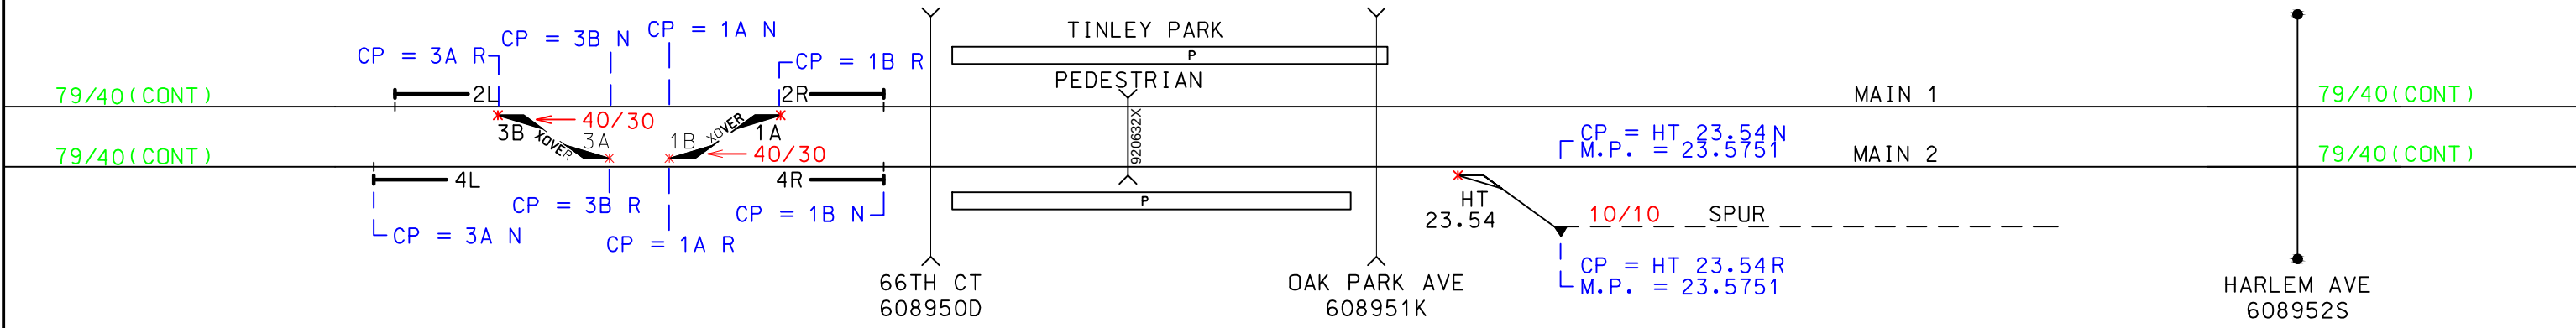




<----- EAST

WEST ----->

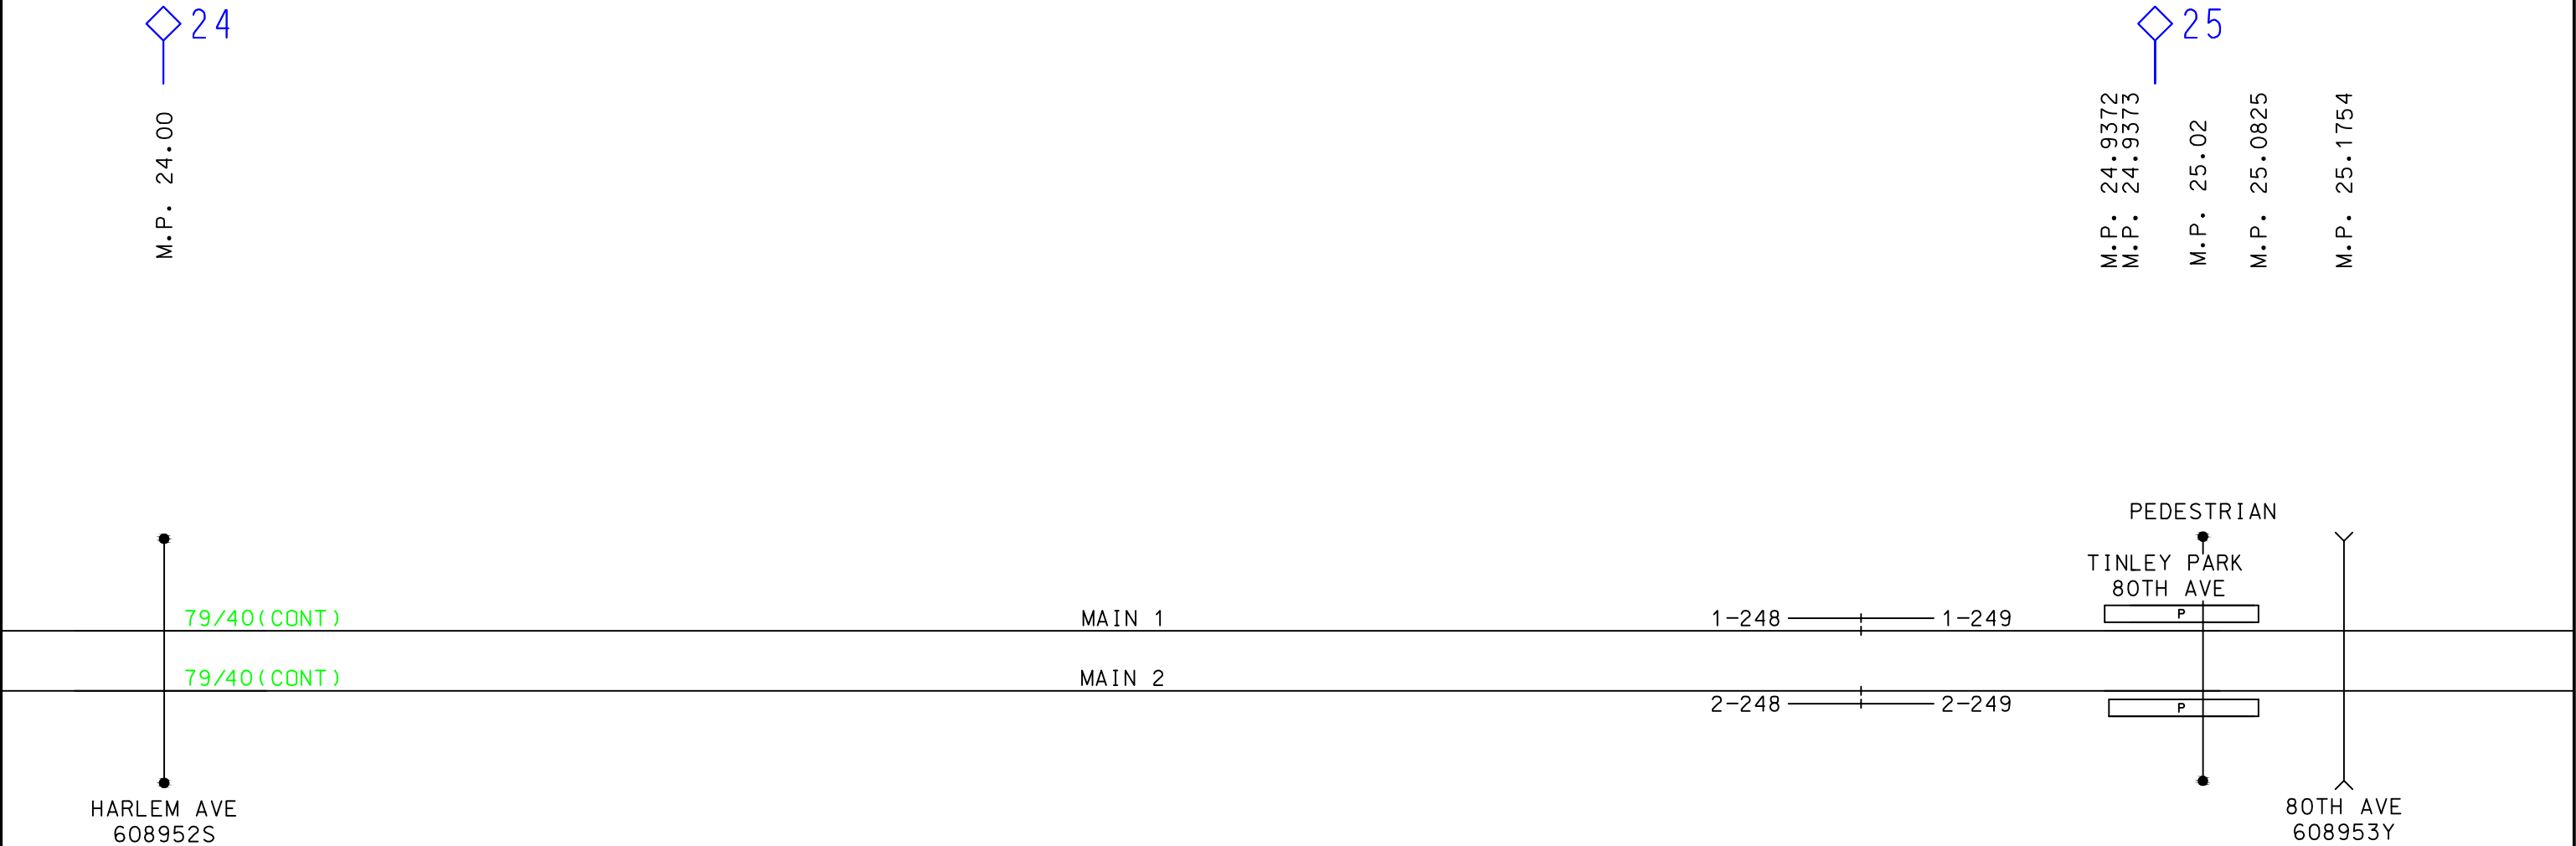


<----- EAST

WEST ----->

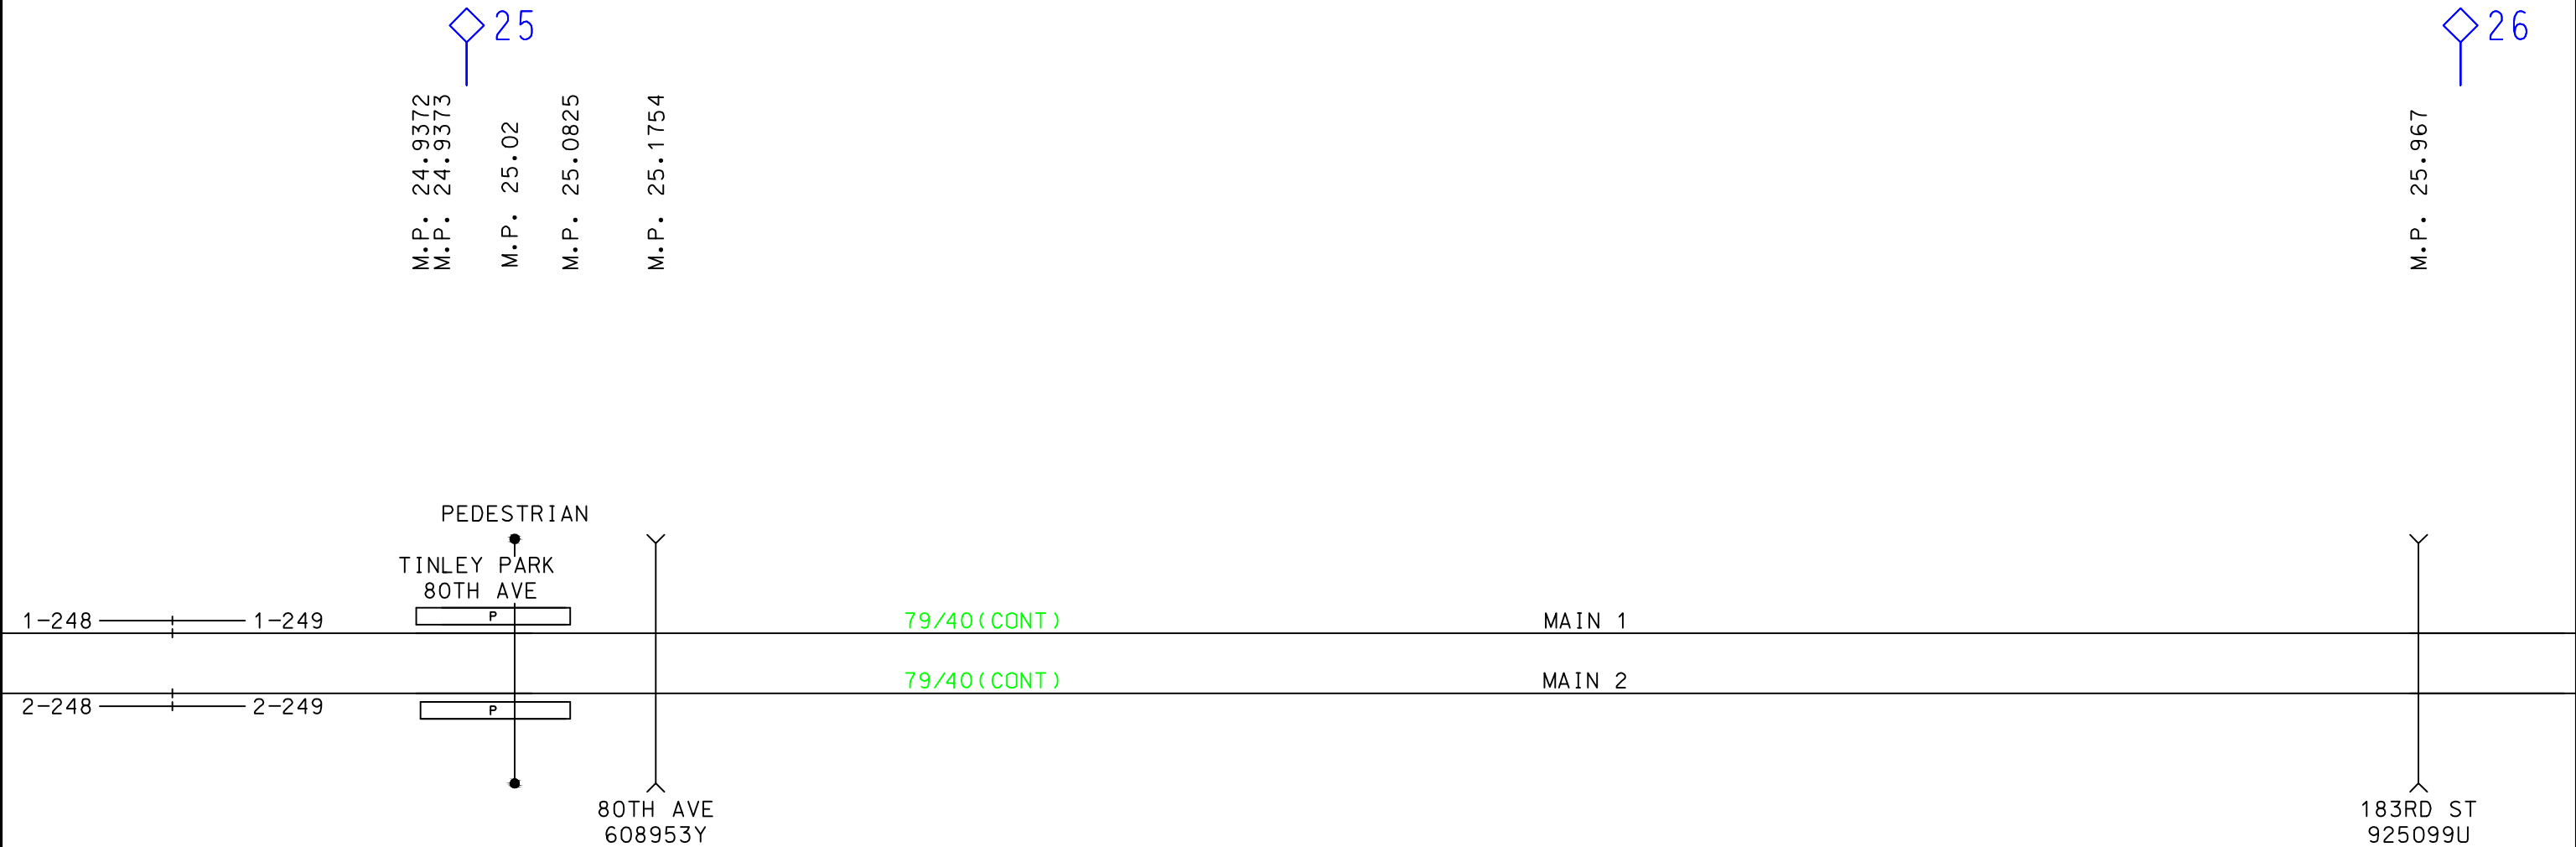

<----- EAST

WEST ----->

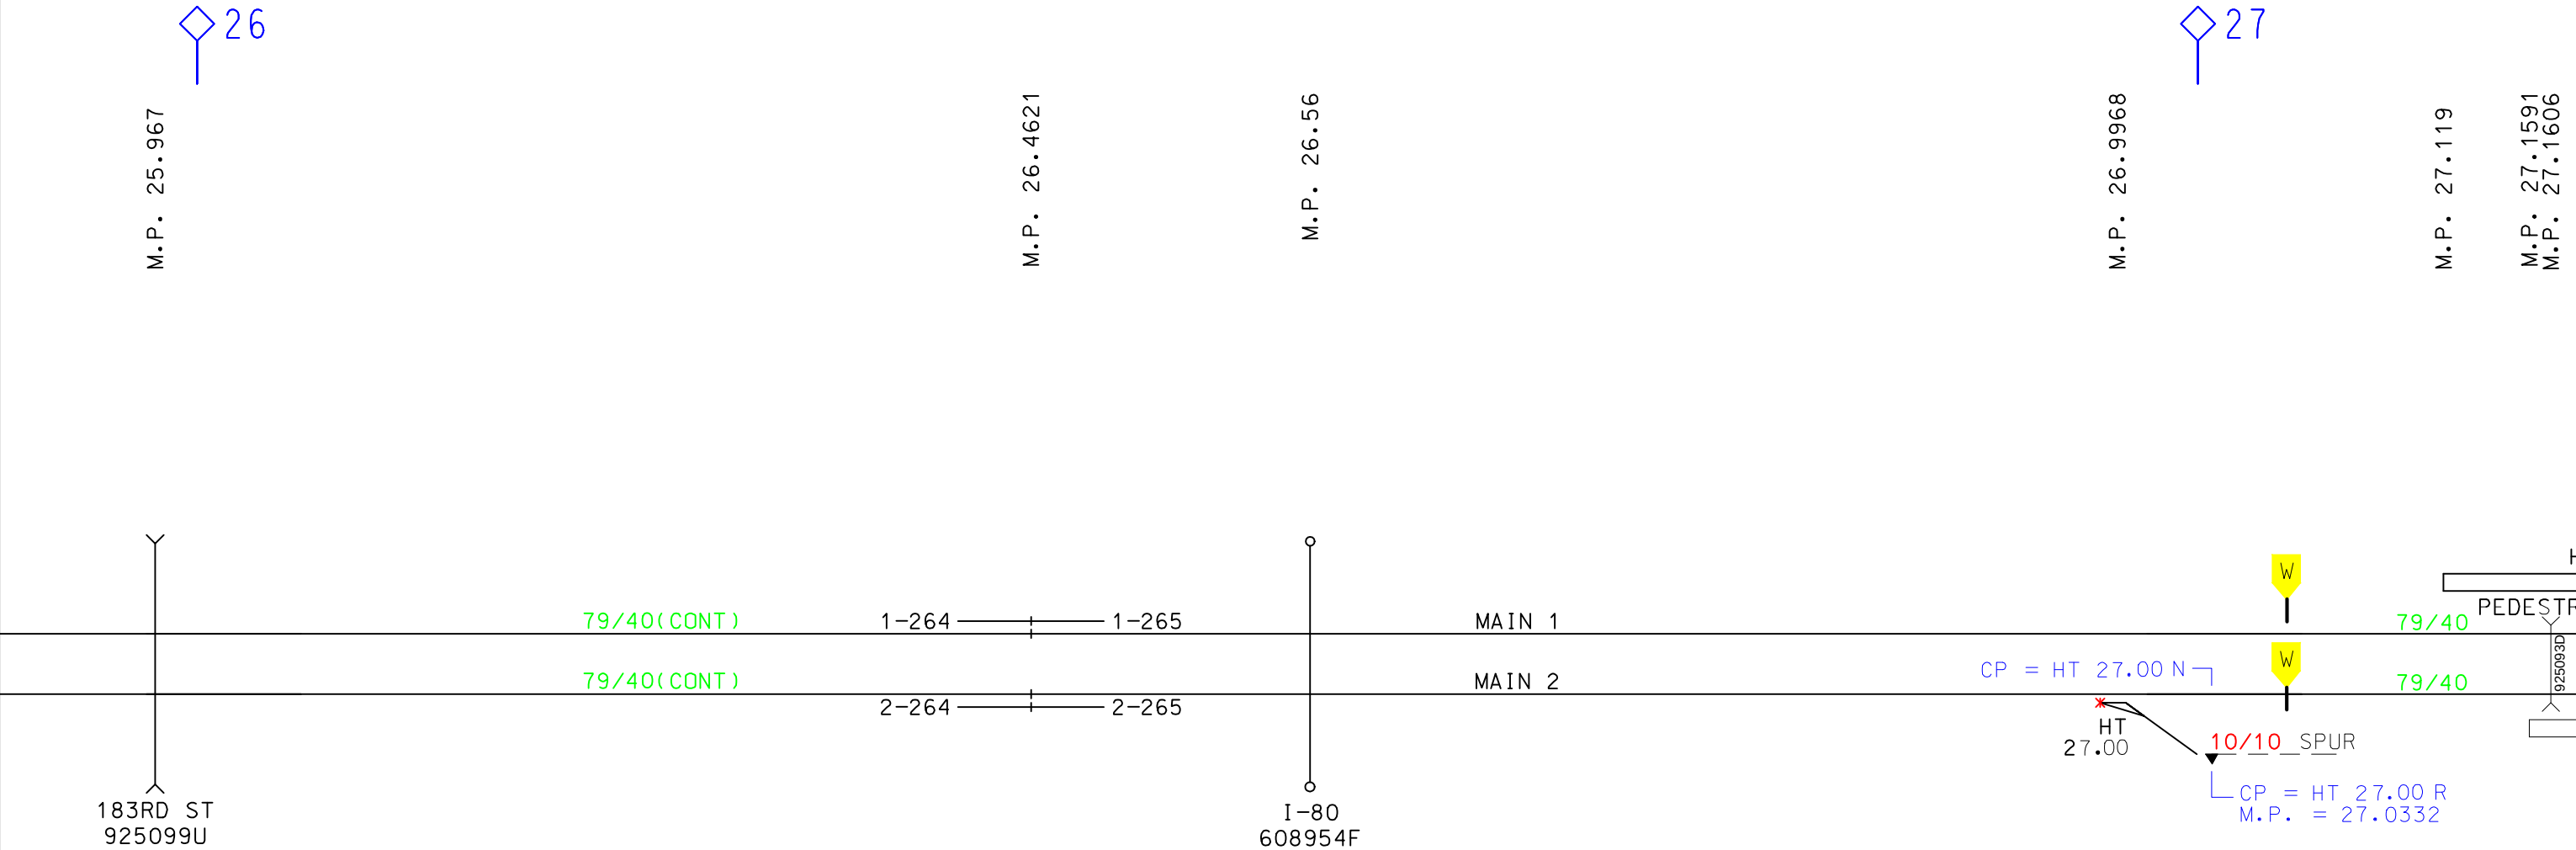

| REV. | DATE     | BY | DESCRIPTION                                                    | REV. | DATE     | BY | DESCRIPTION                                                     |
|------|----------|----|----------------------------------------------------------------|------|----------|----|-----------------------------------------------------------------|
| 29   | 10/05/22 | JA | REVISED PER CHANGES TO CP WESTERN, INTERCHANGE AND ROBBINS     | 34   | 09/17/24 | JE | REVISED PER 16TH ST DIAMOND REPLACEMENT                         |
| 30   | 12/21/22 | JE | REVISED PER CHANGES TO SPEED OF XOVER 115 AT WESTERN           | 35   | 11/11/24 | JE | REVISED PER SPEED CHANGE TO 10 MPH ACROSS UD TOWER DIAMONDS     |
| 31   | 05/05/23 | JA | REVISED NONCOMM TRACK AT CHI TERM & SPEED AT WESTERN 115 XOVER | 36   | 01/08/25 | JE | REVISED PER AUDIT RUN CHANGES, CRs for PEDs and PLATFORMS       |
| 32   | 01/08/24 | JE | REVISED PER CF AUDIT CHANGES AT 80TH AVE AND 105TH ST          | 37   | 02/04/25 | ES | REVISED TO UPDATE SWITCHES TO ELECTRIC LOCK                     |
| 33   | 01/08/24 | JA | REVISED PER REMOVAL OF CON1SCAL TRACK AT 16TH ST               | 38   | 02/06/25 | JE | REVISED TO UPDATE FREIGHT SPEEDS TO 40MPH BETWEEN ROBBINS & EJA |

DISCLOSURE:  
CHARTS ARE A VISUAL REPRESENTATION OF  
THE SUBDIV AND ARE TO BE USED FOR PTC  
SUBDIV PURPOSES ONLY




METRA SUBDIV FILE  
MASTER DRAWING  
JOLIET SUB  
ILLINOIS  
M.P.26.0 - 27.0

SHEET NO. 27

<----- EAST

WEST ----->

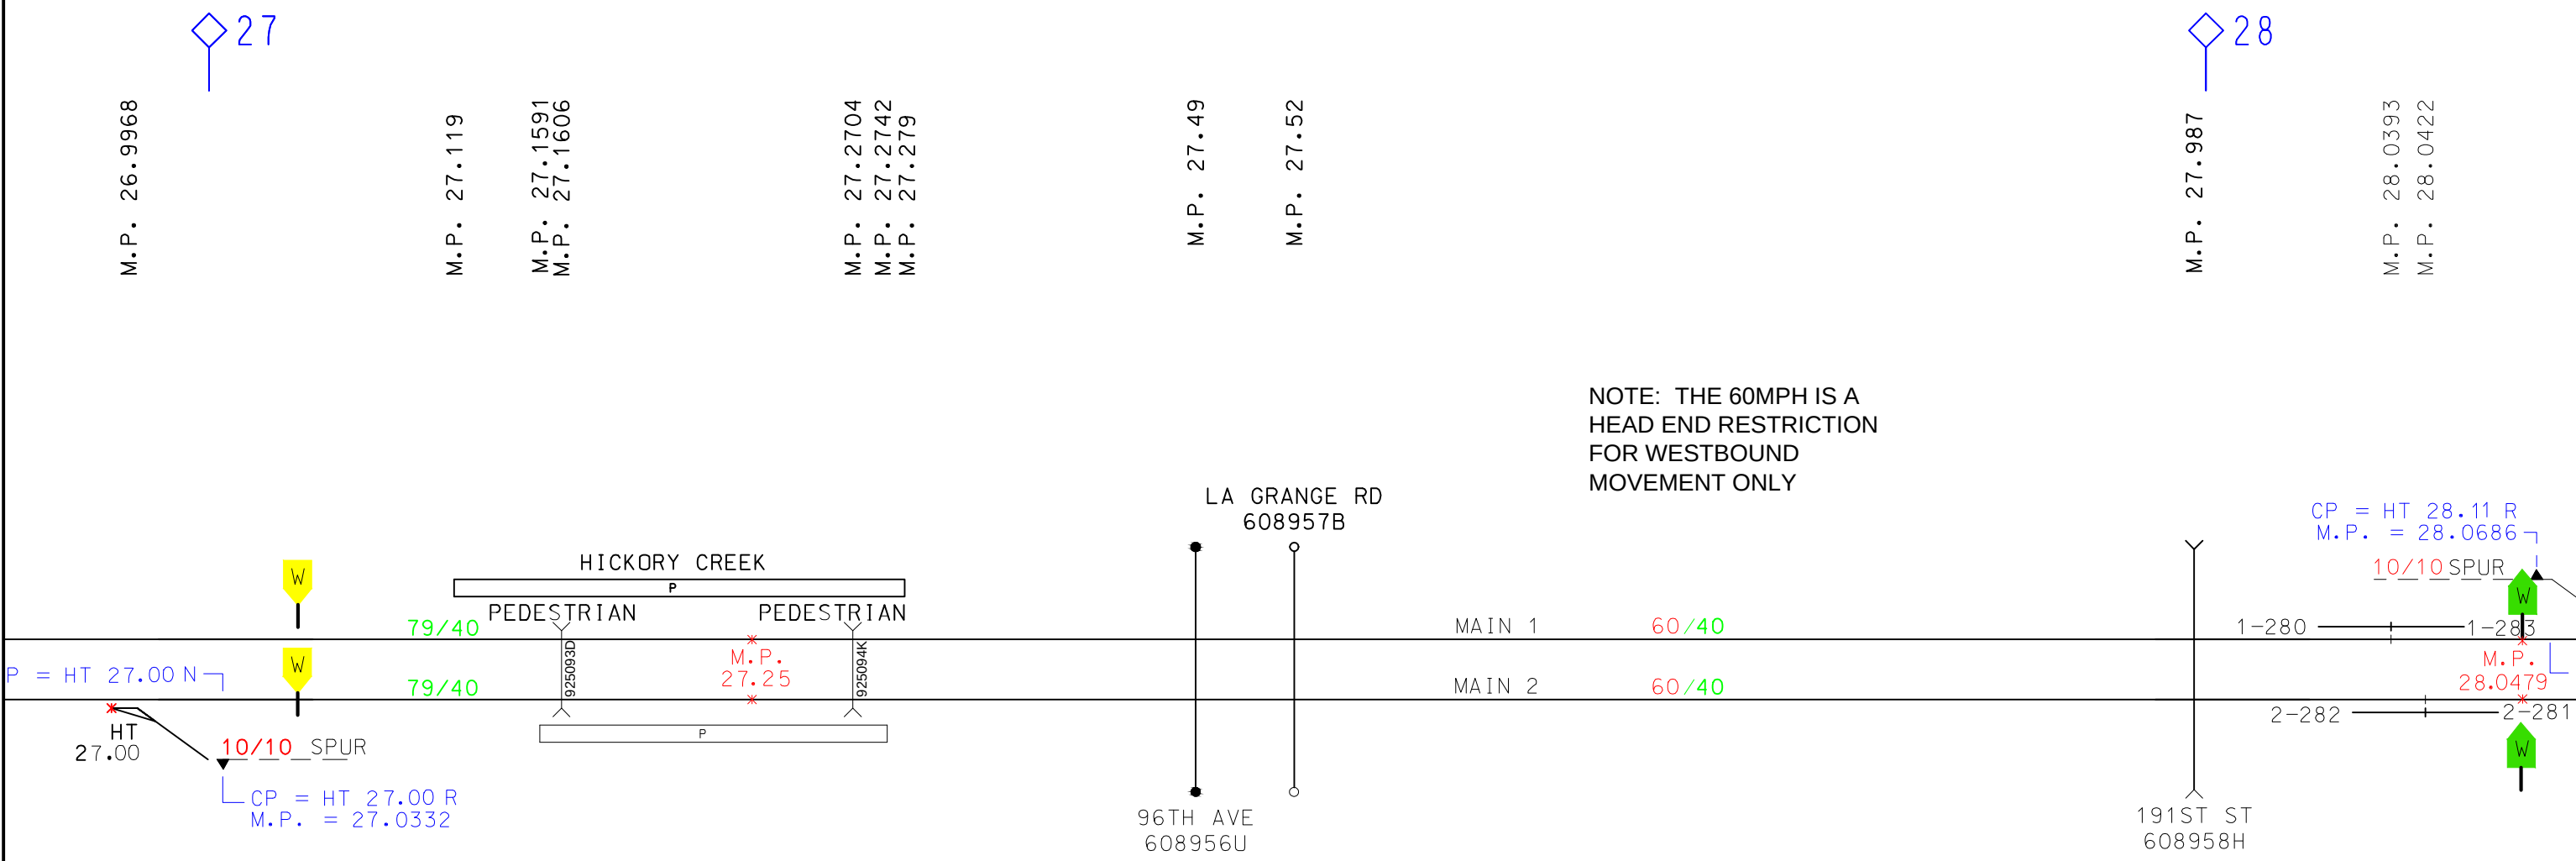

<----- EAST


WEST -----&gt;




M.P. 27.987

M.P. 28.0393  
M.P. 28.0422

M.P. 28.1056

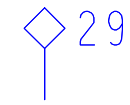

M.P. 29.2144

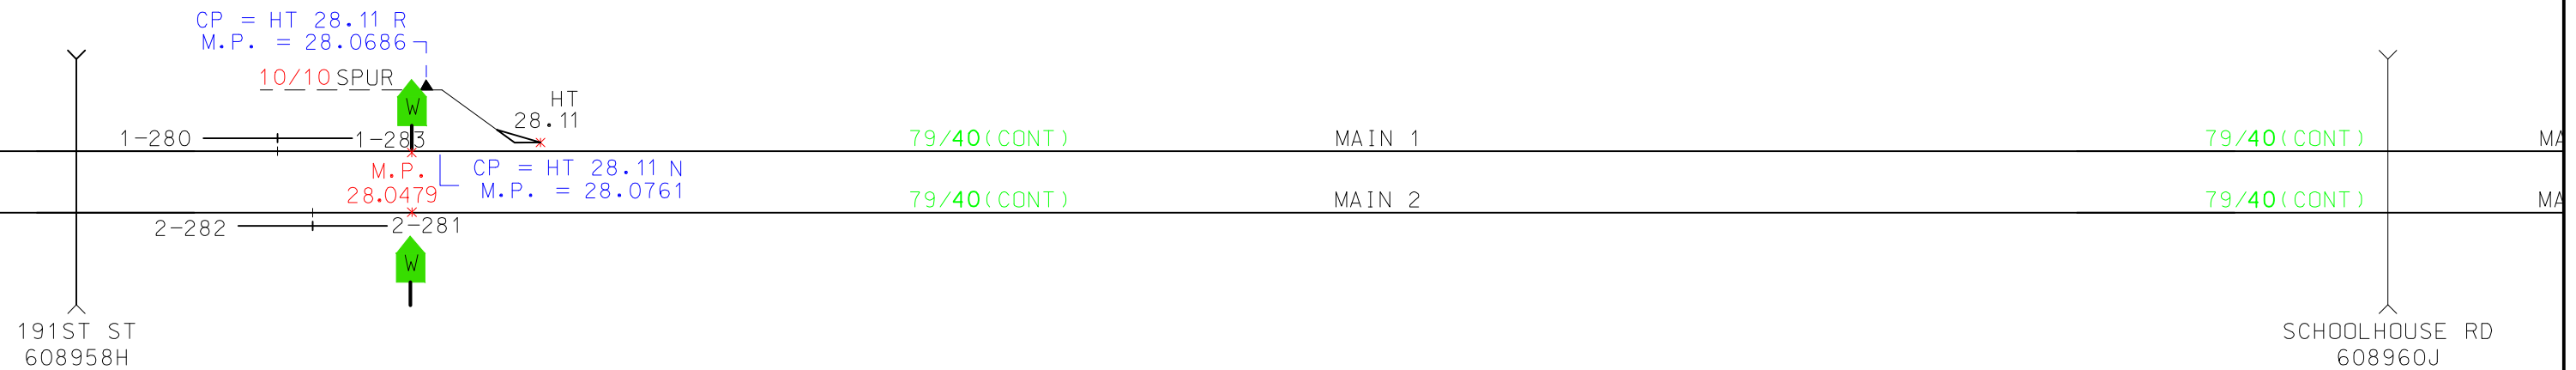

| REV. | DATE     | BY | DESCRIPTION                                                    | REV. | DATE     | BY | DESCRIPTION                                                     |
|------|----------|----|----------------------------------------------------------------|------|----------|----|-----------------------------------------------------------------|
| 29   | 10/05/22 | JA | REVISED PER CHANGES TO CP WESTERN, INTERCHANGE AND ROBBINS     | 34   | 09/17/24 | JE | REVISED PER 16TH ST DIAMOND REPLACEMENT                         |
| 30   | 12/21/22 | JE | REVISED PER CHANGES TO SPEED OF XOVER 115 AT WESTERN           | 35   | 11/11/24 | JE | REVISED PER SPEED CHANGE TO 10 MPH ACROSS UD TOWER DIAMONDS     |
| 31   | 05/05/23 | JA | REVISED NONCOMM TRACK AT CHI TERM & SPEED AT WESTERN 115 XOVER | 36   | 01/08/25 | JE | REVISED PER AUDIT RUN CHANGES, CRs for PEDs and PLATFORMS       |
| 32   | 01/08/24 | JE | REVISED PER CF AUDIT CHANGES AT 80TH AVE AND 105TH ST          | 37   | 02/04/25 | ES | REVISED TO UPDATE SWITCHES TO ELECTRIC LOCK                     |
| 33   | 01/08/24 | JA | REVISED PER REMOVAL OF CON1SCAL TRACK AT 16TH ST               | 38   | 02/06/25 | JE | REVISED TO UPDATE FREIGHT SPEEDS TO 40MPH BETWEEN ROBBINS & EJA |

DISCLOSURE:  
CHARTS ARE A VISUAL REPRESENTATION OF  
THE SUBDIV AND ARE TO BE USED FOR PTC  
SUBDIV PURPOSES ONLY



METRA SUBDIV FILE  
MASTER DRAWING  
JOLIET SUB  
ILLINOIS  
M.P.28.0 - 29.0

SHEET NO. 29

<----- EAST

WEST ----->

29

30


M.P. 29.2144

M.P. 29.5674  
M.P. 29.5701  
M.P. 29.5862  
M.P. 29.5886

M.P. 29.603  
M.P. 29.6121  
M.P. 29.6424  
M.P. 29.6567  
M.P. 29.7091  
M.P. 29.7168  
M.P. 29.7296  
M.P. 29.7943  
M.P. 29.804

M.P. 29.8262

"CP MOKENA"  
(Mokena)

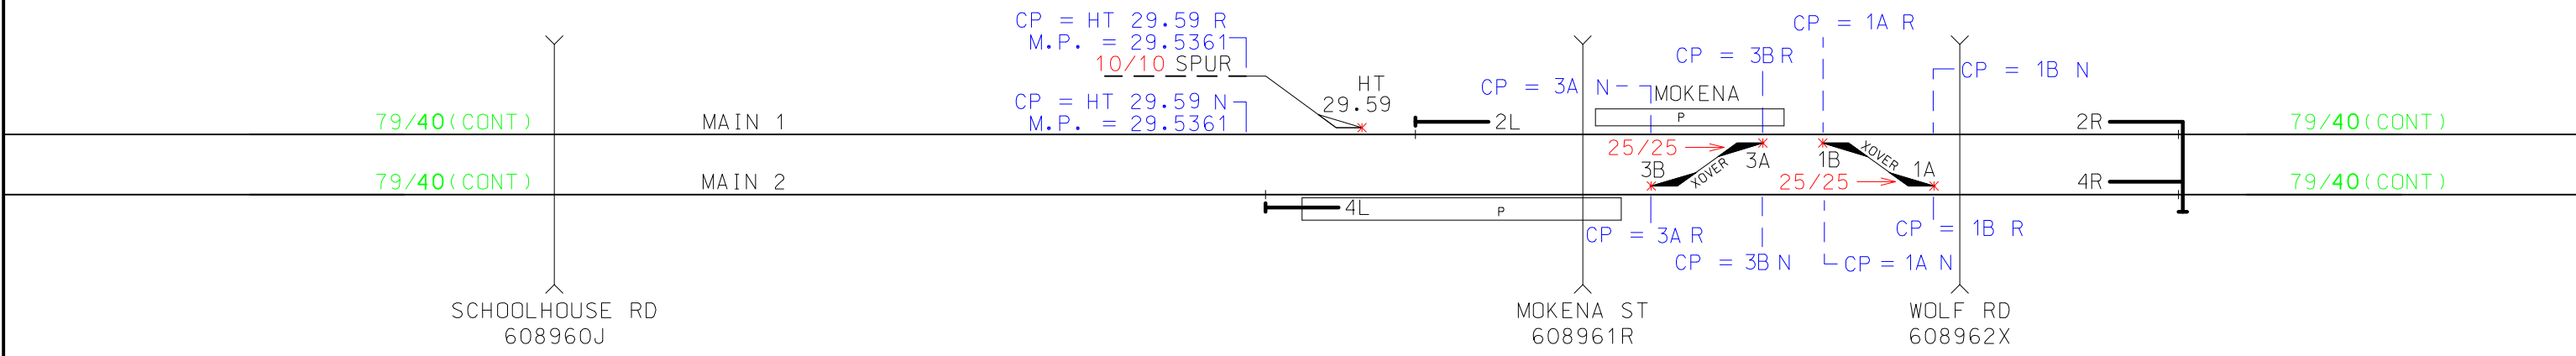



<----- EAST

WEST ----->


30

31

M.P. 29.8262

M.P. 30.2163

CP = 1B N

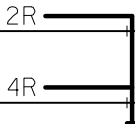

79/40 (CONT)

79/40 (CONT)

MAIN 1

MAIN 2

W

79/40 (CONT)

W

79/40 (CONT)

1B R

RD  
62X

FRANCIS RD  
608963E

| REV. | DATE     | BY | DESCRIPTION                                                    | REV. | DATE     | BY | DESCRIPTION                                                     |
|------|----------|----|----------------------------------------------------------------|------|----------|----|-----------------------------------------------------------------|
| 29   | 10/05/22 | JA | REVISED PER CHANGES TO CP WESTERN, INTERCHANGE AND ROBBINS     | 34   | 09/17/24 | JE | REVISED PER 16TH ST DIAMOND REPLACEMENT                         |
| 30   | 12/21/22 | JE | REVISED PER CHANGES TO SPEED OF XOVER 115 AT WESTERN           | 35   | 11/11/24 | JE | REVISED PER SPEED CHANGE TO 10 MPH ACROSS UD TOWER DIAMONDS     |
| 31   | 05/05/23 | JA | REVISED NONCOMM TRACK AT CHI TERM & SPEED AT WESTERN 115 XOVER | 36   | 01/08/25 | JE | REVISED PER AUDIT RUN CHANGES, CRs for PEDs and PLATFORMS       |
| 32   | 01/08/24 | JE | REVISED PER CF AUDIT CHANGES AT 80TH AVE AND 105TH ST          | 37   | 02/04/25 | ES | REVISED TO UPDATE SWITCHES TO ELECTRIC LOCK                     |
| 33   | 01/08/24 | JA | REVISED PER REMOVAL OF CON1SCAL TRACK AT 16TH ST               | 38   | 02/06/25 | JE | REVISED TO UPDATE FREIGHT SPEEDS TO 40MPH BETWEEN ROBBINS & EJE |

DISCLOSURE:  
CHARTS ARE A VISUAL REPRESENTATION OF  
THE SUBDIV AND ARE TO BE USED FOR PTC  
SUBDIV PURPOSES ONLY



METRA SUBDIV FILE  
MASTER DRAWING  
JOLIET SUB  
ILLINOIS  
M.P.30.0 - 31.0

<----- EAST

WEST ----->


31

32

M.P. 31.638

M.P. 31.641

M.P. 31.99

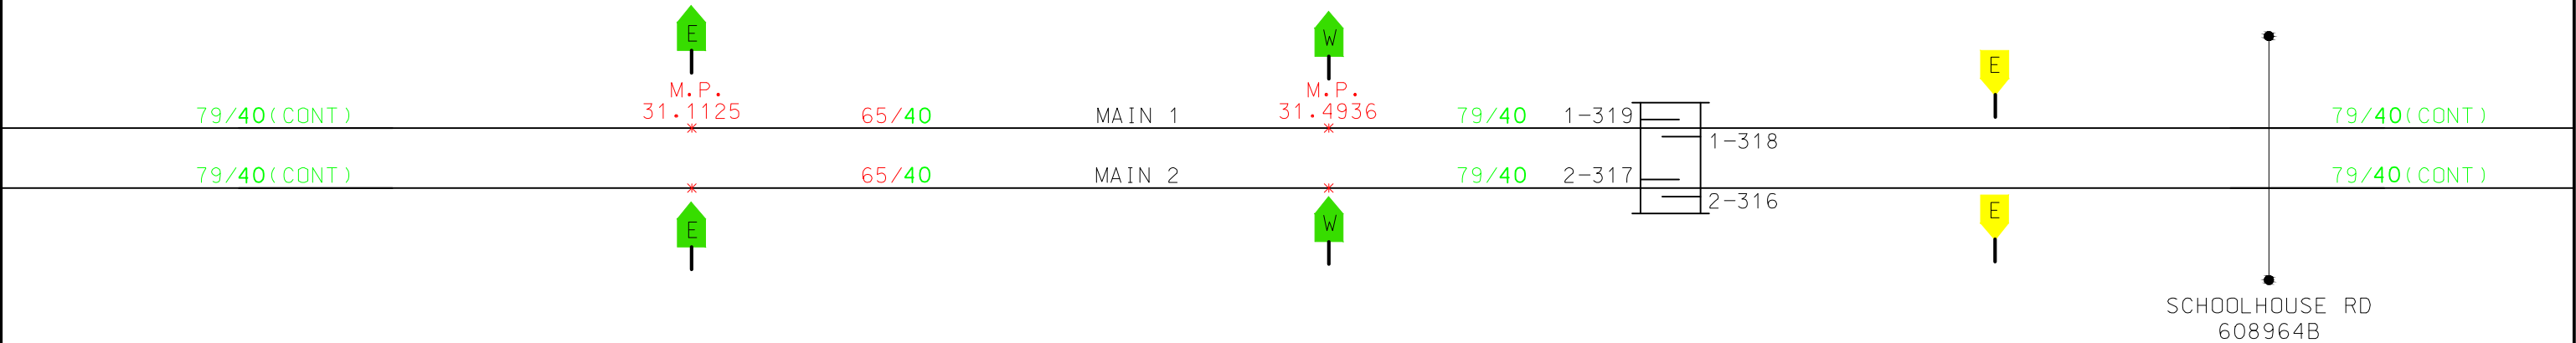


| REV. | DATE     | BY | DESCRIPTION                                                    | REV. | DATE     | BY | DESCRIPTION                                                    | DISCLOSURE:<br>CHARTS ARE A VISUAL REPRESENTATION OF<br>THE SUBDIV AND ARE TO BE USED FOR PTC<br>SUBDIV PURPOSES ONLY | <br>547 W. JACKSON BLVD.<br>CHICAGO, IL. 60661 | METRA SUBDIV FILE<br>MASTER DRAWING<br>JOLIET SUB<br>ILLINOIS<br>M.P.31.0 - 32.0 | SHEET NO. 32 |
|------|----------|----|----------------------------------------------------------------|------|----------|----|----------------------------------------------------------------|---|---|----------------------------------------------------------------------------------|--------------|
| 29   | 10/05/22 | JA | REVISED PER CHANGES TO CP WESTERN, INTERCHANGE AND ROBBINS     | 34   | 09/17/24 | JE | REVISED PER 16TH ST DIAMOND REPLACEMENT                        |   |   |                                                                                  |              |
| 30   | 12/21/22 | JE | REVISED PER CHANGES TO SPEED OF XOVER 115 AT WESTERN           | 35   | 11/11/24 | JE | REVISED PER SPEED CHANGE TO 10 MPH ACROSS UD TOWER DIAMONDS    |   |   |                                                                                  |              |
| 31   | 05/05/23 | JA | REVISED NONCOMM TRACK AT CHI TERM & SPEED AT WESTERN 115 XOVER | 36   | 01/08/25 | JE | REVISED PER AUDIT RUN CHANGES, CRs for PEDs and PLATFORMS      |   |   |                                                                                  |              |
| 32   | 01/08/24 | JE | REVISED PER CF AUDIT CHANGES AT 80TH AVE AND 105TH ST          | 37   | 02/04/25 | ES | REVISED TO UPDATE SWITCHES TO ELECTRIC LOCK                    |   |   |                                                                                  |              |
| 33   | 01/08/24 | JA | REVISED PER REMOVAL OF CON1SCAL TRACK AT 16TH ST               | 38   | 02/06/25 | JE | REVISED TO UPDATE FREIGHT SPEEDS TO 40MPH BETWEEN ROBBINS & EJ |   |   |                                                                                  |              |




<----- EAST

WEST ----->

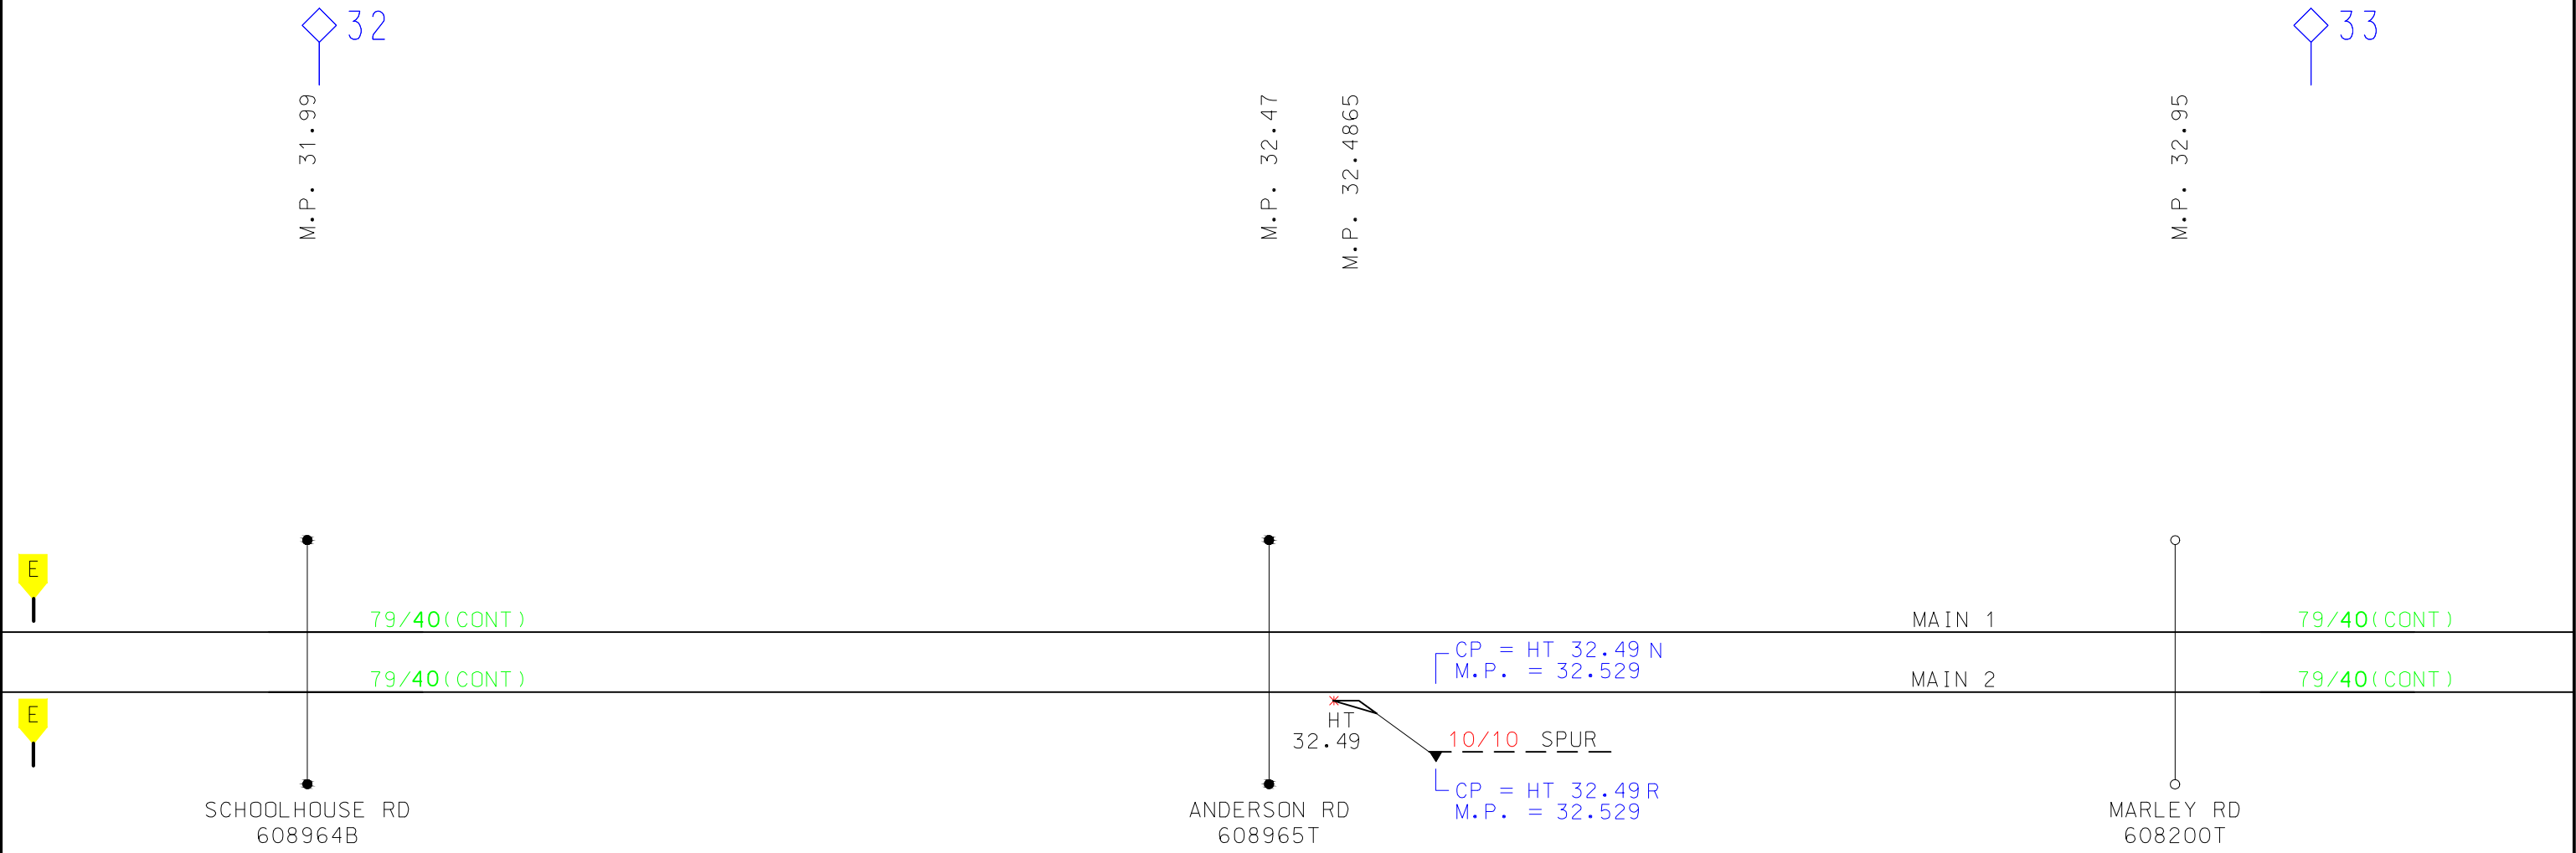


<----- EAST

WEST ----->

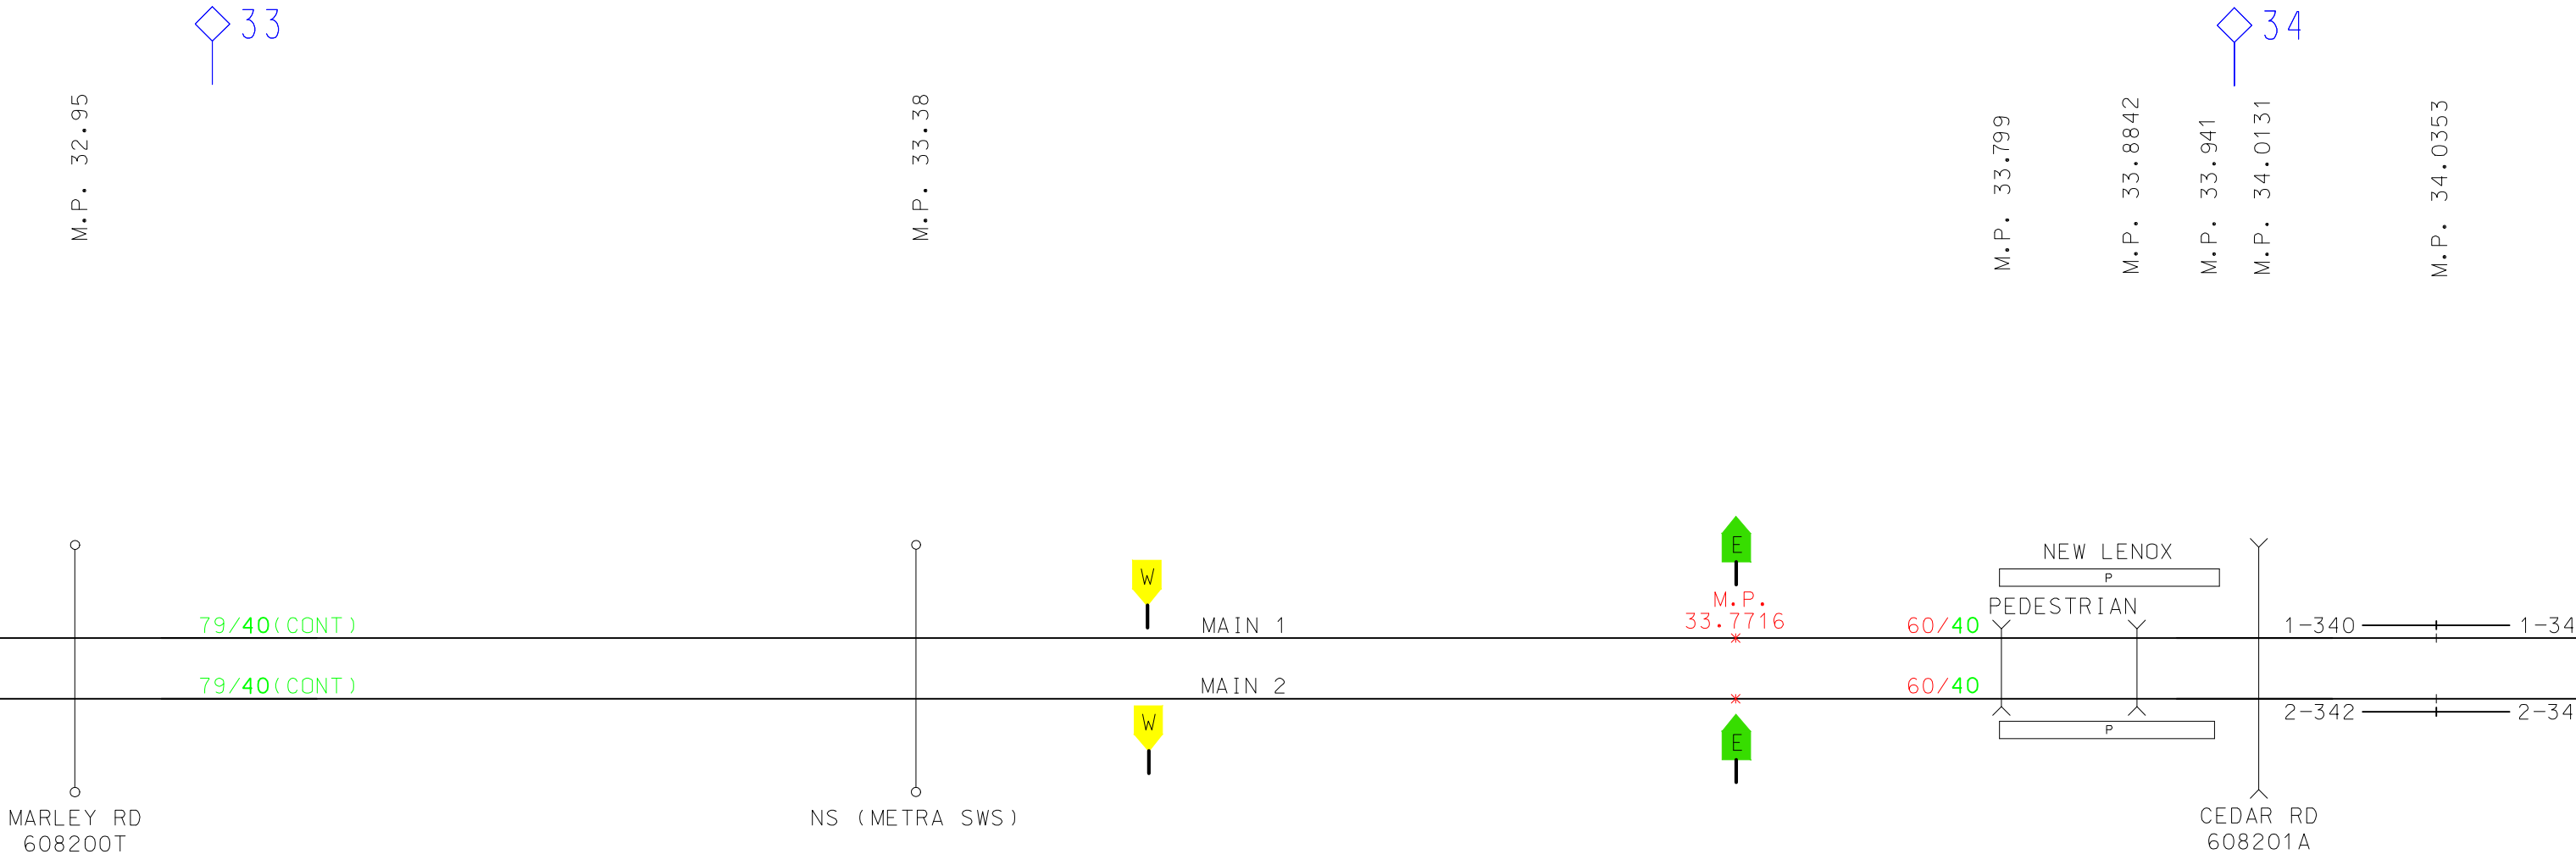

<----- EAST



WEST ----->

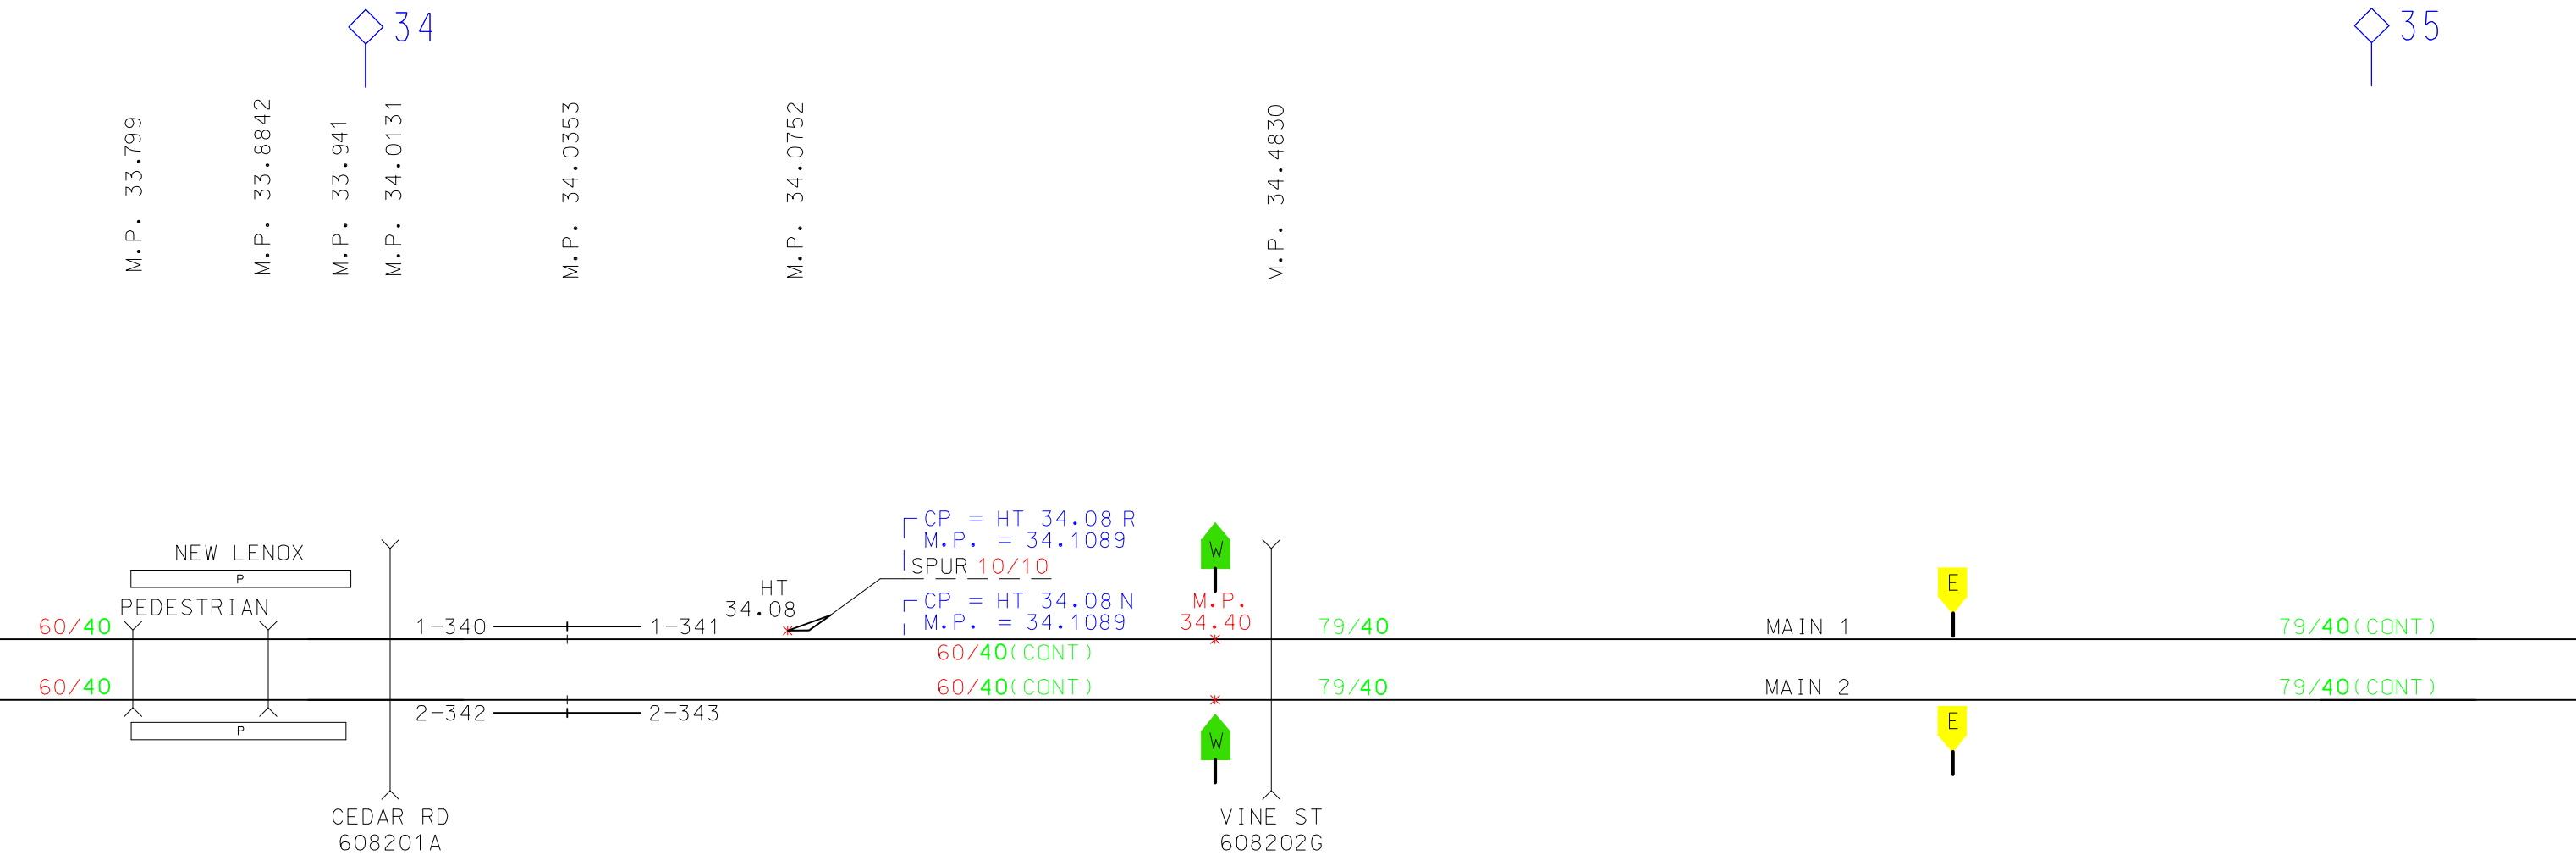

| REV. | DATE     | BY | DESCRIPTION                                                    | REV. | DATE     | BY | DESCRIPTION                                                    | DISCLOSURE:<br>CHARTS ARE A VISUAL REPRESENTATION OF<br>THE SUBDIV AND ARE TO BE USED FOR PTC<br>SUBDIV PURPOSES ONLY | <br>547 W. JACKSON BLVD.<br>CHICAGO, IL. 60661 | METRA SUBDIV FILE<br>MASTER DRAWING<br>JOLIET SUB<br>ILLINOIS<br>M.P.34.0 - 35.0 | SHEET NO. 35 |
|------|----------|----|----------------------------------------------------------------|------|----------|----|----------------------------------------------------------------|---|---|----------------------------------------------------------------------------------|--------------|
| 29   | 10/05/22 | JA | REVISED PER CHANGES TO CP WESTERN, INTERCHANGE AND ROBBINS     | 34   | 09/17/24 | JE | REVISED PER 16TH ST DIAMOND REPLACEMENT                        |   |   |                                                                                  |              |
| 30   | 12/21/22 | JE | REVISED PER CHANGES TO SPEED OF XOVER 115 AT WESTERN           | 35   | 11/11/24 | JE | REVISED PER SPEED CHANGE TO 10 MPH ACROSS UD TOWER DIAMONDS    |   |   |                                                                                  |              |
| 31   | 05/05/23 | JA | REVISED NONCOMM TRACK AT CHI TERM & SPEED AT WESTERN 115 XOVER | 36   | 01/08/25 | JE | REVISED PER AUDIT RUN CHANGES, CRs for PEDs and PLATFORMS      |   |   |                                                                                  |              |
| 32   | 01/08/24 | JE | REVISED PER CF AUDIT CHANGES AT 80TH AVE AND 105TH ST          | 37   | 02/04/25 | ES | REVISED TO UPDATE SWITCHES TO ELECTRIC LOCK                    |   |   |                                                                                  |              |
| 33   | 01/08/24 | JA | REVISED PER REMOVAL OF CON1SCAL TRACK AT 16TH ST               | 38   | 02/06/25 | JE | REVISED TO UPDATE FREIGHT SPEEDS TO 40MPH BETWEEN ROBBINS & EJ |   |   |                                                                                  |              |

<----- EAST

WEST ----->

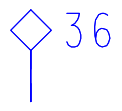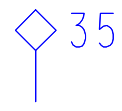

M.P. 35.304  
M.P. 35.3435

M.P. 35.3488

M.P. 35.40  
M.P. 35.42


M.P. 35.4387

M.P. 35.4972

M.P. 35.5012

M.P. 36.1216

"CP 35.5"  
(35.5)

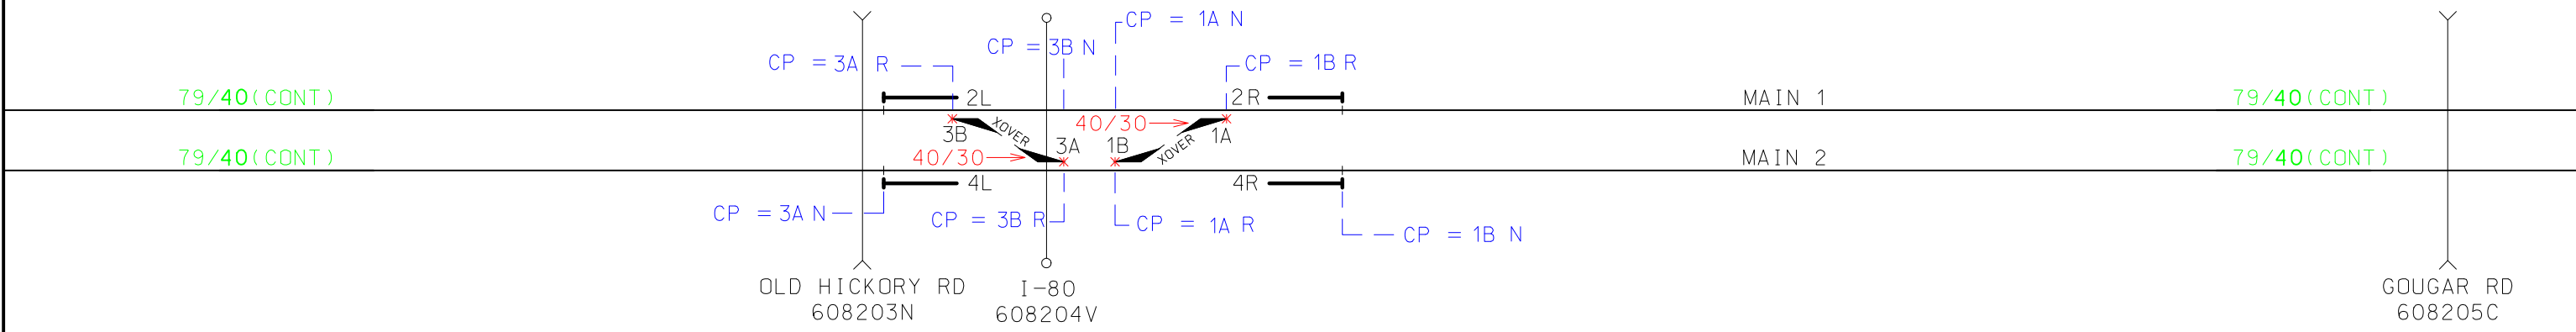

<----- EAST


WEST ----->

36

37

M.P. 36.1216

M.P. 37.1075

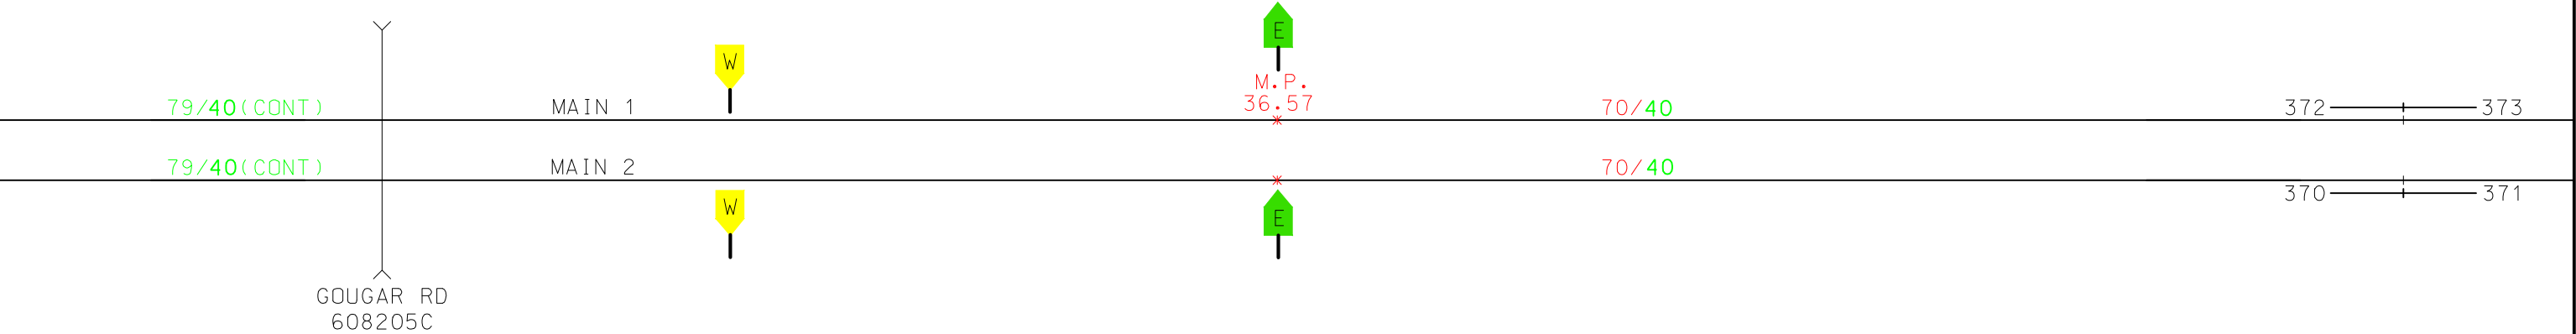

| REV. | DATE     | BY | DESCRIPTION                                                    | REV. | DATE     | BY | DESCRIPTION                                                     | DISCLOSURE:<br>CHARTS ARE A VISUAL REPRESENTATION OF<br>THE SUBDIV AND ARE TO BE USED FOR PTC<br>SUBDIV PURPOSES ONLY | <br>547 W. JACKSON BLVD.<br>CHICAGO, IL. 60661 | METRA SUBDIV FILE<br>MASTER DRAWING<br>JOLIET SUB<br>ILLINOIS<br>M.P.36.0 - 37.0 | SHEET NO. 37 |
|------|----------|----|----------------------------------------------------------------|------|----------|----|-----------------------------------------------------------------|---|---|----------------------------------------------------------------------------------|--------------|
| 29   | 10/05/22 | JA | REVISED PER CHANGES TO CP WESTERN, INTERCHANGE AND ROBBINS     | 34   | 09/17/24 | JE | REVISED PER 16TH ST DIAMOND REPLACEMENT                         |   |   |                                                                                  |              |
| 30   | 12/21/22 | JE | REVISED PER CHANGES TO SPEED OF XOVER 115 AT WESTERN           | 35   | 11/11/24 | JE | REVISED PER SPEED CHANGE TO 10 MPH ACROSS UD TOWER DIAMONDS     |   |   |                                                                                  |              |
| 31   | 05/05/23 | JA | REVISED NONCOMM TRACK AT CHI TERM & SPEED AT WESTERN 115 XOVER | 36   | 01/08/25 | JE | REVISED PER AUDIT RUN CHANGES, CRs for PEDs and PLATFORMS       |   |   |                                                                                  |              |
| 32   | 01/08/24 | JE | REVISED PER CF AUDIT CHANGES AT 80TH AVE AND 105TH ST          | 37   | 02/04/25 | ES | REVISED TO UPDATE SWITCHES TO ELECTRIC LOCK                     |   |   |                                                                                  |              |
| 33   | 01/08/24 | JA | REVISED PER REMOVAL OF CON1SCAL TRACK AT 16TH ST               | 38   | 02/06/25 | JE | REVISED TO UPDATE FREIGHT SPEEDS TO 40MPH BETWEEN ROBBINS & EJE |   |   |                                                                                  |              |

<----- EAST

WEST ----->

37

M.P. 37.1075

38

M.P. 37.87

372 373

70/40 (CONT)

MAIN 1

M.P. 37.83

79/40

E

370 371

70/40 (CONT)

MAIN 2

CASS ST  
608207R

79/40

E


| REV. | DATE     | BY | DESCRIPTION                                                    | REV. | DATE     | BY | DESCRIPTION                                                     |
|------|----------|----|----------------------------------------------------------------|------|----------|----|-----------------------------------------------------------------|
| 29   | 10/05/22 | JA | REVISED PER CHANGES TO CP WESTERN, INTERCHANGE AND ROBBINS     | 34   | 09/17/24 | JE | REVISED PER 16TH ST DIAMOND REPLACEMENT                         |
| 30   | 12/21/22 | JE | REVISED PER CHANGES TO SPEED OF XOVER 115 AT WESTERN           | 35   | 11/11/24 | JE | REVISED PER SPEED CHANGE TO 10 MPH ACROSS UD TOWER DIAMONDS     |
| 31   | 05/05/23 | JA | REVISED NONCOMM TRACK AT CHI TERM & SPEED AT WESTERN 115 XOVER | 36   | 01/08/25 | JE | REVISED PER AUDIT RUN CHANGES, CRs for PEDs and PLATFORMS       |
| 32   | 01/08/24 | JE | REVISED PER CF AUDIT CHANGES AT 80TH AVE AND 105TH ST          | 37   | 02/04/25 | ES | REVISED TO UPDATE SWITCHES TO ELECTRIC LOCK                     |
| 33   | 01/08/24 | JA | REVISED PER REMOVAL OF CON1SCAL TRACK AT 16TH ST               | 38   | 02/06/25 | JE | REVISED TO UPDATE FREIGHT SPEEDS TO 40MPH BETWEEN ROBBINS & EJA |

DISCLOSURE:  
CHARTS ARE A VISUAL REPRESENTATION OF  
THE SUBDIV AND ARE TO BE USED FOR PTC  
SUBDIV PURPOSES ONLY



METRA SUBDIV FILE  
MASTER DRAWING  
JOLIET SUB  
ILLINOIS  
M.P.37.0 - 38.0



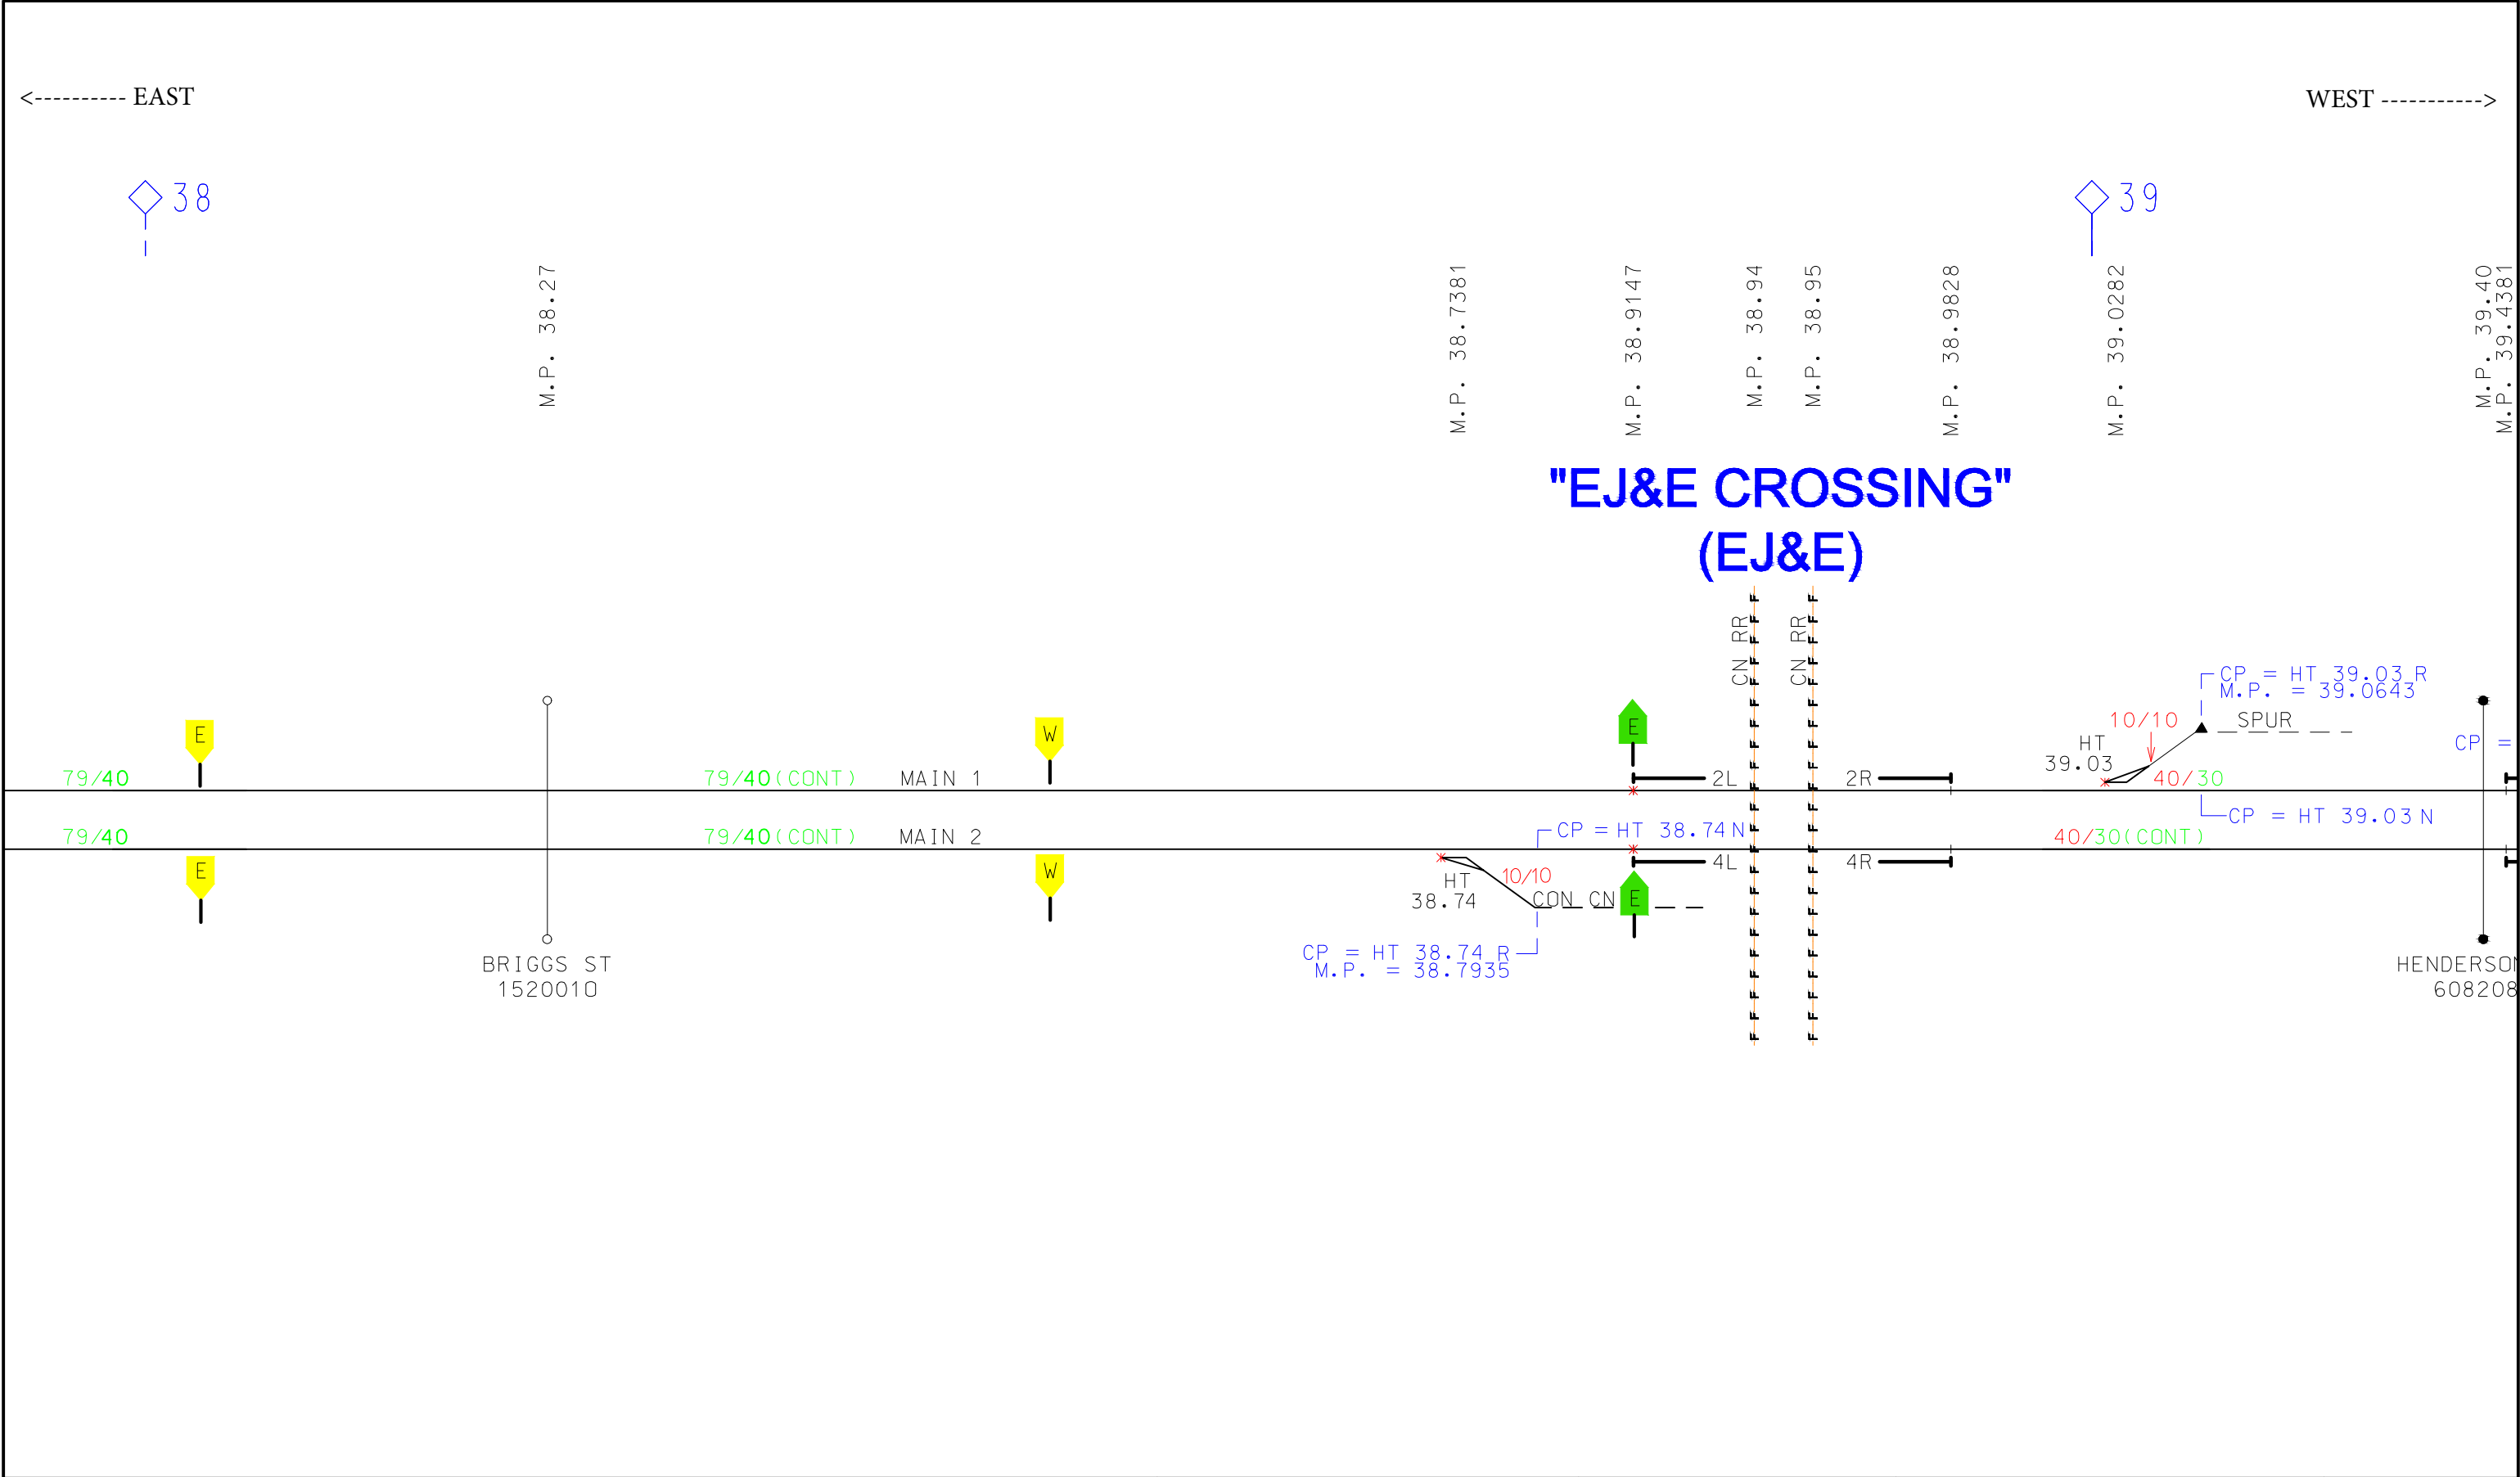

| REV. | DATE     | BY | DESCRIPTION                                                    | REV. | DATE     | BY | DESCRIPTION                                                      | DISCLOSURE:<br>CHARTS ARE A VISUAL REPRESENTATION OF<br>THE SUBDIV AND ARE TO BE USED FOR PTC<br>SUBDIV PURPOSES ONLY | <br>547 W. JACKSON BLVD.<br>CHICAGO, IL. 60661 | METRA SUBDIV FILE<br>MASTER DRAWING<br>JOLIET SUB<br>ILLINOIS<br>M.P.38.0 - 39.0 | SHEET NO. 39 |
|------|----------|----|----------------------------------------------------------------|------|----------|----|------------------------------------------------------------------|---|---|----------------------------------------------------------------------------------|--------------|
| 29   | 10/05/22 | JA | REVISED PER CHANGES TO CP WESTERN, INTERCHANGE AND ROBBINS     | 34   | 09/17/24 | JE | REVISED PER 16TH ST DIAMOND REPLACEMENT                          |   |   |                                                                                  |              |
| 30   | 12/21/22 | JE | REVISED PER CHANGES TO SPEED OF XOVER 115 AT WESTERN           | 35   | 11/11/24 | JE | REVISED PER SPEED CHANGE TO 10 MPH ACROSS UD TOWER DIAMONDS      |   |   |                                                                                  |              |
| 31   | 05/05/23 | JA | REVISED NONCOMM TRACK AT CHI TERM & SPEED AT WESTERN 115 XOVER | 36   | 01/08/25 | JE | REVISED PER AUDIT RUN CHANGES, CRs for PEDs and PLATFORMS        |   |   |                                                                                  |              |
| 32   | 01/08/24 | JE | REVISED PER CF AUDIT CHANGES AT 80TH AVE AND 105TH ST          | 37   | 02/04/25 | ES | REVISED TO UPDATE SWITCHES TO ELECTRIC LOCK                      |   |   |                                                                                  |              |
| 33   | 01/08/24 | JA | REVISED PER REMOVAL OF CON1SCAL TRACK AT 16TH ST               | 38   | 02/06/25 | JE | REVISED TO UPDATE FREIGHT SPEEDS TO 40MPH BETWEEN ROBBINS & EJ&E |   |   |                                                                                  |              |

←----- EAST

WEST ----->

39

40

M.P. 38.95  
M.P. 38.9828  
M.P. 39.0282  
M.P. 39.40  
M.P. 39.4381  
M.P. 39.4567  
M.P. 39.4931  
M.P. 39.504  
M.P. 39.5379  
M.P. 39.5659


M.P. 39.7286  
M.P. 39.7756  
M.P. 39.7819  
M.P. 39.8065  
M.P. 39.8088  
M.P. 39.8357  
M.P. 39.8491  
M.P. 39.9019  
M.P. 39.91  
M.P. 39.9982  
M.P. 40.0487

"ROSSING"  
(J&E)

"CP MILLER ST"  
(Miller)

"CP RICHARDS ST"  
(Rich)

"UD II"

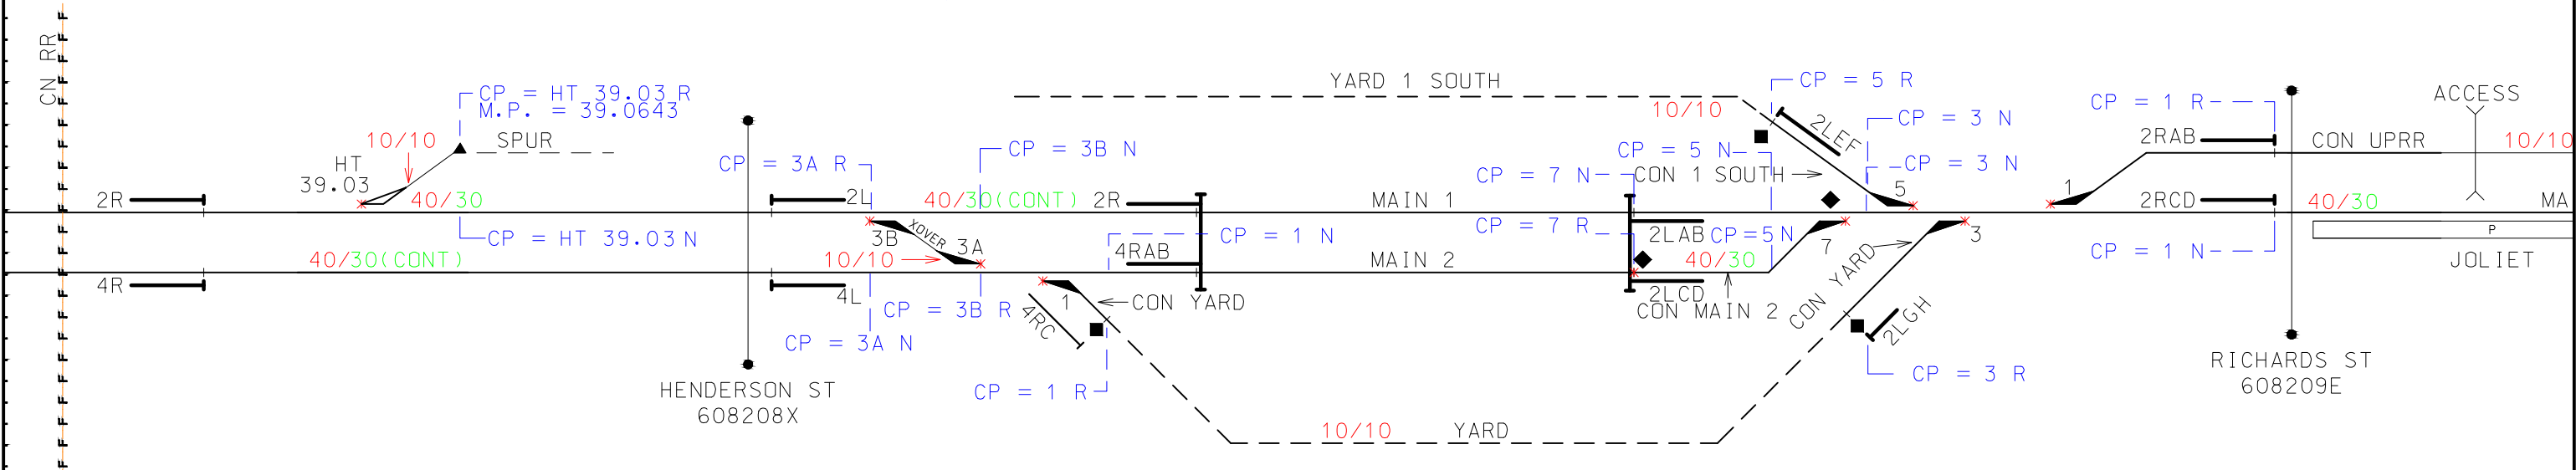

| REV. | DATE     | BY | DESCRIPTION                                                    | REV. | DATE     | BY | DESCRIPTION                                                     |
|------|----------|----|----------------------------------------------------------------|------|----------|----|-----------------------------------------------------------------|
| 29   | 10/05/22 | JA | REVISED PER CHANGES TO CP WESTERN, INTERCHANGE AND ROBBINS     | 34   | 09/17/24 | JE | REVISED PER 16TH ST DIAMOND REPLACEMENT                         |
| 30   | 12/21/22 | JE | REVISED PER CHANGES TO SPEED OF XOVER 115 AT WESTERN           | 35   | 11/11/24 | JE | REVISED PER SPEED CHANGE TO 10 MPH ACROSS UD TOWER DIAMONDS     |
| 31   | 05/05/23 | JA | REVISED NONCOMM TRACK AT CHI TERM & SPEED AT WESTERN 115 XOVER | 36   | 01/08/25 | JE | REVISED PER AUDIT RUN CHANGES, CRs for PEDs and PLATFORMS       |
| 32   | 01/08/24 | JE | REVISED PER CF AUDIT CHANGES AT 80TH AVE AND 105TH ST          | 37   | 02/04/25 | ES | REVISED TO UPDATE SWITCHES TO ELECTRIC LOCK                     |
| 33   | 01/08/24 | JA | REVISED PER REMOVAL OF CON1SCAL TRACK AT 16TH ST               | 38   | 02/06/25 | JE | REVISED TO UPDATE FREIGHT SPEEDS TO 40MPH BETWEEN ROBBINS & EJ& |

DISCLOSURE:  
CHARTS ARE A VISUAL REPRESENTATION OF  
THE SUBDIV AND ARE TO BE USED FOR PTC  
SUBDIV PURPOSES ONLY





METRA SUBDIV FILE  
MASTER DRAWING  
JOLIET SUB  
ILLINOIS  
M.P.39.0 - 40.0



<----- EAST

WEST ----->

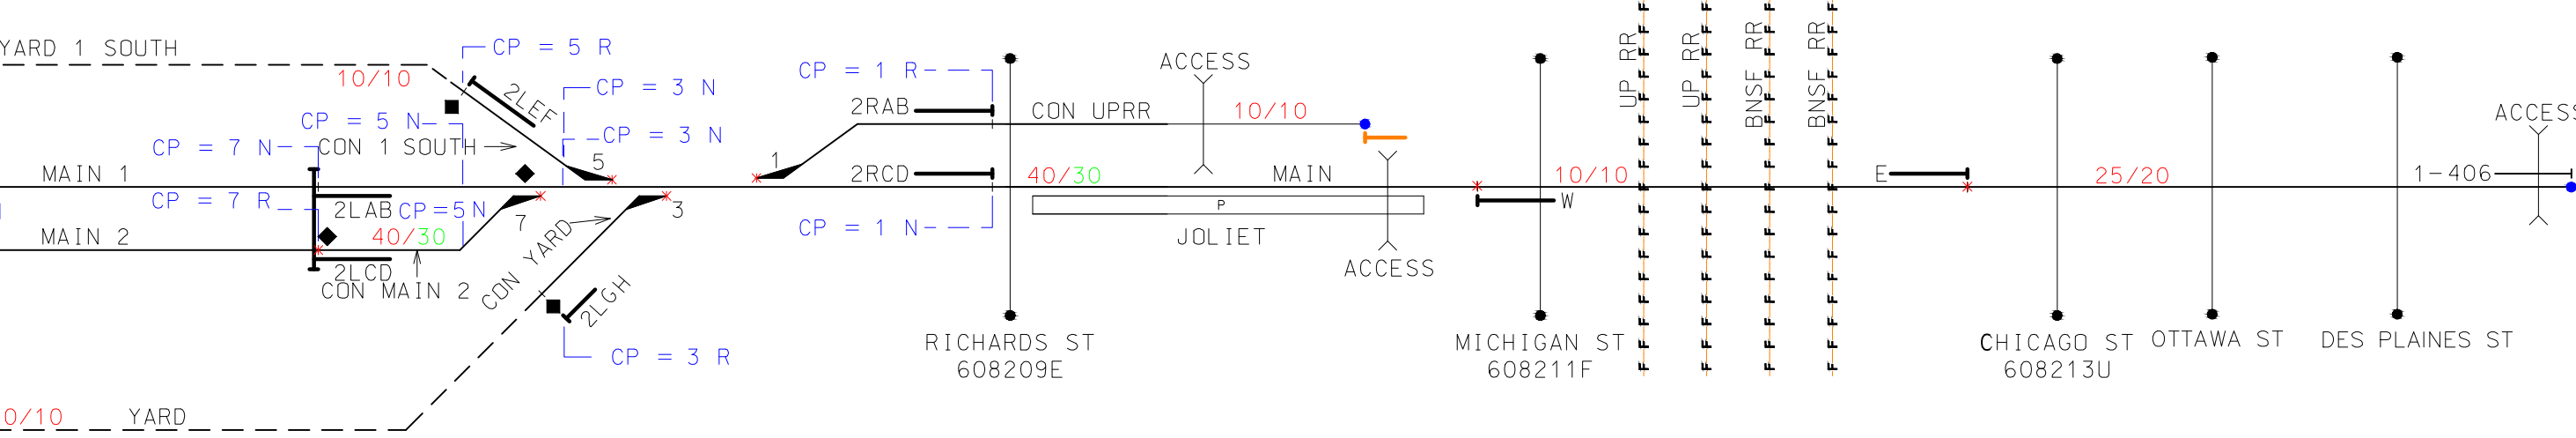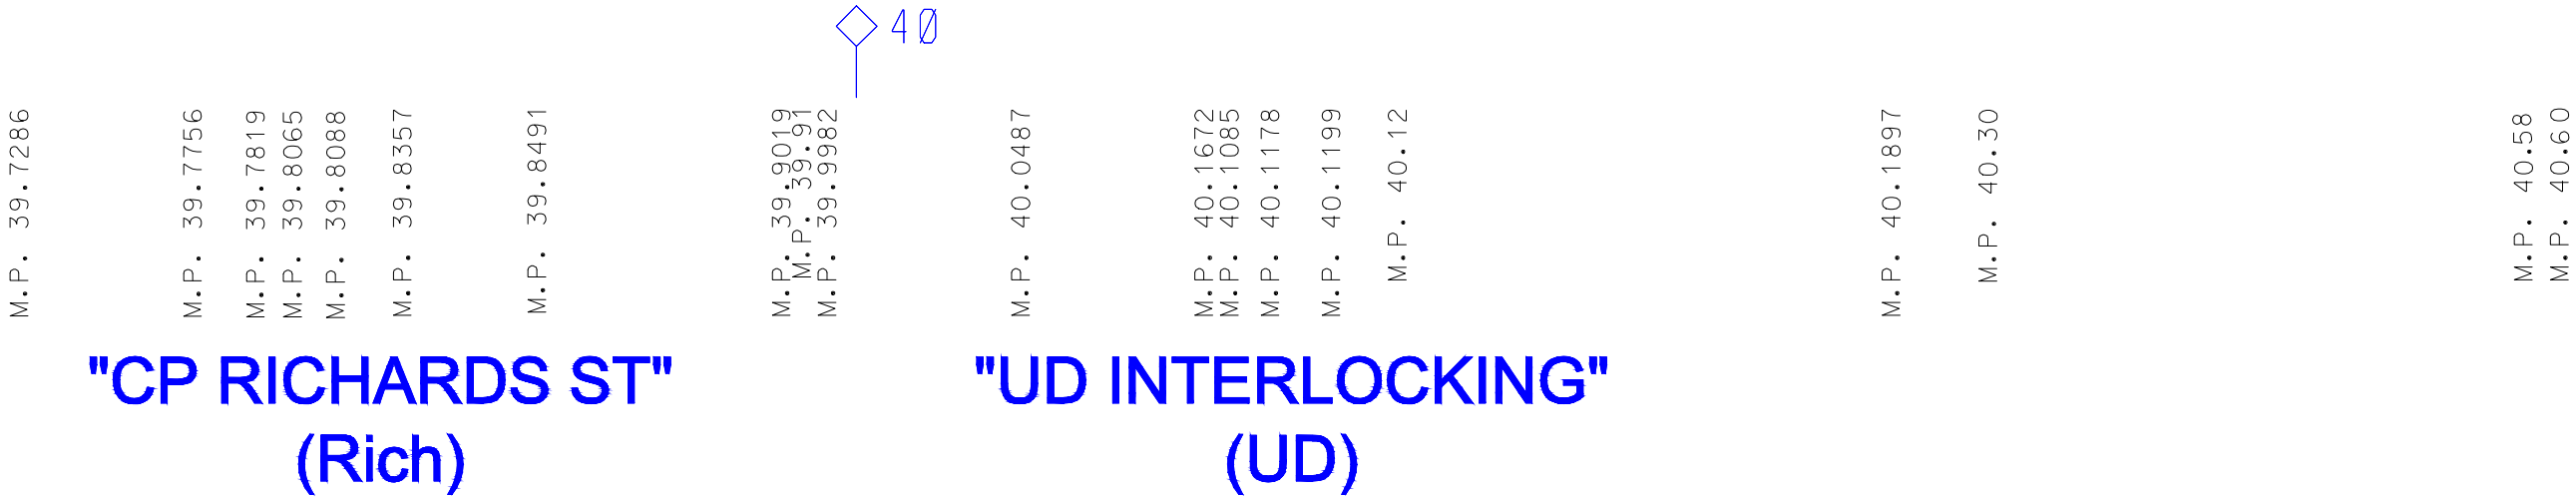

| REV. | DATE     | BY | DESCRIPTION                                                    | REV. | DATE     | BY | DESCRIPTION                                                     | DISCLOSURE:<br>CHARTS ARE A VISUAL REPRESENTATION OF<br>THE SUBDIV AND ARE TO BE USED FOR PTC<br>SUBDIV PURPOSES ONLY | <br>547 W. JACKSON BLVD.<br>CHICAGO, IL. 60661 | METRA SUBDIV FILE<br>MASTER DRAWING<br>JOLIET SUB<br>ILLINOIS<br>M.P. 40.0 - E.O.T. | SHEET NO. 41 |
|------|----------|----|----------------------------------------------------------------|------|----------|----|-----------------------------------------------------------------|---|---|-------------------------------------------------------------------------------------|--------------|
| 29   | 10/05/22 | JA | REVISED PER CHANGES TO CP WESTERN, INTERCHANGE AND ROBBINS     | 34   | 09/17/24 | JE | REVISED PER 16TH ST DIAMOND REPLACEMENT                         |   |   |                                                                                     |              |
| 30   | 12/21/22 | JE | REVISED PER CHANGES TO SPEED OF XOVER 115 AT WESTERN           | 35   | 11/11/24 | JE | REVISED PER SPEED CHANGE TO 10 MPH ACROSS UD TOWER DIAMONDS     |   |   |                                                                                     |              |
| 31   | 05/05/23 | JA | REVISED NONCOMM TRACK AT CHI TERM & SPEED AT WESTERN 115 XOVER | 36   | 01/08/25 | JE | REVISED PER AUDIT RUN CHANGES, CRs for PEDs and PLATFORMS       |   |   |                                                                                     |              |
| 32   | 01/08/24 | JE | REVISED PER CF AUDIT CHANGES AT 80TH AVE AND 105TH ST          | 37   | 02/04/25 | ES | REVISED TO UPDATE SWITCHES TO ELECTRIC LOCK                     |   |   |                                                                                     |              |
| 33   | 01/08/24 | JA | REVISED PER REMOVAL OF CON1SCAL TRACK AT 16TH ST               | 38   | 02/06/25 | JE | REVISED TO UPDATE FREIGHT SPEEDS TO 40MPH BETWEEN ROBBINS & EJA |   |   |                                                                                     |              |