



Please Notice
The BLUE DOT
denotes HYPERLINKS
throughout this document

OPERATIONS PROFILE

W.K. TUPPER Chief Operations Officer G.L. HARDWIDGE Chief Transportation Officer

S.A. AUSTIN Chief Communications Officer

D.A. ORSENO Director, Safety & Rules

CUS SERVICES-SOUTH

TABLE OF CONTENTS

- Title Pages 8
- CUS Territory 10
- South West Service 14
- Heritage Corridor 32
- Ash St. Brighton Park 49
- Joliet Area Detail 50
- Index 53

JUNE 15, 2008

Operations Profile represents Metra's compliance with **49CFR239** governing emergency preparedness specific to geographic locations on specific line segments.

PROJECT MANAGER & CHIEF DESIGNER:
J.M. GOTTLIEB

PRIMARY CONSULTANTS
M.W. SCHAEFER, J.A. WILHELMS


OPERATING RULES DATA:
L.C. MICHAEL


COMPLIANCE, EDITING & REORGANIZATION:
L.G. GOMM



FIELD VERIFICATION TEAM:
METRA POLICE DEPT.
(for off right-of-way locations)
J.S. TALLYN,
T.G. PITZEN, M.B. MINOR

GRADE CROSSING DATA:
S.C. LAFFEY (ICC)
PERIODIC REVIEW PERFORMED BY
SIGNAL DEPARTMENT

PARKING LOT DATA:
L.G. GOMM , M.C. PALMER

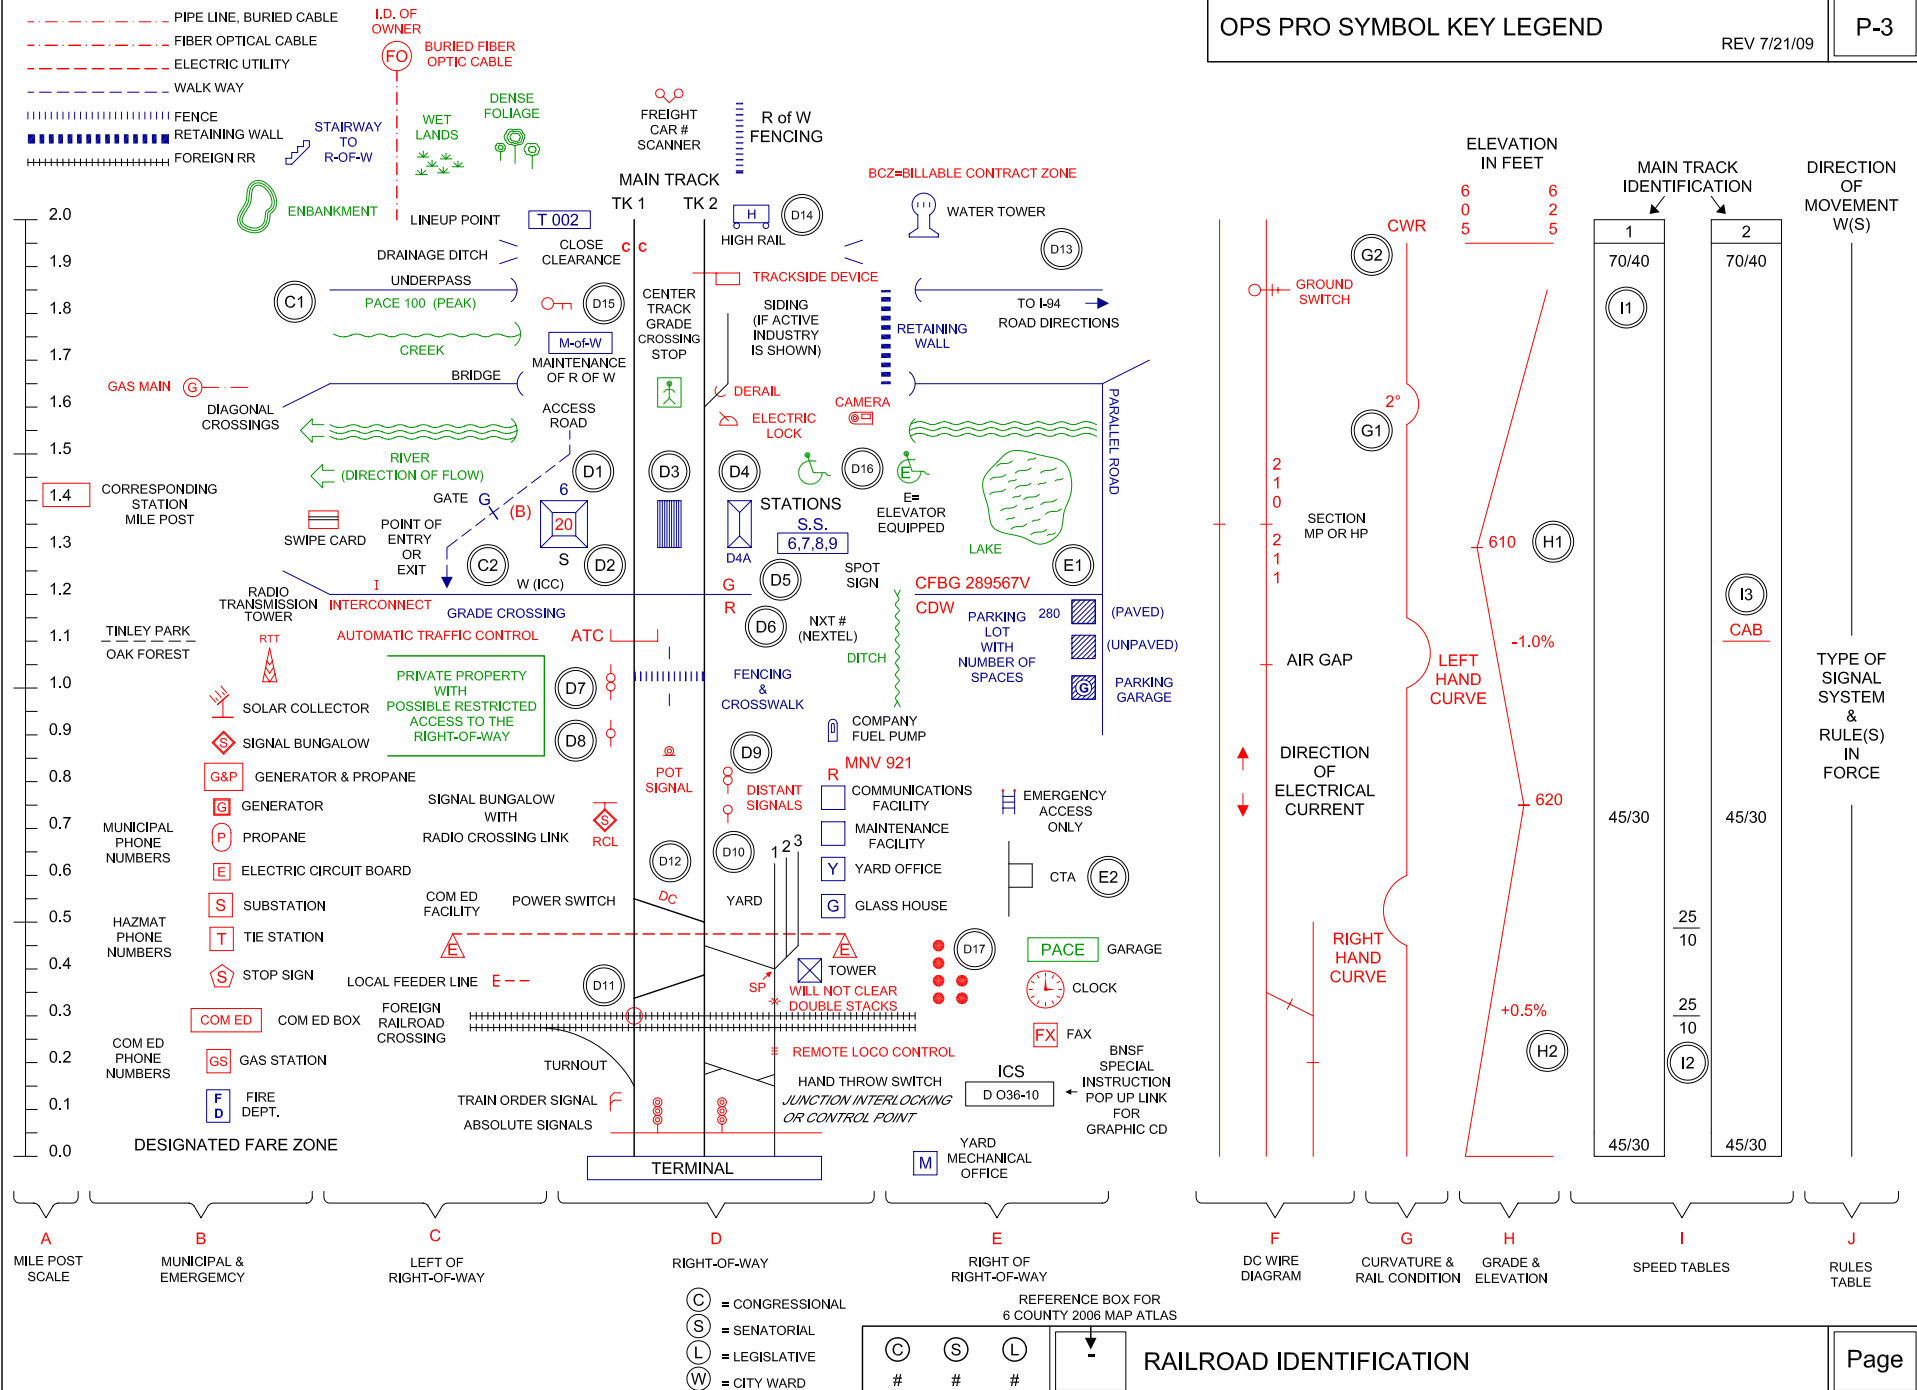


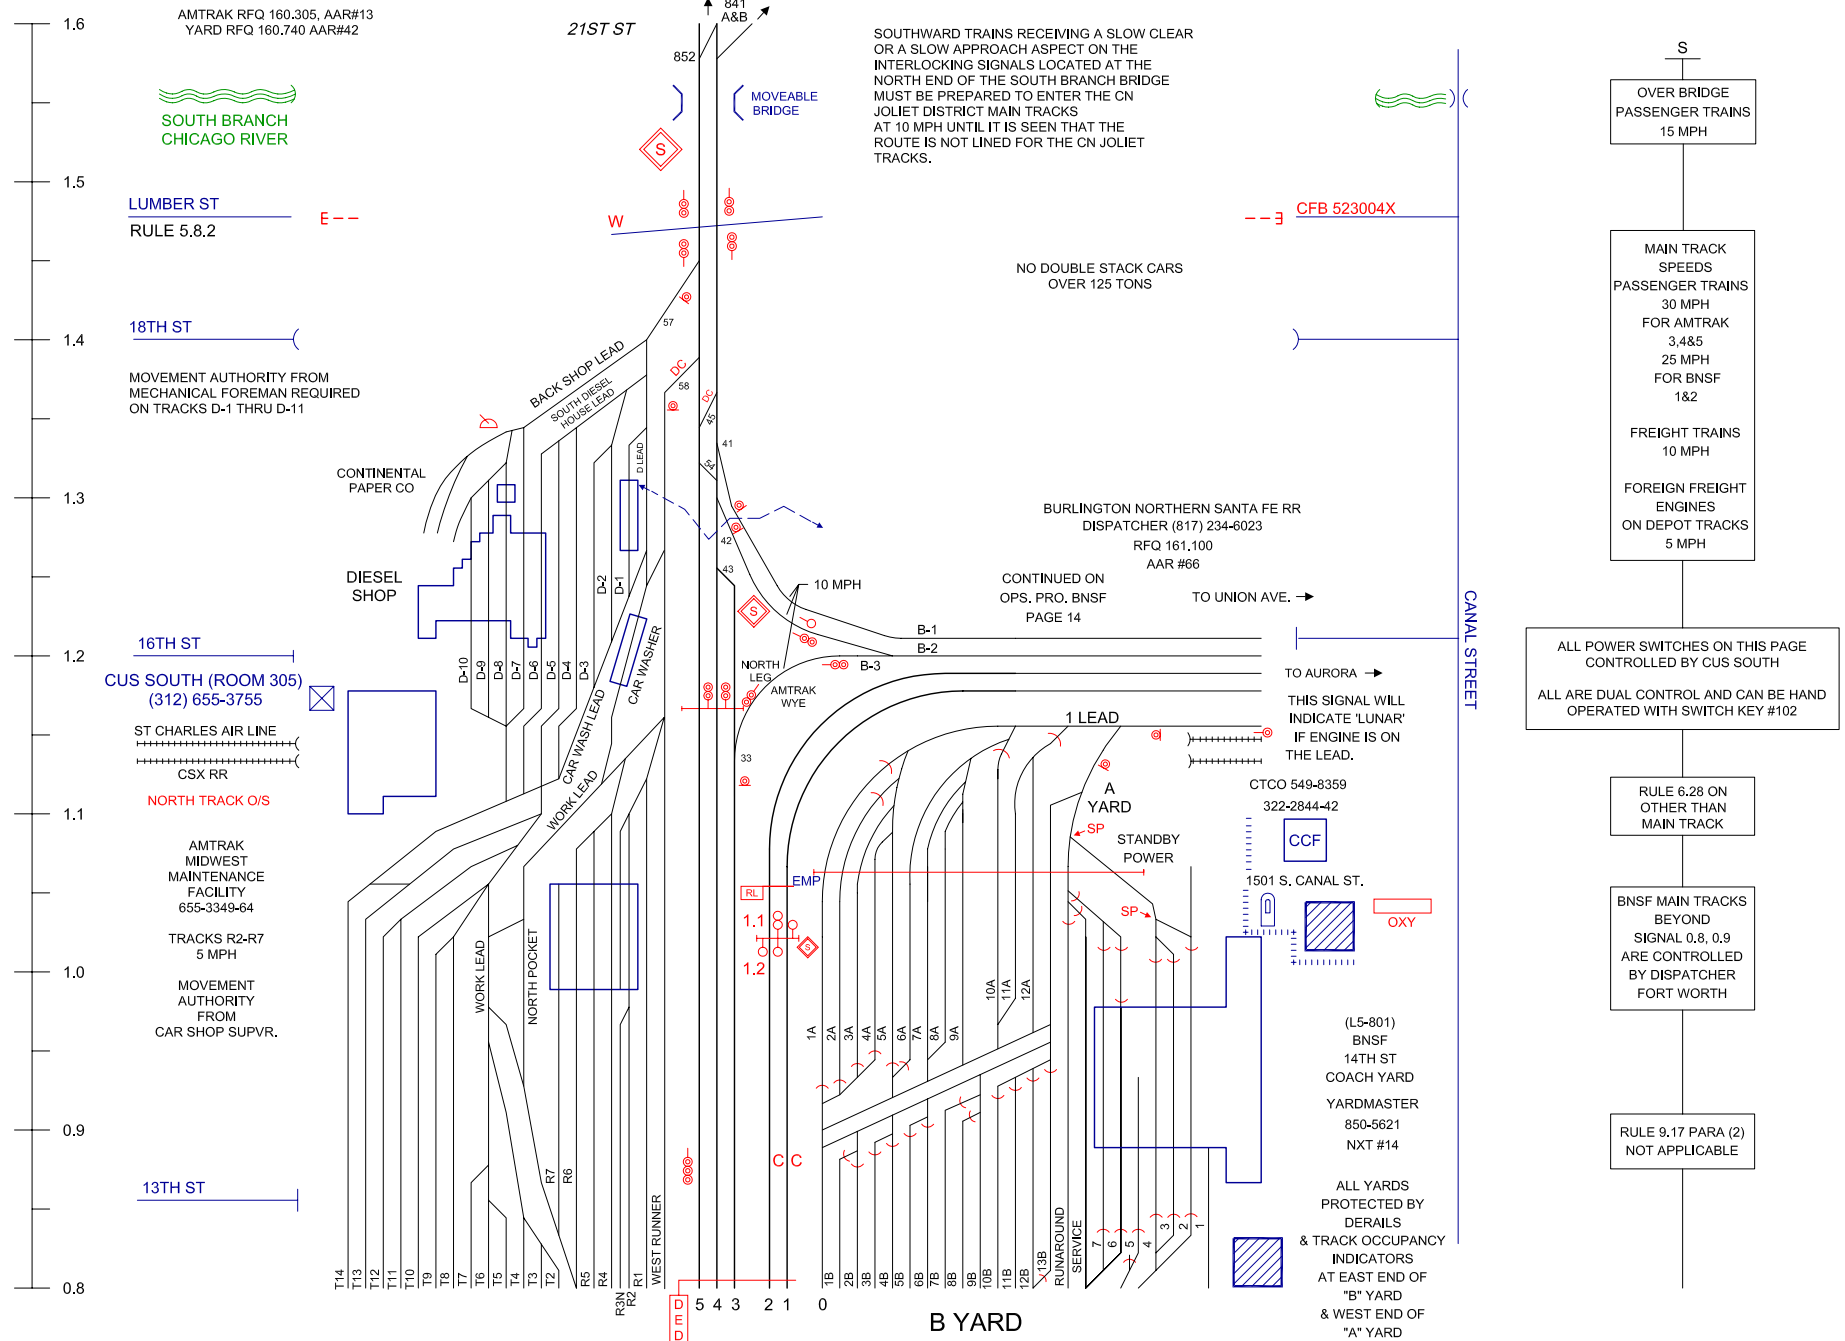


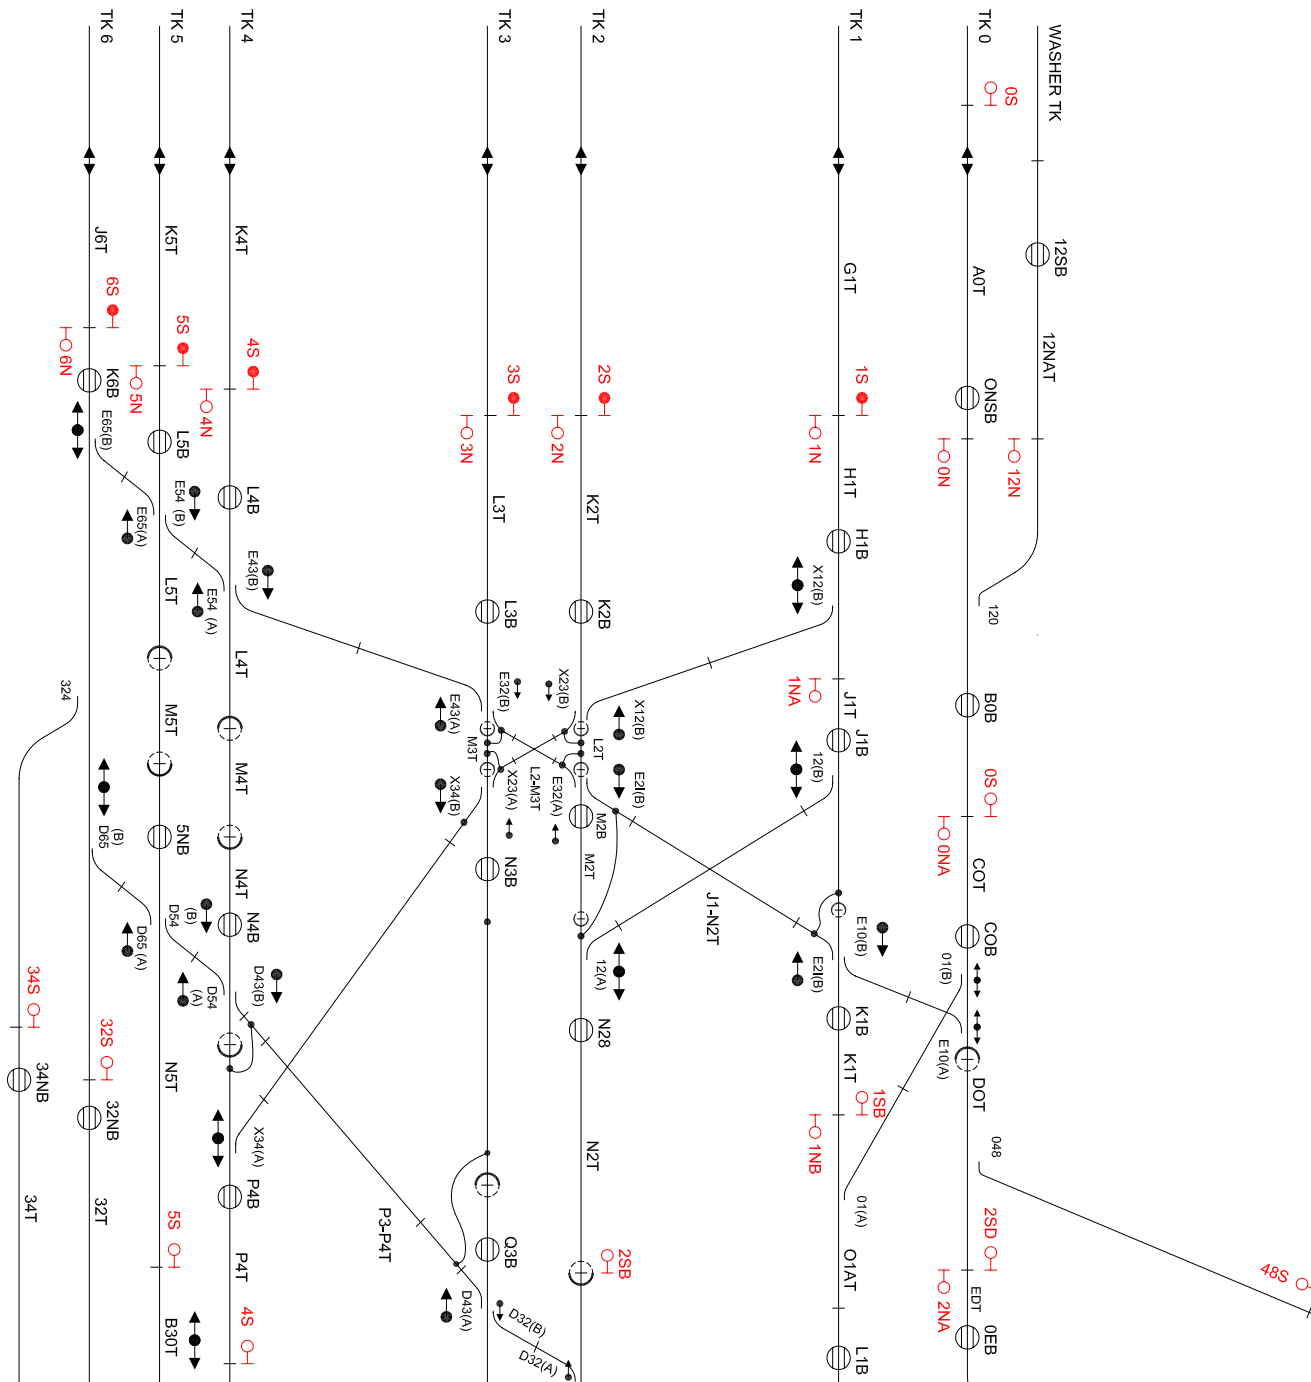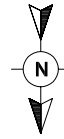

RFQ 160.440 AAR 22


RFQ 161.340 AAR 82
FOR METRA MAIN

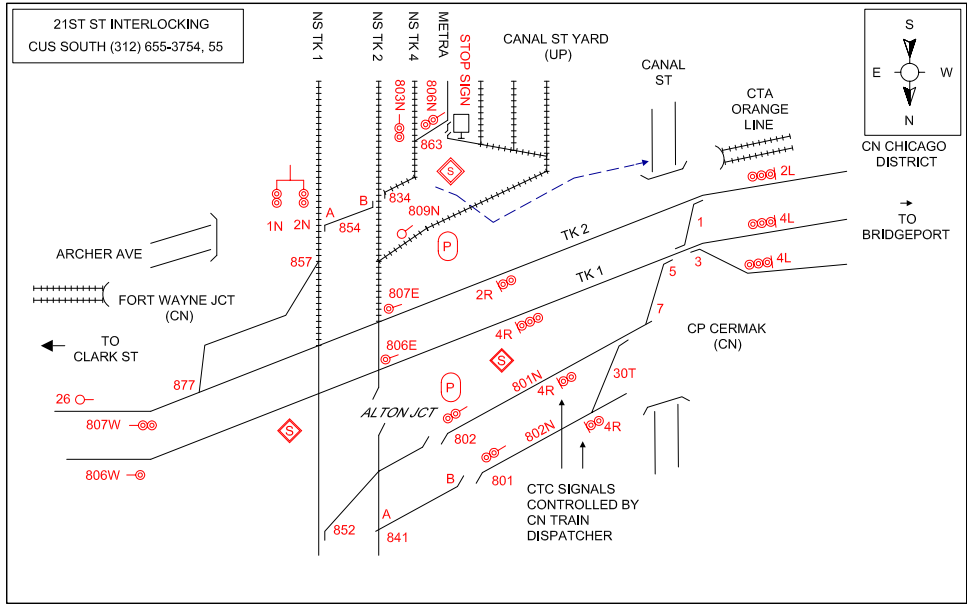

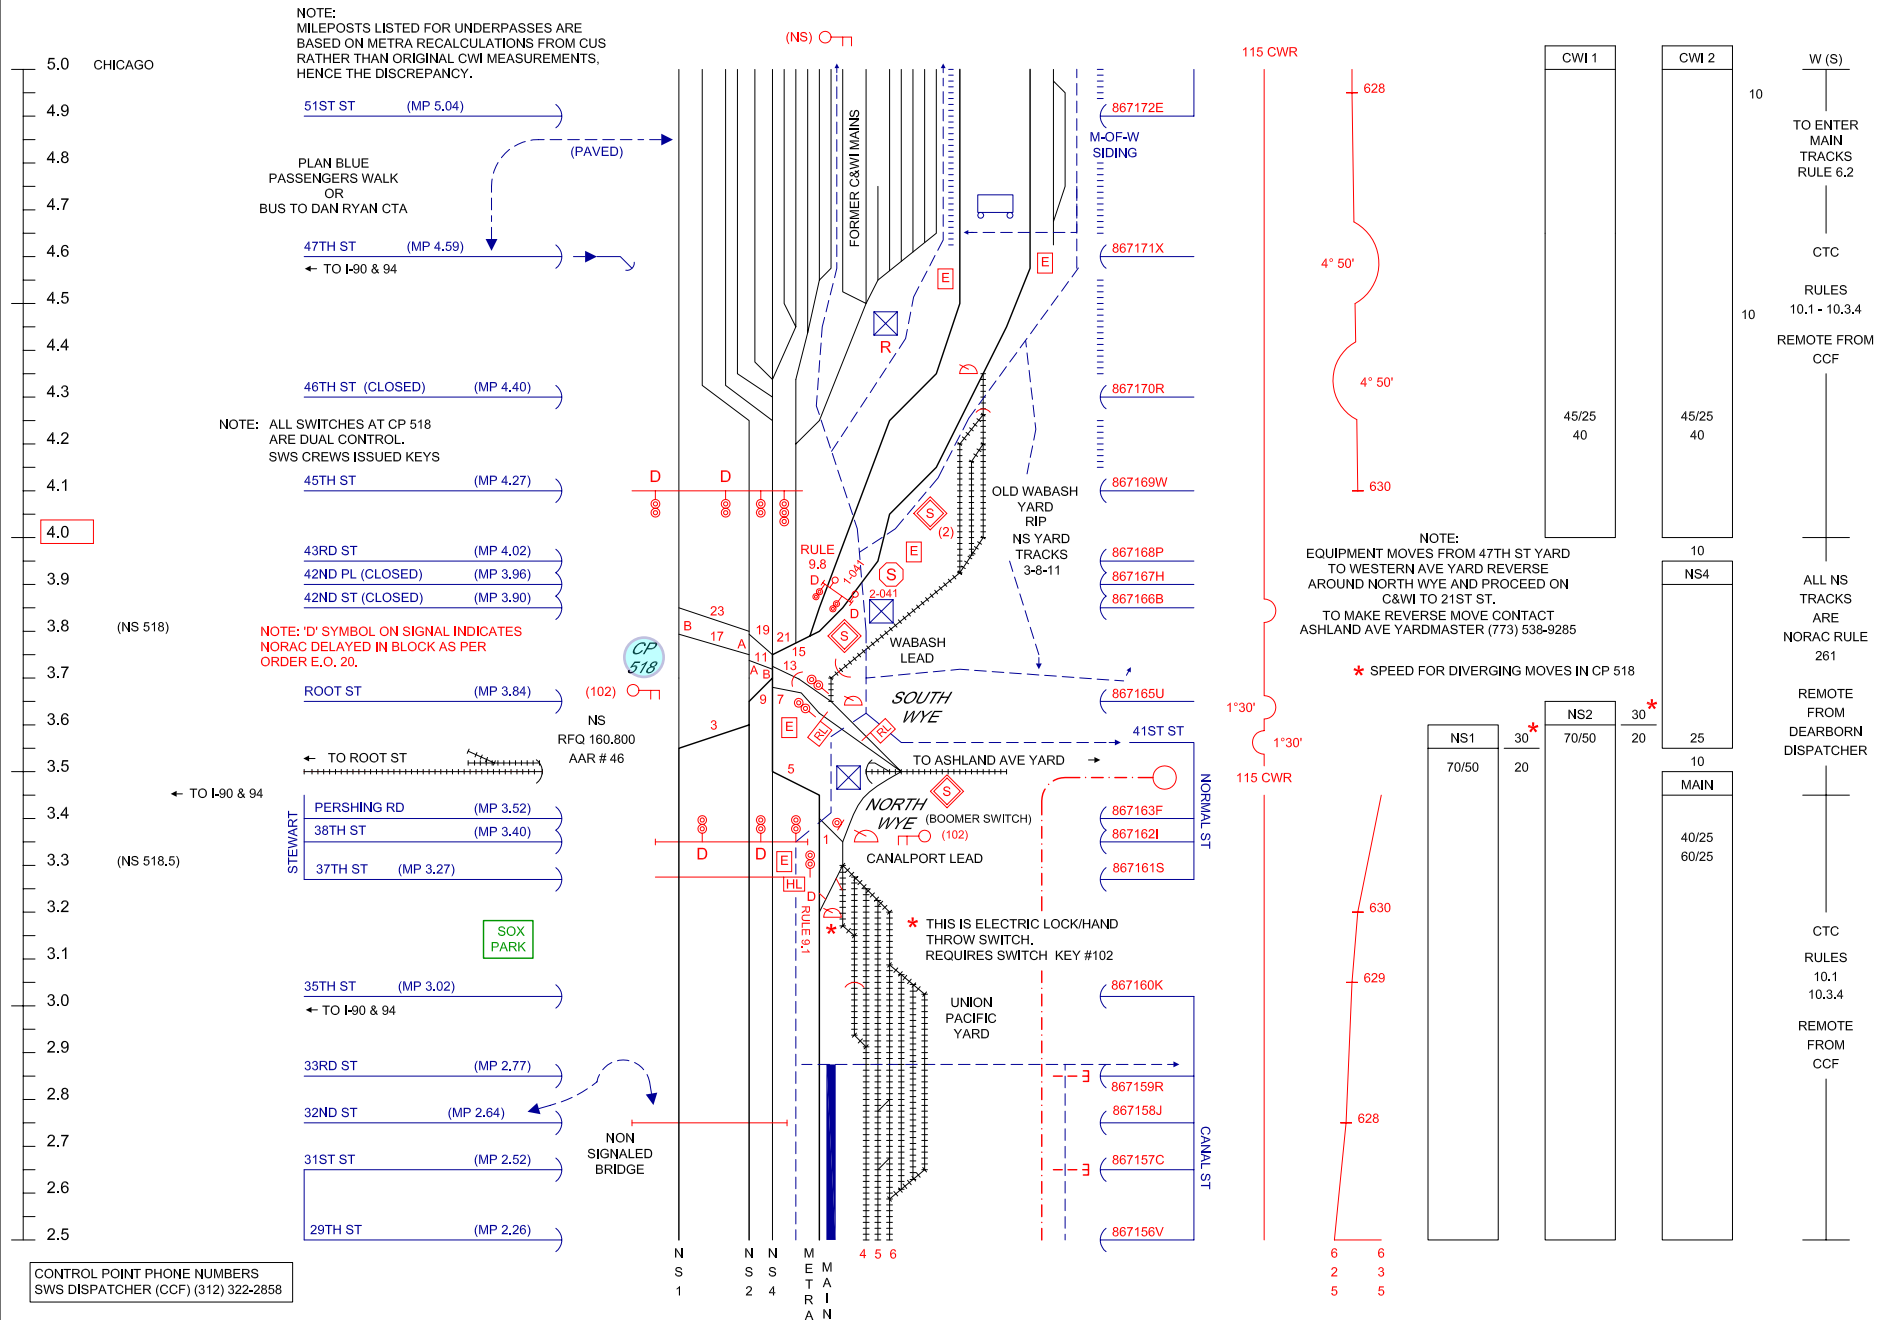

NOTE:
MILEPOSTS LISTED FOR UNDERPASSES ARE
BASED ON METRA RECALCULATIONS FROM CUS
RATHER THAN ORIGINAL CWI MEASUREMENTS,
HENCE THE DISCREPANCY.

6
2
5

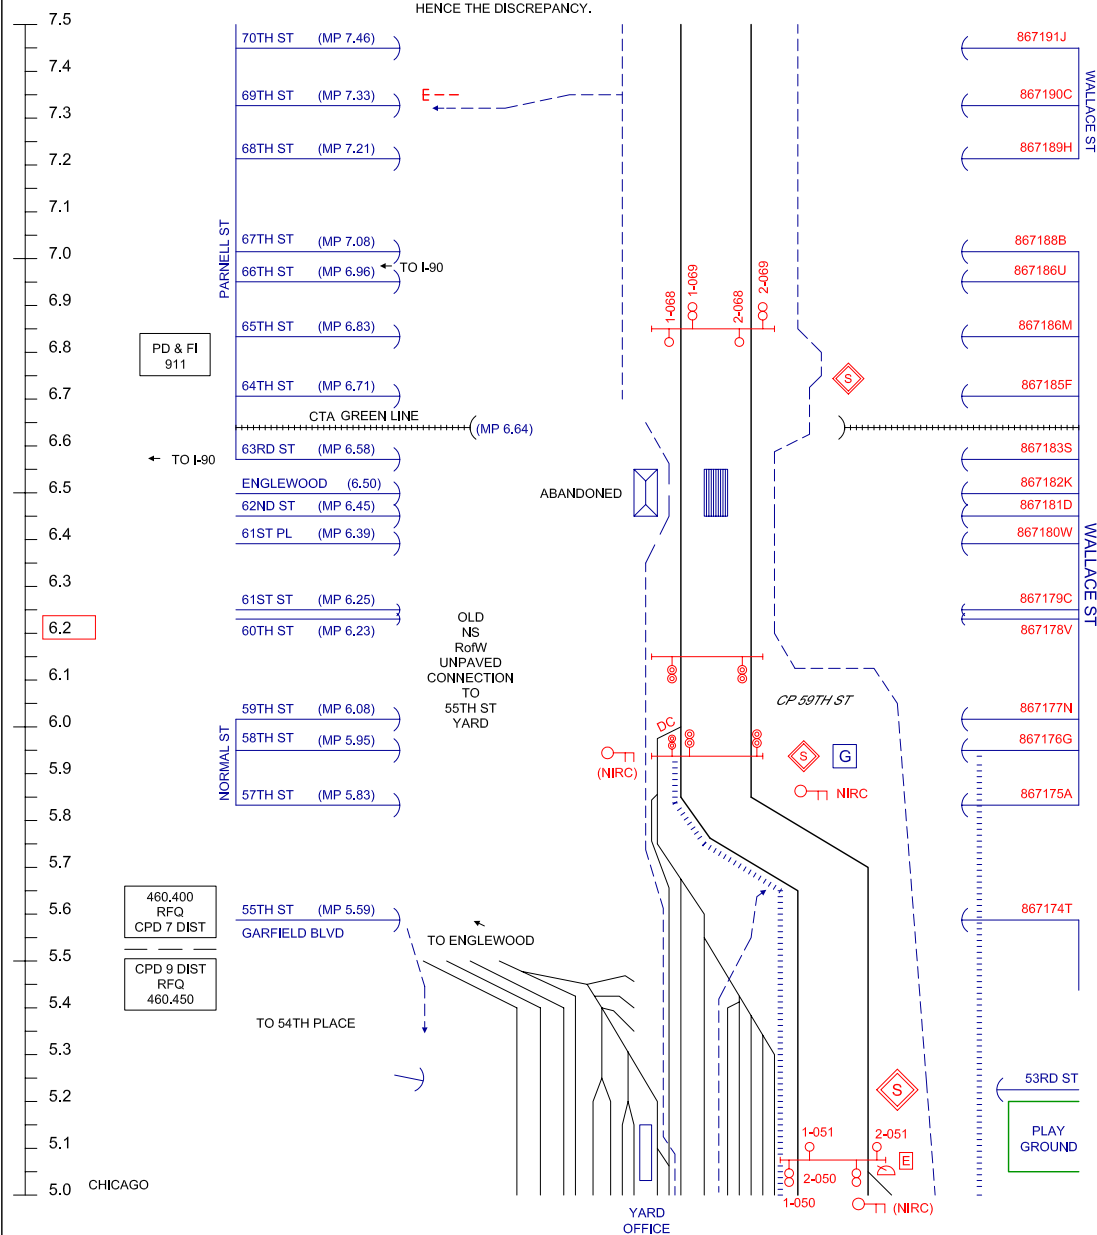

3°

NOTE:
THIS DRAWING IS A SCHEMATIC.
REAL LAYOUT FOR METRA MT'S
IS STRAIGHT.
NS YARD BENDS AROUND,
NOT METRA MT'S.

115 CWR

60/25 55/25	60/25 55/25	CTC RULES 10.1 10.3.4 REMOTE FROM CCF
55/25 60/25	55/25 60/25	CONTROL POINT RULE 9.12.1 TO ENTER MAIN TRACKS RULE 6.2
UNIT TRAINS OVER 100 TONS PER CAR 20 MPH 5 CARS WITH 6-AXLE UNIT 20 MPH 60/25	UNIT TRAINS OVER 100 TONS PER CAR 20 MPH 5 CARS WITH 6-AXLE UNIT 20 MPH 60/25	
CWI 1	CWI 2	F (N)

BRC DISPATCHER (708) 496-4101.3
(CLEARING YARD) (708) 496-4045 FAX


C 3,7 S 3 L 31 W 17

3151, 3152
3213, 3214


CUS SERVICE / SOUTHWEST SUBDISTRICT

P-17

NOTE:
AT BELT JCT STOP SIGNAL CANNOT BE PASSED
UNTIL CONTROL OPERATOR CONFERS WITH
DISPATCHER OF BRC OR CSX RAILROAD

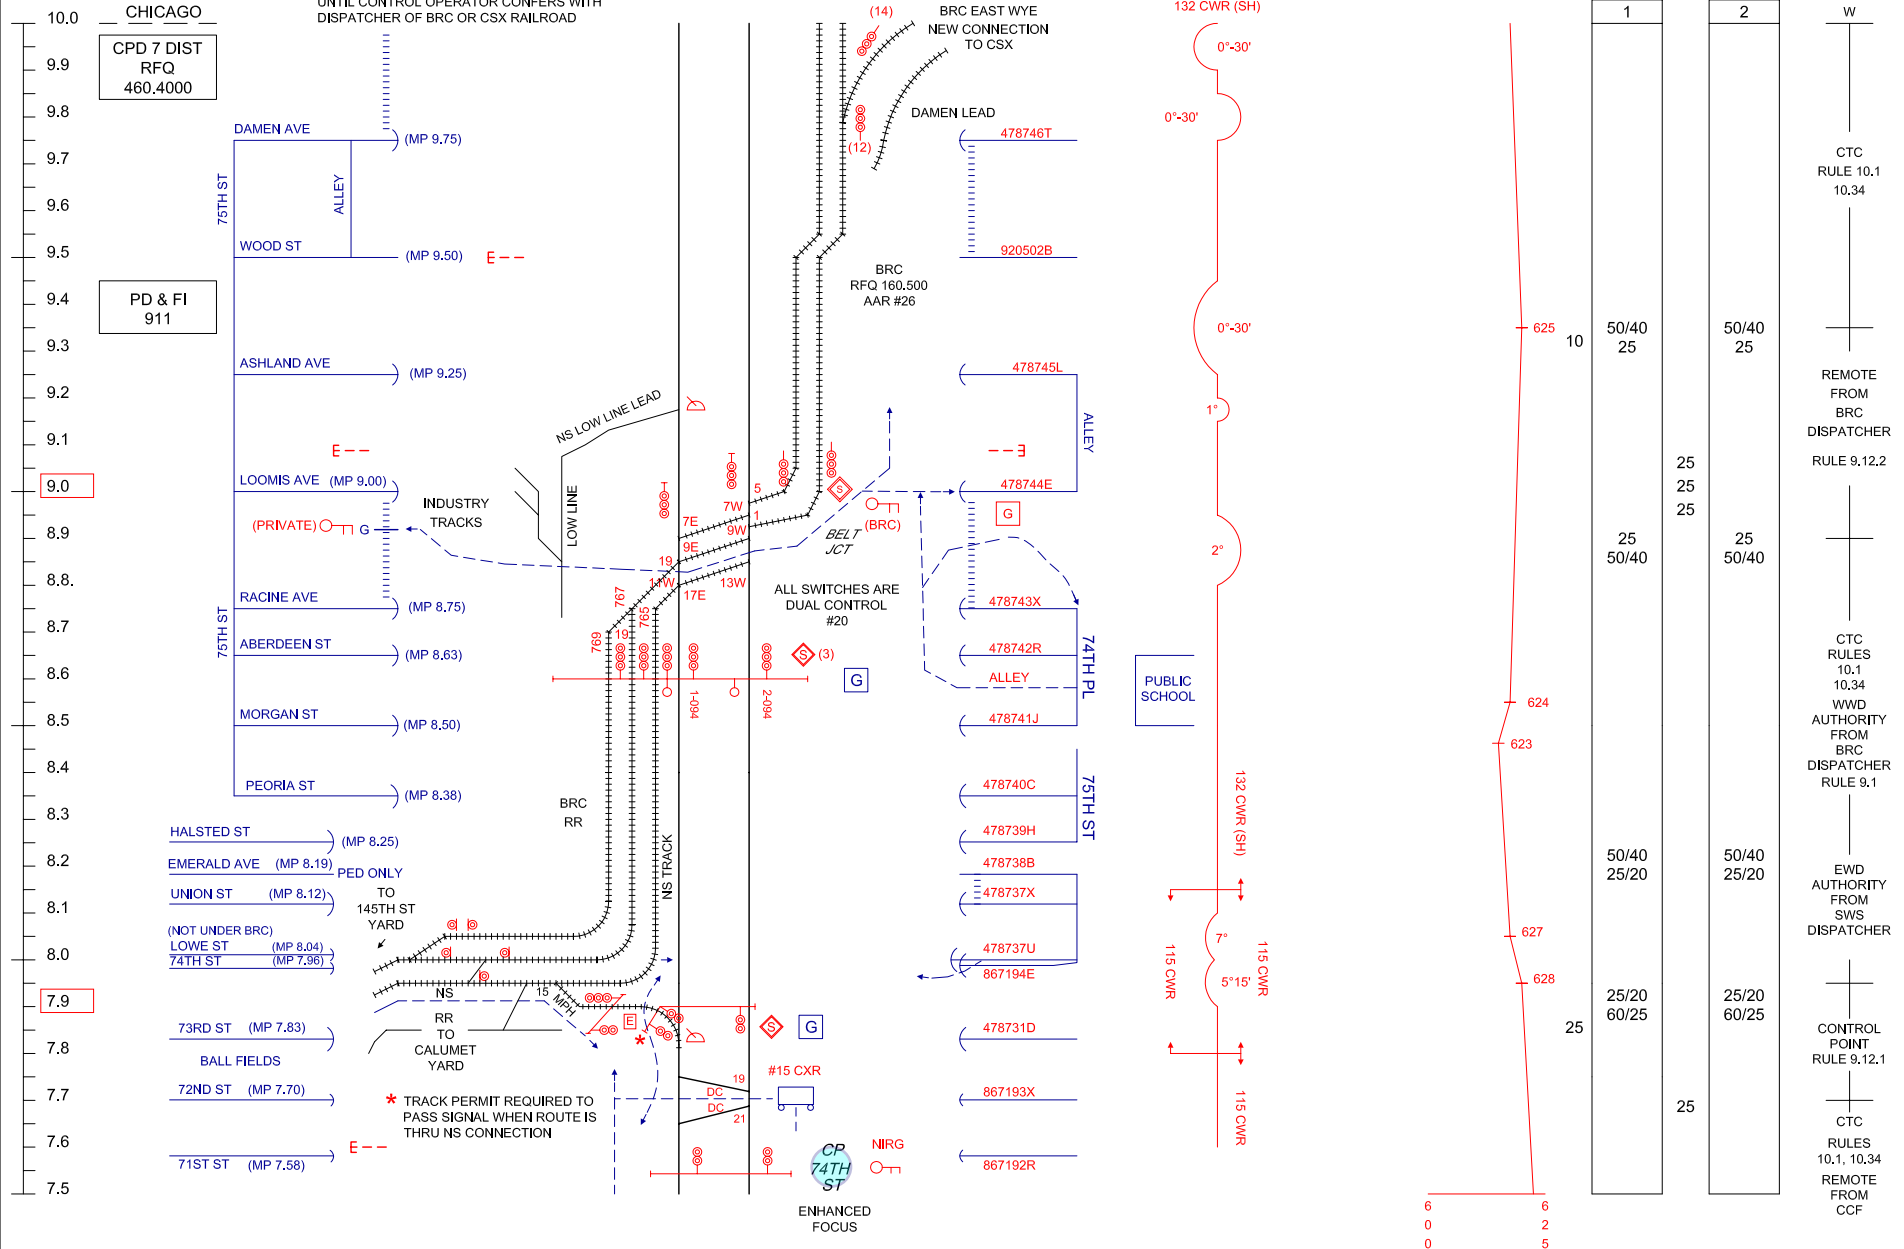

RFQ 160.440 AAR 22

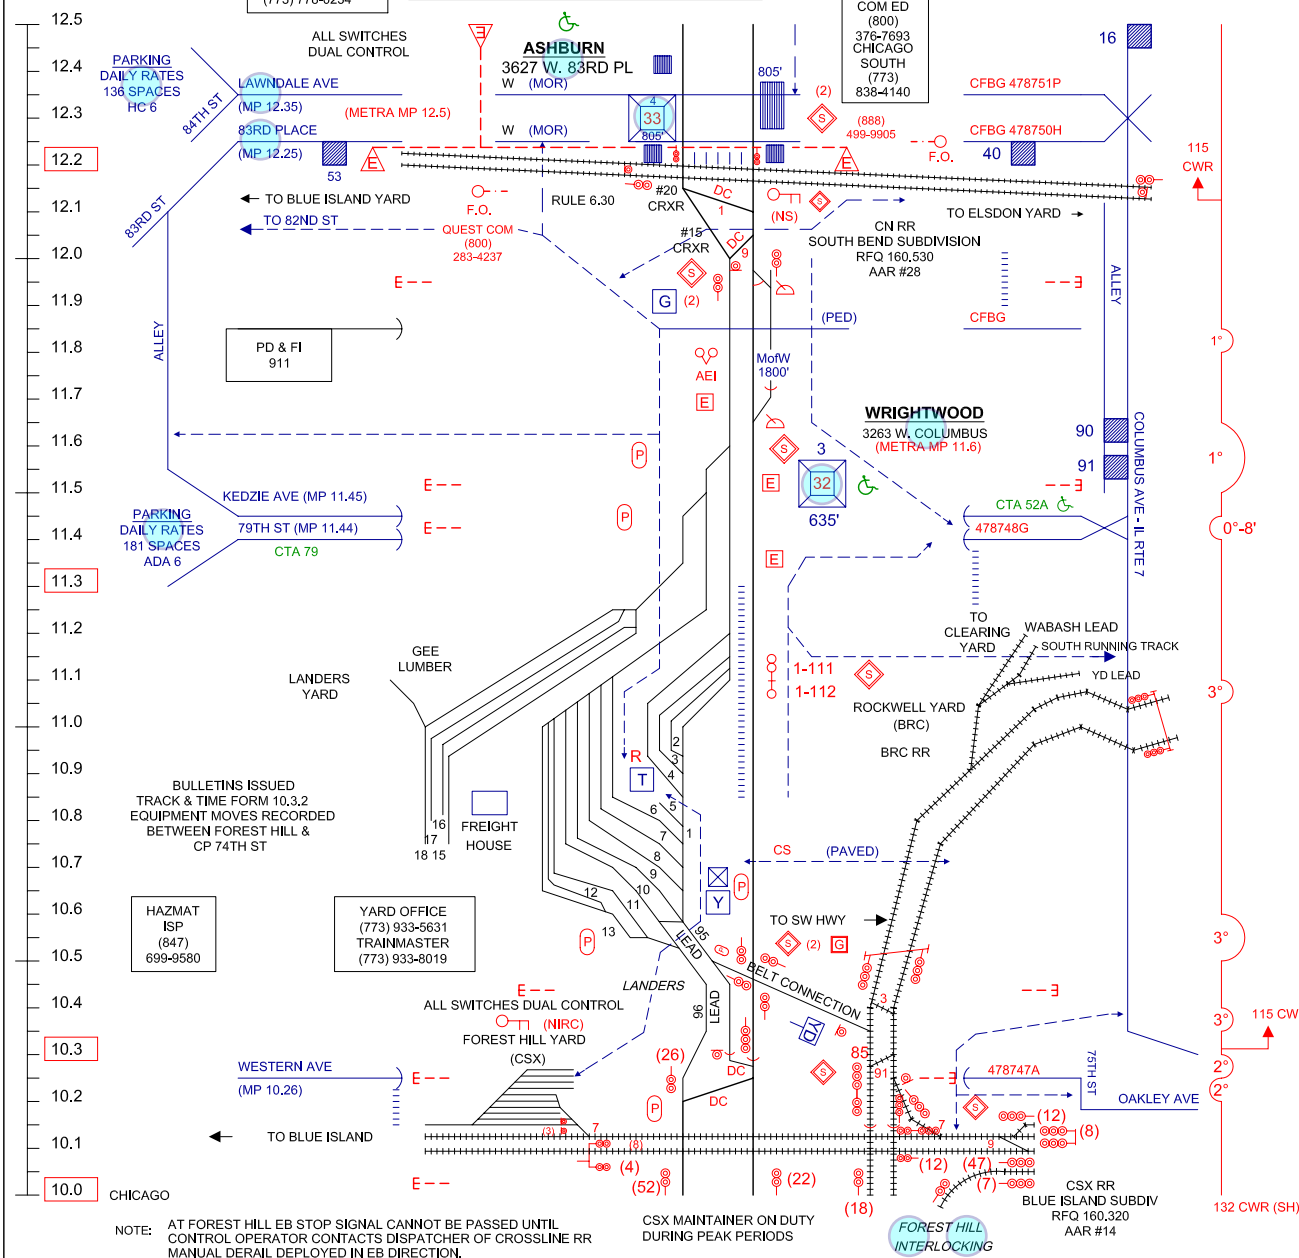

6	6
0	2
5	5

25*
79/40
1

	79/40
0	2
0	50/40 25* 40/30
5	

CTC
RULES
10.1-10.3.4

CONTROLLED
BY
LANDERS
OPERATOR
RULE 9.12.2

CTC
RULES
10.1-10.3.4

REMOTE
FROM
LANDERS
OPERATOR

30 30 1	10	50/40
	25	MAIN
		30
		30
		2

CONTROLLED
FROM
CLEARING
YARD (CSX)
RULE 9.12.2

F

* SPEED WHEN CROSSING CN DIAMOND

FARE ZONE C


REV 04-15-06

1 16 31,32

3212, 3213


CUS SERVICE / SOUTHWEST SUBDISTRICT

P-18

 

CONTROL POINT PHONE NUMBERS
 IHB DISPATCHER (219) 989-4815 (708) 832-2087
 LANDERS OPERATOR (773) 933-5631 (773) 778-0234
 SWS DISPATCHER (312) 322-2858

RFQ 160.440 AAR 22

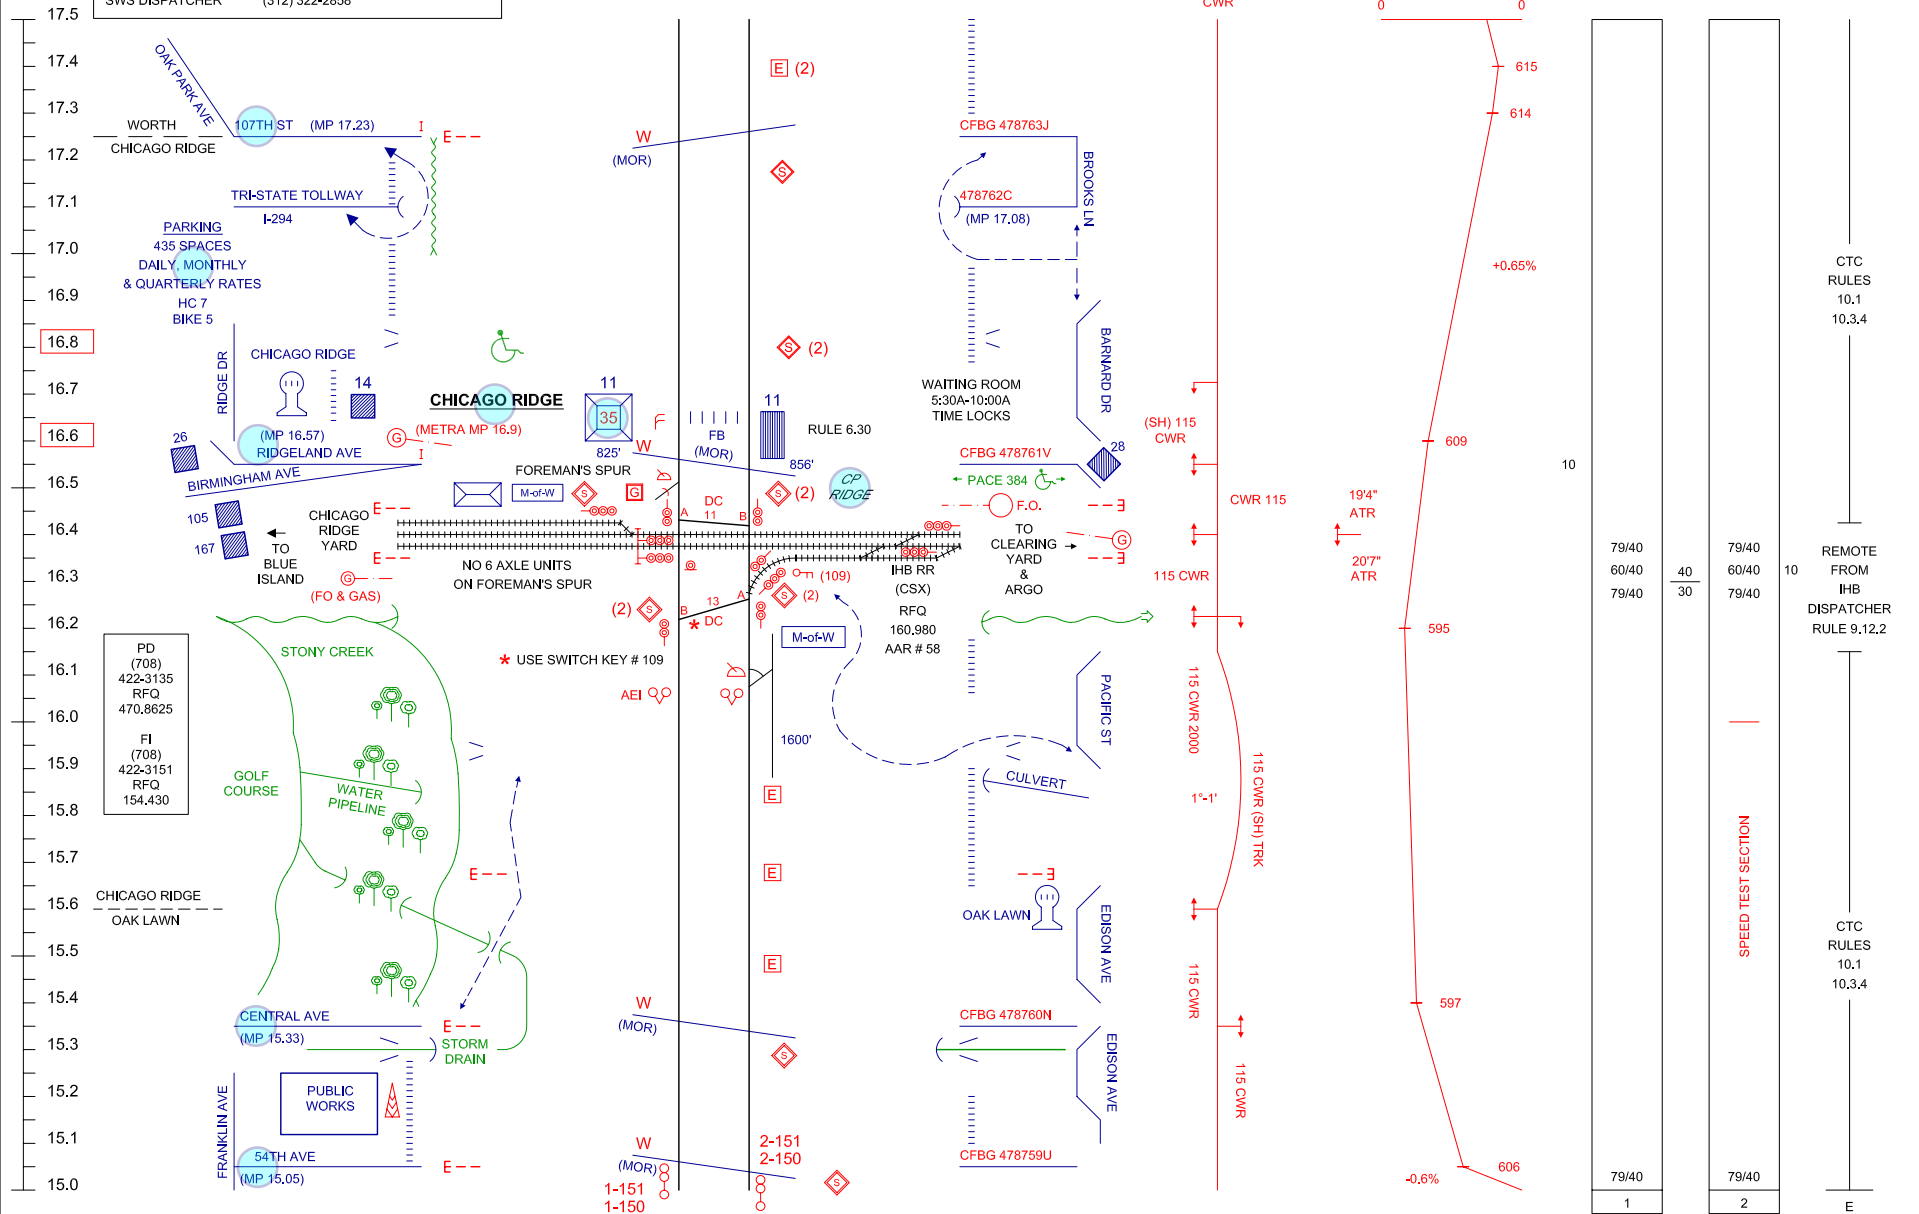

FARE ZONE D


REV 05-15-08

3 18 36

3211, 3275

CUS SERVICE / SOUTHWEST SUBDISTRICT



P-20

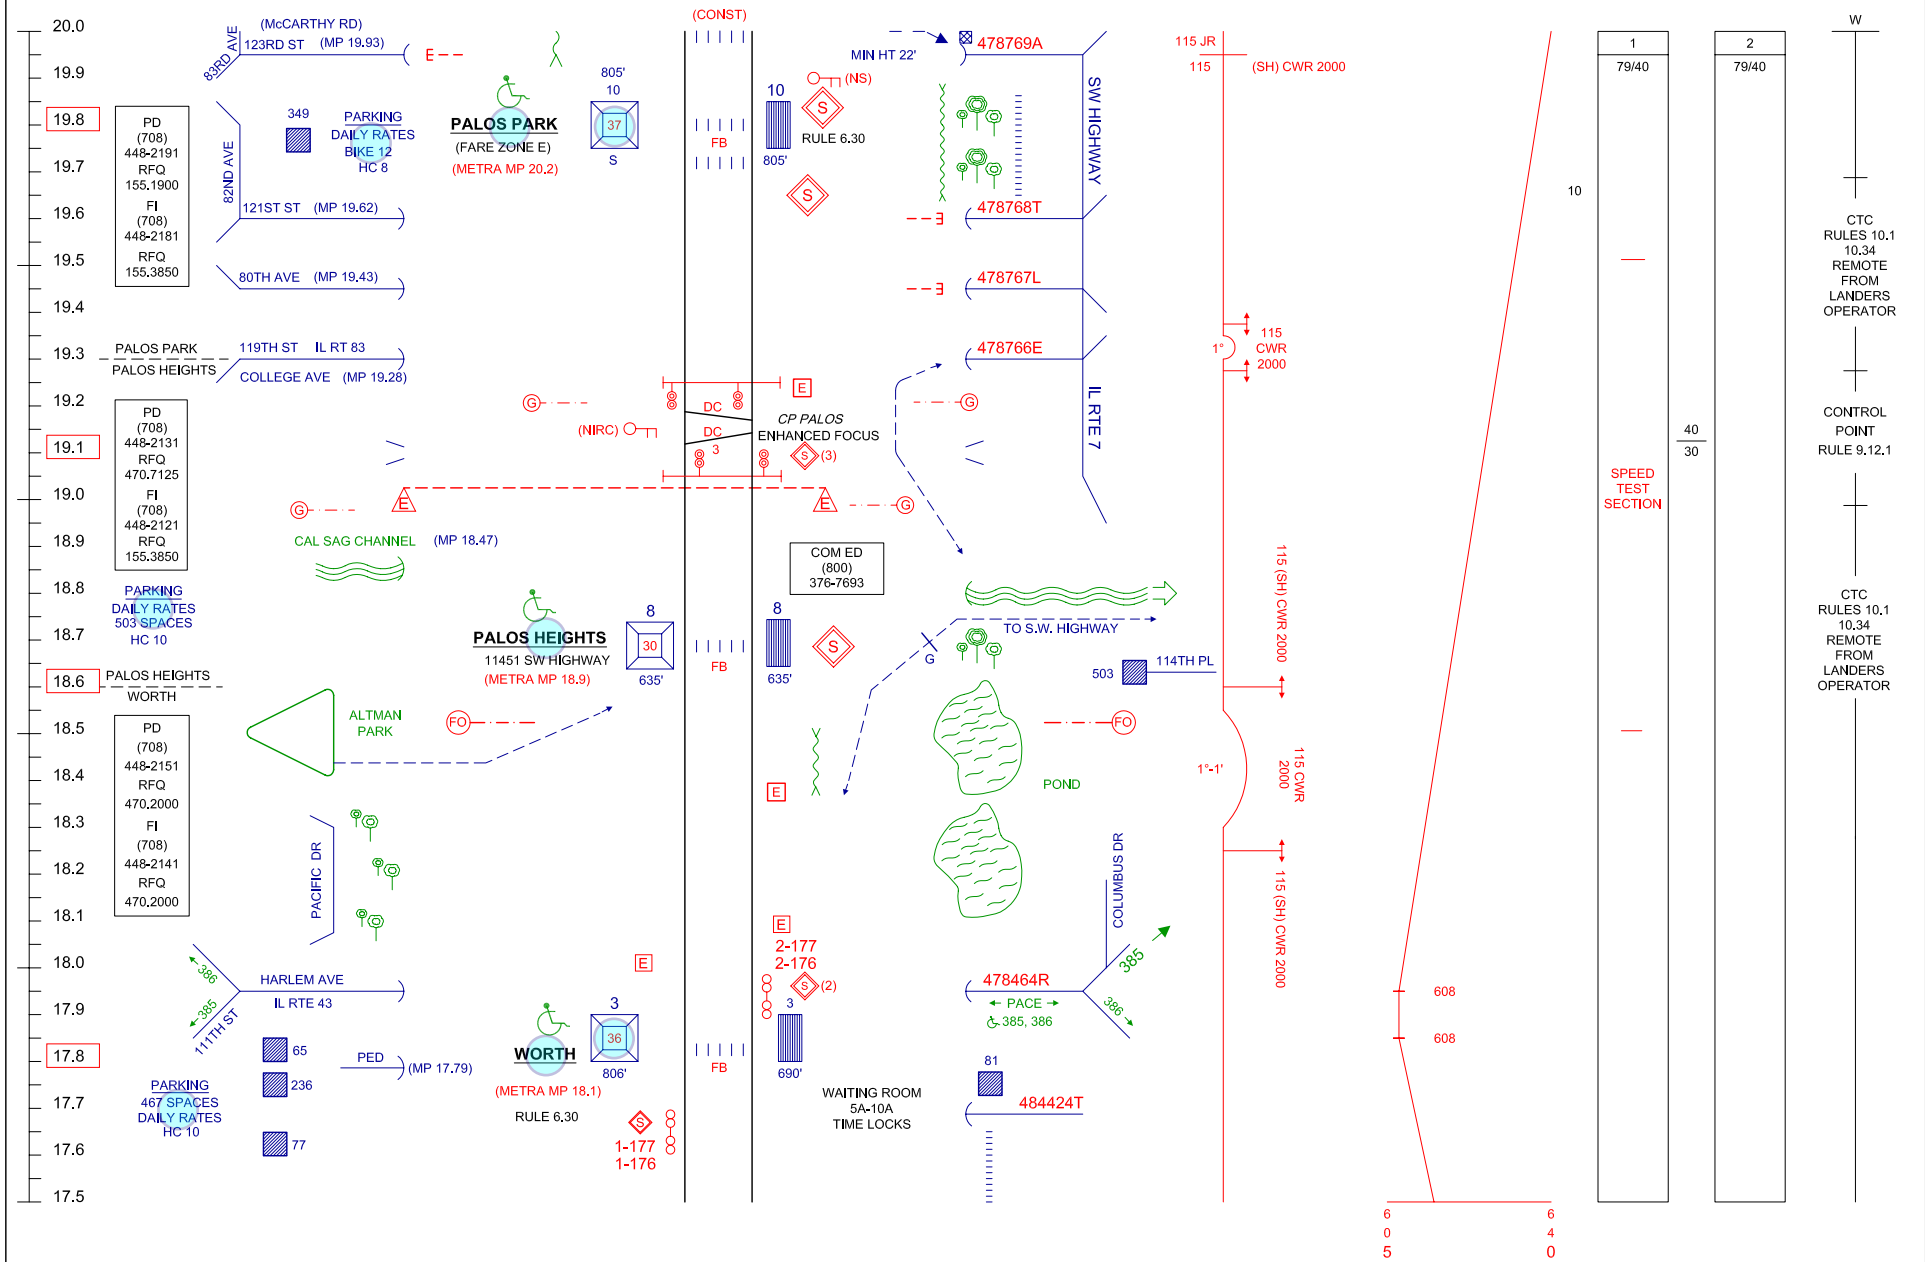

CONTROL POINT PHONE NUMBERS
 LANDERS OPERATOR (773) 933-5631 (773) 778-0234
 SWS DISPATCHER (312) 322-2858

RFQ 160.440 AAR 22

22.5
22.4
22.3
22.2
22.1
22.0
21.9
21.8
21.7
21.6
21.5
21.4
21.3
21.2
21.1
21.0
20.9
20.8
20.7
20.6
20.5
20.4
20.3
20.2
20.1
20.0

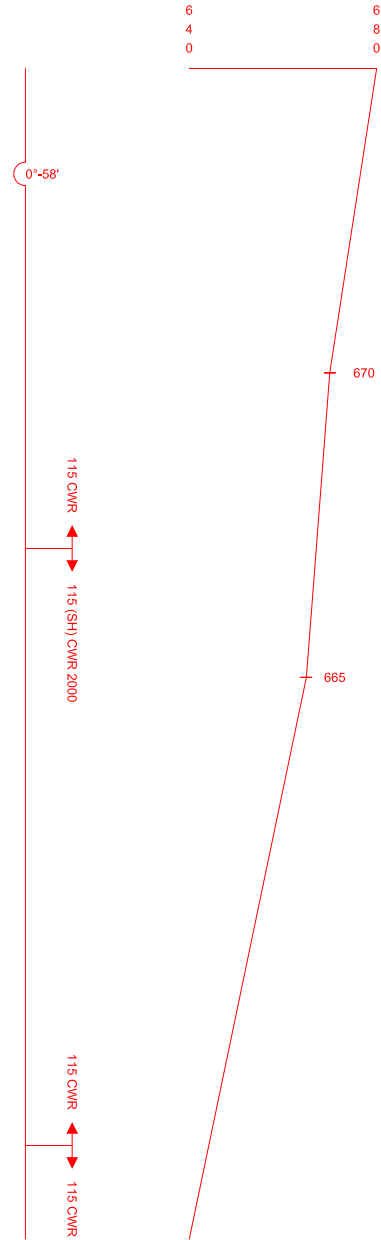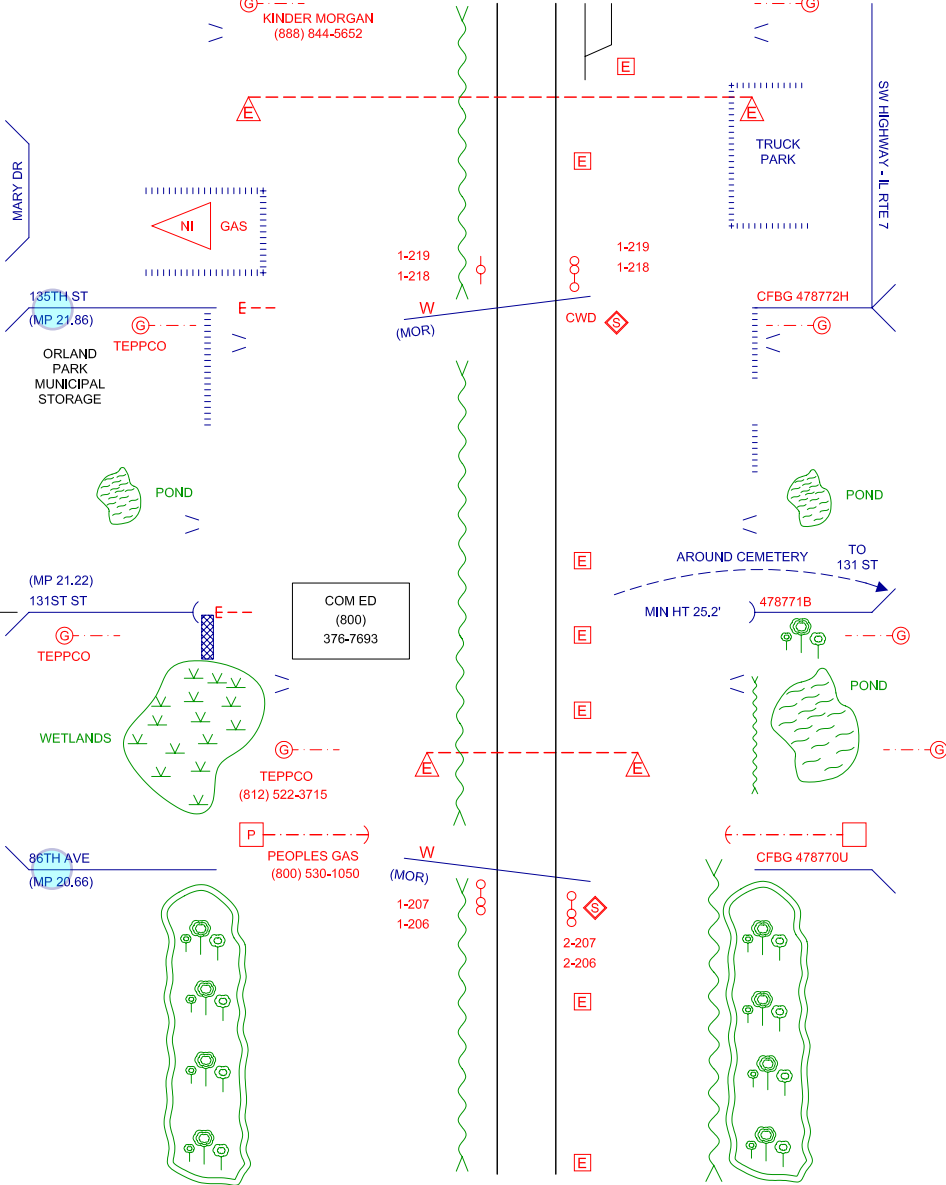

			CTC RULES 10.1-10.3.4 REMOTE FROM LANDERS OPERATOR
79/40	79/40	E	
1	2		

FARE ZONE E

REV 05-15-08


13 41 37.81

3274
3345, 3346

CUS SERVICE / SOUTHWEST SUBDISTRICT


P-22

P-23

 

CONTROL POINT PHONE NUMBERS
 LANDERS OPERATOR (773) 933-5631
 SWS DISPATCHER (312) 322-2858

RFQ 160.440 AAR 22

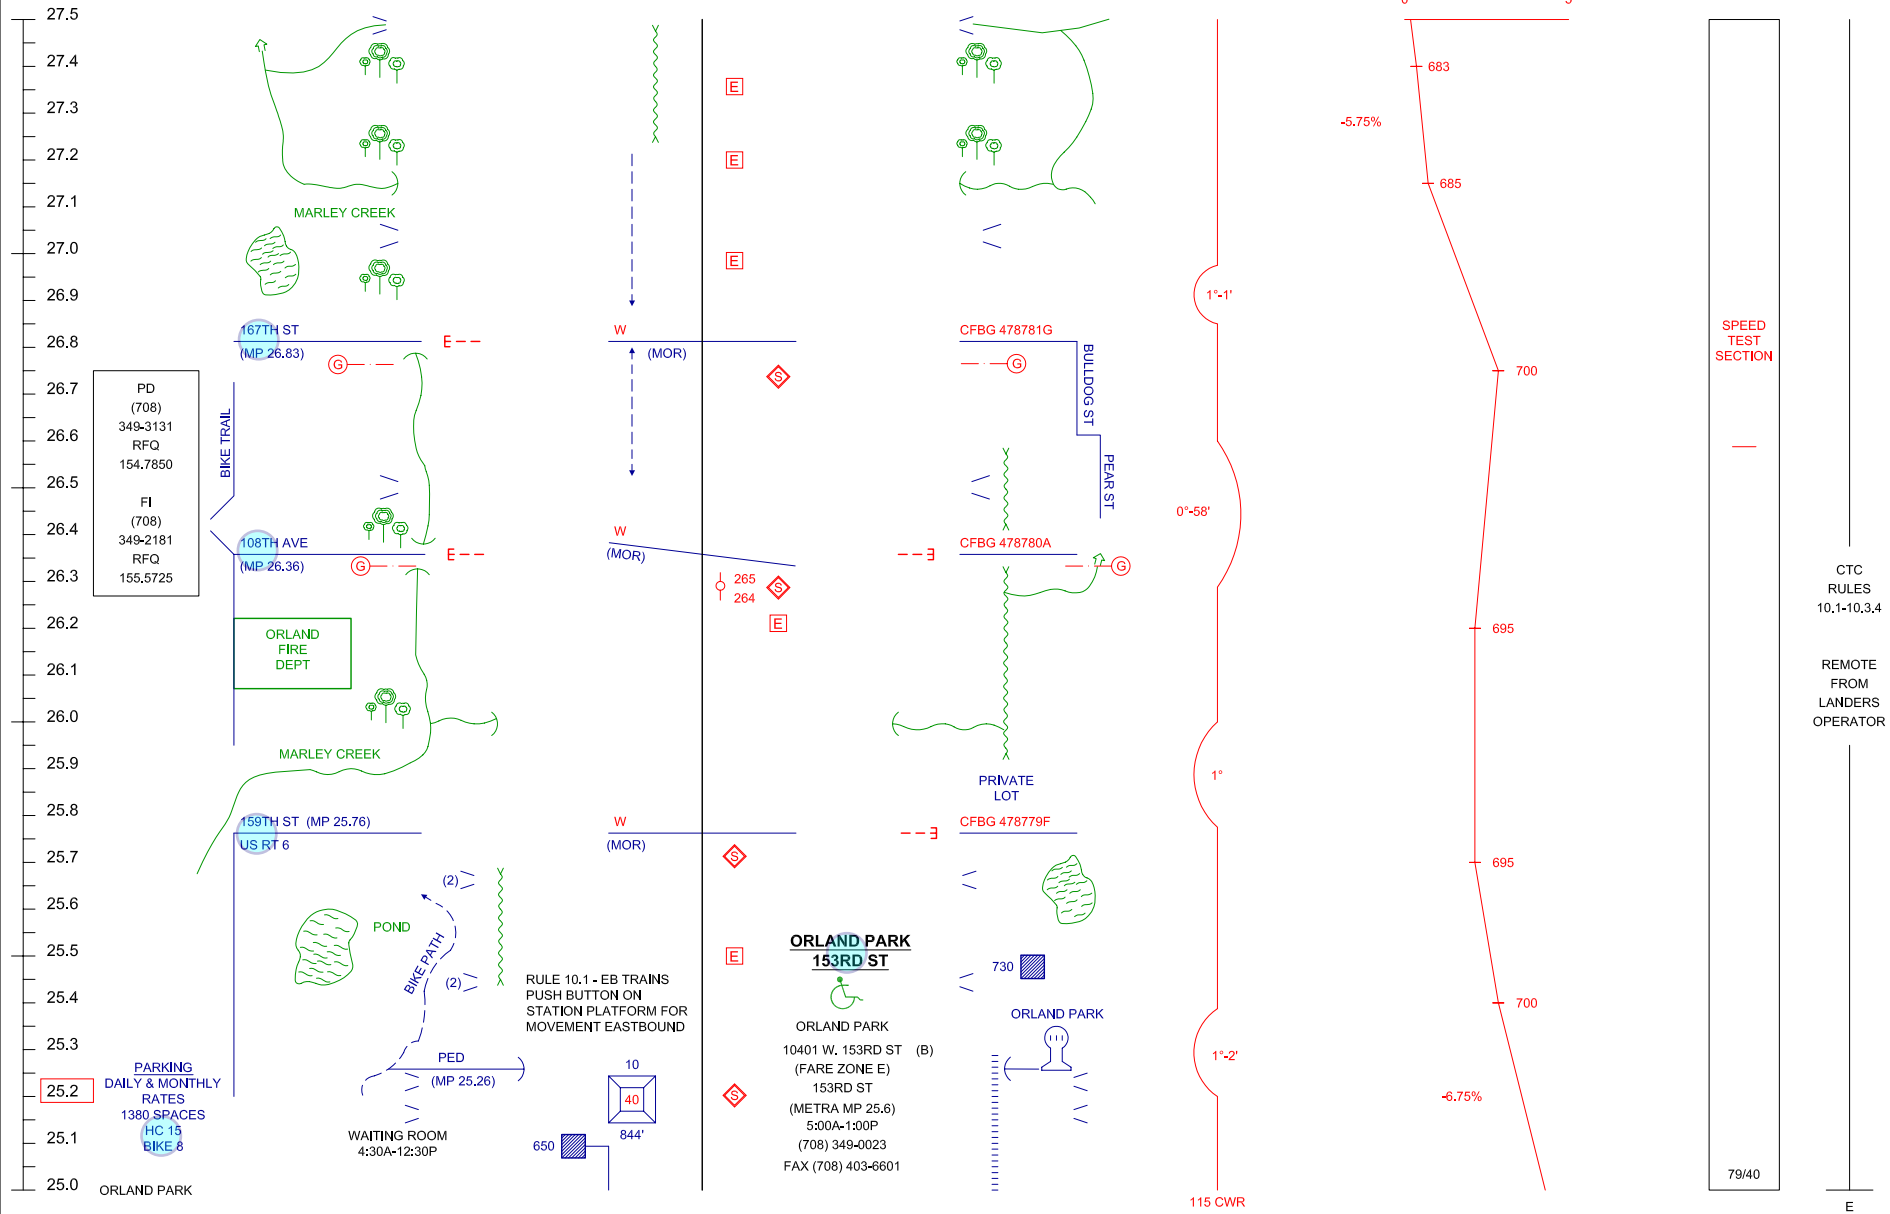

FARE ZONE F


REV 05-15-08

13 41 81


3345, 3423


CUS SERVICE \ SOUTHWEST SUBDISTRICT

P-24

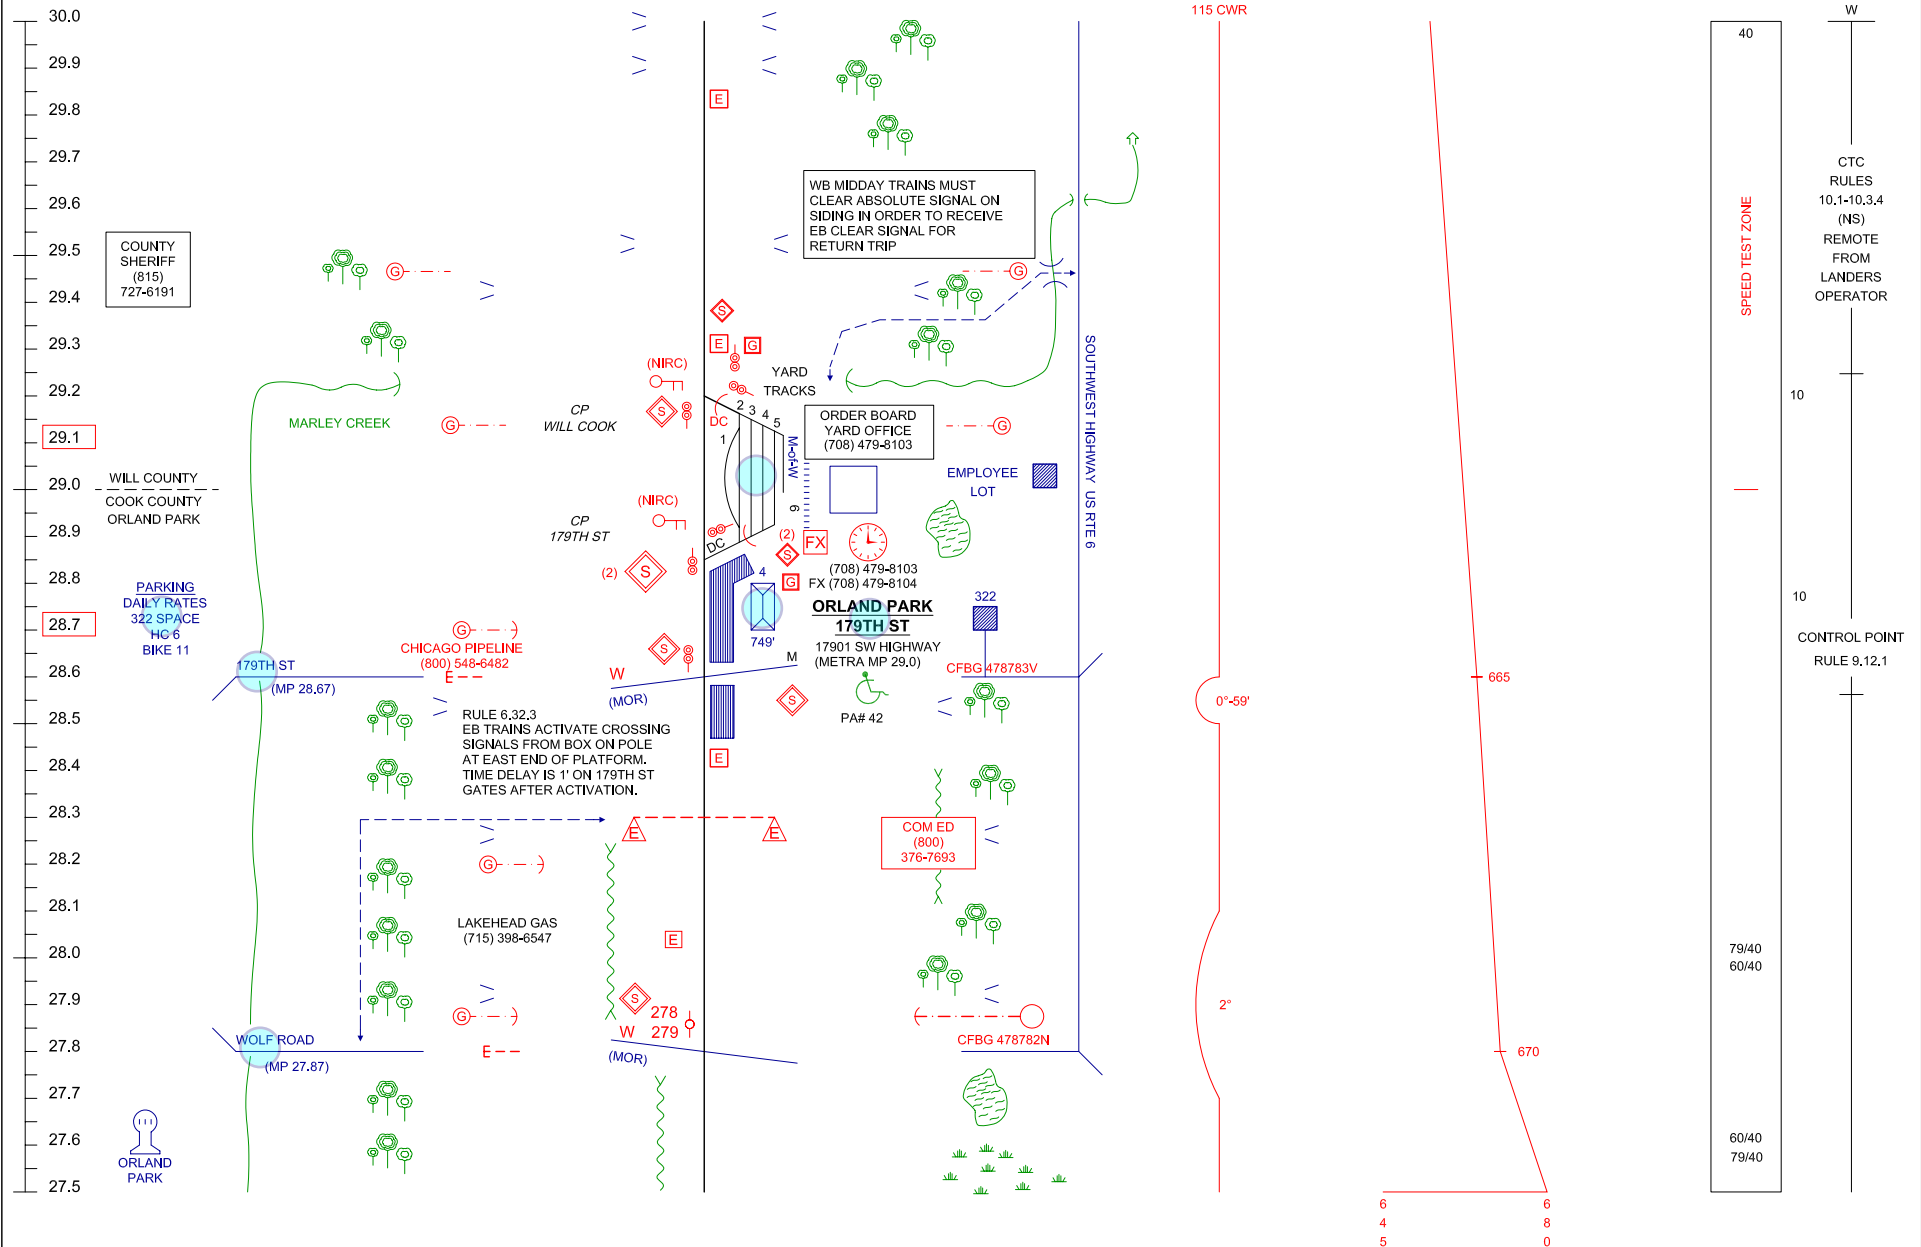


RFQ 160.440 AAR 22

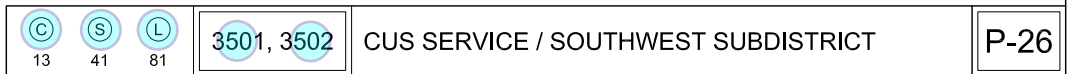

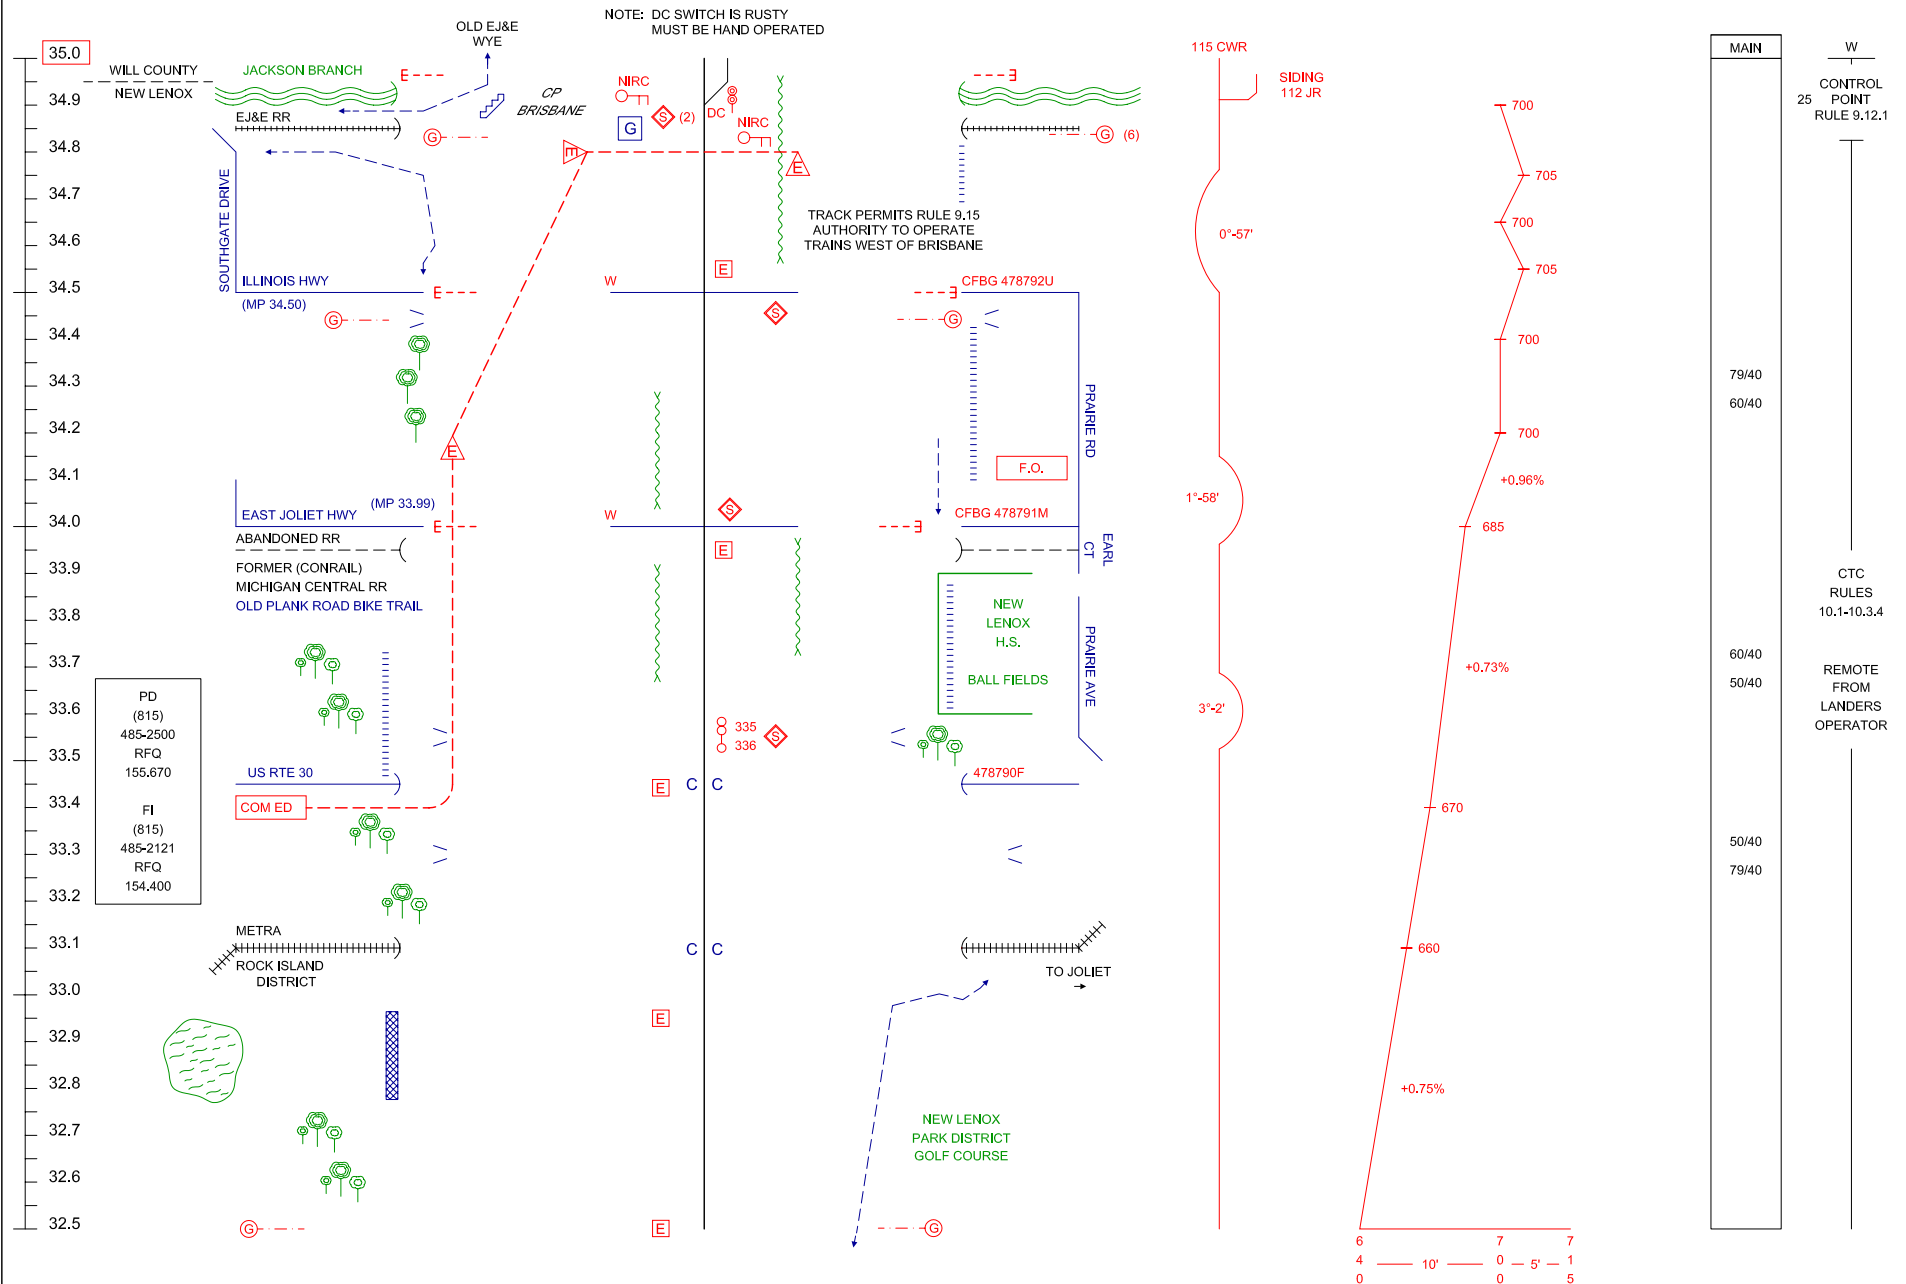

CONTROL POINT PHONE NUMBER
LANDERS OPERATOR (773) 933-5631

RFQ 160.440 AAR 22

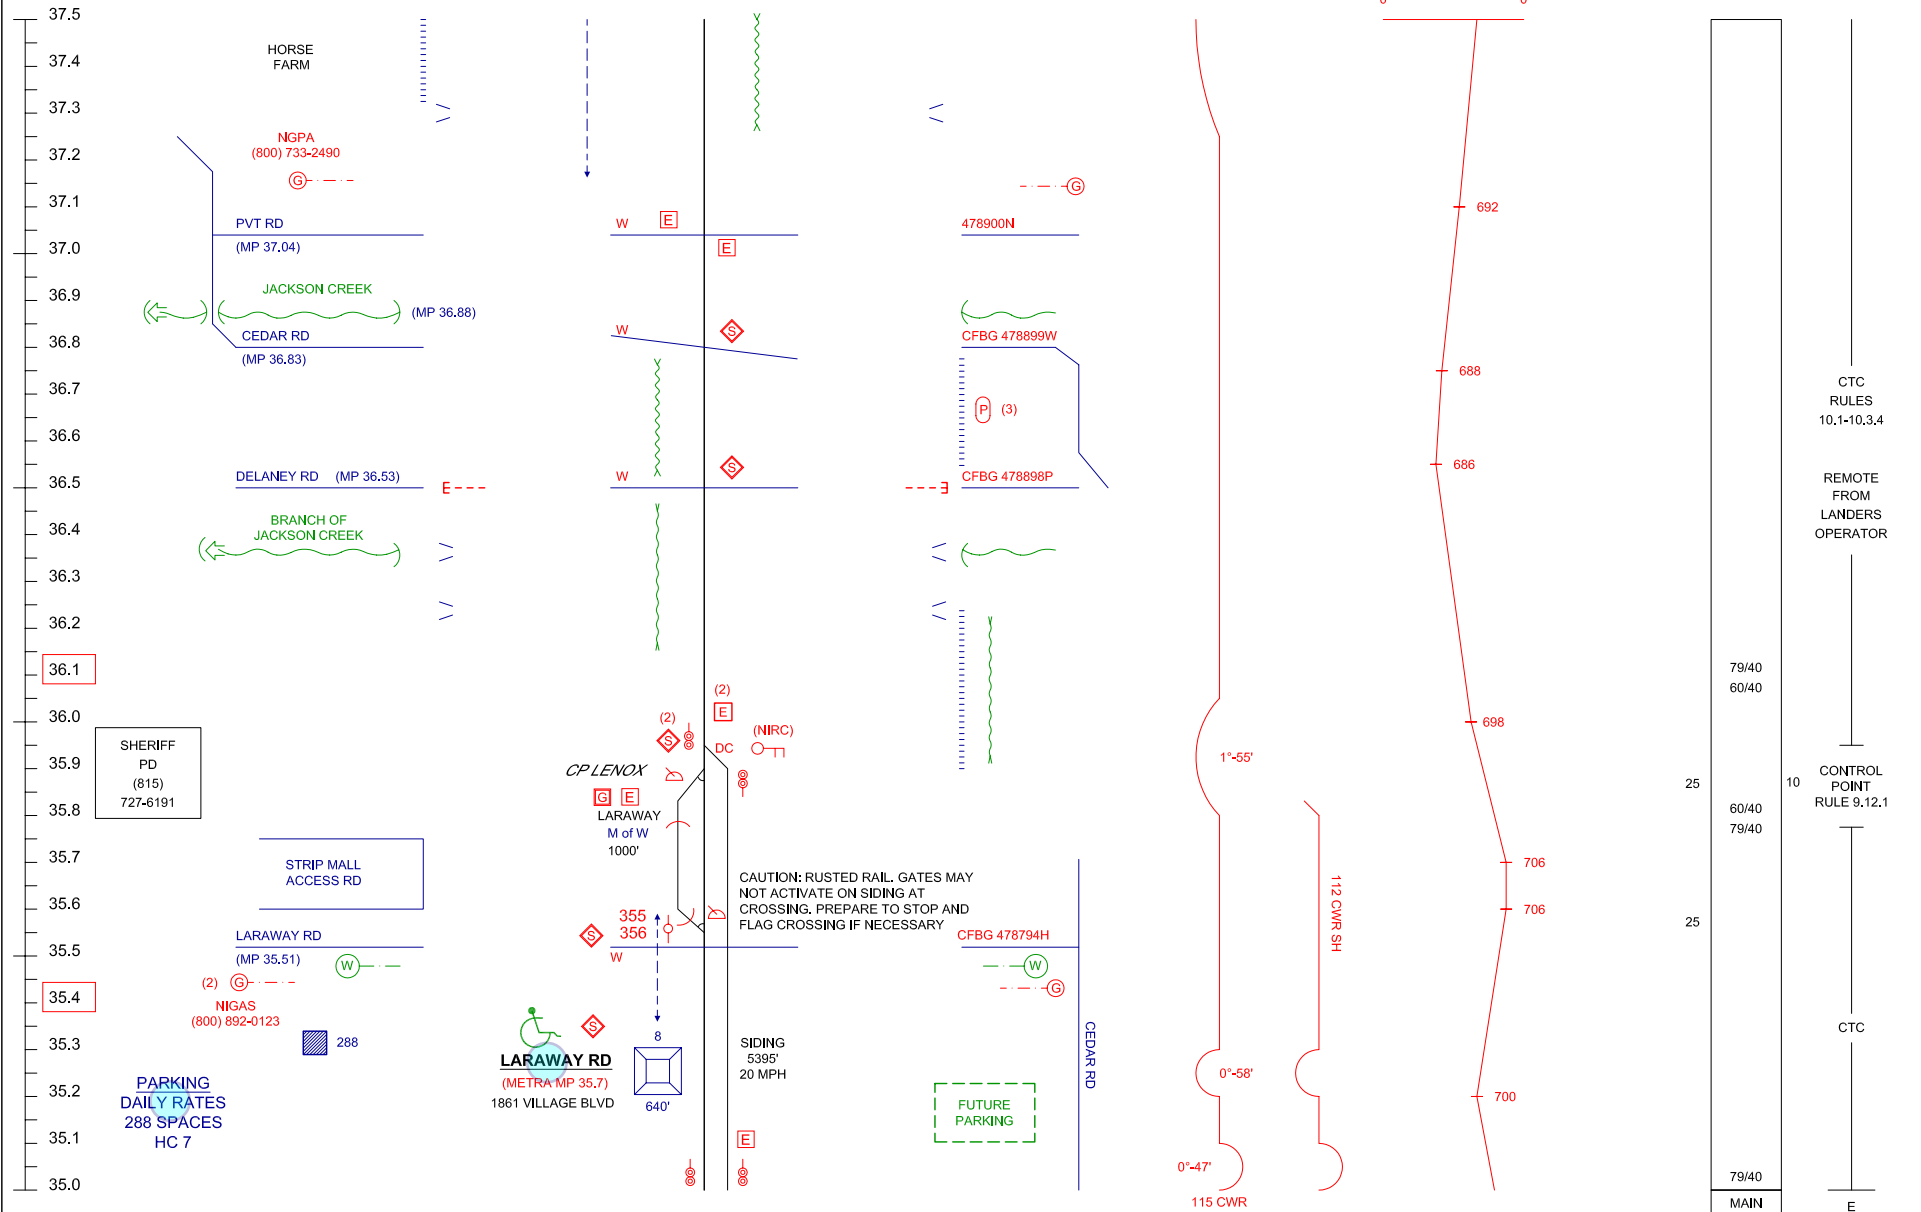


REV 04-15-06

11 41 86

3589


CUS SERVICE / SOUTHWEST SUBDISTRICT

P-28

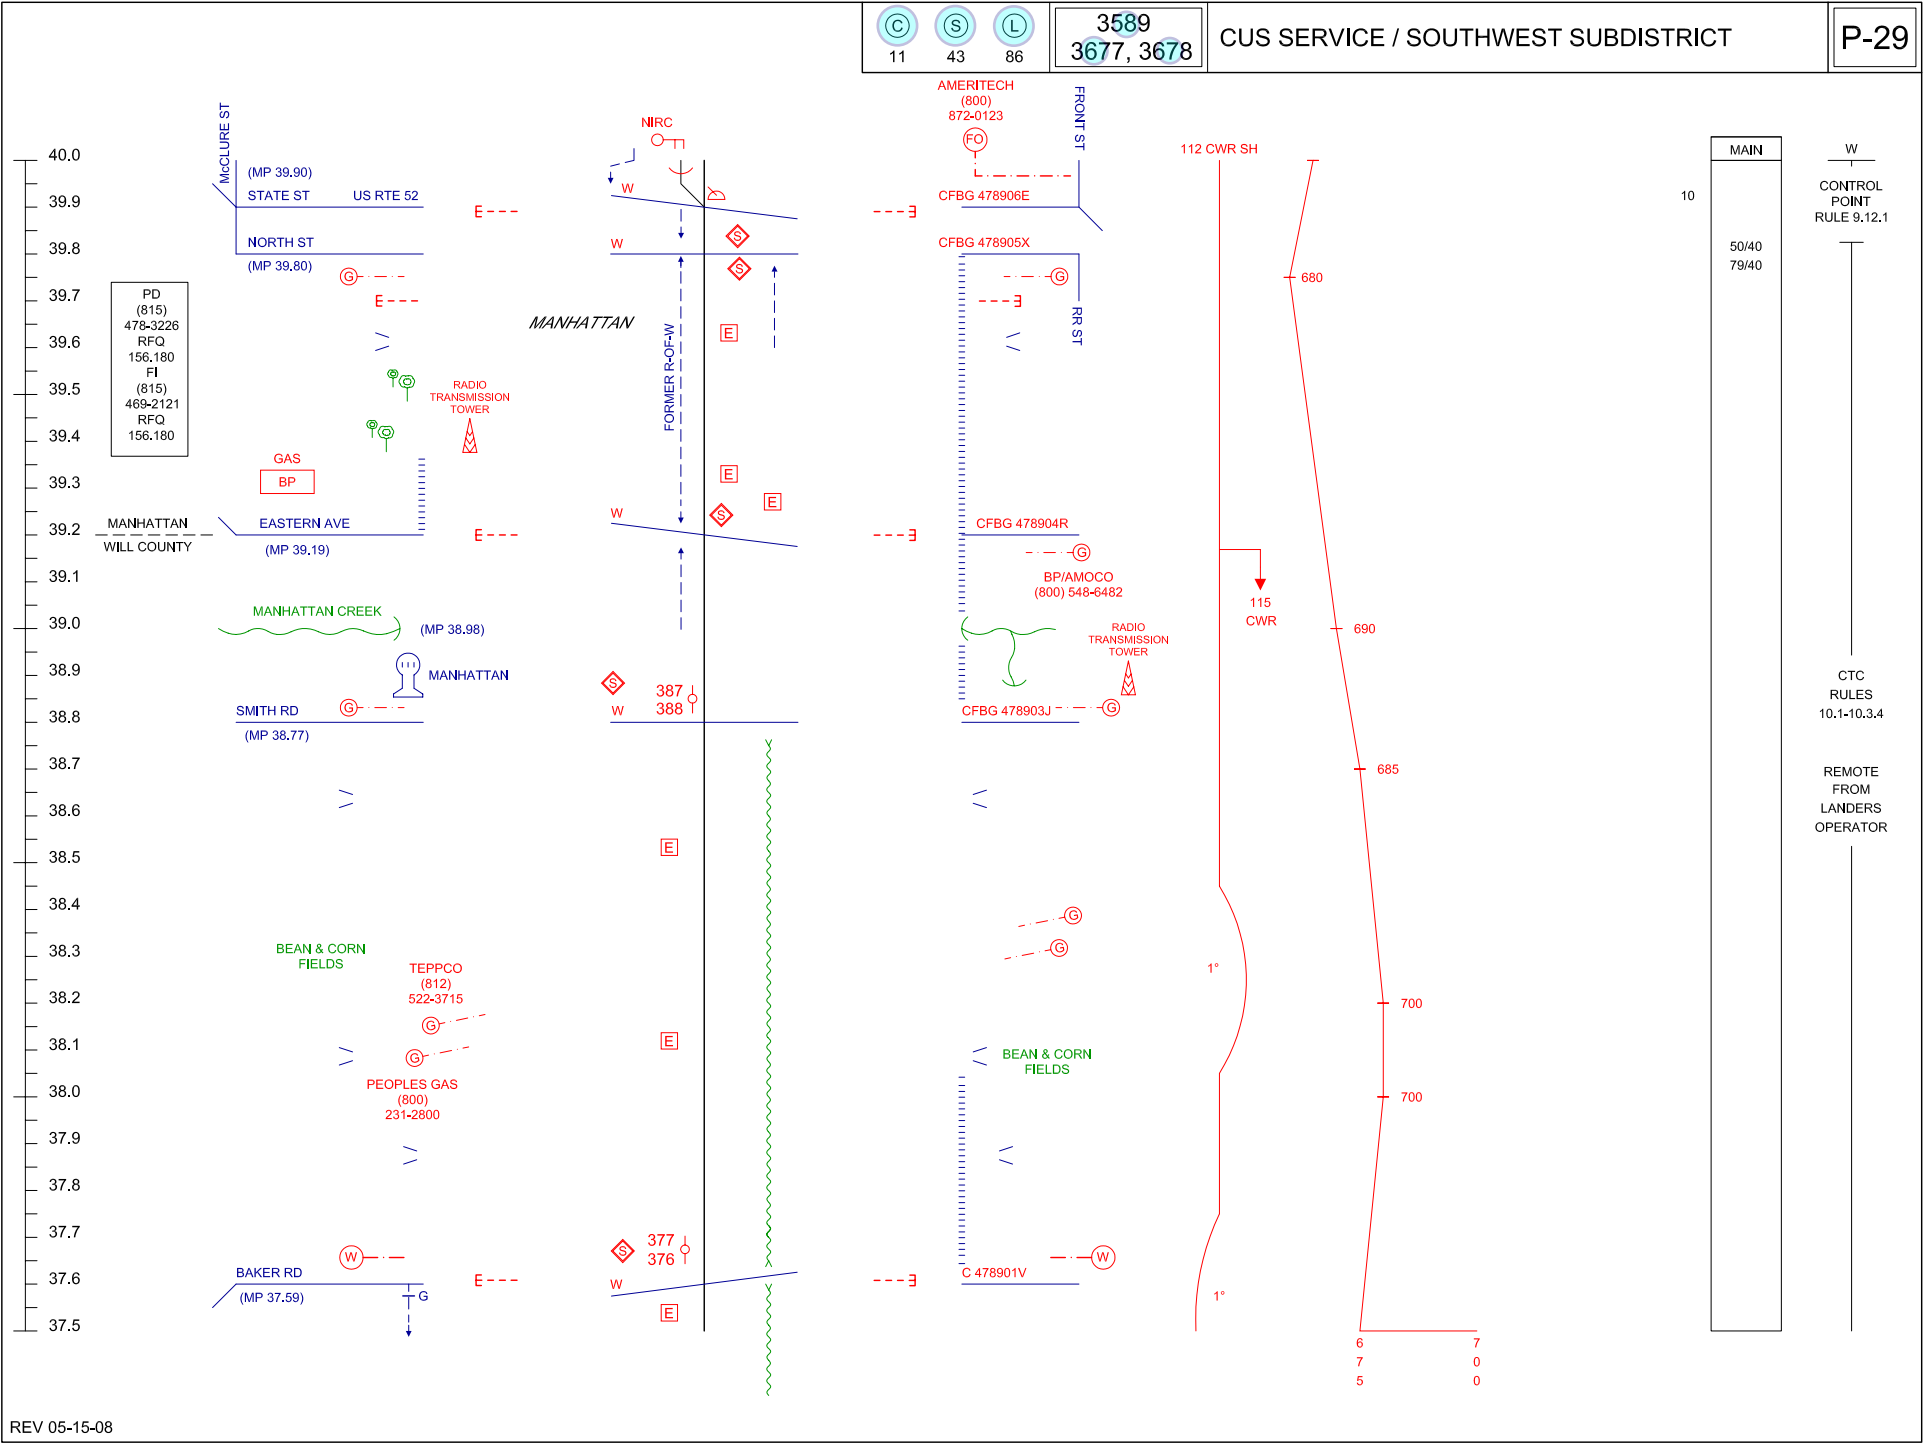

CONTROL POINT PHONE NUMBER
LANDER OPERATOR (312) 933-5631

RFQ 160.440 AAR 22

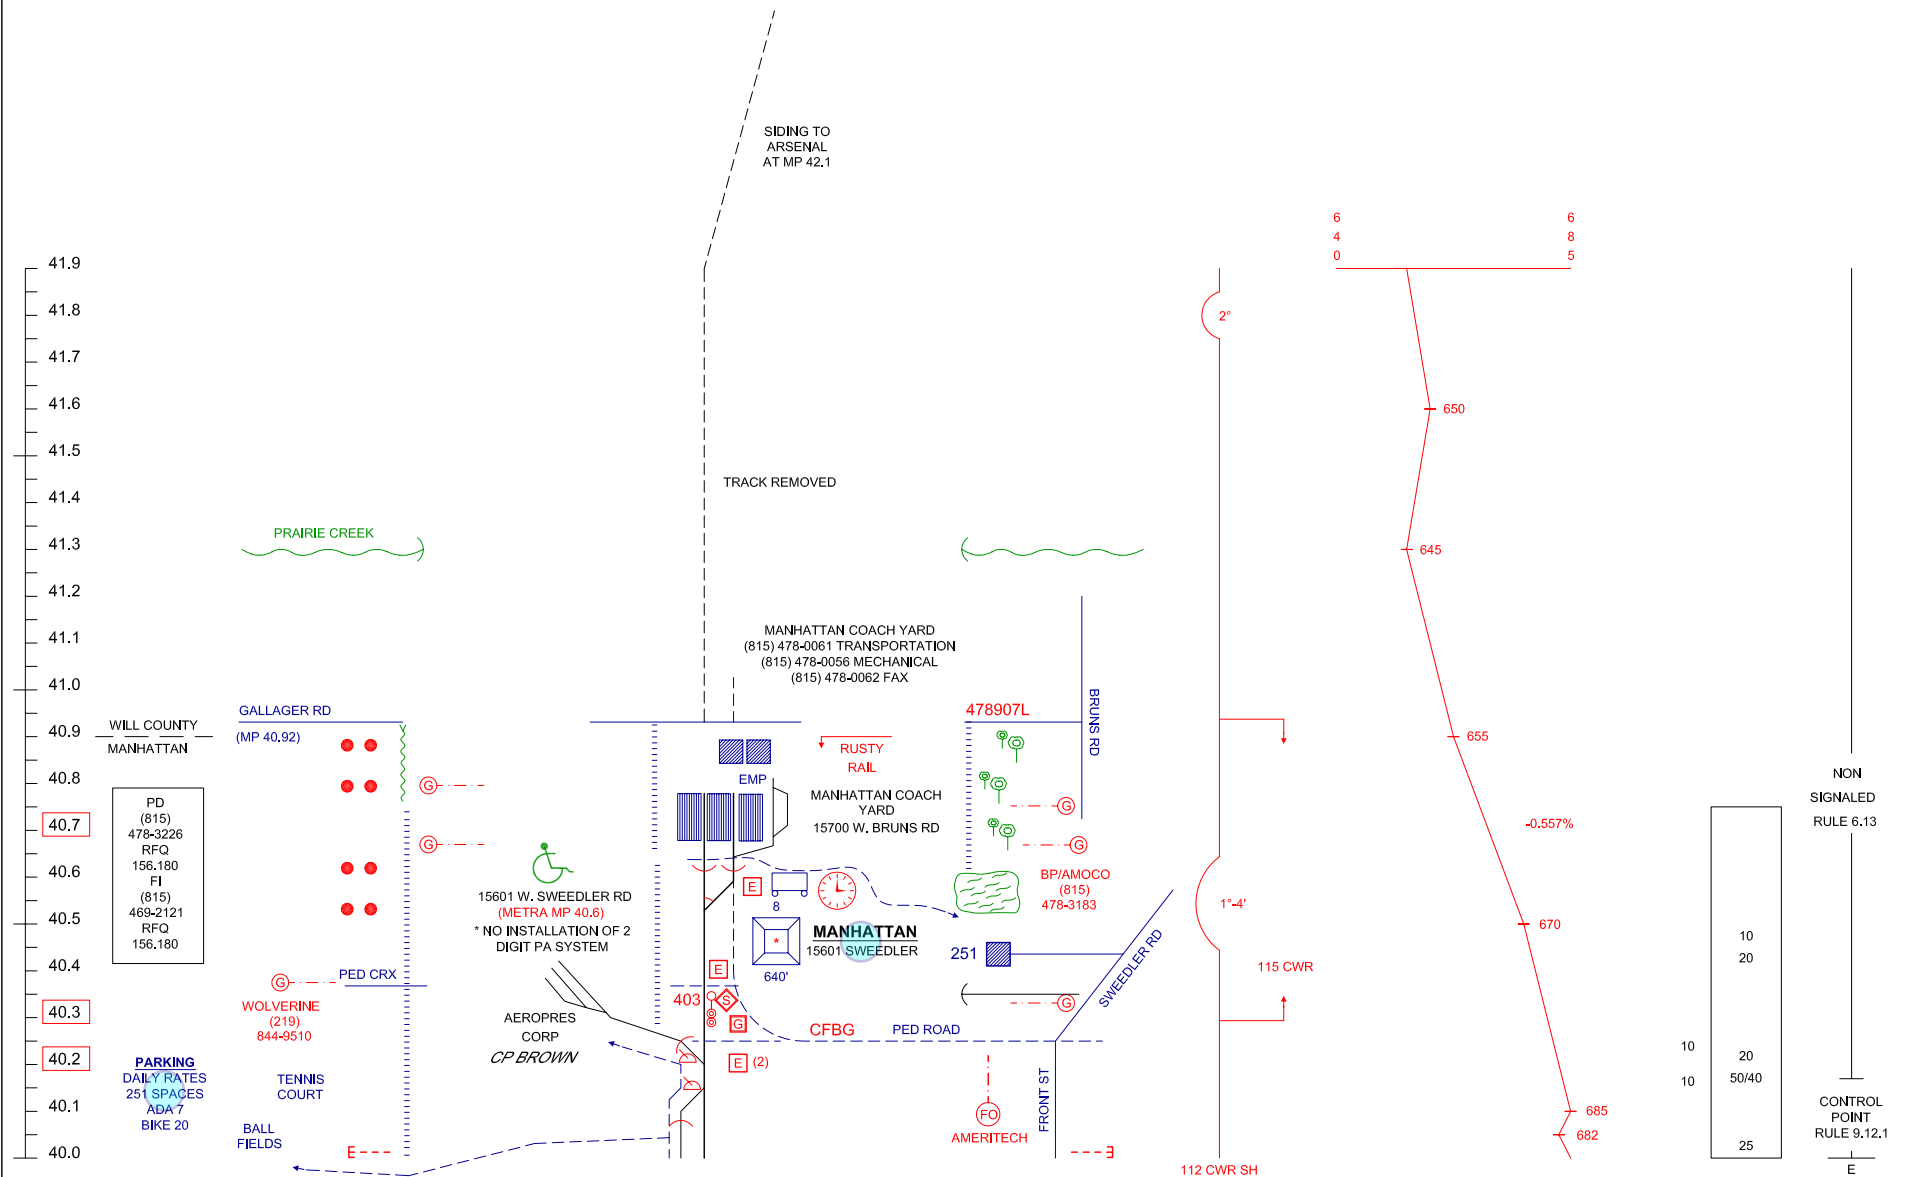

REV 05-15-08

11 43 86

3677

CUS SERVICE / SOUTHWEST SUBDISTRICT

P-30