



NICTD DOUBLE TRACK NWI
PROPOSED TRACK SCHEMATIC
CONCEPTUAL LAYOUT

CARROLL AVENUE TO CP 58.8
MP 32.2 TO MP 58.8

DATE: 05/12/2017

HDR

CHECKED *Z. HARTJES*

DRAWN *M. QUALY* CHECKED *Z. HARTJES*

STATUS
PRELIMINARY


NICTO

Track Chart Sheets 1-6.dgn

BY: ZHARTJES

TIME: 7:29:26 PM

5/17/2017

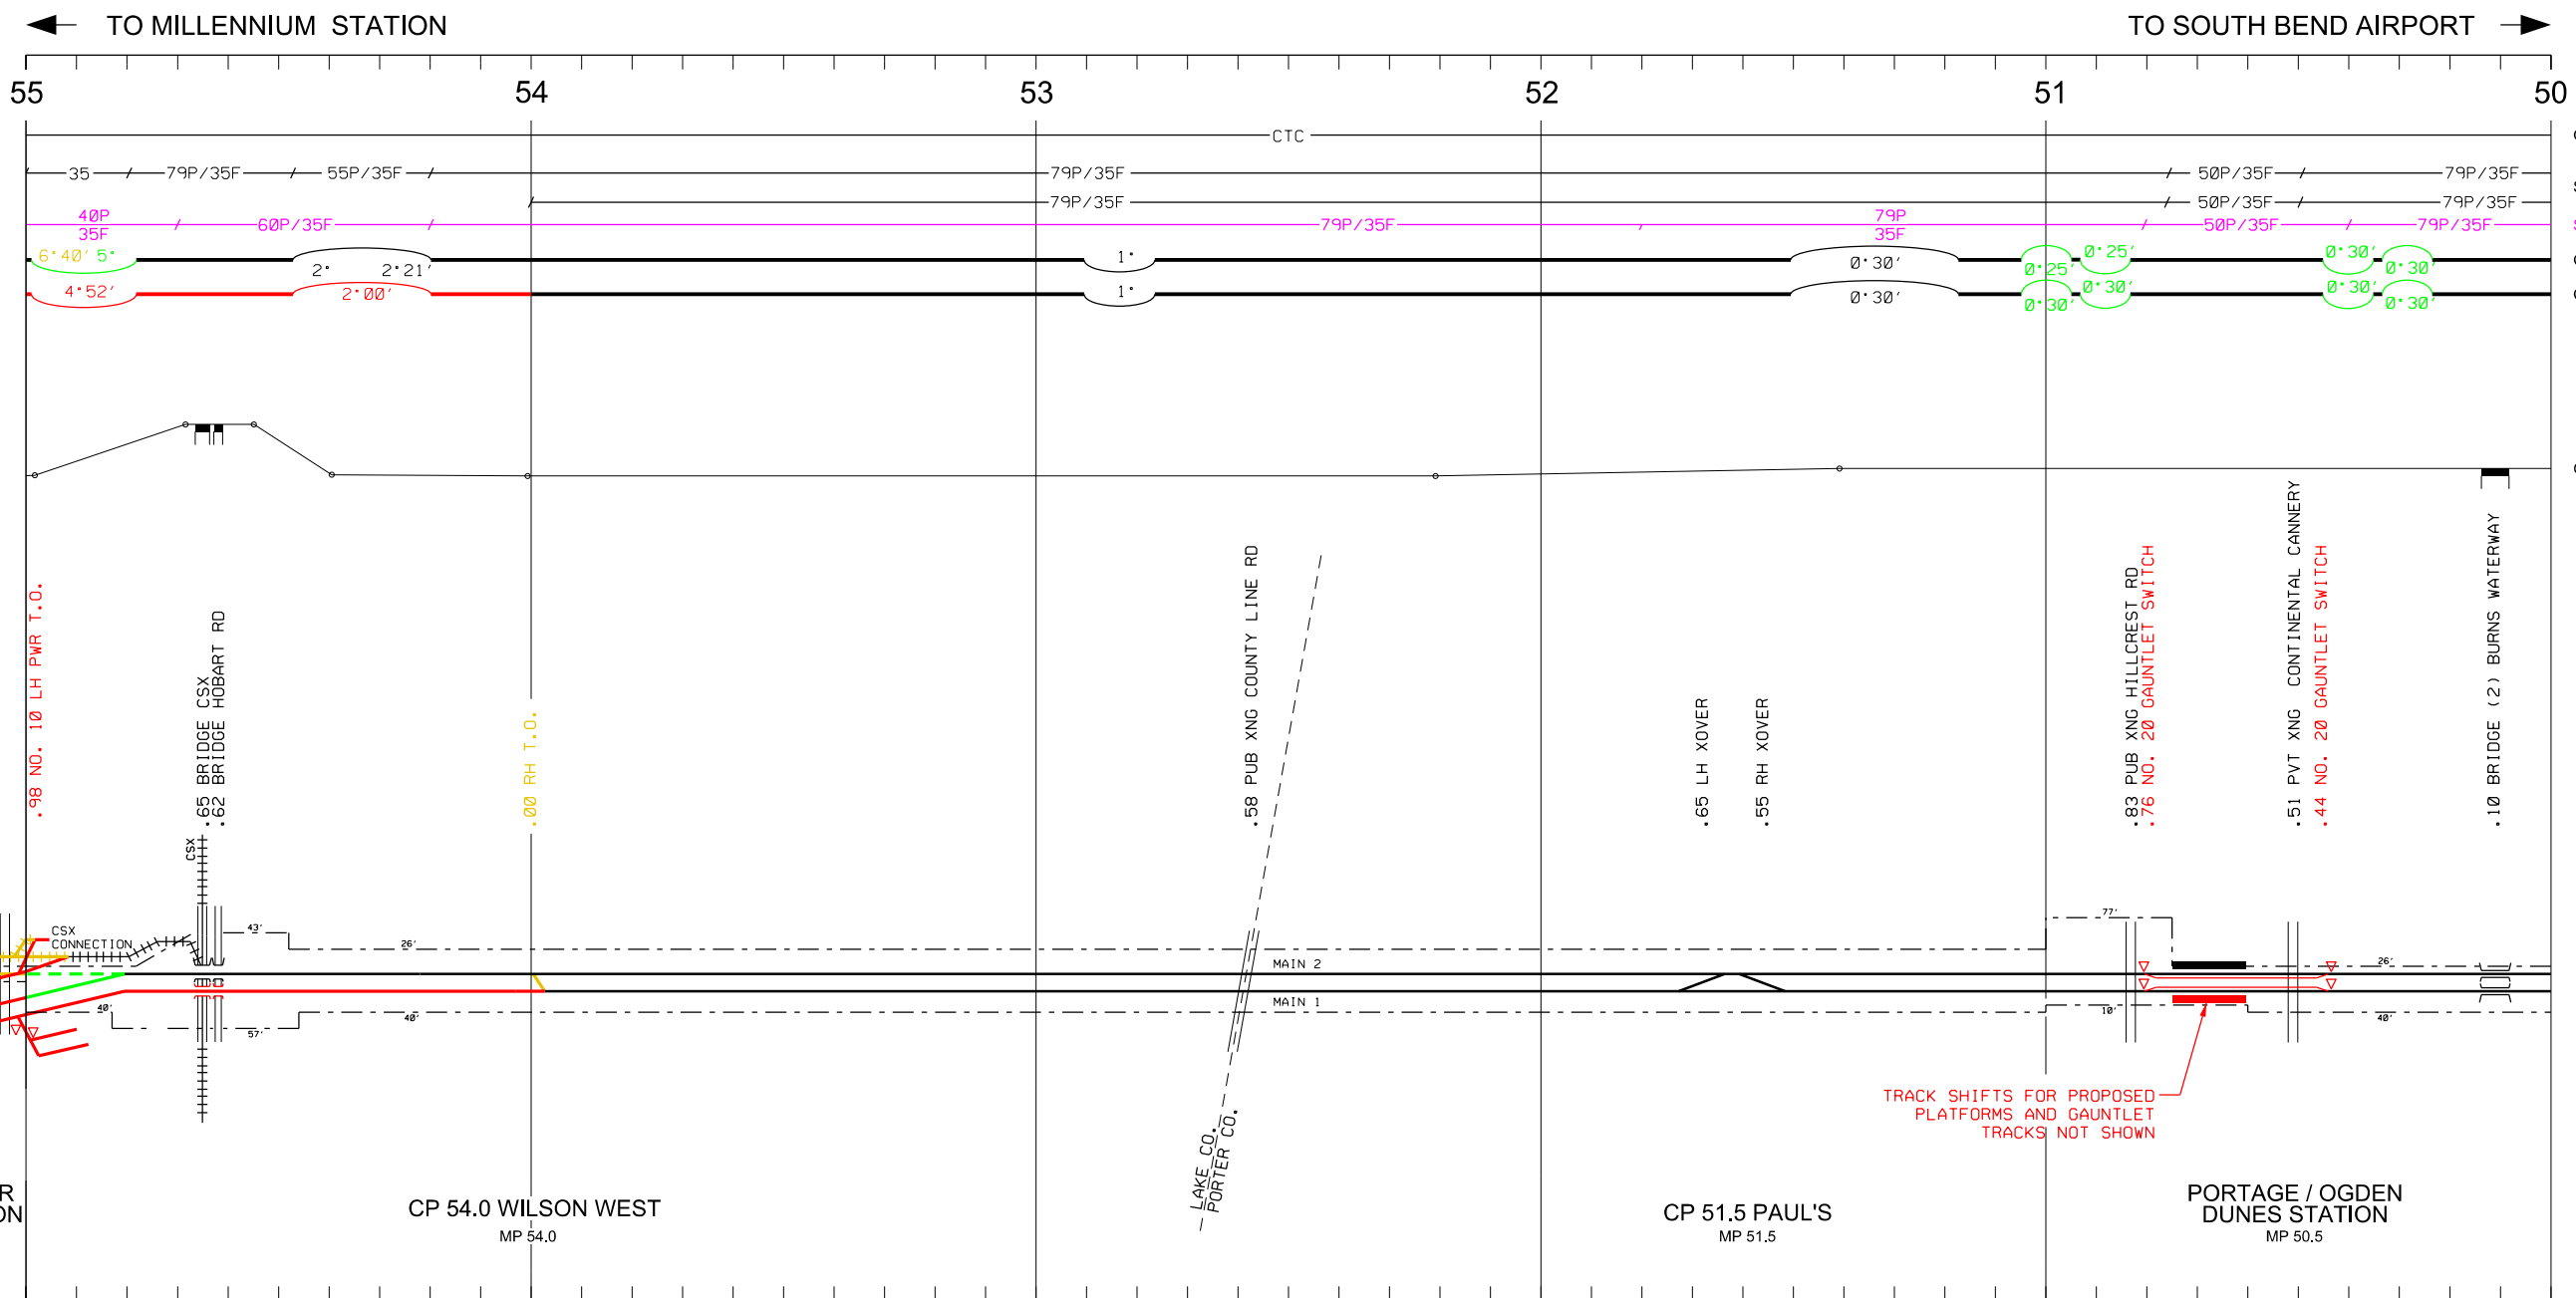

OPERATION
SPEED
SPEED MAIN 1&2
CURVATURE MAIN 1
CURVATURE MAIN 2
GRADE LINE



PRELIMINARY

NICTD DOUBLE TRACK NWI
PROPOSED TRACK SCHEMATIC
CONCEPTUAL LAYOUT

CARROLL AVENUE TO CP 58.8
MP 32.2 TO MP 58.8

LEGEND:
— EXISTING TRACK
++++ FOREIGN TRACK
— CONSTRUCT
— REMOVE
— RELOCATE FROM
— RELOCATE TO
— UPGRADE TRACK
--- RIGHT OF WAY
◆ CLEAR POINT
▽ CHANGE OWNERSHIP
▽ POWER TURNOUT



STATUS
PRELIMINARY


FILE: TRACK CHART

SHEET 2 OF 6

DATE: 05/12/2017

DRAWN M. QUALY

CHECKED Z. HARTJES

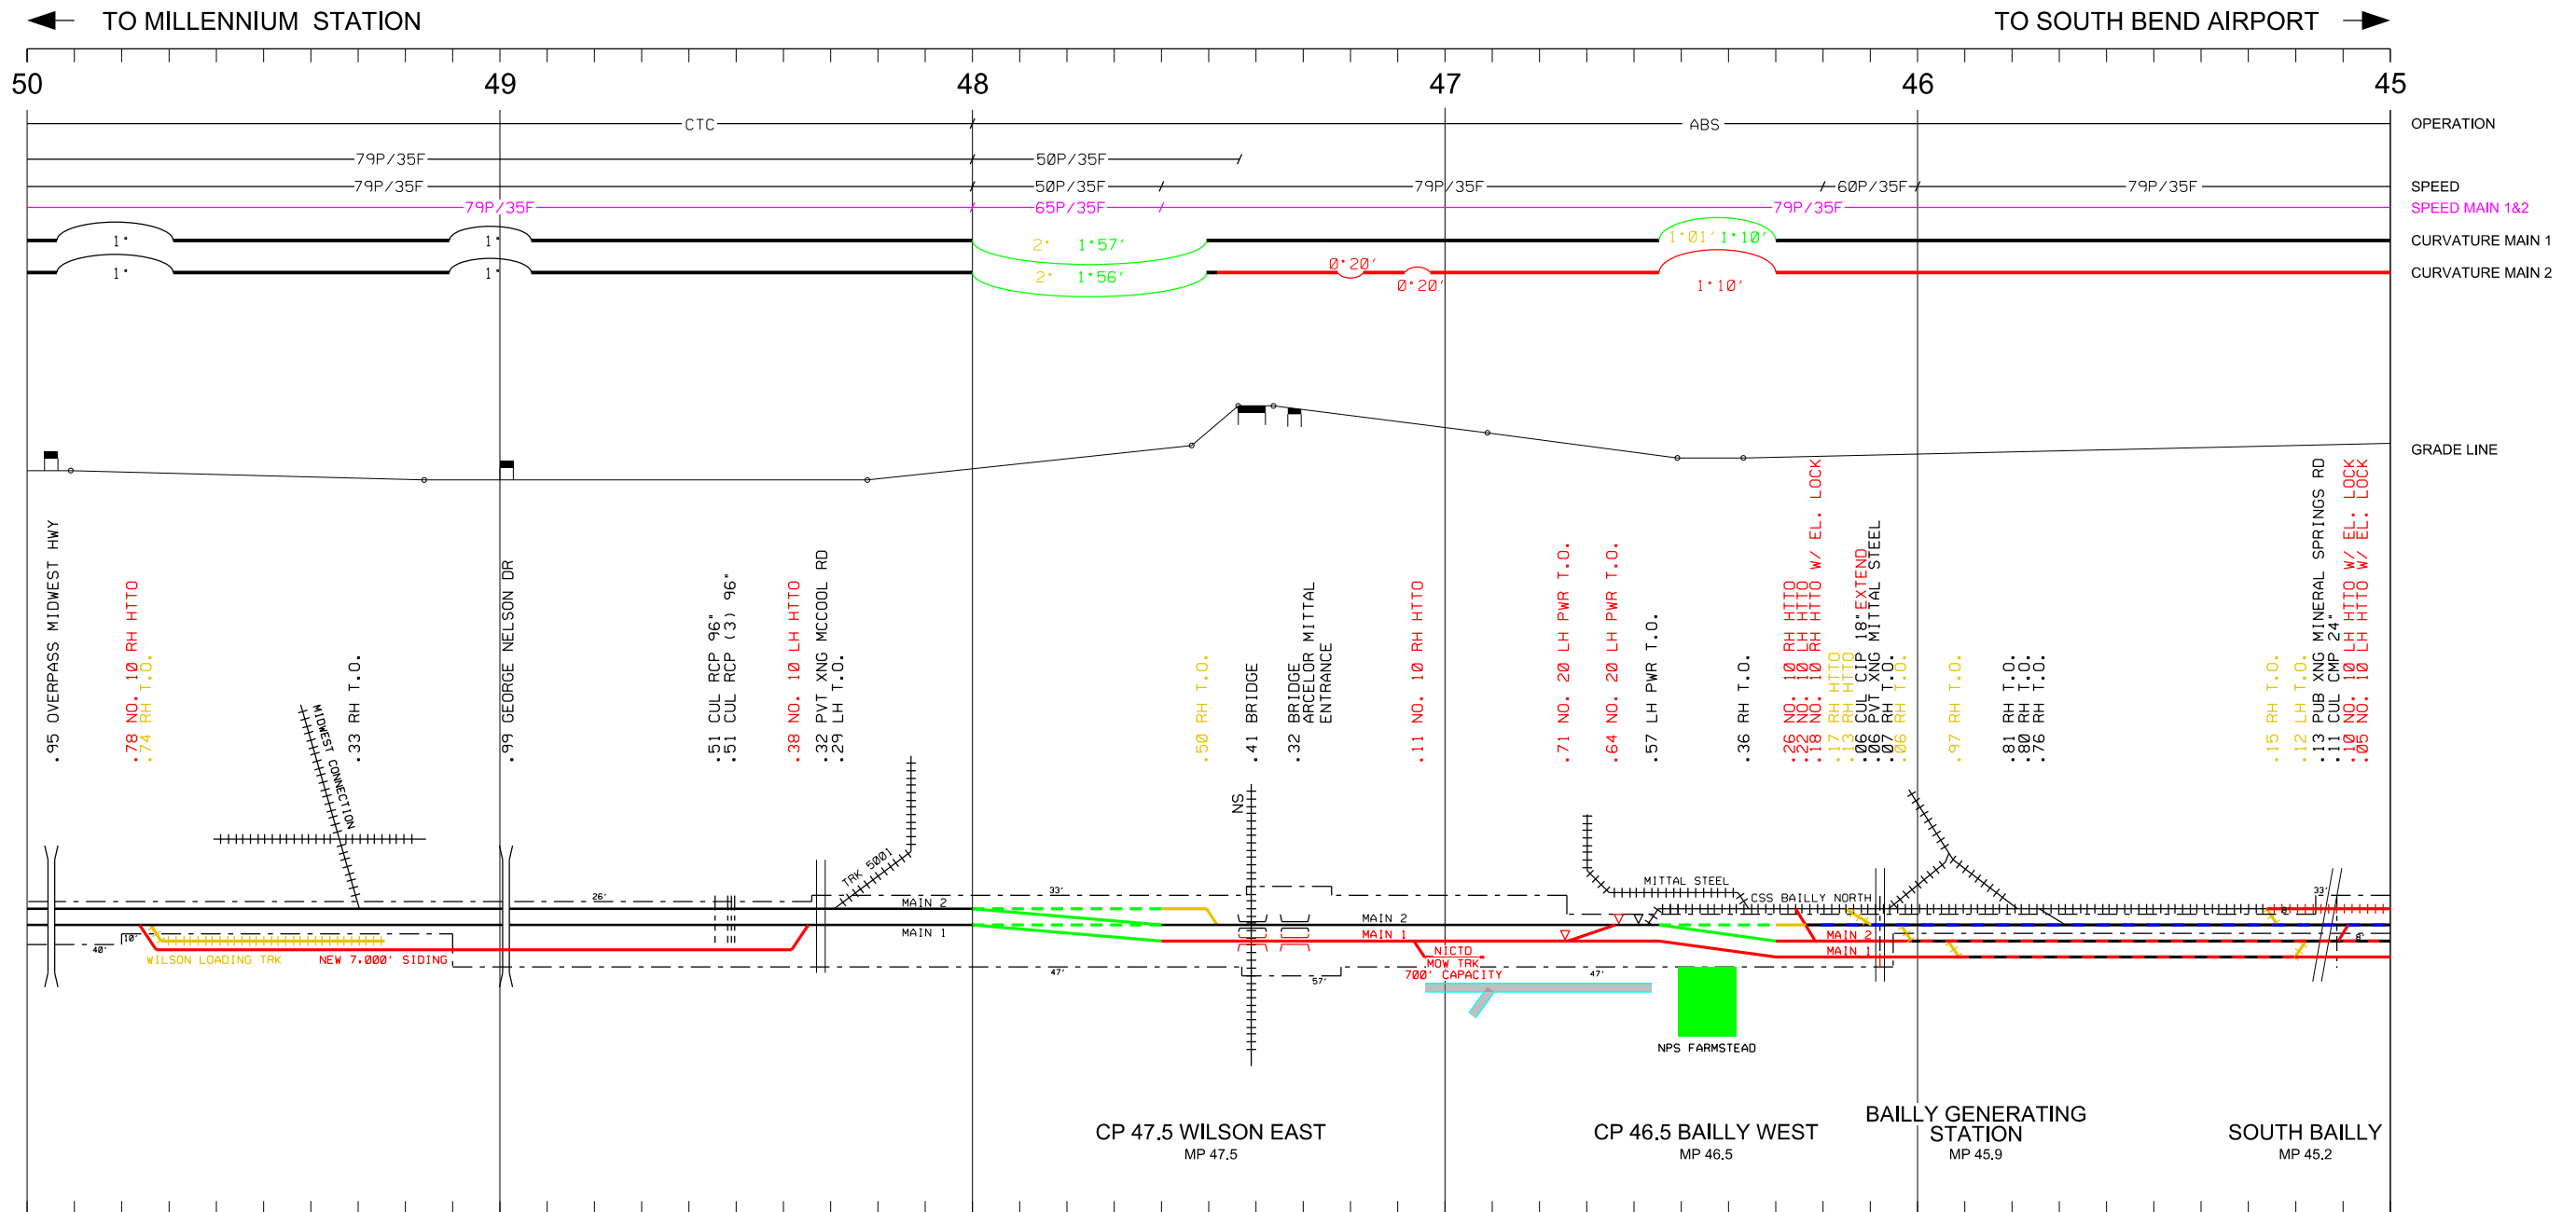

PRELIMINARY

NICTD DOUBLE TRACK NWI
PROPOSED TRACK SCHEMATIC
CONCEPTUAL LAYOUTCARROLL AVENUE TO CP 58.8
MP 32.2 TO MP 58.8

LEGEND:

— EXISTING TRACK
++++ FOREIGN TRACK

79P/35F

— REVISED SPEED
— CONSTRUCT
— REMOVE— ACCESS ROAD
--- RELOCATE FROM
--- RELOCATE TO— UPGRADE TRACK
--- RIGHT OF WAY◆ CLEAR POINT
▽ CHANGE OWNERSHIP
▽ POWER TURNOUTSTATUS
PRELIMINARY

NICTD

FILE: TRACK CHART

SHEET 3 OF 6

DATE: 05/12/2017

Track Chart Sheets 1-6.dgn

BY: ZHARTJES

TIME: 7:30:51 PM

6/17/2017



PRELIMINARY

NICTD DOUBLE TRACK NWI
PROPOSED TRACK SCHEMATIC
CONCEPTUAL LAYOUT

CARROLL AVENUE TO CP 58.8
MP 32.2 TO MP 58.8

LEGEND:		79P/35F	REVISD SPEED	ACCESS ROAD	RELOCATE FROM	UPGRADE TRACK	CLEAR POINT	CHANGE OWNERSHIP	POWER TURNOUT
—	EXISTING TRACK	—	—	—	—	—	◆	—	▽
+++++	FOREIGN TRACK	—	—	—	—	—	—	—	—
—	CONSTRUCT	—	—	—	—	—	—	—	—
—	REMOVE	—	—	—	—	—	—	—	—
—	RELOCATE TO	—	—	—	—	—	—	—	—
—	RIGHT OF WAY	—	—	—	—	—	—	—	—


DRAWN M. QUALY CHECKED Z. HARTJES

STATUS
PRELIMINARY

FILE: TRACK CHART

SHEET 4 OF 6

DATE: 05/12/2017

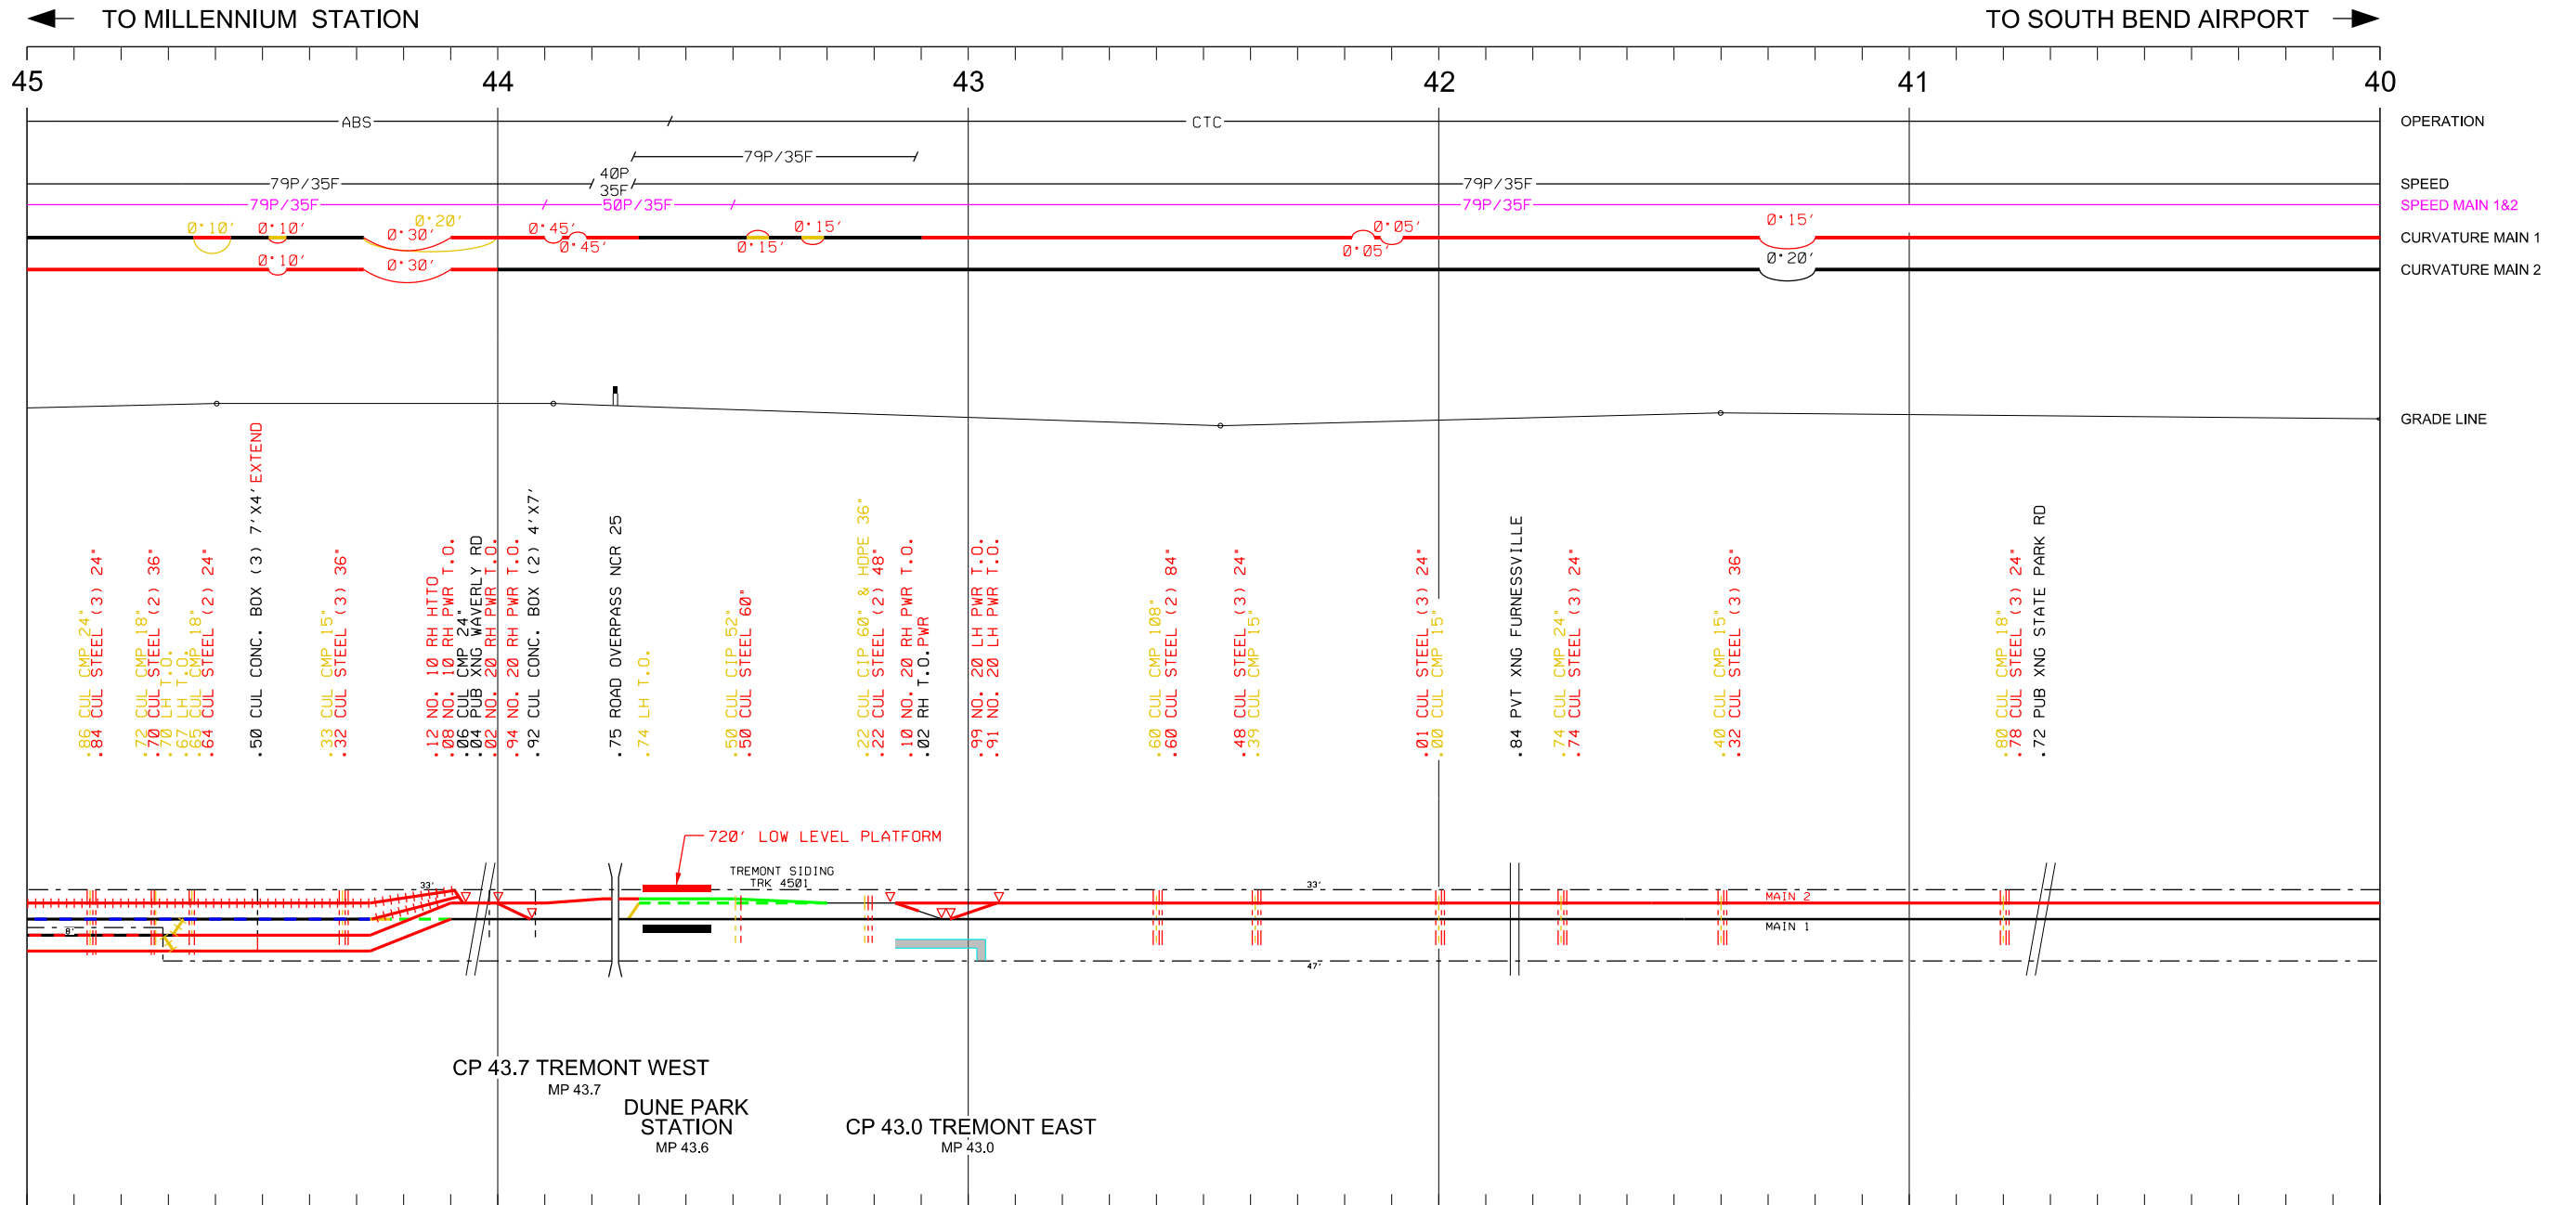

Track Chart Sheets 1-6.dgn

BY: ZHARTJES

TIME 7:30:34 PM

5/17/2017



LEGEND:		79P/35F	REVISD SPEED	ACCESS ROAD	RELOCATE FROM	UPGRADE TRACK	CLEAR POINT	CHANGE OWNERSHIP	POWER TURNOUT
—	EXISTING TRACK	—	CONSTRUCT	—	—	—	◆	—	▽
+++++	FOREIGN TRACK	—	REMOVE	—	—	—	—	—	—

DRAWN M. QUALY

CHECKED Z. HARTJES

STATUS
PRELIMINARY



PRELIMINARY


NICTD DOUBLE TRACK NWI
PROPOSED TRACK SCHEMATIC
CONCEPTUAL LAYOUT

CARROLL AVENUE TO CP 58.8
MP 32.2 TO MP 58.8

FILE: TRACK CHART

SHEET 5 OF 6

DATE: 05/12/2017

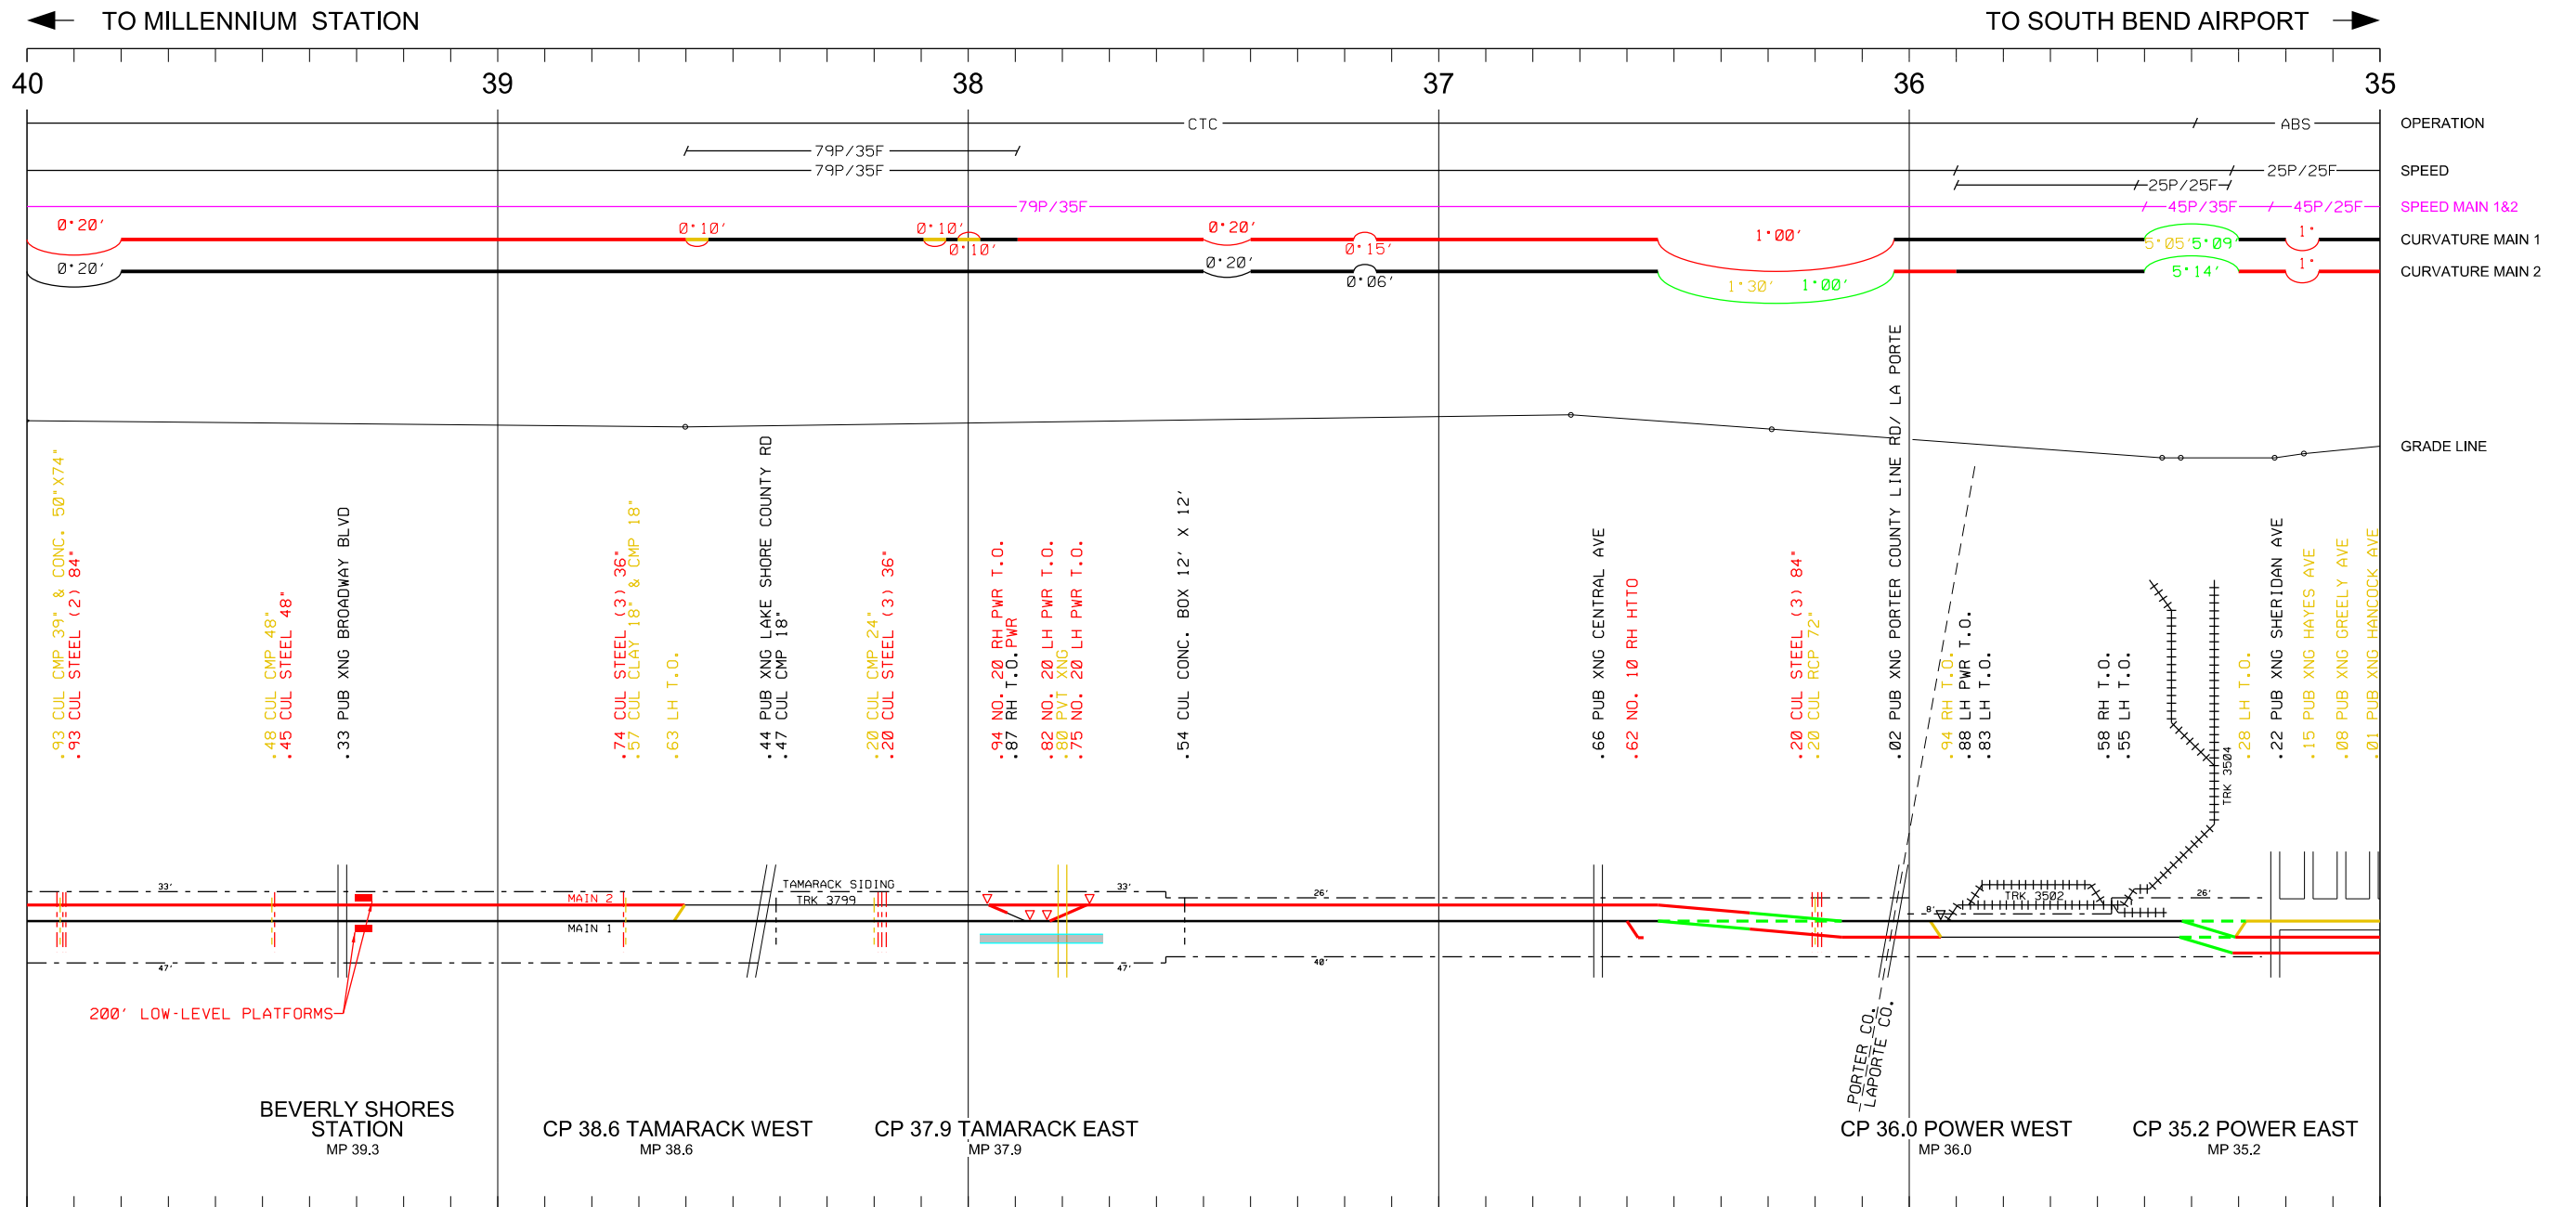

Track Chart Sheets 1-6.dgn

BY: ZHARTJES

TIME: 7:31:10 PM

5/17/2017



LEGEND:

— EXISTING TRACK
++++ FOREIGN TRACK

79P/35F
— CONSTRUCT
— REMOVE

— ACCESS ROAD
--- RELOCATE FROM
--- RELOCATE TO

— REMOVE AND RECONSTRUCT
--- RIGHT OF WAY

◆ CLEAR POINT
▽ CHANGE OWNERSHIP
POWER TURNOUT

STATUS
PRELIMINARY



PRELIMINARY


NICTD DOUBLE TRACK NWI
PROPOSED TRACK SCHEMATIC
CONCEPTUAL LAYOUT

CARROLL AVENUE TO CP 58.8
MP 32.2 TO MP 58.8

FILE: TRACK CHART

SHEET 6 OF 6

DATE: 05/12/2017

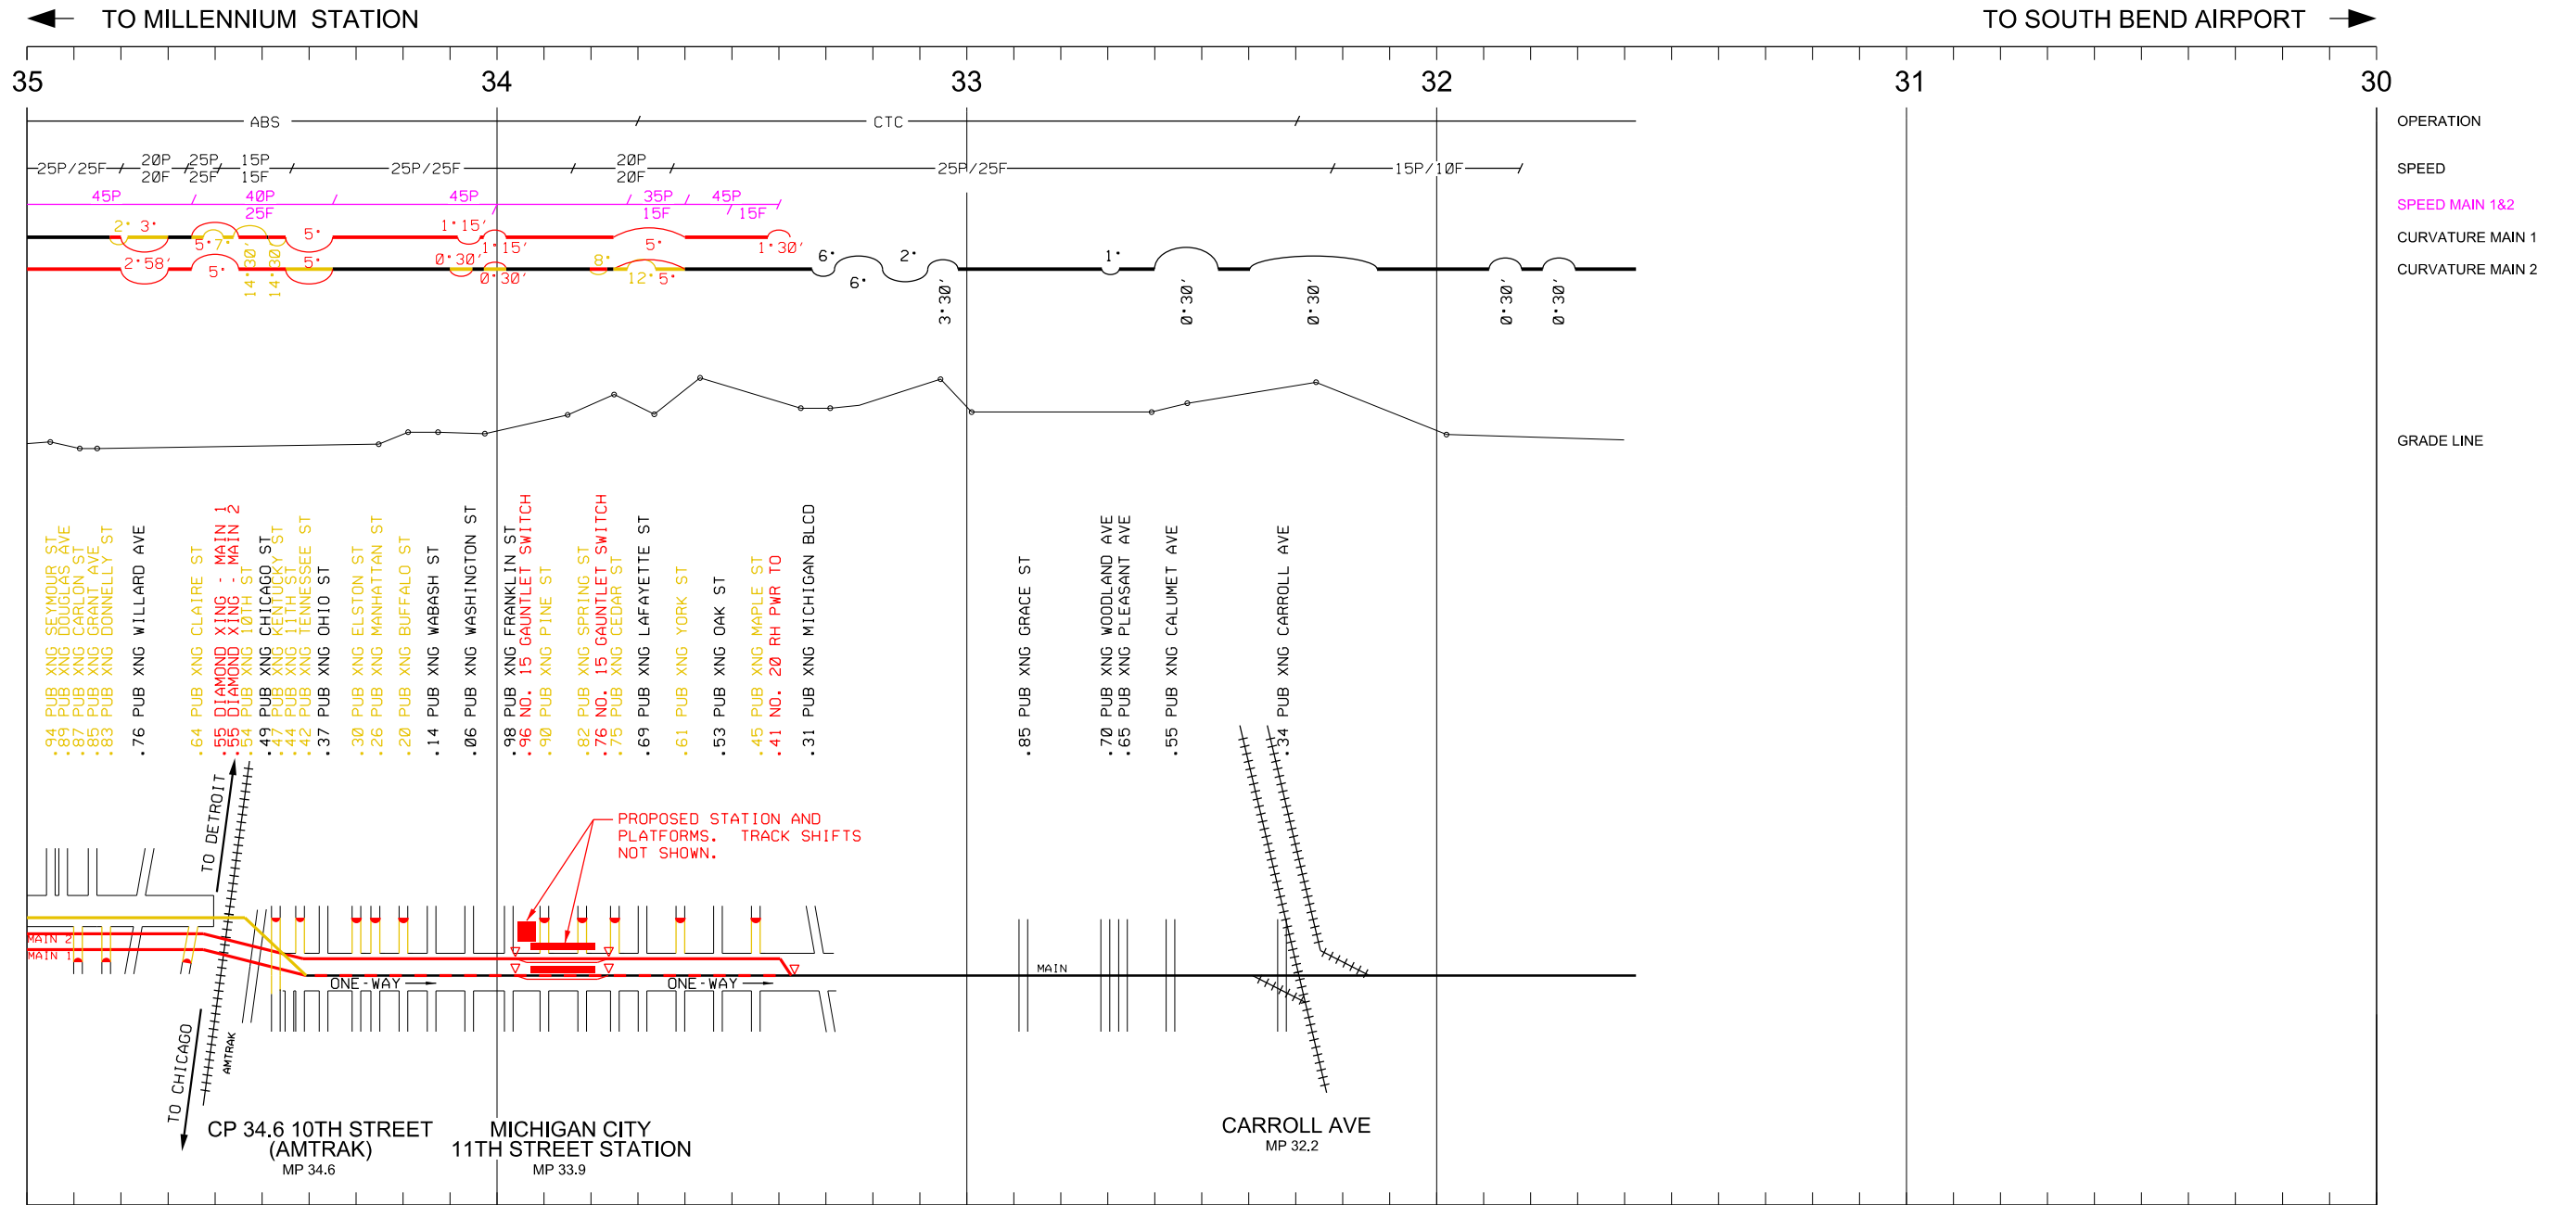


NORTHERN INDIANA COMMUTER TRANSPORTATION DISTRICT

DOUBLE TRACK NWI (NORTHWEST INDIANA)
MILEPOST 32.2 TO MILEPOST 58.8
MICHIGAN CITY TO GARY, INDIANA

TRACK DESIGN PLANS

SHEET INDEX

SHEET #	TITLE	DESCRIPTION
1	RGN-001	COVER SHEET
2	RGN-002	GENERAL NOTES, LEGEND & ABBREVIATIONS
3	RGN-003	PROJECT OVERVIEW
4-9	RTS-001 TO -006	TRACK DESIGN TYPICAL SECTIONS
10-104	RPP-001 TO -095	PLAN & PROFILE SHEETS
105-112	RPP-096 TO -103	MAIN 2 PROFILE STA 3014+00 TO 2636+00
113-129	RPP-104 TO -120	MAIN 1 PROFILE STA 2538+00 TO 1758+00
130	RPP-121	BOAT HOUSE LEAD PROFILE
131	RPP-122	GOFF SIDING PROFILE
132	RPP-123	CN CONNECTION PROFILES
133	RPP-124	GARY MOW TRACK PROFILE
134-135	RPP-125 TO -126	CSX CONNECTION TRACK PROFILE
136	RPP-127	MILLER SET OUT TRACKS PROFILES
137-139	RPP-128 TO -130	WILSON SIDING PROFILE
140	RPP-131	NICTD MOW PROFILE
141	RPP-132	BAILLY NORTH PROFILE
142	RPP-133	5406 & CSS TRK 1 PROFILE
143-145	RPP-134 TO -136	PROP BAILLY NORTH PROFILE
146	RPP-137	PROP CSS TRK 1 PROFILE
147	RPP-138	3502 PROFILE
148-193	RXS-001 TO -046	CROSS-SECTIONS

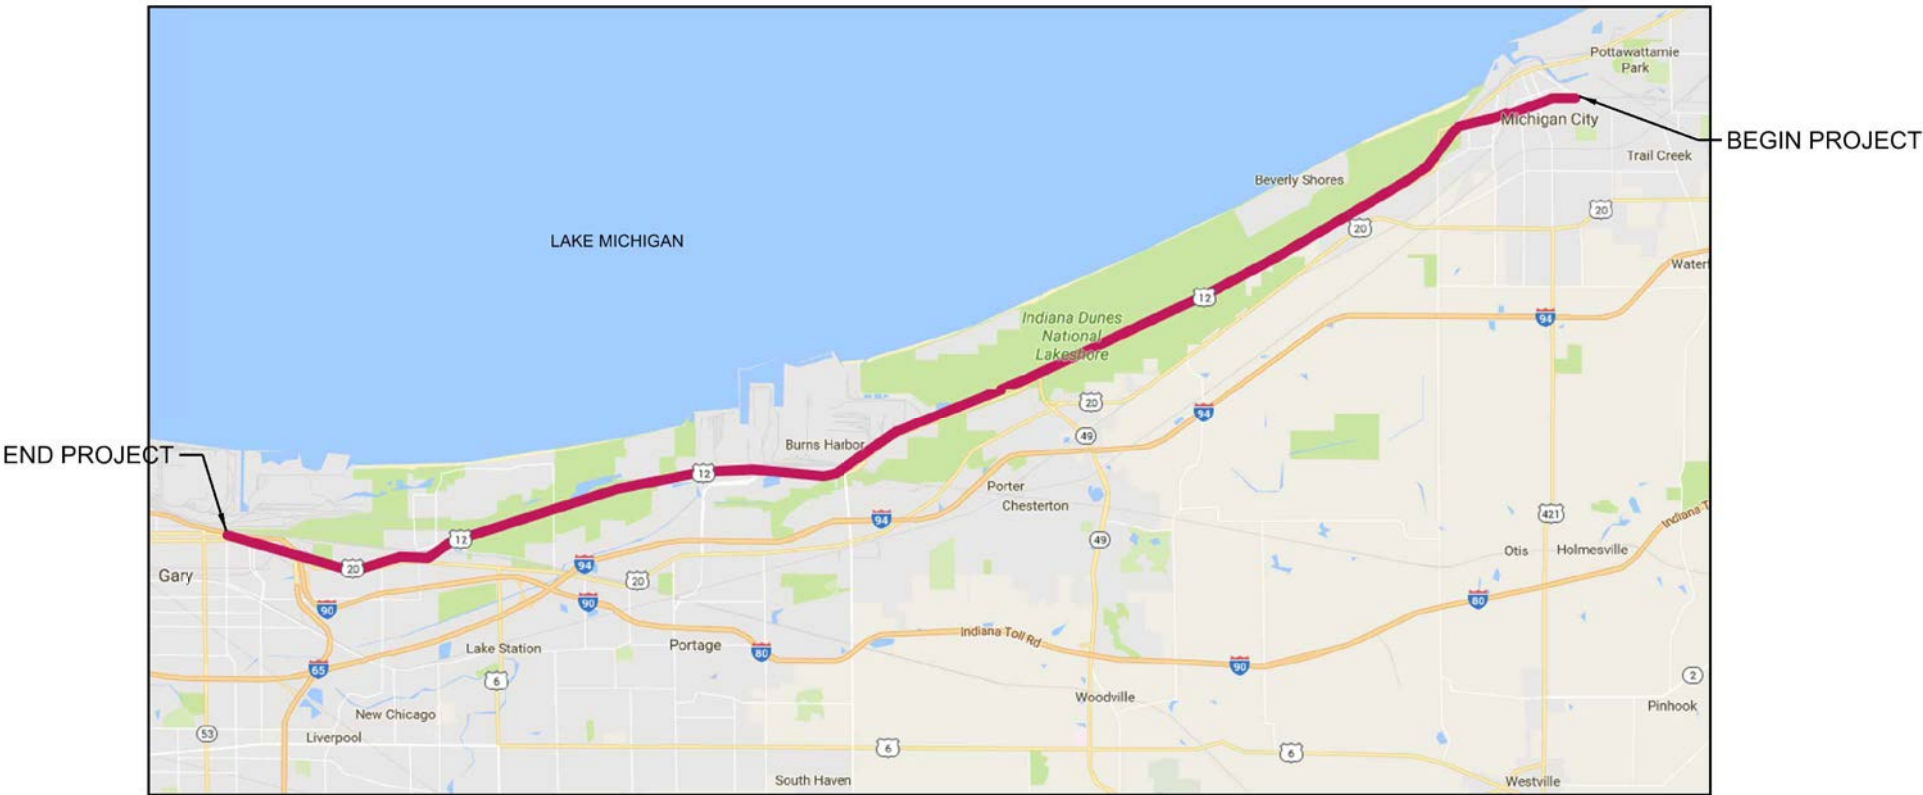

PLOT DATE: 5/16/2017 3:52:03 PM WJACKSON



HDR Engineering, Inc.
8550 W Bryn Mawr Ave., Suite 900
Chicago, IL 60631
www.hdrinc.com



NORTHERN INDIANA COMMUTER
TRANSPORTATION DISTRICT
33 East Highway 12
Chesterton, Indiana 46304



MICHIGAN CITY TO GARY, INDIANA

DESIGNED: HDR-MMQ
DRAWN: HDR-WJJ
CHECKED: HDR-ZDH
DATE: MAY 12, 2017

NOT FOR CONSTRUCTION SERIES RGN-001 OF RGN-003

NICTD - SOUTH SHORE LINE - MP 32.2 TO 58.8
DOUBLE TRACK-NWI

COVER SHEET

FILENAME
SCALE

Cover Sheet
AS NOTED

SHEET

001 OF 193

PLOT DATE: 5/16/2017 3:52:06 PM WJACKSON

GENERAL NOTES

1. THE EXISTENCE, LOCATION, AND ELEVATION OF UTILITIES AND/OR CONCEALED STRUCTURES AT THE PROJECT SITE ARE NOT GUARANTEED. THE CONTRACTOR IS RESPONSIBLE FOR DETERMINING THE EXISTENCE, LOCATION, AND ELEVATION OF ALL SUCH UTILITIES AND/OR STRUCTURES AND IS RESPONSIBLE FOR NOTIFYING THE APPROPRIATE COMPANY, DEPARTMENT, OR PERSON(S) OF ITS INTENTION TO CARRY OUT ITS OPERATIONS.



0	05/12/2017	FINAL PRELIMINARY DESIGN
ISSUE	DATE	DESCRIPTION



DESIGNED:	HDR-MMQ
DRAWN:	MDR-WJJ
CHECKED:	HDR-ZDH
DATE:	MAY 12, 2017

NOT FOR CONSTRUCTION		SERIES RGN-002 OF RGN-003
NICTD - SOUTH SHORE LINE - MP 32.2 TO 58.8 DOUBLE TRACK-NWI		
GENERAL NOTES, LEGEND, & ABBREVIATIONS		
FILENAME	General Notes	SHEET
SCALE	AS NOTED	002 OF 193

LEGEND


ABBREVIATIONS

	EXISTING TRACK TO REMAIN AS IS		EXISTING OVERHEAD ELECTRIC
	EXISTING TRACK TO BE REMOVED		PROPOSED OVERHEAD ELECTRIC
	EXISTING TRACK TO BE SHIFTED		TREE/SHRUB/VEGETATION
	EXISTING TRACK TO BE SURFACED		EDGE OF GRAVEL
	PROPOSED TRACK		EXISTING RIGHT OF WAY
	PROPOSED POWER OPERATED TURNOUT		PROPOSED RIGHT OF WAY
	PROPOSED HAND-THROW TURNOUT		PARCELS
	PROPOSED ELECTRIC LOCK TURNOUT		PROPOSED CONSTRUCTION EASEMENT
	PROPOSED DOUBLE SWITCH POINT DERAIL		ACCESS ROAD/TURNOUT PAD
	PROPOSED SLIDING DERAIL		HIGH QUALITY WETLAND
	PROPOSED CULVERT EXTENSION		NON HIGH QUALITY WETLAND/UNDETERMINED
	CONSTRUCTION LIMITS		STREAM OR DITCH
	COMMUNICATION LINE		RIP RAP
	EXISTING OVERHEAD POWER LINE		ELECTRIC POLE
	EXISTING FENCE		COMMUNICATION POLE
	EXISTING SANITARY SEWER		EXISTING CROSSING SIGNAL
	PROPOSED SANITARY SEWER		PROPOSED CROSSING SIGNAL
	OVERHEAD FIBER		GUARDRAIL
	EXISTING FIBER OPTIC		SIGNS (NON-RAILROAD)
	EXISTING UNDERGROUND FIBER OPTIC		GAS WARNING SIGN
	PROPOSED UNDERGROUND FIBER OPTIC		RAILROAD SIGN
	EXISTING OVERHEAD FIBER OPTIC		FIBER OPTIC MARKER
	PROPOSED OVERHEAD FIBER OPTIC		WHISTLE POST SIGN
	EXISTING GAS LINE		LIGHT POLE
	PROPOSED GAS LINE		FIRE HYDRANT
	PETRO GAS LINE		RAIL SIGNAL (DWARF SIGNAL)
	PROPOSED PETRO GAS LINE		TRAFFIC SIGNAL
	EXISTING WATER LINE		
	PROPOSED WATER LINE		
	EXISTING UNDERGROUND ELECTRIC		
	PROPOSED UNDERGROUND ELECTRIC		

	FIBER OPTIC HAND HOLE
	ELECTRIC METER
	ELECTRIC PEDESTAL
	COMMUNICATION PEDESTAL
	CONTROL POINT
	GRADE CROSSING PAVEMENT MARKING
	PEDESTRIAN CROSSING GATE
	EXISTING CROSSBUCK

APPROX	APPROXIMATE
BLDG	BUILDING
BM	BENCH MARK
CB	CATCH BASIN
CL	CENTERLINE
CMP	CORRUGATED METAL PIPE
CN	CANADIAN NATIONAL
CONC	CONCRETE
CS	CURVE TO SPIRAL
CSS	CHICAGO SOUTH SHORE
CSXT	CSX TRANSPORTATION
CWR	CONTINUOUSLY WELDED RAIL
CY	CUBIC YARD
Dc	DEGREE OF CURVE
DI	DUCTILE IRON
DIAM.	DIAMETER
DOT	DEPARTMENT OF TRANSPORTATION
DSPD	DUAL SWITCH POINT DERAILS
DWG	DRAWING
E	EASTING
EA	EACH
E.L.	ELECTRIC LOCK
ELEC	ELECTRICAL
ELEV, EL	ELEVATION
ENGR	ENGINEER
EXIST, EX	EXISTING
FOTS	FIBER OPTIC TRANSMISSION SYSTEM
FT	FOOT, FEET
G	GAS
GND	GROUND
HDPE	HIGH DENSITY POLYETHYLENE
HORZ	HORIZONTAL
HTTO	HAND THROW TURNOUT
HMA	HOT MIX ASPHALT
INV	INVERT
LB	POUND
Lc	LENGTH OF CURVE
LH	LEFT HAND
Ls	LENGTH OF SPIRAL
LIN FT, LF	LINEAR FOOT
LLT	LAST LONG TIE
LN	LANE
LT	LEFT
MAX	MAXIMUM
MH	MANHOLE
MIN	MINIMUM
MISC	MISCELLANEOUS
MOW	MAINTENANCE OF WAY
MP	MILE POST
N	NORTHING
NIC	NOT IN CONTRACT

NICTD	NORTHERN INDIANA COMMUTER TRANSPORTATION DISTRICT
NIPSCO	NORTHERN INDIANA PUBLIC SERVICE COMPANY
N.T.S.	NOT TO SCALE
NO., #	NUMBER
NS	NORFOLK SOUTHERN
OHP	OVERHEAD POWER
OVH	OVERHEAD
PC	POINT OF CURVE
PI	POINT OF INTERSECTION
PITO	POINT OF INTERSECTION OF TURNOUT
POB	POINT OF BEGINNING
POE	POINT OF ENDING
POTO	POWER OPERATED TURNOUT
PR, PROP	PROPOSED
P.S.	POINT OF SWITCH
PT	POINT OF TANGENCY, POINT
PVC	POINT OF VERTICAL CURVE
PVI	POINT OF VERTICAL INTERSECTION
PVT	POINT OF VERTICAL TANGENCY
R	RADIUS
RE	RAILWAY ENGINEERED, AREMA APPROVED RAIL SECTION
REV	REVISION
RH	RIGHT HAND
RR	RAILROAD
RT	RIGHT, ROUTE
R/W, ROW	RIGHT-OF-WAY
S	SOUTH
SC	SPIRAL TO CURVE
SD	STORM DRAIN, SLIDING DERAIL
SDWC	SLIDING DERAIL WITH CROWDER
SDG	SIDING
SDWLK	SIDEWALK
SF	SQUARE FOOT
SS	SANITARY SEWER
STA	STATION
ST	STREET, SPIRAL TO TANGENT
STD	STANDARD
STM, SD	STORM SEWER, STORM DRAIN
SW	SWITCH
TEMP	TEMPORARY
TF	TRACK FOOT, TRACK FEET
T.O.	TURNOUT
TOR	TOP OF RAIL
TRK	TRACK
TS	TANGENT TO SPIRAL
TYP, TYP.	TYPICAL
UG	UNDERGROUND
V	VELOCITY
VC	VERTICAL CURVE
W	WATER, WEST
XOVER	CROSSOVER
XING	CROSSING
YD	YARD

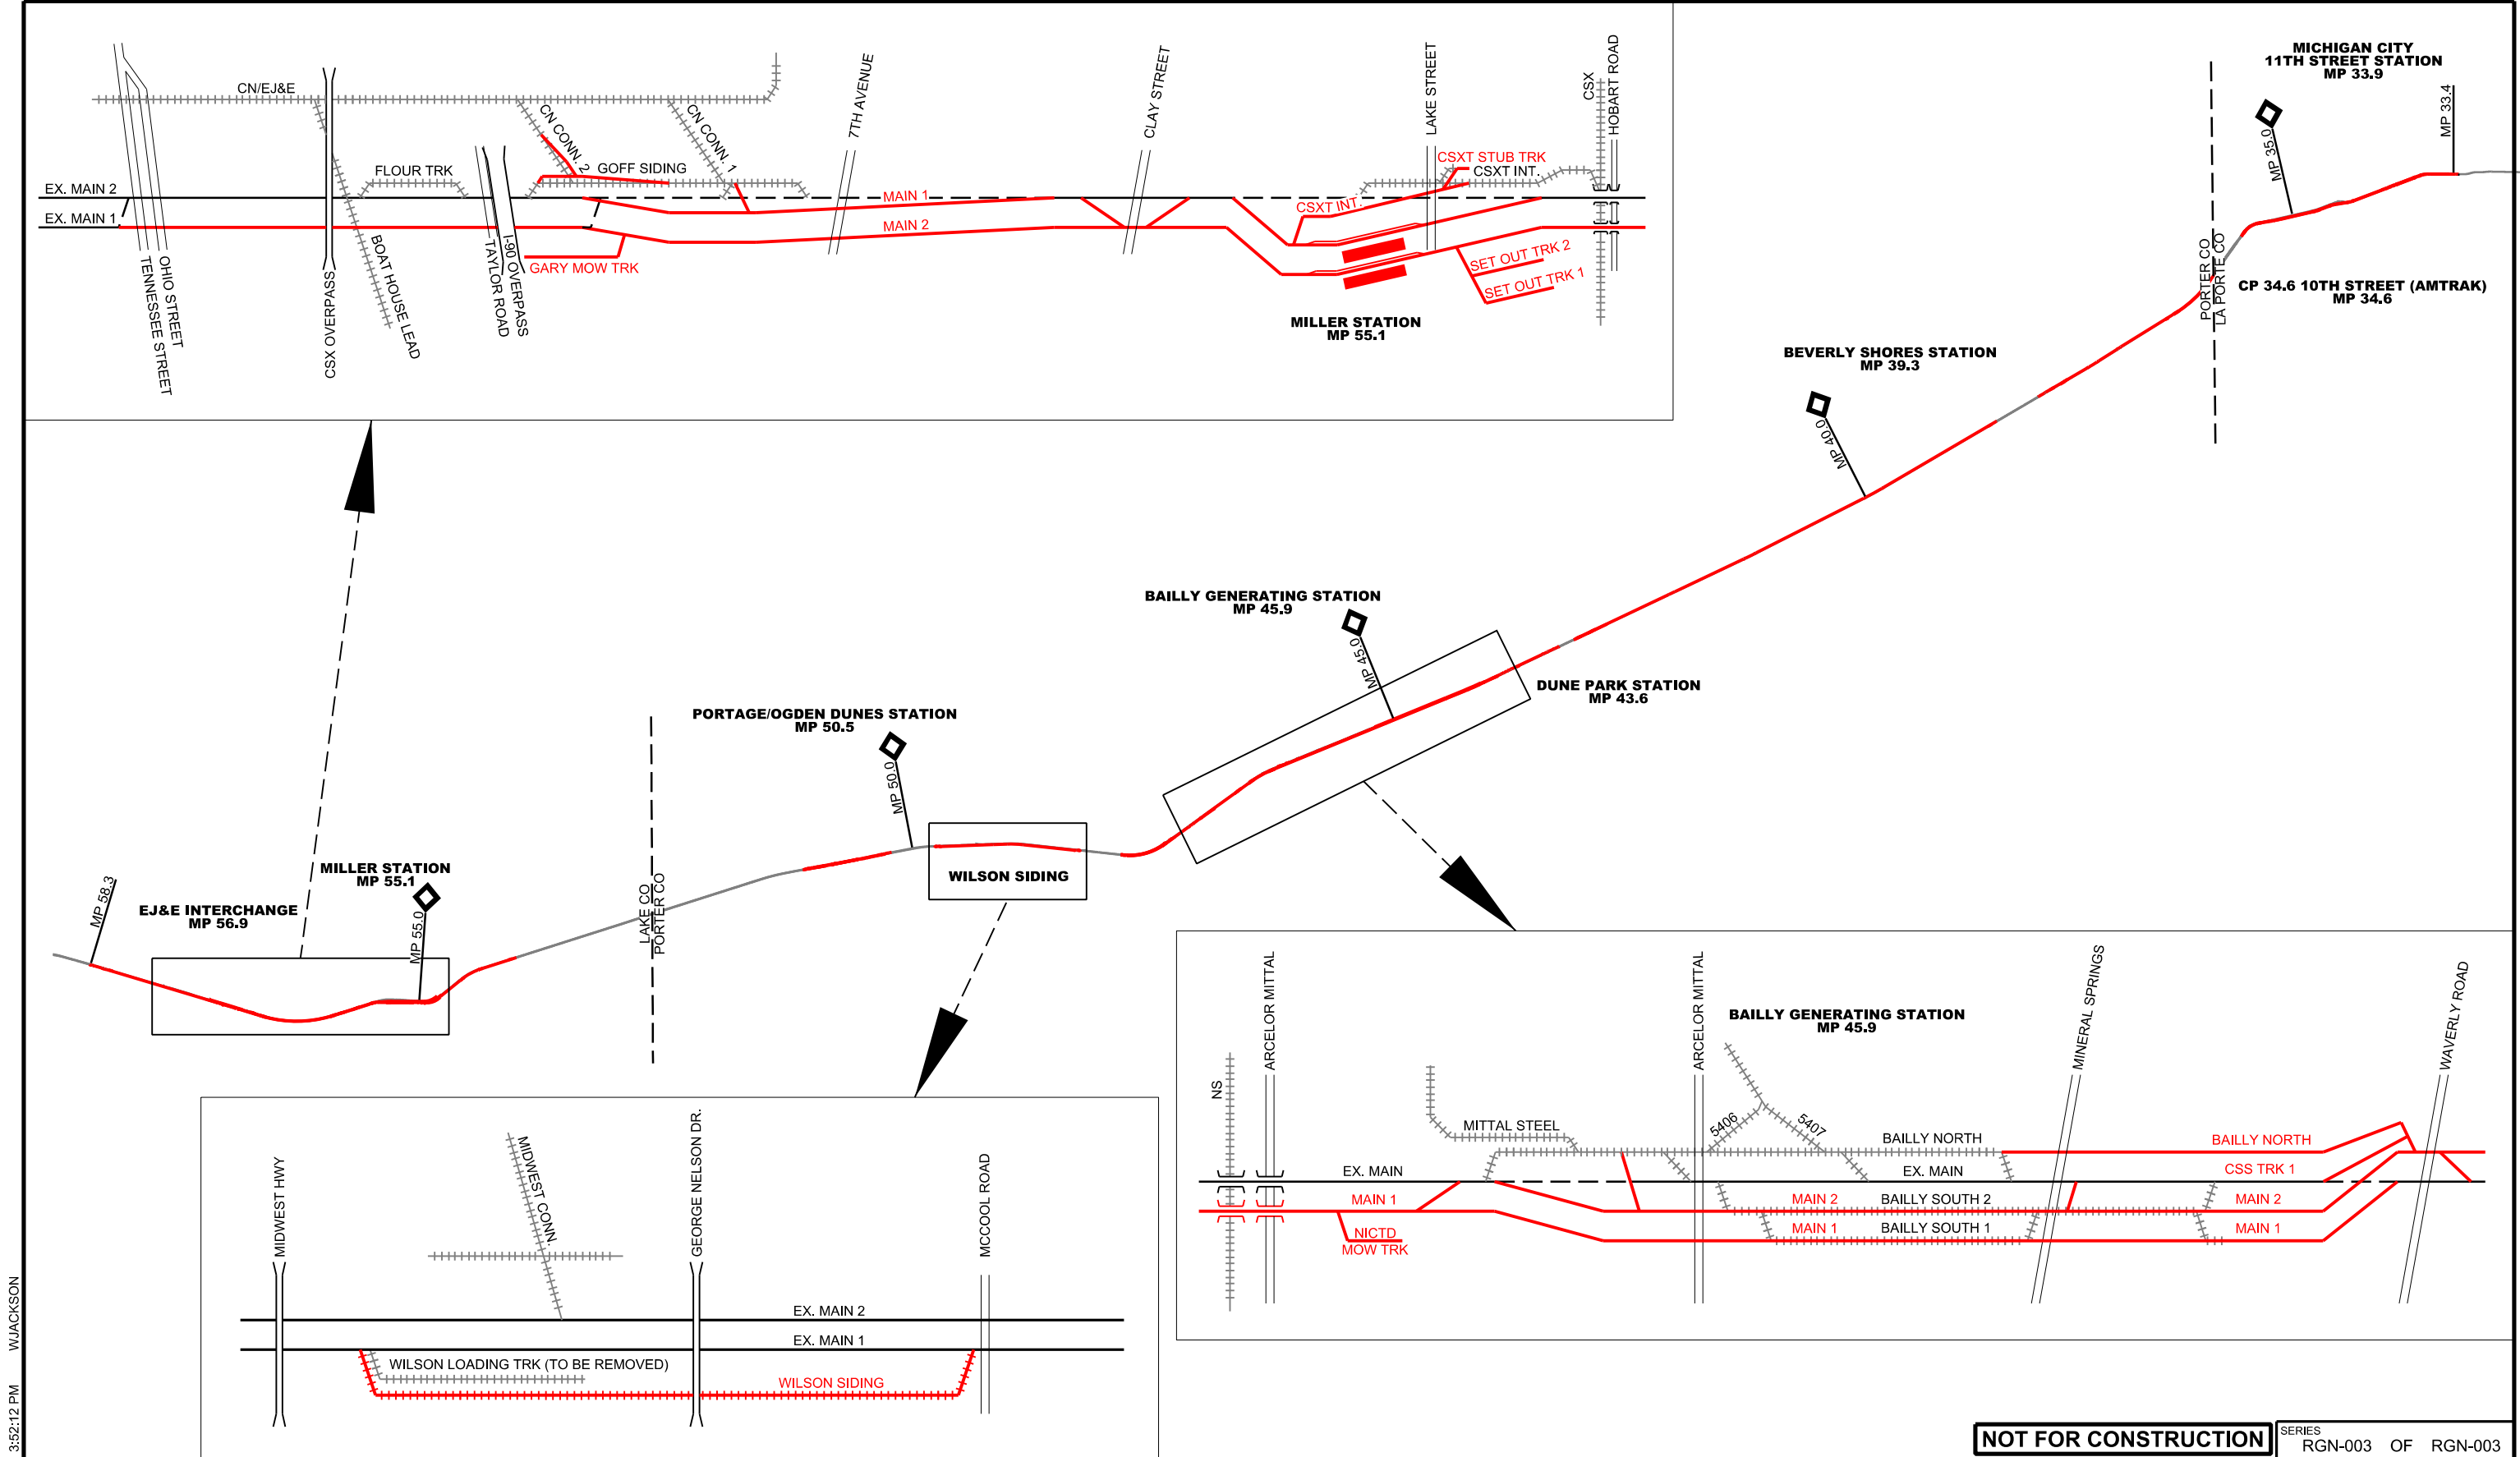

PLOT DATE: 5/16/2017 3:52:12 PM WJACKSON



HDR Engineering, Inc.
8550 W Bryn Mawr Ave., Suite 900
Chicago, IL 60631
www.hdrinc.com



PATRICK
ENGINEERING

0	05/12/2017	FINAL PRELIMINARY DESIGN
ISSUE	DATE	DESCRIPTION



NORTHERN INDIANA COMMUTER
TRANSPORTATION DISTRICT
33 East Highway 12
Chesterton, Indiana 46304



MICHIGAN CITY TO GARY, INDIANA

DESIGNED:	HDR-WJJ
DRAWN:	MDR-WJJ
CHECKED:	HDR-ZDH
DATE:	MAY 12, 2017

NOT FOR CONSTRUCTION

SERIES
RGN-003 OF RGN-003

NICTD - SOUTH SHORE LINE - MP 32.2 TO 58.8
DOUBLE TRACK-NWI

PROJECT OVERVIEW

FILENAME	Project Overview
SCALE	AS NOTED

SHEET
003 OF 193