


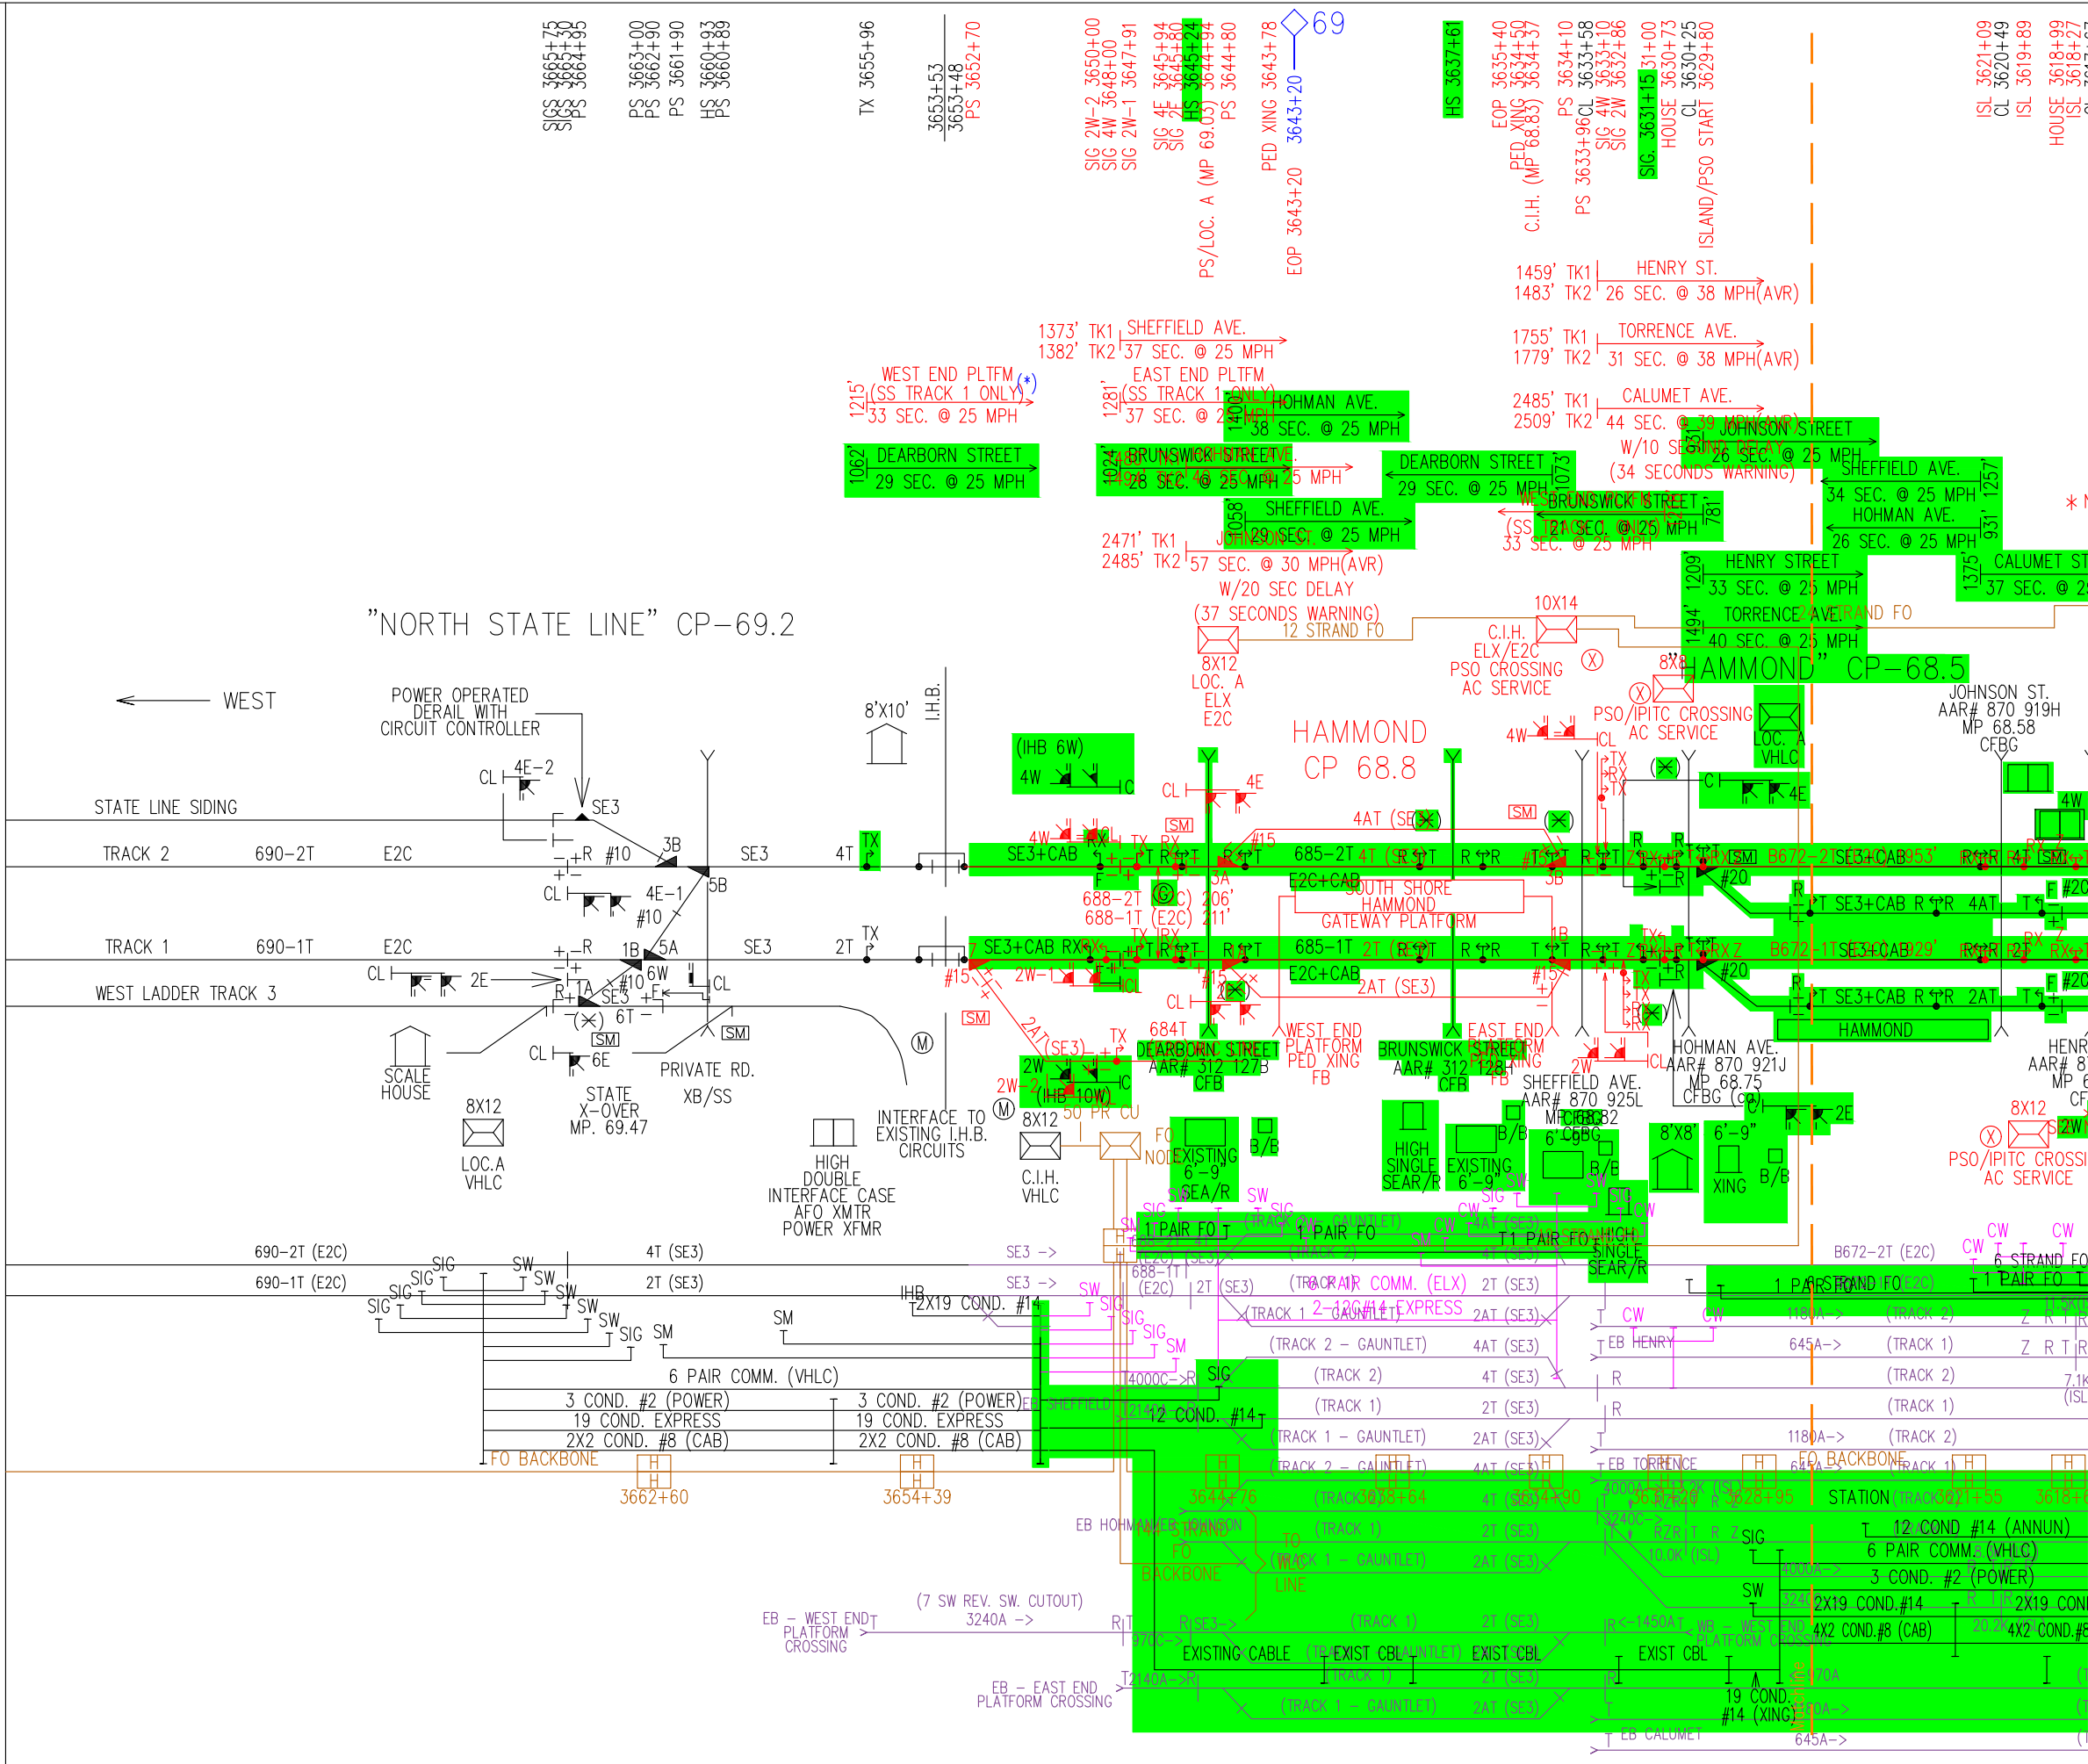

REVISIONS

- (*) = EXISTING CASE/HOUSE LOCATION
- (X) = PROPOSED CASE/HOUSE LOCATION
- (LEVEL 1) TITLE BLOCK AND BORDER
- (LEVEL 2) BLACK = EXISTING
- BLUE = NOTE
- (LEVEL 3) RED = IN
- (LEVEL 4) GREEN = OUT
- (LEVEL 5) (X) = NEW AC SERVICE
- (LEVEL 5) (M) = EXISTING AC SERVICE
- (LEVEL 6) BLACK = EXISTING X-ING
- (LEVEL 7) BROWN = FO - COMM. LINES
- (LEVEL 8) MAGENTA = OPERATION CABLES
- (LEVEL 15) = CROSSING START FREQUENCIES (LEVEL MUST BE ACTIVATED, WITH LEVEL 7 & 8 DEACTIVATED).
- (LEVEL 16) ORANGE = FREQUENCY OUT
- (LEVEL 17) PURPLE = FREQUENCY IN

HORIZONTAL SCALE :
1 INCH = 500 FEET




NORTHERN INDIANA COMMUTER TRANSPORTATION DISTRICT

WEST LAKE
CORRIDOR PROJECT
M.P. 67 TO M.P. 69

DESIGNER SKETCH WITH CROSSING FREQUENCY STUDY

DESIGNED DAI/JNV	DIGITIZED DAI/JNV
NEXT FILE	NEXT SH
CHECKED DAI/BDO	DATE 12-01-23
FILE SKETCH	SHEET 001A



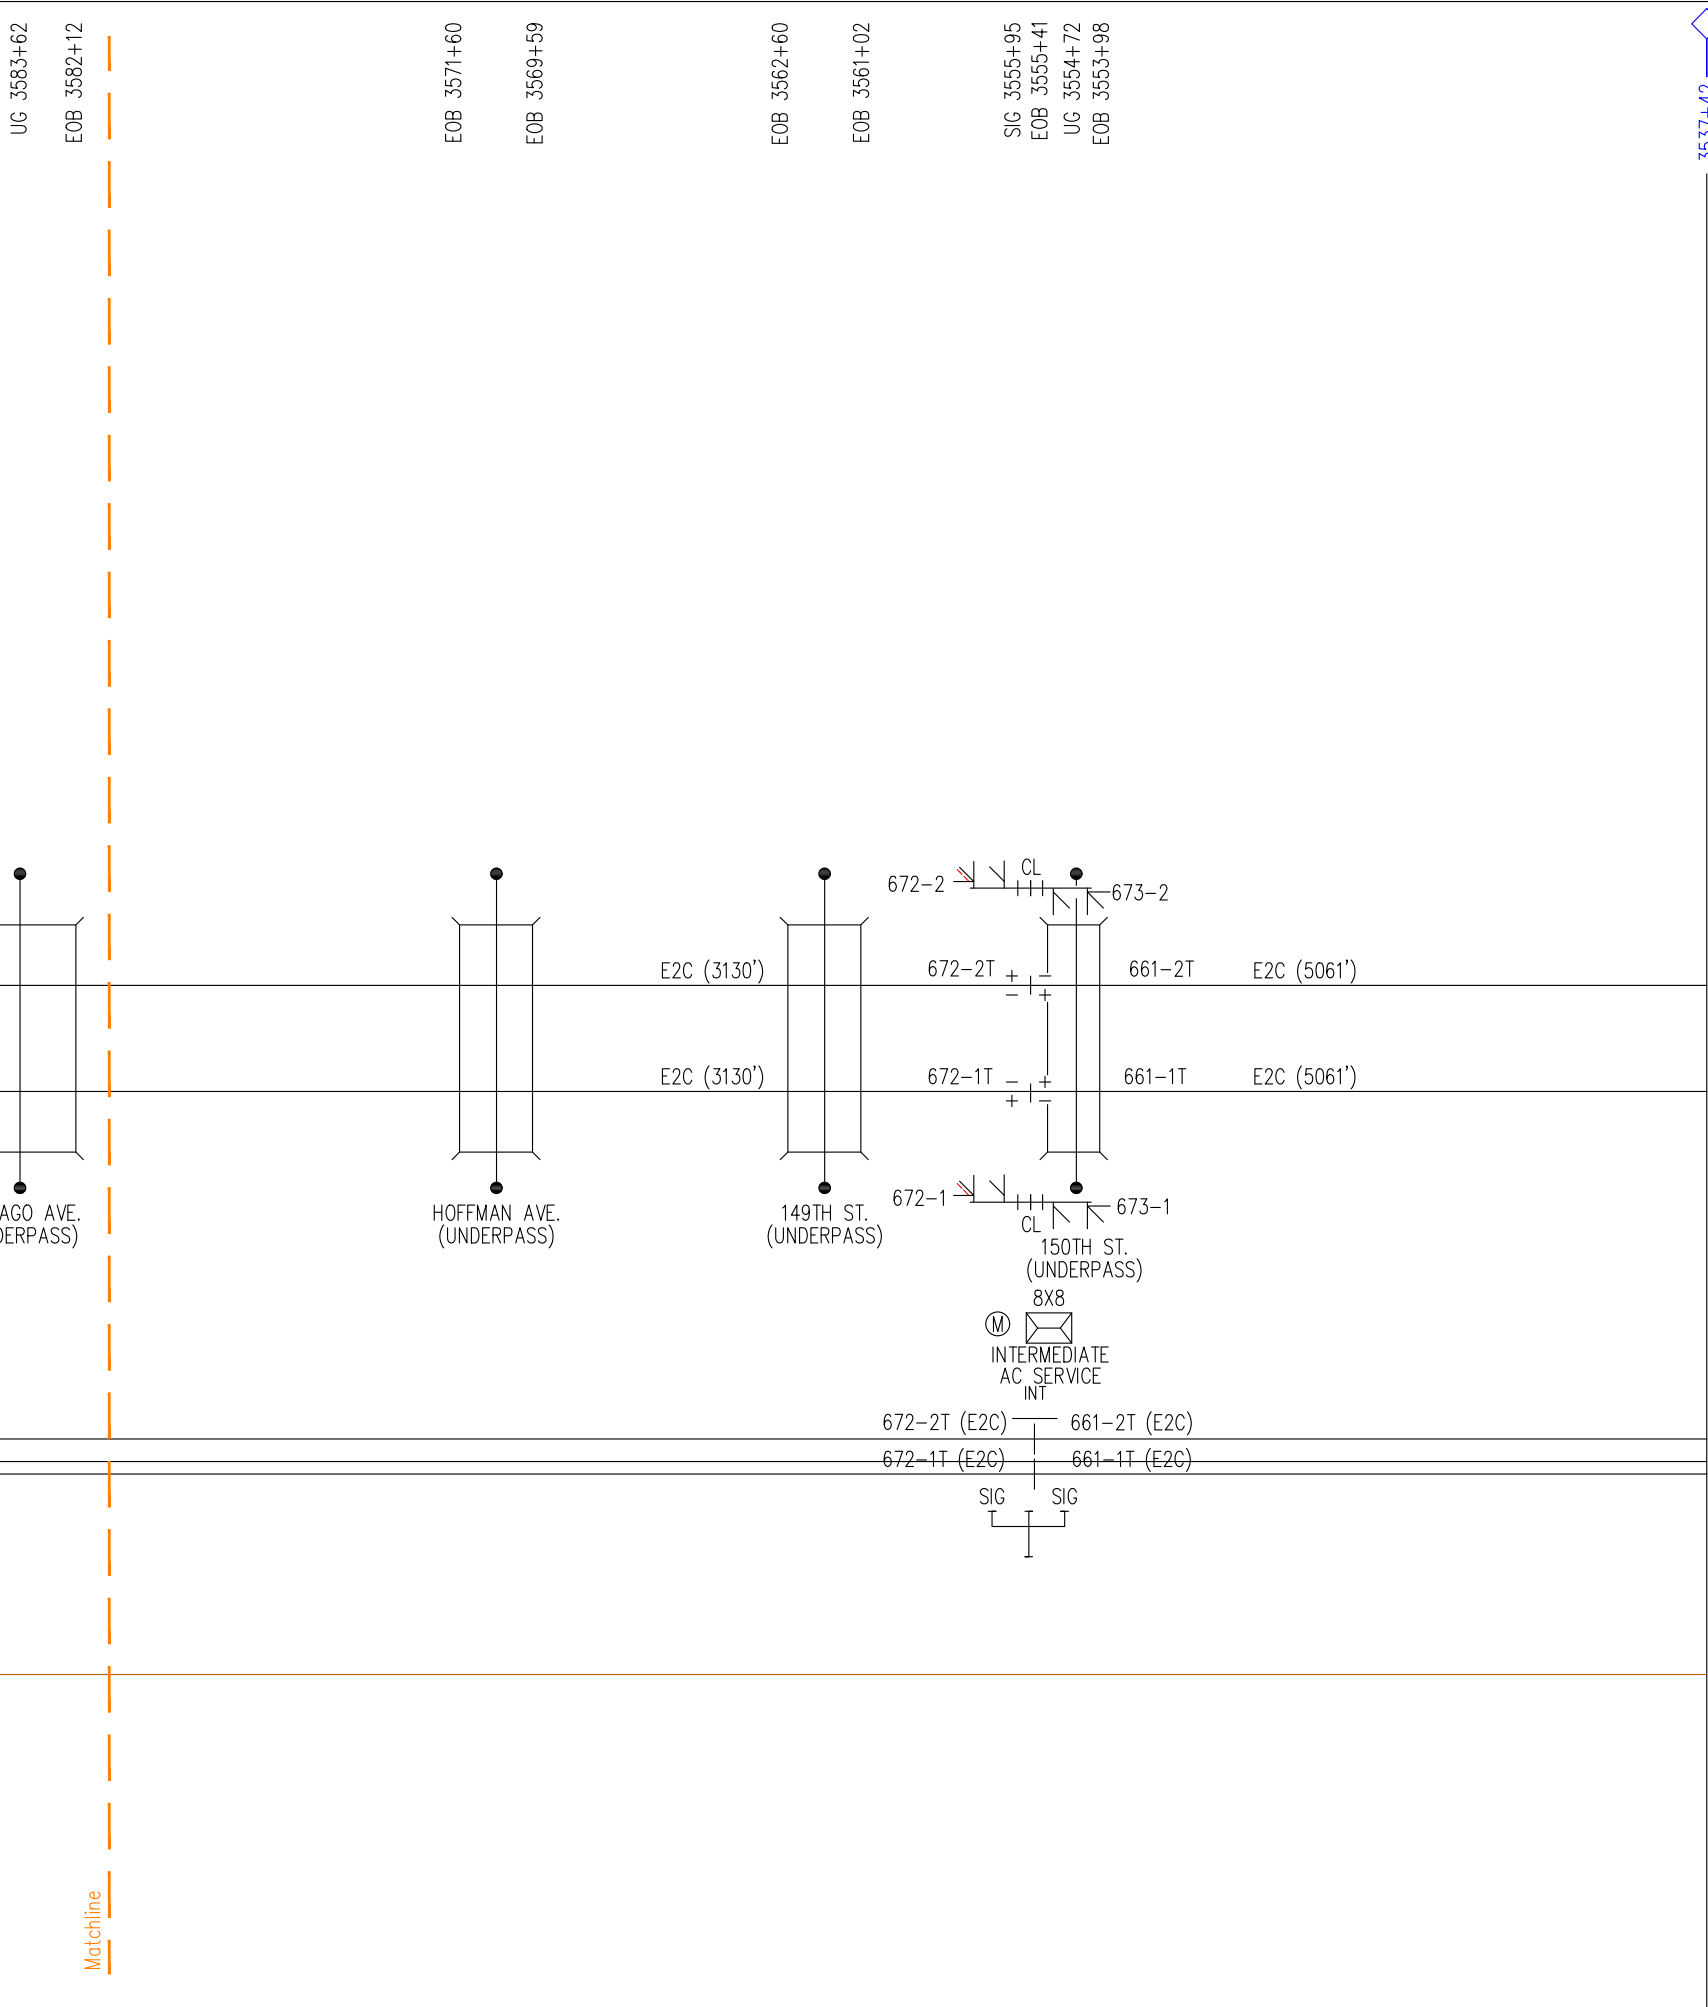

67

3537+42

70

3696+01

7

INSULATED END JOINT

SM

SNOW MELTER

TX

TRANS-MITTER

RX

RECEIVER

Y

HIGHWAY GRADE CROSSING

O

HIGHWAY OVER PASS

●

HIGHWAY UNDER PASS

▲

POWER DERAIL

⌋

CONTROLLED SWITCH IN INTERLOCKING

⌋

CONTROLLED SIGNAL

⌋

DWARF SIGNAL

⌋

AUTOMATIC SIGNAL

⌋

HAND HOLE

⊗

METER SERVICE

⌋

CROSSING START LOCATION

⌋

DERAIL

⌋

CRIBBING

⌋

BUILDING

⌋

SIGNAL CASE

⌋

C.I.H. = CENTRAL INSTRUMENT HOUSE
DER = DERAIL
EOB = END OF BLOCK
FO = FIBER OPTIC
HS = HIGHWAY CROSSING
IJ = INSULATED JOINT
LOC.A = SUPPLEMENTAL HOUSE
OG = OVER GRADE
UG = UNDER GRADE
PLT = PLATFORM
PS = POINT OF SWITCH
SIG = SIGNAL
SW = SWITCH
F/R = SE3 FEED AND RELAY
KEYED = RECEIVER KEYS ADJACENT TRANSMITTER
CABLE = RELAY LOGIC OVER EXPRESS CABLE
SE3 = SAFETRAN AC TRACK CIRCUIT
MAS = MAXIMUM AUTHORIZED SPEED
K = # 1000 HERTZ
ISL = ISLAND CIRCUIT
AVR = AVERAGE SPEED IN M.P.H.
Z = HIGH IMPEDANCE RCVR COUPLER
C = CROSSING
F = FLASHERS
B = BELLS
G = GATES
CW = CROSSING WARNING
ELX = ELECTROLOGIXS
FO = FIBER OPTIC
TPSS = TRACTION POWER SUBSTATION
CL = COLORLIGHT
Z = HIGH IMPEDANCE COUPLER
(cd) = CANTILEVER
E2C = ELECTRIFIED ELECTROCODE

REVISIONS

(×) = EXISTING CASE/HOUSE LOCATION
(×) = PROPOSED CASE/HOUSE LOCATION
(LEVEL 1) TITLE BLOCK AND BORDER
(LEVEL 2) BLACK = EXISTING
BLUE = NOTE
(LEVEL 3) RED = IN
(LEVEL 4) GREEN = OUT
(LEVEL 5) ⊗ = NEW AC SERVICE
(LEVEL 5) ⊙ = EXISTING AC SERVICE
(LEVEL 6) BLACK = EXISTING X-ING
(LEVEL 7) BROWN = FO - COMM. LINES
(LEVEL 8) MAGENTA = OPERATION CABLES
(LEVEL 15) = CROSSING START FREQUENCIES
(LEVEL MUST BE ACTIVATED, WITH LEVEL 7 & 8 DEACTIVATED).
(LEVEL 16) ORANGE = FREQUENCY OUT
(LEVEL 17) PURPLE = FREQUENCY IN

HORIZONTAL SCALE :
1 INCH = 500 FEET

NICTD
NORTHERN INDIANA COMMUTER TRANSPORTATION DISTRICT
WEST LAKE
CORRIDOR PROJECT
M.P. 67 TO M.P. 69
DESIGNER SKETCH WITH CROSSING FREQUENCY STUDY

DESIGNED DAI/JNV	DIGITIZED DAI/JNV
NEXT FILE	NEXT SH
CHECKED DAI/BD0	DATE 12-01-23
FILE SKETCH	SHEET 001C