



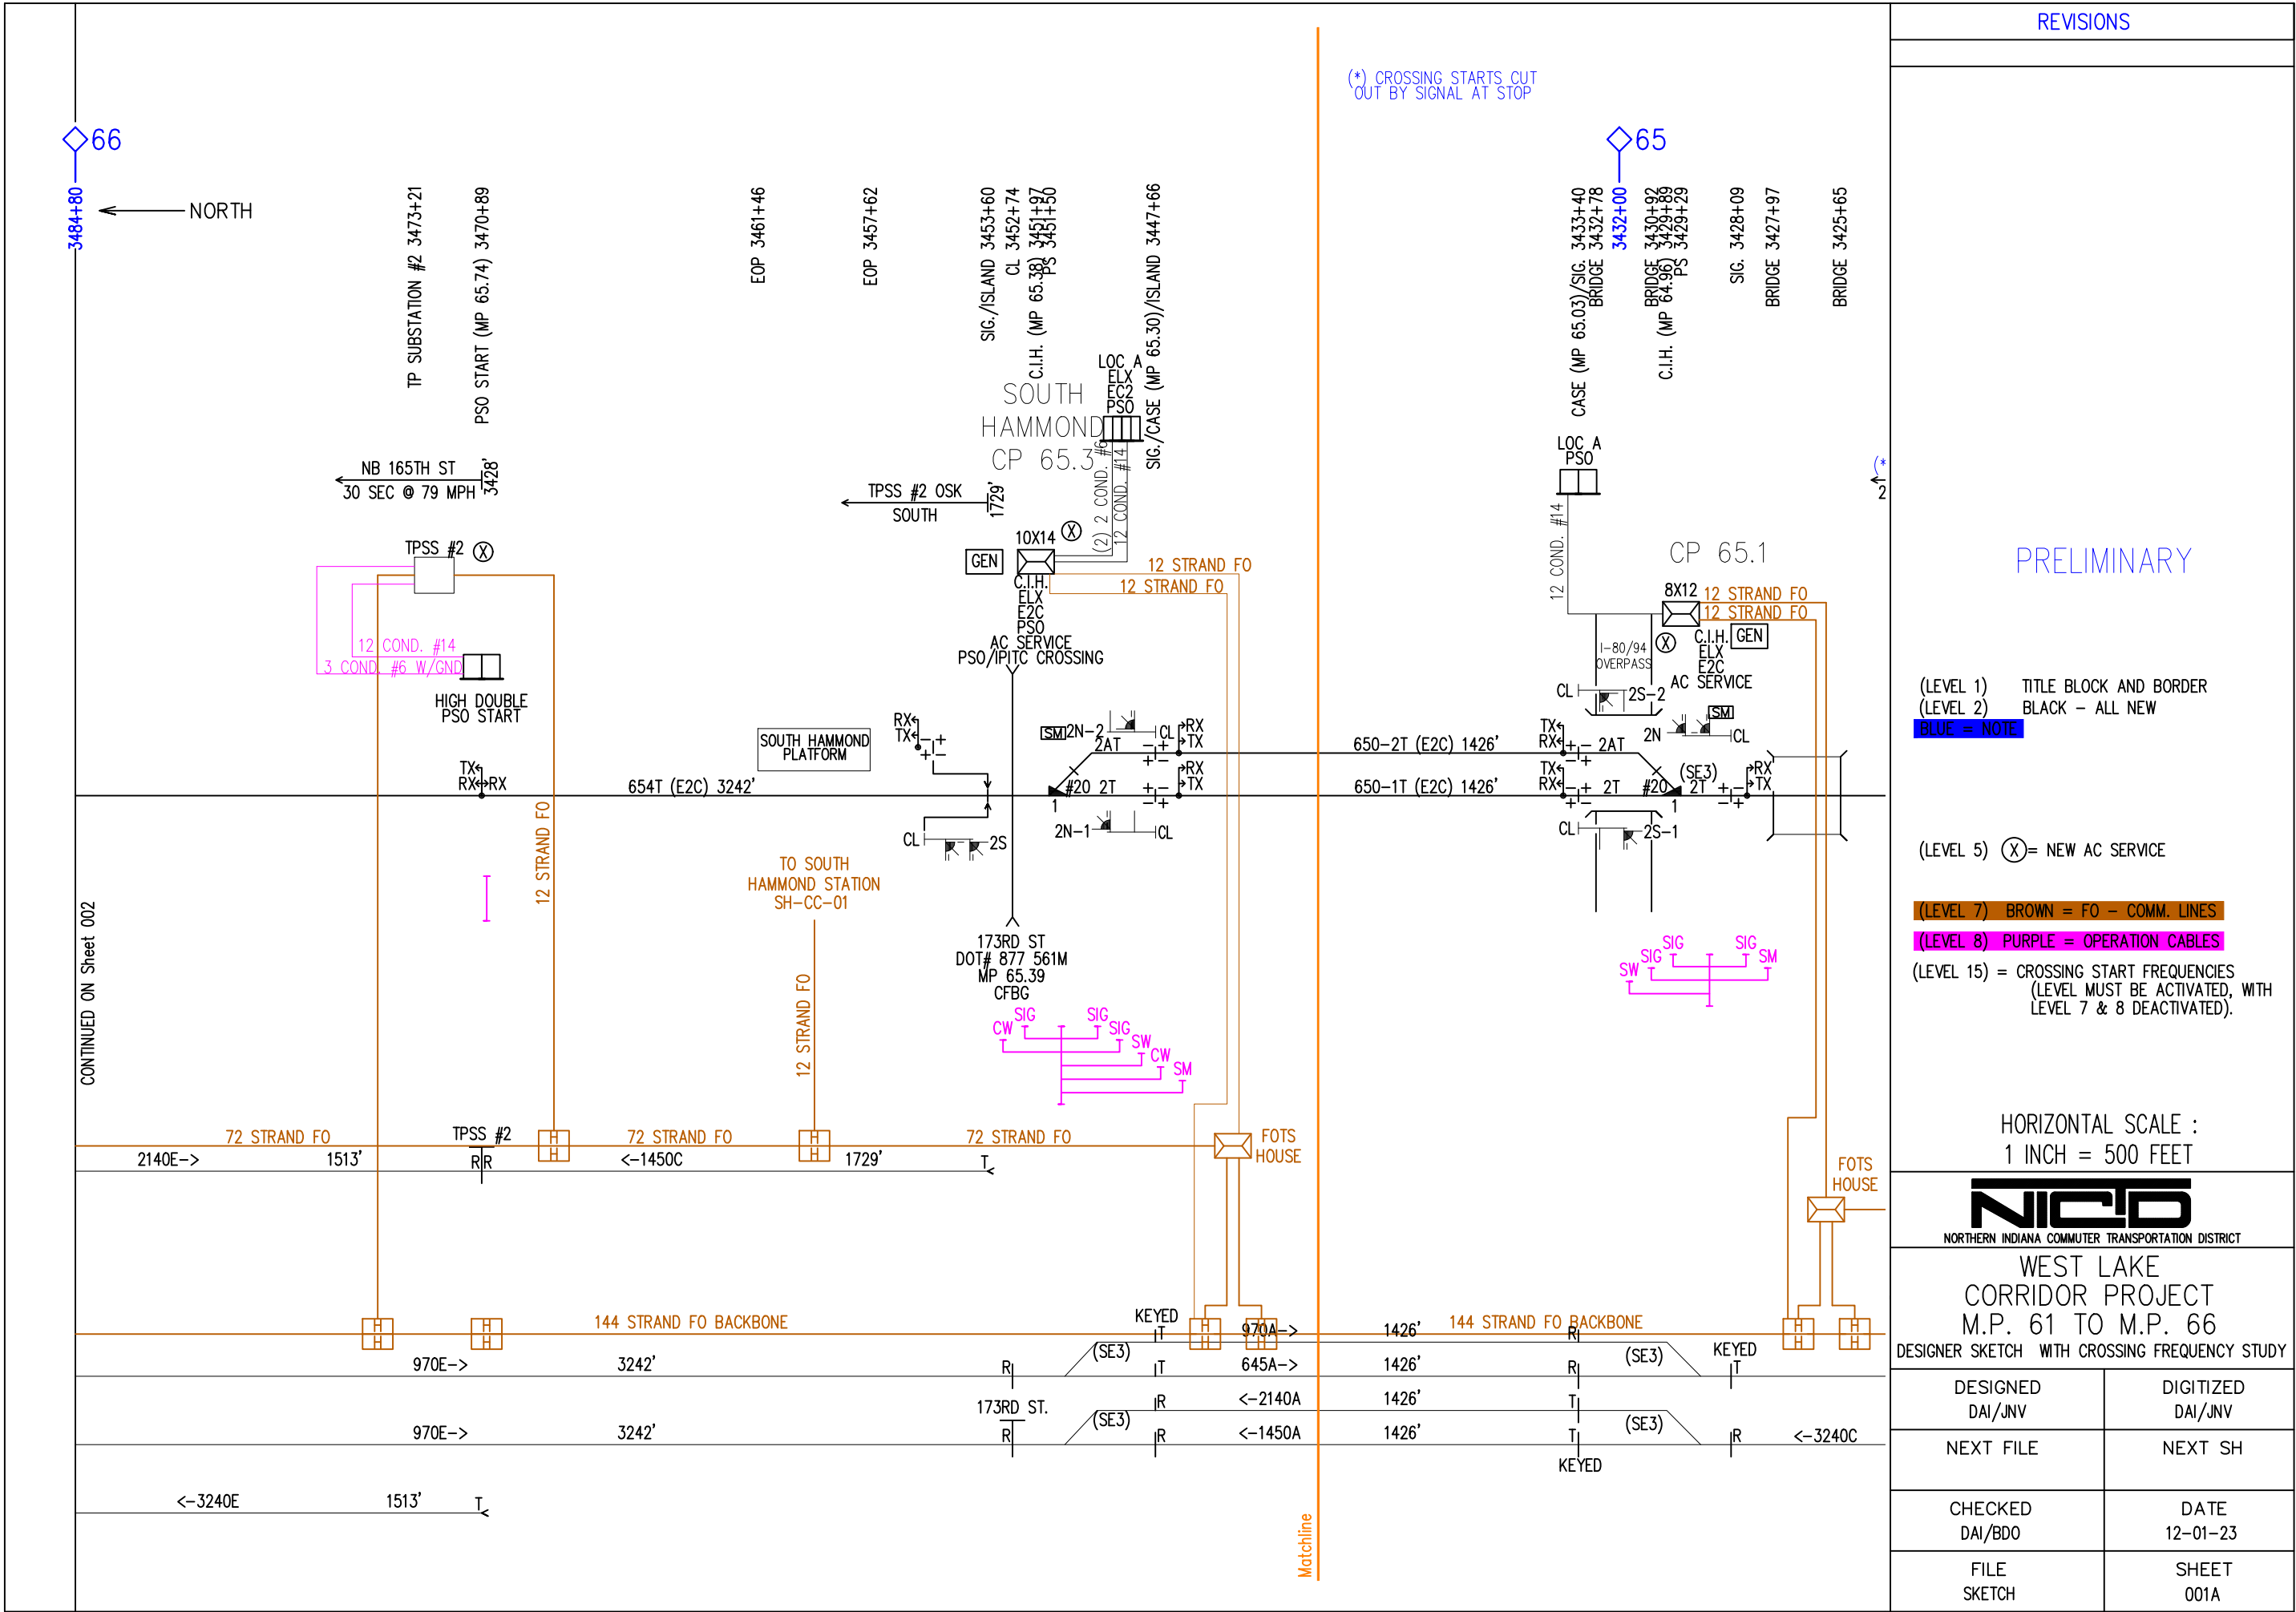

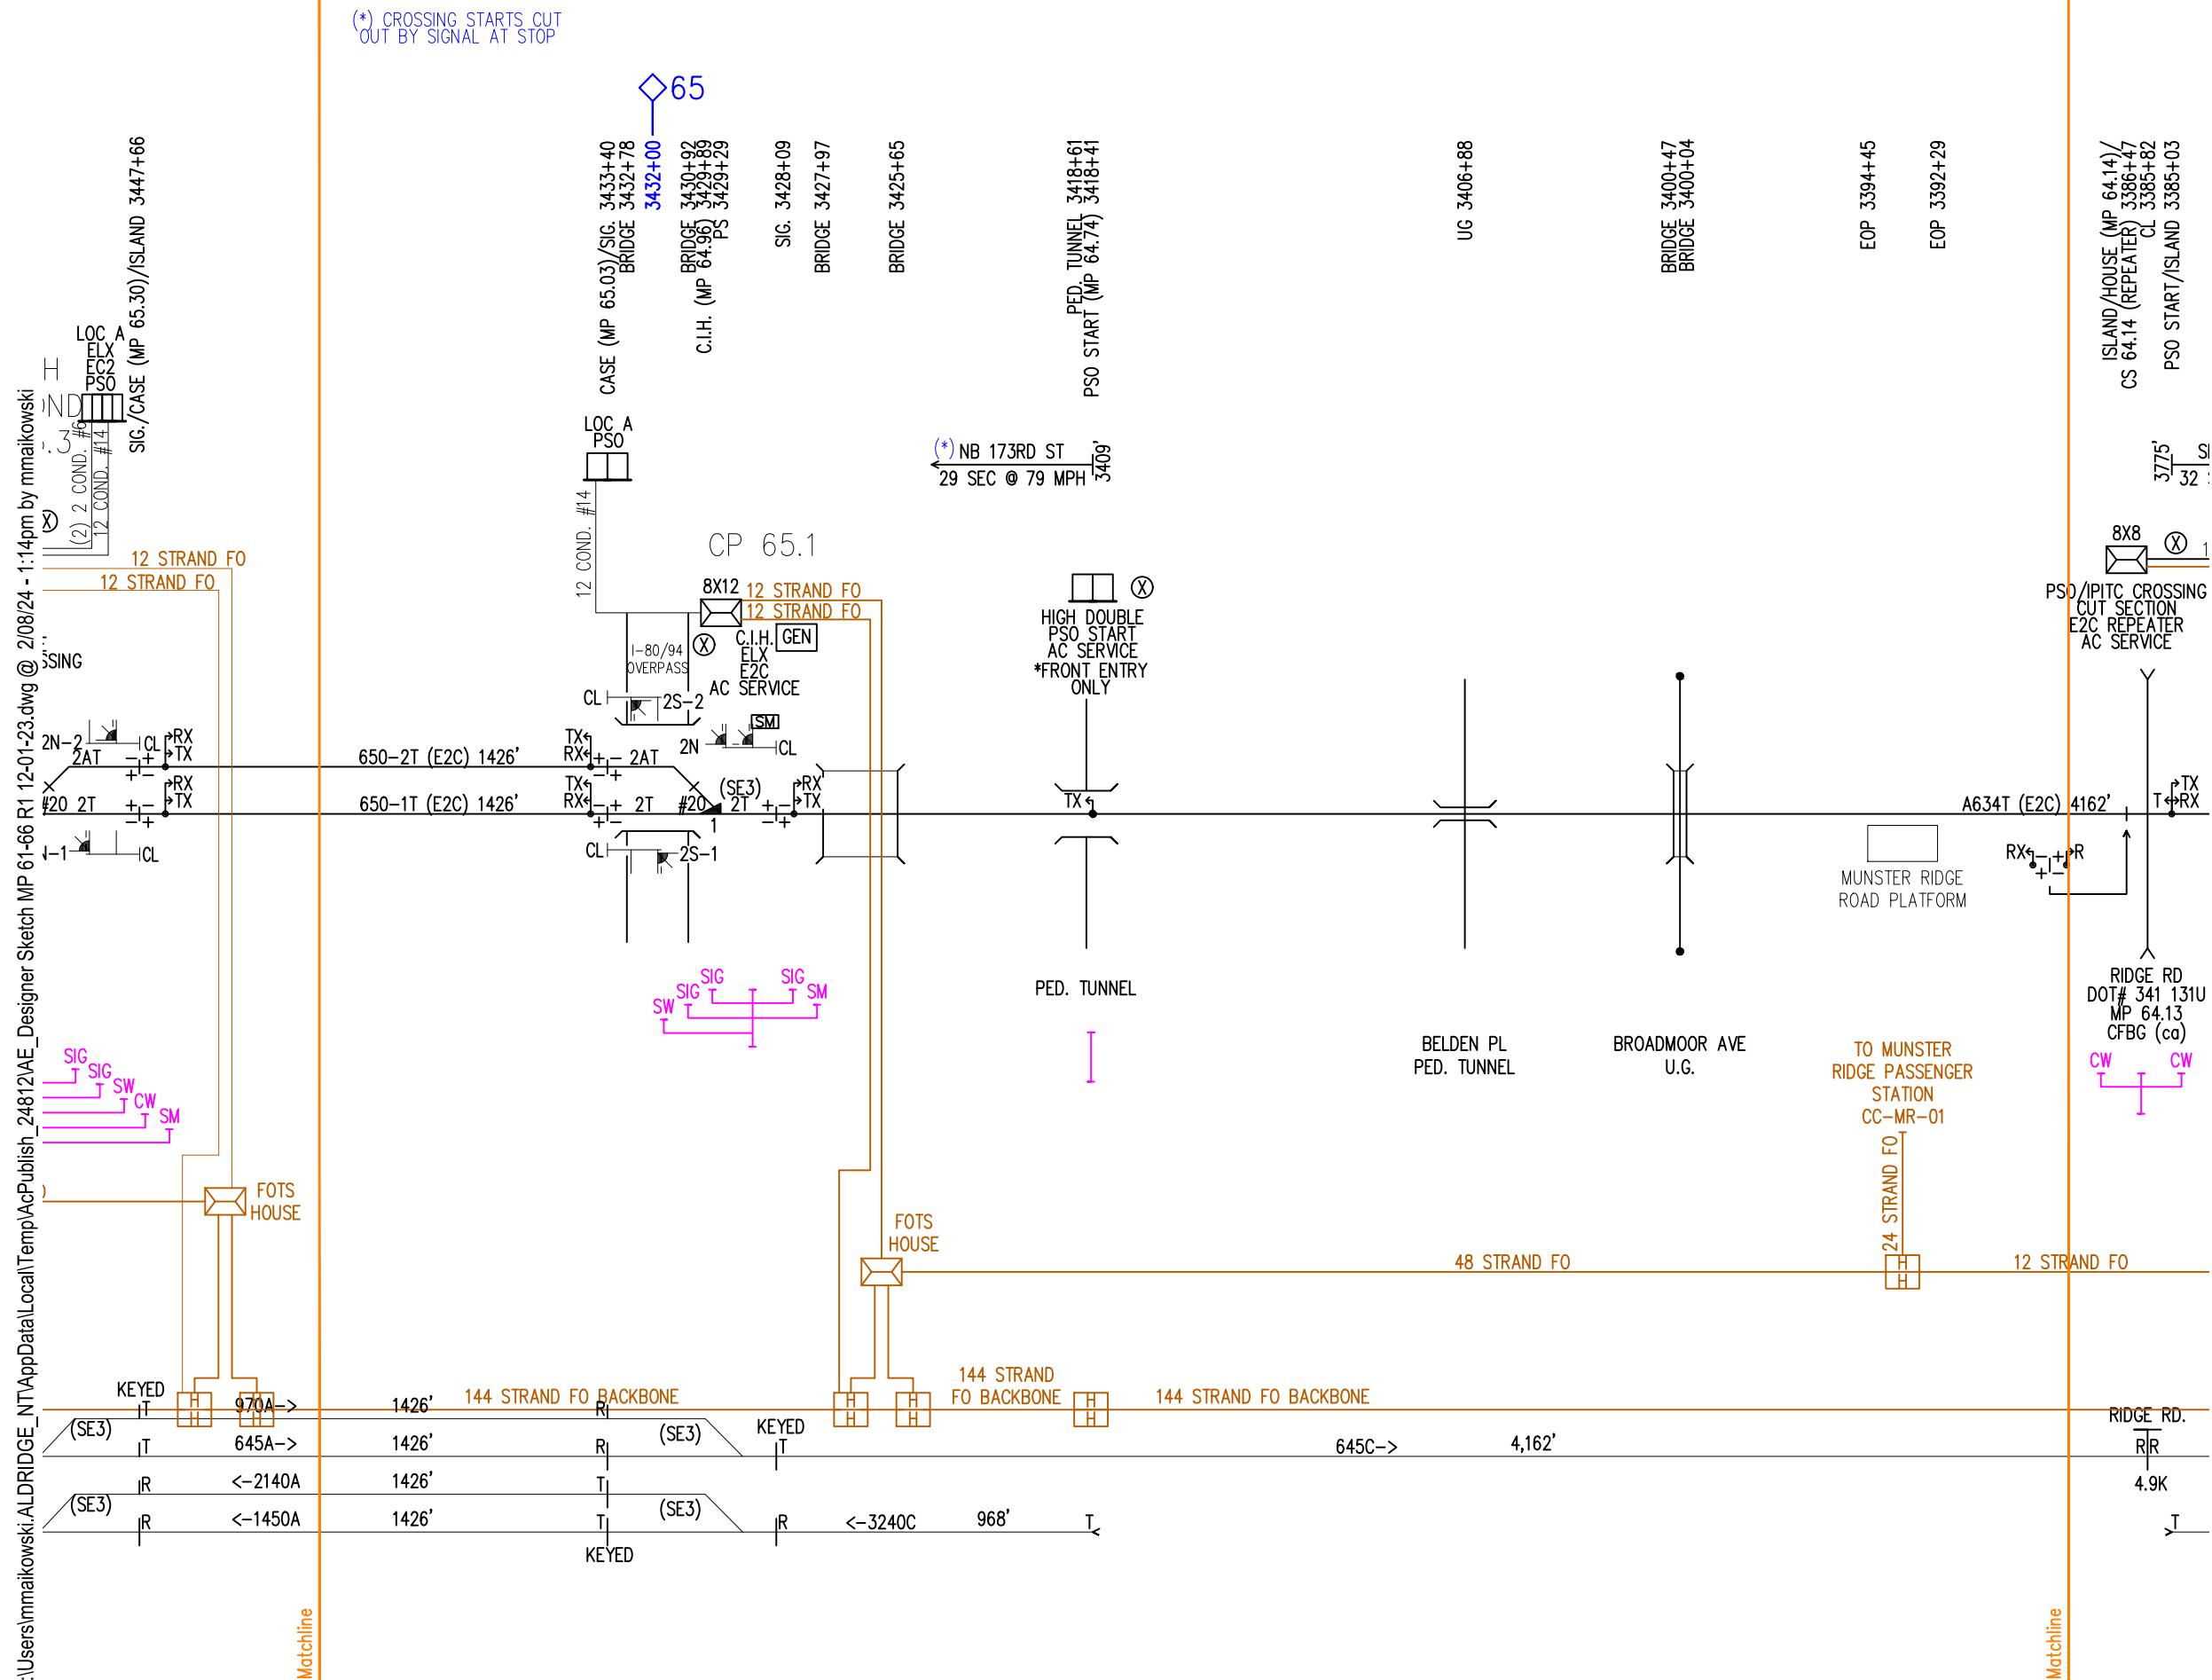

REVISIONS

PRELIMINARY

(LEVEL 1) TITLE BLOCK AND BORDER
(LEVEL 2) BLACK - ALL NEW
BLUE = NOTE

(LEVEL 5) (X) = NEW AC SERVICE

(LEVEL 7) BROWN = FO - COMM. LINES

(LEVEL 8) PURPLE = OPERATION CABLES

(LEVEL 15) = CROSSING START FREQUENCIES
(LEVEL MUST BE ACTIVATED, WITH
LEVEL 7 & 8 DEACTIVATED).

HORIZONTAL SCALE :
1 INCH = 500 FEET



NORTHERN INDIANA COMMUTER TRANSPORTATION DISTRICT

WEST LAKE
CORRIDOR PROJECT
M.P. 61 TO M.P. 66

DESIGNER SKETCH WITH CROSSING FREQUENCY STUDY

DESIGNED DAI/JNV	DIGITIZED DAI/JNV
NEXT FILE	NEXT SH
CHECKED DAI/BD0	DATE 12-01-23
FILE SKETCH	SHEET 001B



NICTD
NORTHERN INDIANA COMMITTEE TRANSPORTATION DISTRICT

WEST LAKE
CORRIDOR PROJECT
M.P. 61 TO M.P. 66
DESIGNER SKETCH WITH CROSSING FREQUENCY STUDY

DESIGNED DAI/JNV	DIGITIZED DAI/JNV
NEXT FILE	NEXT SH
CHECKED DAI/BDO	DATE 12-01-23
FILE SKETCH	SHEET 001C



PRELIMINARY

BLUE = NOTE

(LEVEL 7) BROWN = FO - COMM. LINES

(LEVEL 15) = CROSSING START FREQUENCIES



DESIGNED	DIGITIZED
----------	-----------

DESIGNED	DIGITIZE
DAL/INV	DAL/INV


NEXT FILE	NEXT S
-----------	--------

CHECKED	DATE
---------	------

FILE	SHEET
------	-------

Matchline

C:\Users\mmaikowski\NTAppData\Local\Temp\AcPublish_24812\AE_Designer Sketch MP 61-66 R1 12-01-23.dwg @ 2/08/24 - 1:14pm by mmaikowski

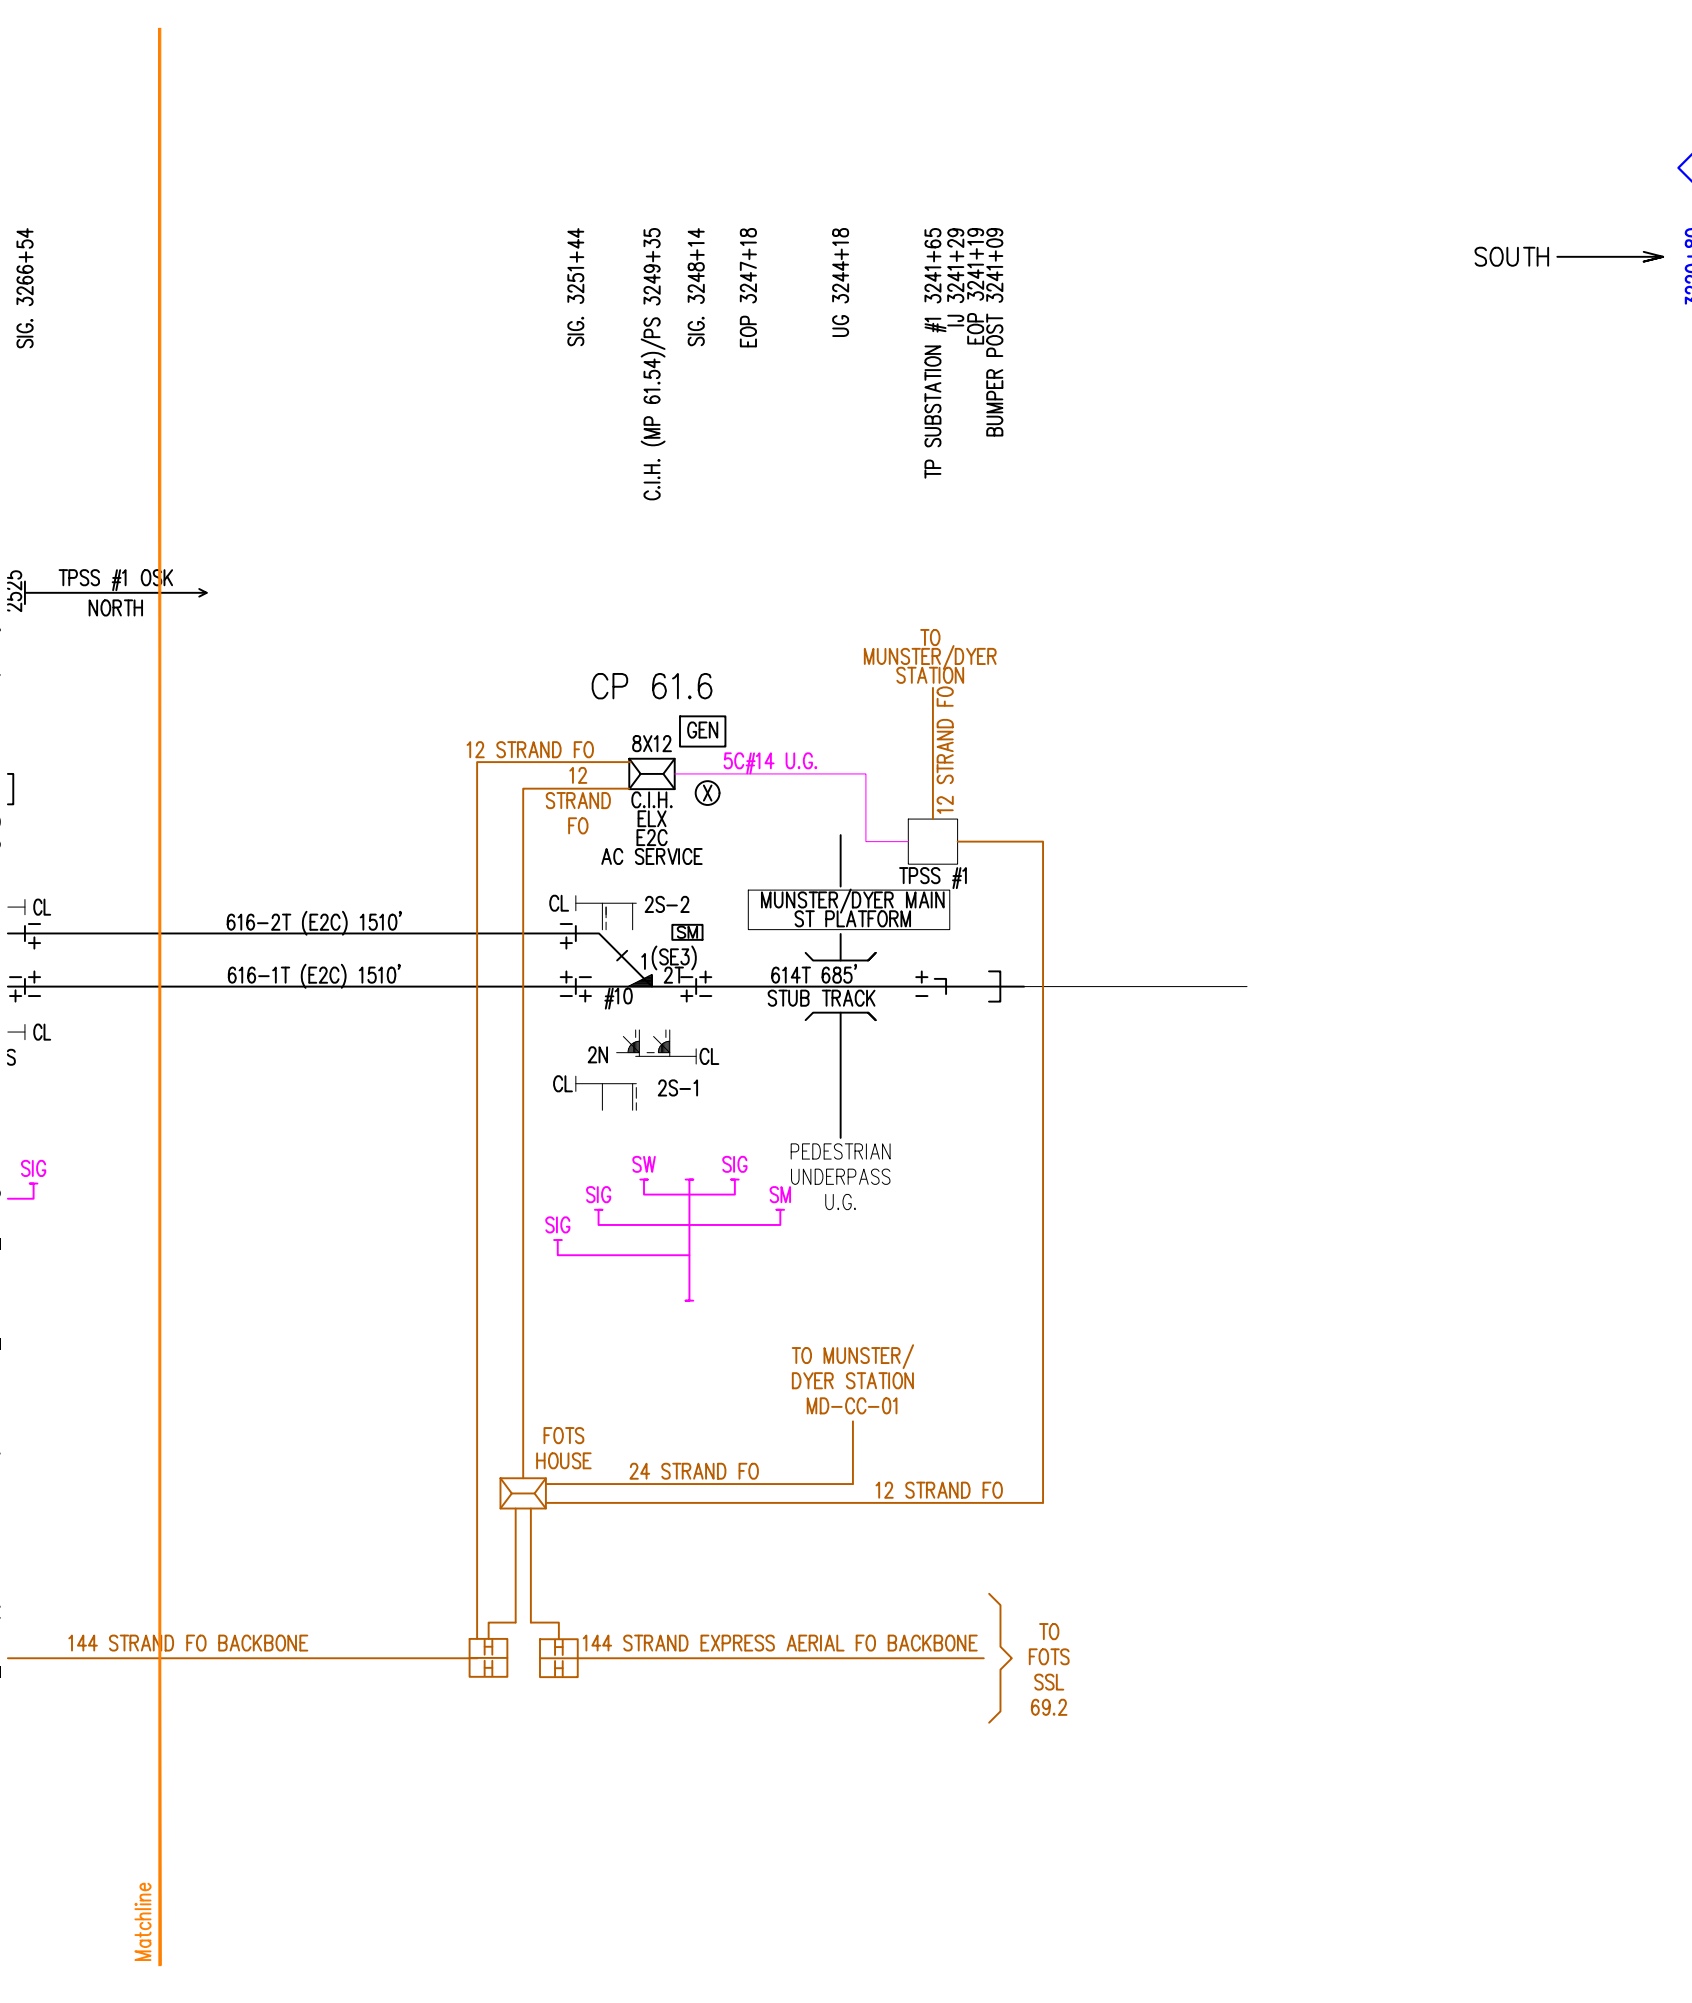

LEGEND

70

61

3696+01

MILE MARKER

Y

Y

HIGHWAY GRADE CROSSING

O

O

HIGHWAY OVER PASS

●

●

HIGHWAY UNDER PASS

TX

↓

TRANS-MITTER

RX

↓

RECEIVER

▲

POWER DERAIL

SM

SM

SNOW MELTER

I

I

INSULATED JOINT

7

7

INSULATED END JOINT

↗

↘

CONTROLLED SWITCH IN INTERLOCKING

⏏

⏏

AUTOMATIC SIGNAL

⏏

⏏

CONTROLLED SIGNAL

⏏

⏏

DWARF SIGNAL

H

H

HAND HOLE

⏏

⏏

BUILDING

□

□

SIGNAL CASE

GEN

GEN

GENERATOR

⊗

⊗

METER SERVICE

⏏

⏏

CRIBBING

▽

▽

DERAIL

←

→

CROSSING START LOCATION

STREET NAME

TIME AND SPEED

DISTANCE

C.I.H. = CENTRAL INSTRUMENT HOUSE

DER = DERAIL

EOB = END OF BLOCK

FO = FIBER OPTIC

HS = HIGHWAY CROSSING

IJ = INSULATED JOINT

LOC.A = SUPPLEMENTAL HOUSE

OG = OVER GRADE

UG = UNDER GRADE

PLT = PLATFORM

PS = POINT OF SWITCH

SIG = SIGNAL

SW = SWITCH

F/R = SE3 FEED AND RELAY

KEYED = RECEIVER KEYS ADJACENT TRANSMITTER

CABLE = RELAY LOGIC OVER EXPRESS CABLE

SE3 = SAFETRAN AC TRACK CIRCUIT

MAS = MAXIMUM AUTHORIZED SPEED

K = # 1000 HERTZ

ISL = ISLAND CIRCUIT

AVR = AVERAGE SPEED IN M.P.H.

C = CROSSING

F = FLASHERS

B = BELLS

G = GATES

CW = CROSSING WARNING

ELX = ELECTROLOGIXS

FO = FIBER OPTIC

TPSS = TRACTION POWER SUBSTATION

CL = COLORLIGHT

(ca) = CANTILEVER

E2C = ELECTRIFIED ELECTROCODE

REVISIONS	
PRELIMINARY	
(LEVEL 1) TITLE BLOCK AND BORDER (LEVEL 2) BLACK - ALL NEW BLUE = NOTE	
(LEVEL 5) ⊗ = NEW AC SERVICE	
(LEVEL 7) BROWN = FO - COMM. LINES	
(LEVEL 8) PURPLE = OPERATION CABLES	
(LEVEL 15) = CROSSING START FREQUENCIES (LEVEL MUST BE ACTIVATED, WITH LEVEL 7 & 8 DEACTIVATED).	
HORIZONTAL SCALE : 1 INCH = 500 FEET	
NICTD NORTHERN INDIANA COMMUTER TRANSPORTATION DISTRICT	
WEST LAKE CORRIDOR PROJECT M.P. 61 TO M.P. 66 DESIGNER SKETCH WITH CROSSING FREQUENCY STUDY	
DESIGNED DAI/JNV	DIGITIZED DAI/JNV
NEXT FILE	NEXT SH
CHECKED DAI/BDO	DATE 12-01-23
FILE SKETCH	SHEET 001E