



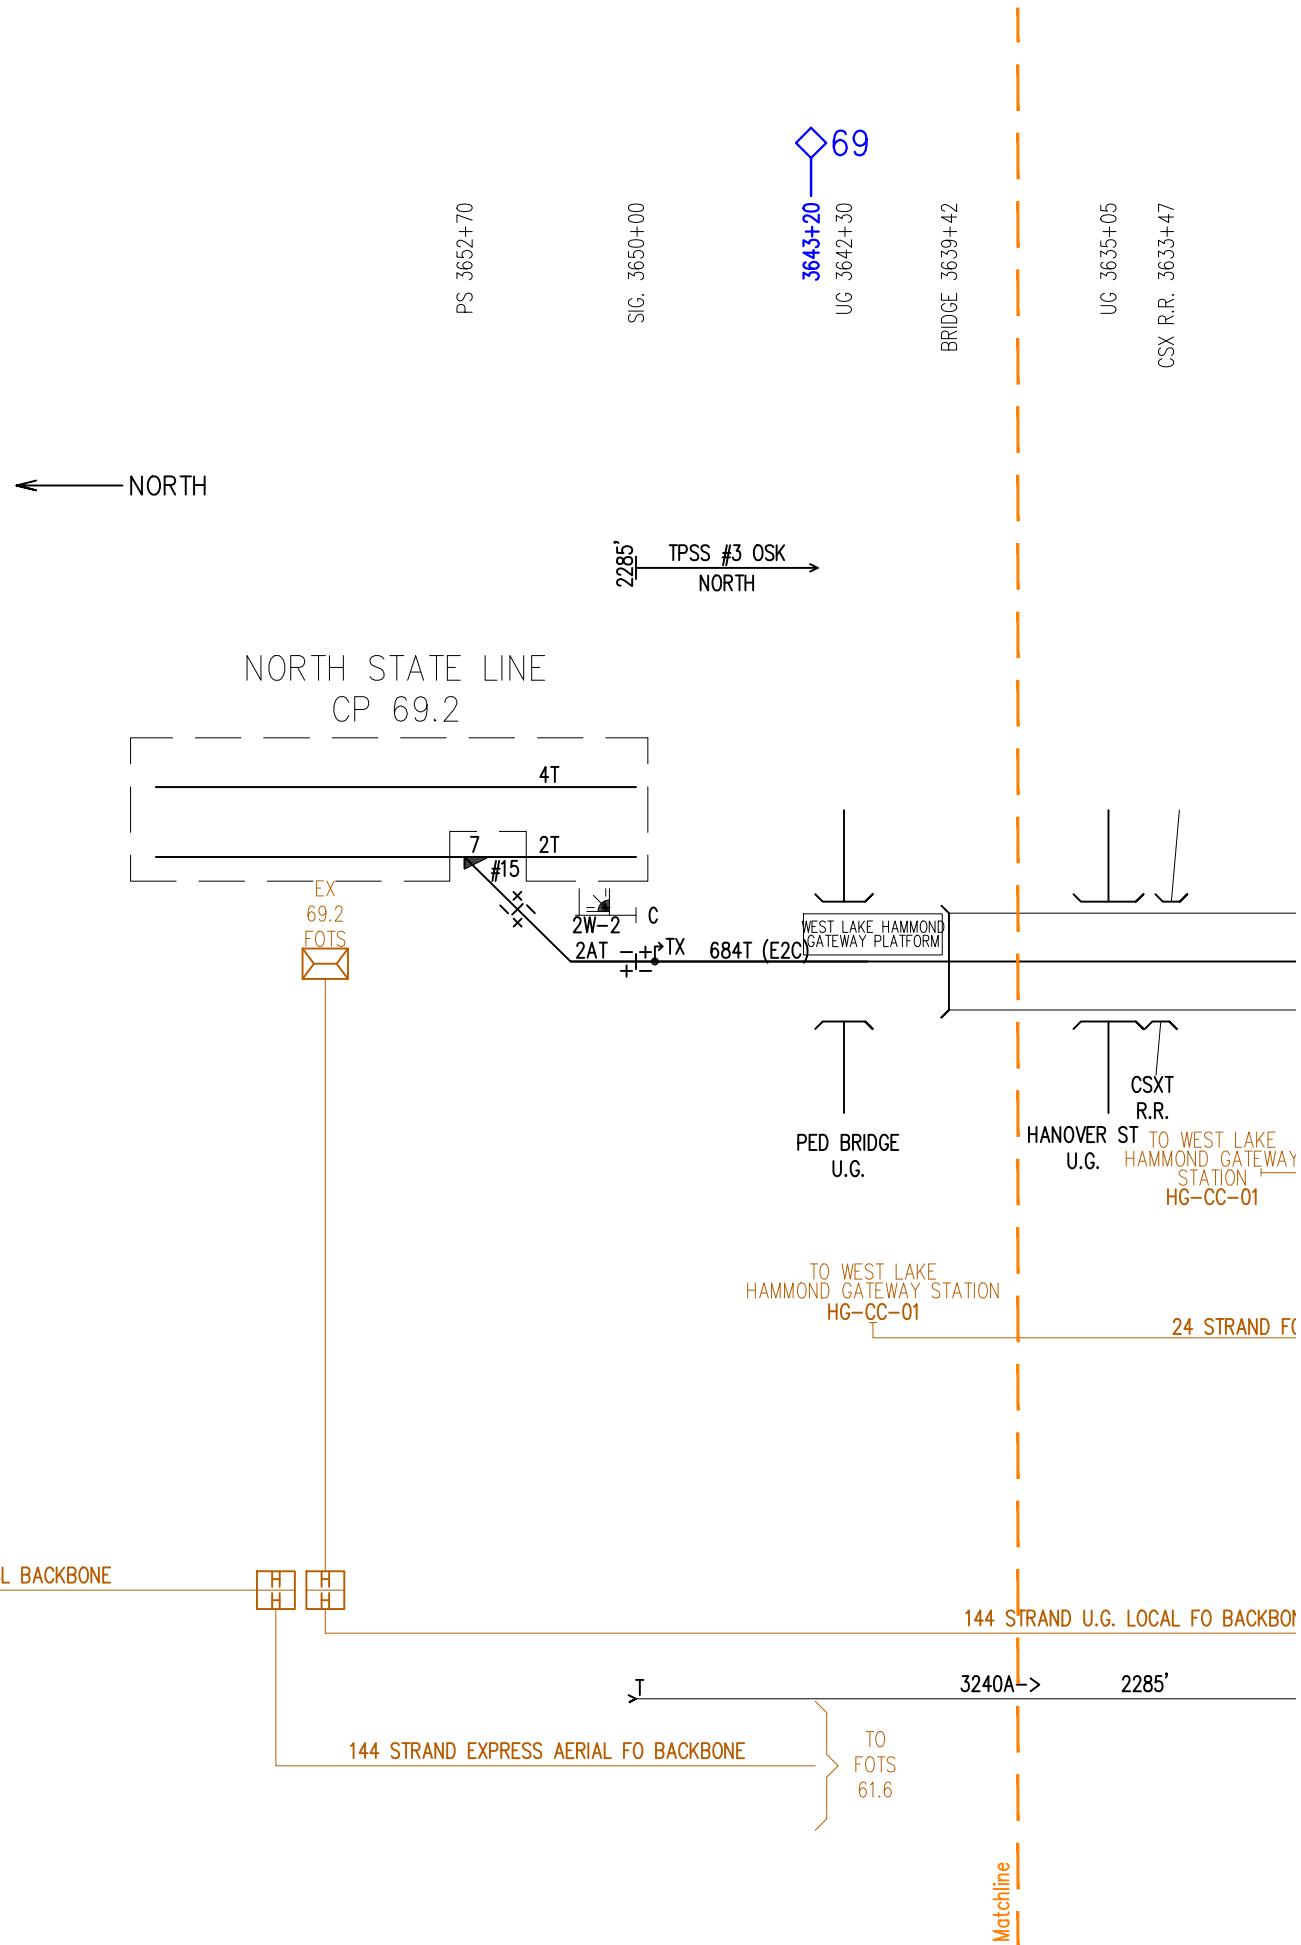

REVISIONS	
PRELIMINARY	
(LEVEL 1) TITLE BLOCK AND BORDER (LEVEL 2) BLACK - ALL NEW BLUE = NOTE (LEVEL 5) ⊗ = NEW AC SERVICE (LEVEL 7) BROWN = FO - COMM. LINES (LEVEL 8) PURPLE = OPERATION CABLES (LEVEL 15) = CROSSING START FREQUENCIES (LEVEL MUST BE ACTIVATED, WITH LEVEL 7 & 8 DEACTIVATED). HORIZONTAL SCALE : 1 INCH = 500 FEET	

NICTD NORTHERN INDIANA COMMUTER TRANSPORTATION DISTRICT	
WEST LAKE CORRIDOR PROJECT M.P. 66 TO M.P. 69 DESIGNER SKETCH WITH CROSSING FREQUENCY STUDY	
DESIGNED DAI/JNV	DIGITIZED DAI/JNV
NEXT FILE	NEXT SH
CHECKED DAI/BDO	DATE 12-01-23
FILE SKETCH	SHEET 002A

C:\Users\mmaikowski\NTAppData\LocalTemp\AcPublish_24812\AE_Designer Sketch MP 66-69 R1 12-01-23.dwg @ 2/08/24 - 1:14pm by mmaikowski

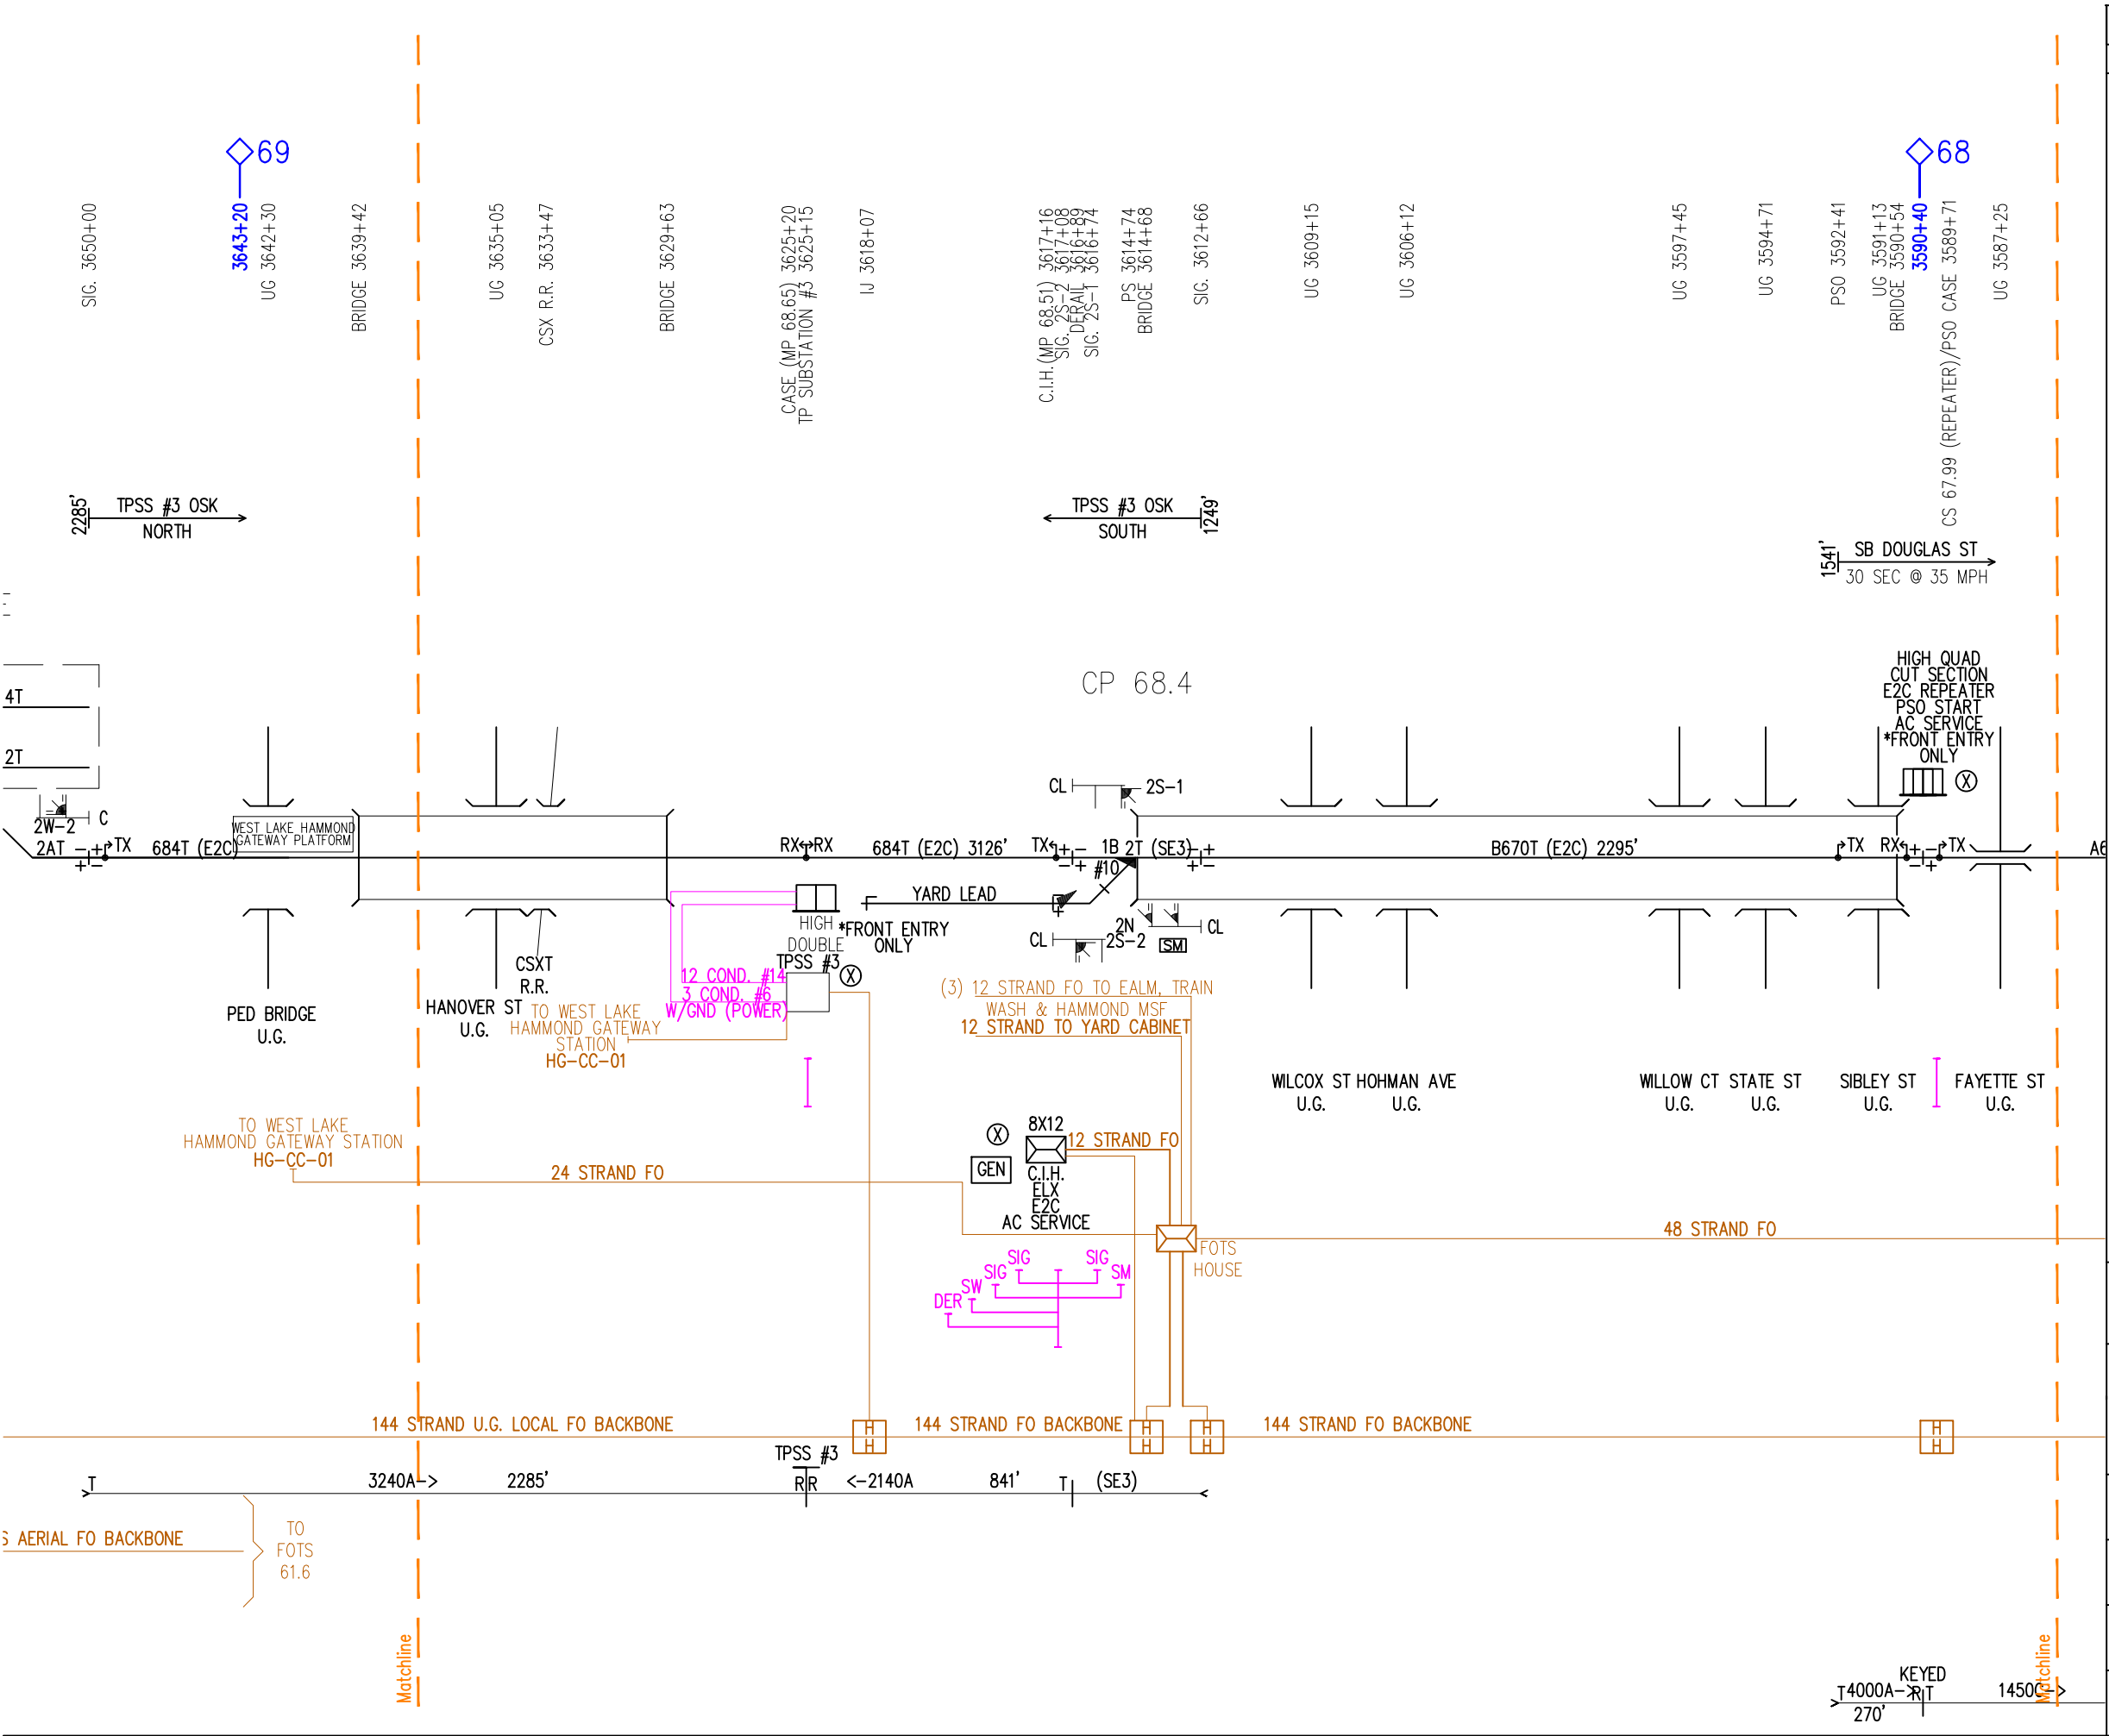

REVISIONS

PRELIMINARY

(LEVEL 1) TITLE BLOCK AND BORDER
(LEVEL 2) BLACK - ALL NEW
BLUE = NOTE

(LEVEL 5) (X) = NEW AC SERVICE

(LEVEL 7) BROWN = FO - COMM. LINES

(LEVEL 8) PURPLE = OPERATION CABLES

(LEVEL 15) = CROSSING START FREQUENCIES
(LEVEL MUST BE ACTIVATED, WITH
LEVEL 7 & 8 DEACTIVATED).

HORIZONTAL SCALE :
1 INCH = 500 FEET




NORTHERN INDIANA COMMUTER TRANSPORTATION DISTRICT

WEST LAKE
CORRIDOR PROJECT
M.P. 66 TO M.P. 69


DESIGNER SKETCH WITH CROSSING FREQUENCY STUDY

DESIGNED DAI/JNV	DIGITIZED DAI/JNV
NEXT FILE	NEXT SH
CHECKED DAI/BD0	DATE 12-01-23
FILE SKETCH	SHEET 002B

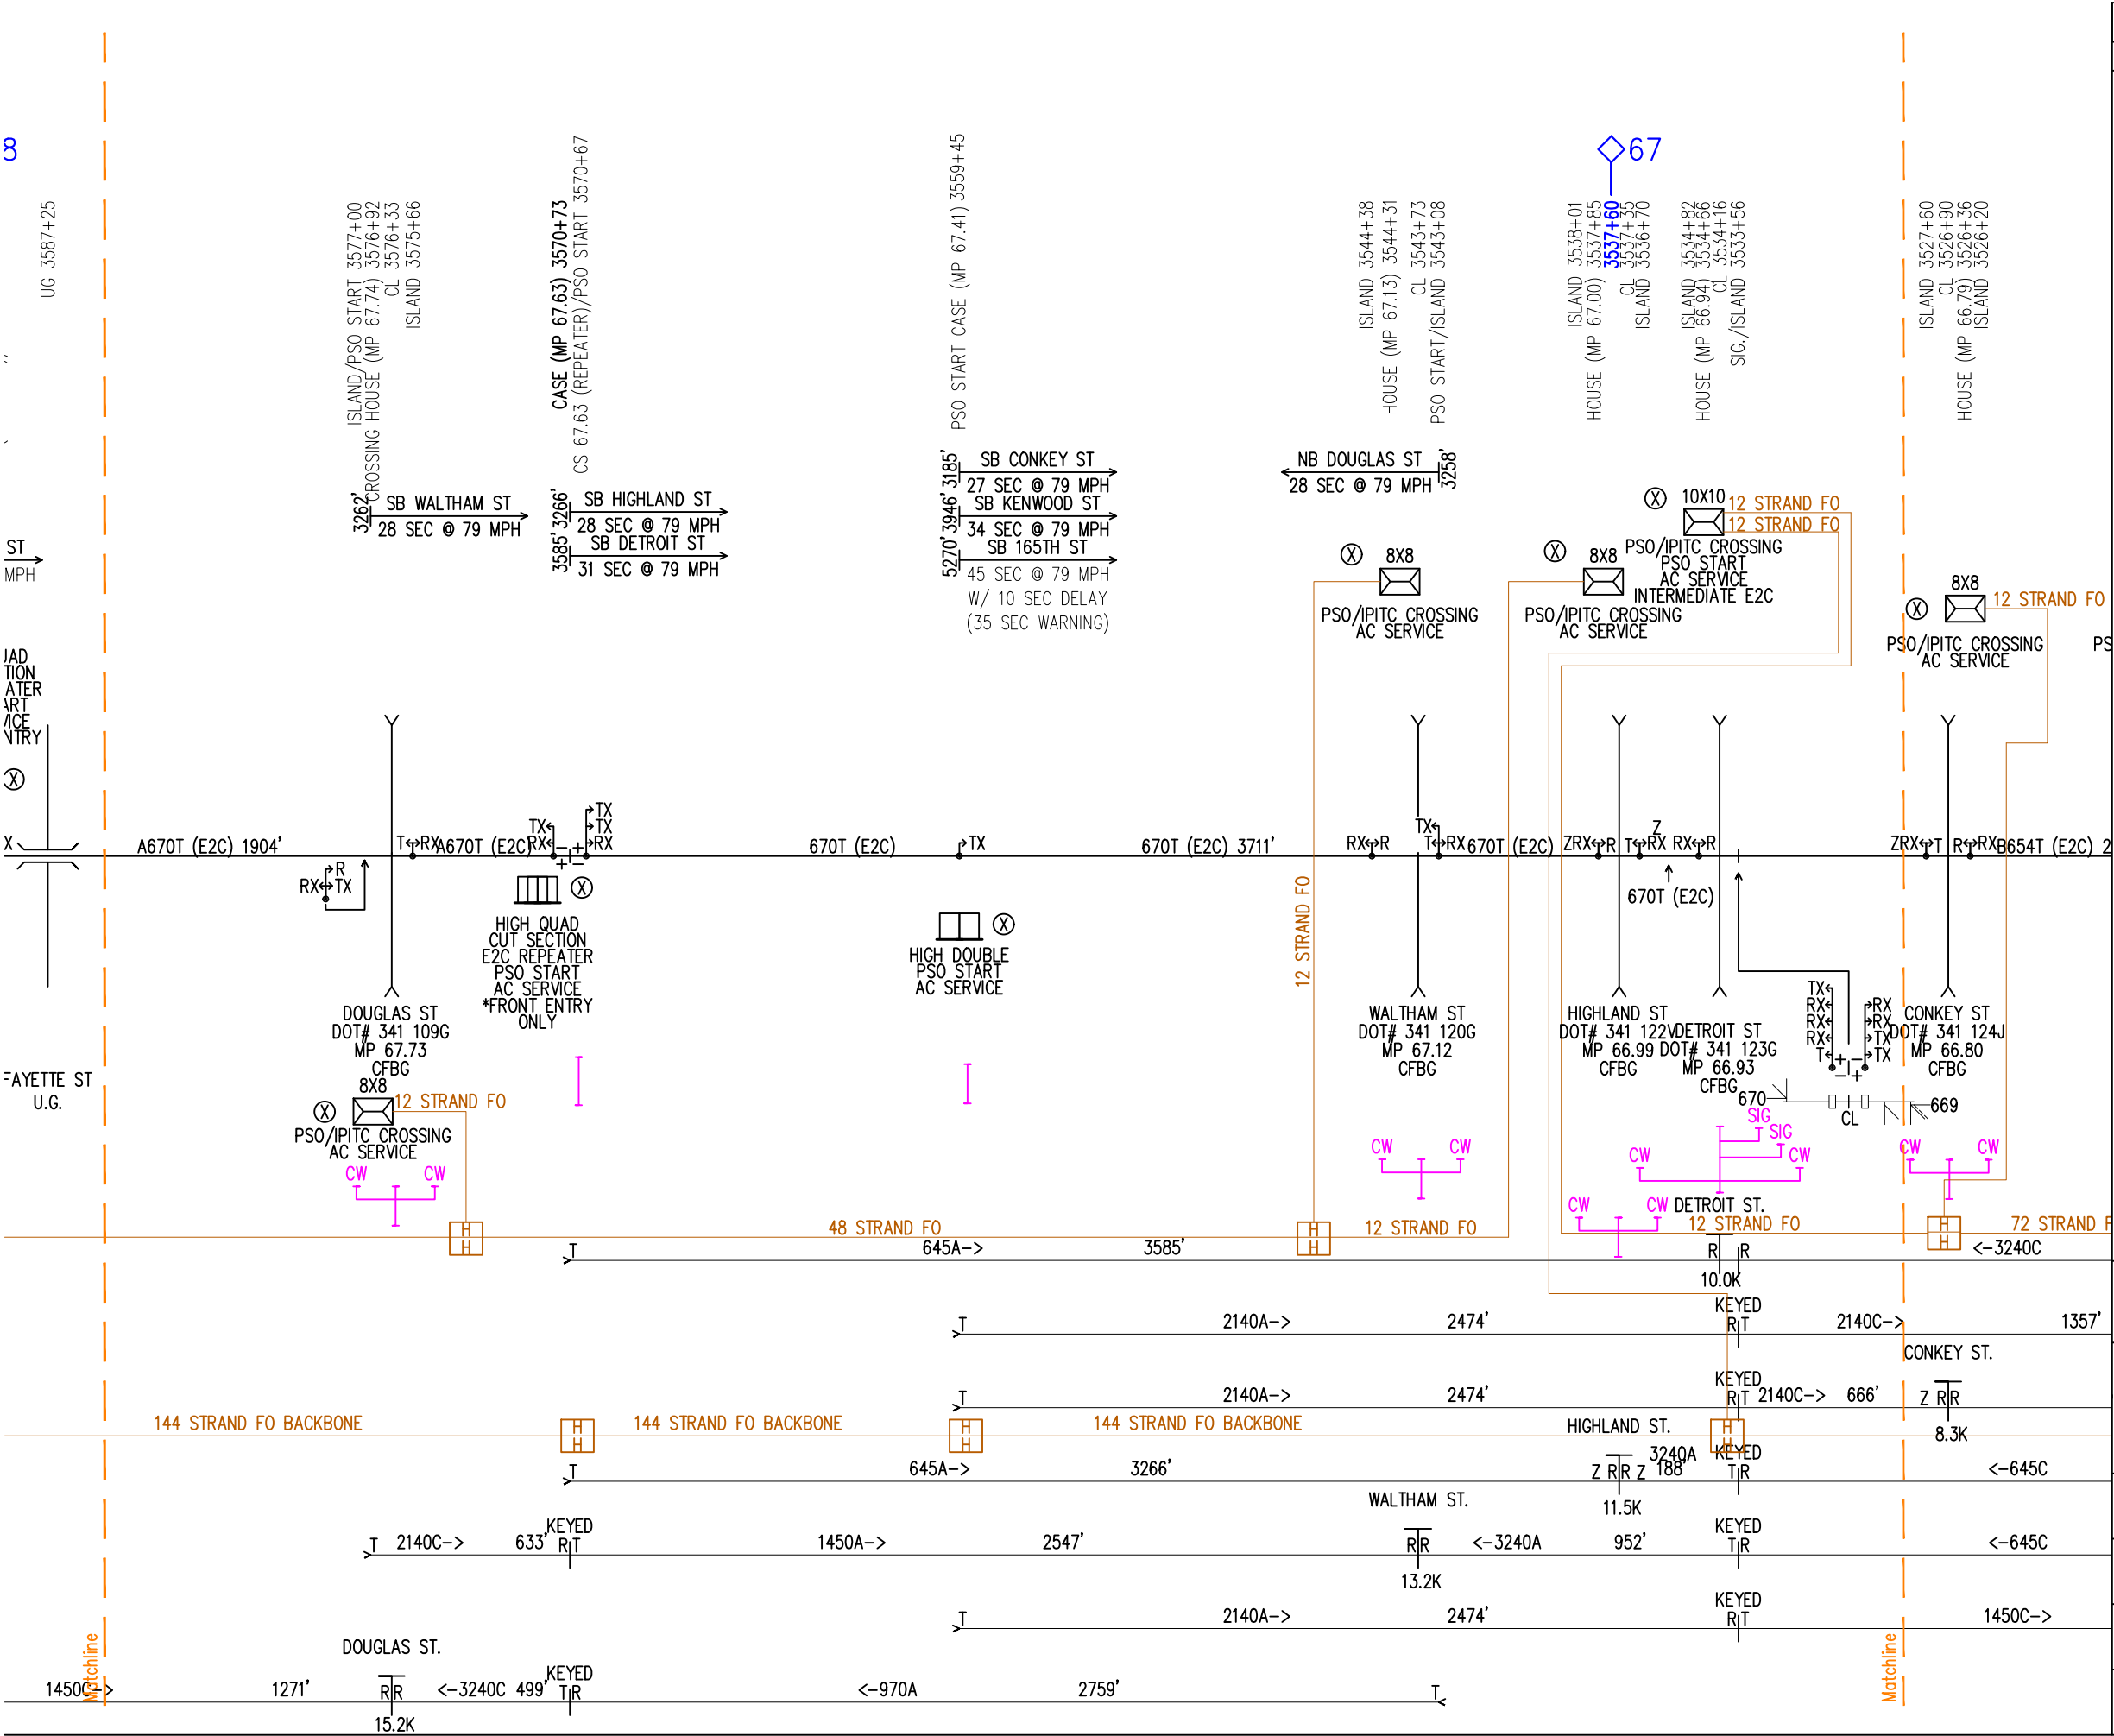

REVISIONS	
PRELIMINARY	
(LEVEL 1) TITLE BLOCK AND BORDER (LEVEL 2) BLACK - ALL NEW BLUE = NOTE	
(LEVEL 5) (X) = NEW AC SERVICE	
(LEVEL 7) BROWN = FO - COMM. LINES	
(LEVEL 8) PURPLE = OPERATION CABLES	
(LEVEL 15) = CROSSING START FREQUENCIES (LEVEL MUST BE ACTIVATED, WITH LEVEL 7 & 8 DEACTIVATED).	
HORIZONTAL SCALE : 1 INCH = 500 FEET	
 NORTHERN INDIANA COMMUTER TRANSPORTATION DISTRICT	
WEST LAKE CORRIDOR PROJECT M.P. 66 TO M.P. 69	
DESIGNER SKETCH WITH CROSSING FREQUENCY STUDY	
DESIGNED DAI/JNV	DIGITIZED DAI/JNV
NEXT FILE	NEXT SH
CHECKED DAI/BDO	DATE 12-01-23
FILE SKETCH	SHEET 002C

C:\Users\mmaikowski\NTAppData\LocalTemp\AcPublish_248\2\AE_Designer Sketch MP 66-69 R1 12-01+23.dwg @ 2/08/24 - 1:14pm by mmaikowski

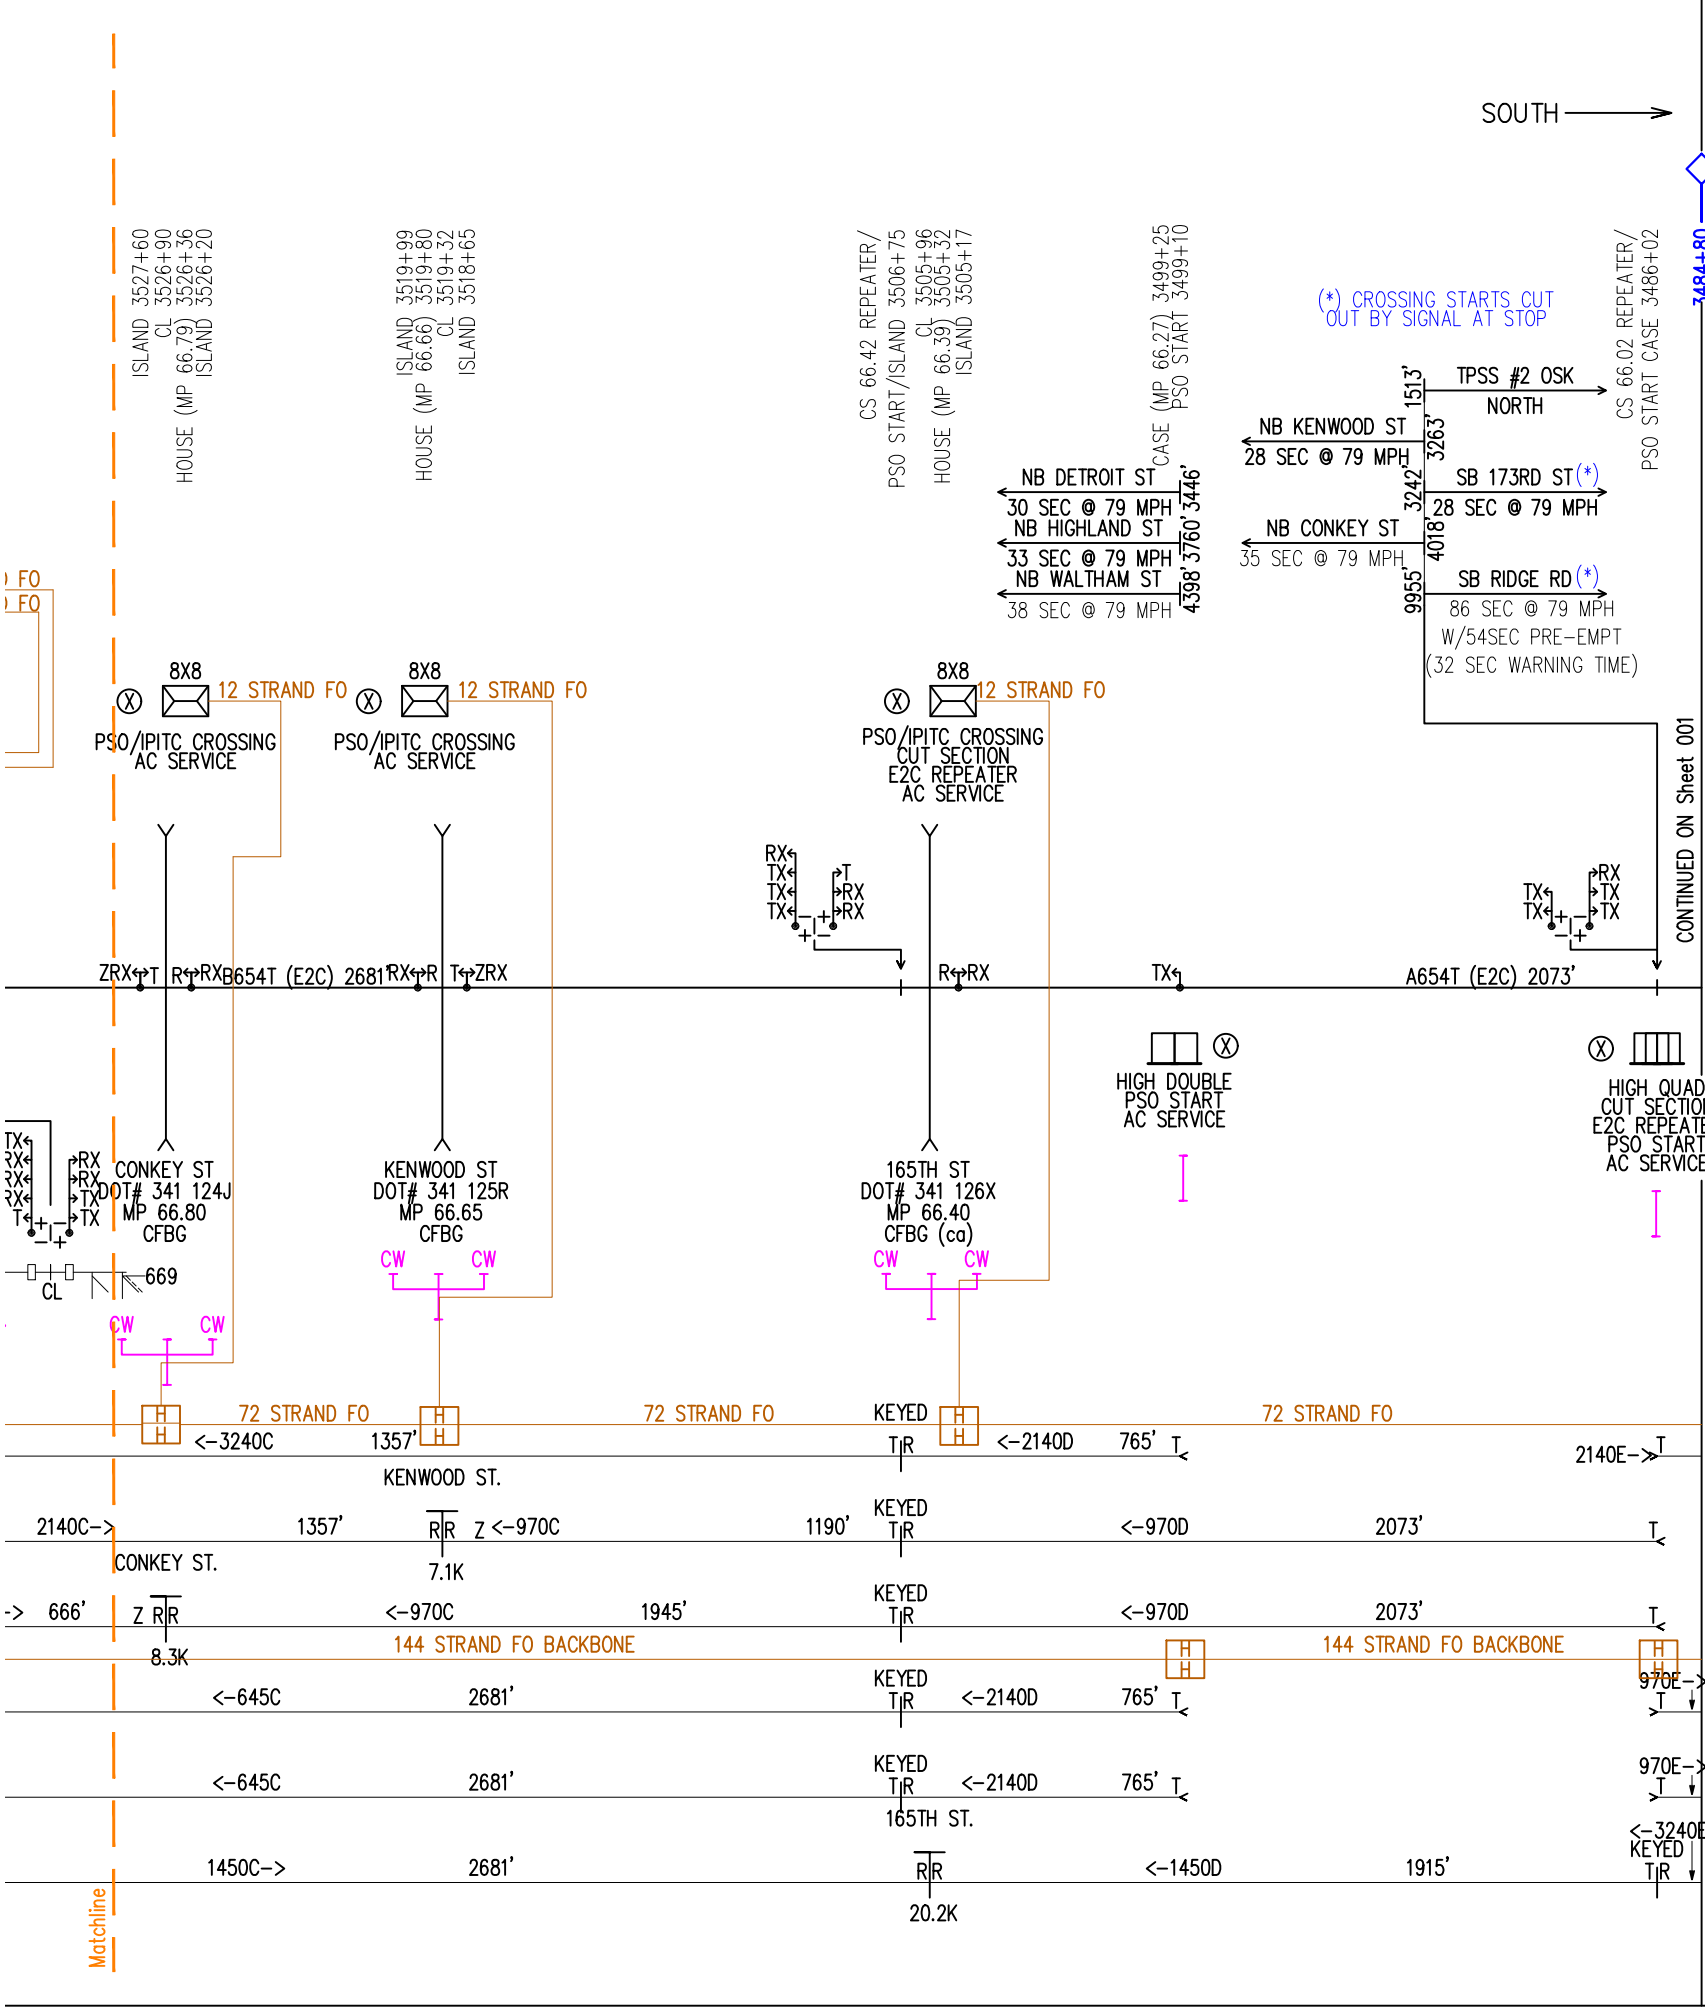

LEGEND

70

MILE MARKER

HIGHWAY GRADE CROSSING

HIGHWAY OVER PASS

HIGHWAY UNDER PASS

TRANSMITTER

RECEIVER

SNOW MELTER

INSULATED JOINT

INSULATED END JOINT

CONTROLLED SWITCH IN INTERLOCKING

AUTOMATIC SIGNAL

CONTROLLED SIGNAL

DWARF SIGNAL

HAND HOLE

BUILDING

SIGNAL CASE

GENERATOR

METER SERVICE

CRIBBING

DERAIL

CROSSING START LOCATION

C.I.H. = CENTRAL INSTRUMENT HOUSE

DER = DERAIL

EOB = END OF BLOCK

FO = FIBER OPTIC

HS = HIGHWAY CROSSING

IJ = INSULATED JOINT

LOC.A = SUPPLEMENTAL HOUSE

OG = OVER GRADE

UG = UNDER GRADE

PLT = PLATFORM

PS = POINT OF SWITCH

SIG = SIGNAL

SW = SWITCH

F/R = SE3 FEED AND RELAY

KEYED = RECEIVER KEYS ADJACENT TRANSMITTER

CABLE = RELAY LOGIC OVER EXPRESS CABLE

SE3 = SAFETRAN AC TRACK CIRCUIT

MAS = MAXIMUM AUTHORIZED SPEED

K = # 1000 HERTZ

ISL = ISLAND CIRCUIT

AVR = AVERAGE SPEED IN M.P.H.

Z = HIGH IMPEDANCE RCVR COUPLER

C = CROSSING

F = FLASHERS

B = BELLS

G = GATES

CW = CROSSING WARNING

ELX = ELECTROLOGIXS

FO = FIBER OPTIC

TPSS = TRACTION POWER SUBSTATION

CL = COLORLIGHT

Z = HIGH IMPEDANCE COUPLER

(ca) = CANTILEVER

EALM = EMPLOYEE ADMINISTRATION LIGHT MAINTENANCE

E2C = ELECTRIFIED ELECTROCODE

REVISIONS

PRELIMINARY

(LEVEL 1) TITLE BLOCK AND BORDER

(LEVEL 2) BLACK - ALL NEW

BLUE = NOTE

(LEVEL 5) (X) = NEW AC SERVICE

(LEVEL 7) BROWN = FO - COMM. LINES

(LEVEL 8) PURPLE = OPERATION CABLES

(LEVEL 15) = CROSSING START FREQUENCIES (LEVEL MUST BE ACTIVATED, WITH LEVEL 7 & 8 DEACTIVATED).

HORIZONTAL SCALE :
1 INCH = 500 FEET

NORTHERN INDIANA COMMUTER TRANSPORTATION DISTRICT

WEST LAKE
CORRIDOR PROJECT
M.P. 66 TO M.P. 69

DESIGNER SKETCH WITH CROSSING FREQUENCY STUDY

DESIGNED DAI/JNV	DIGITIZED DAI/JNV
NEXT FILE	NEXT SH
CHECKED DAI/BDO	DATE 12-01-23
FILE SKETCH	SHEET 002D